
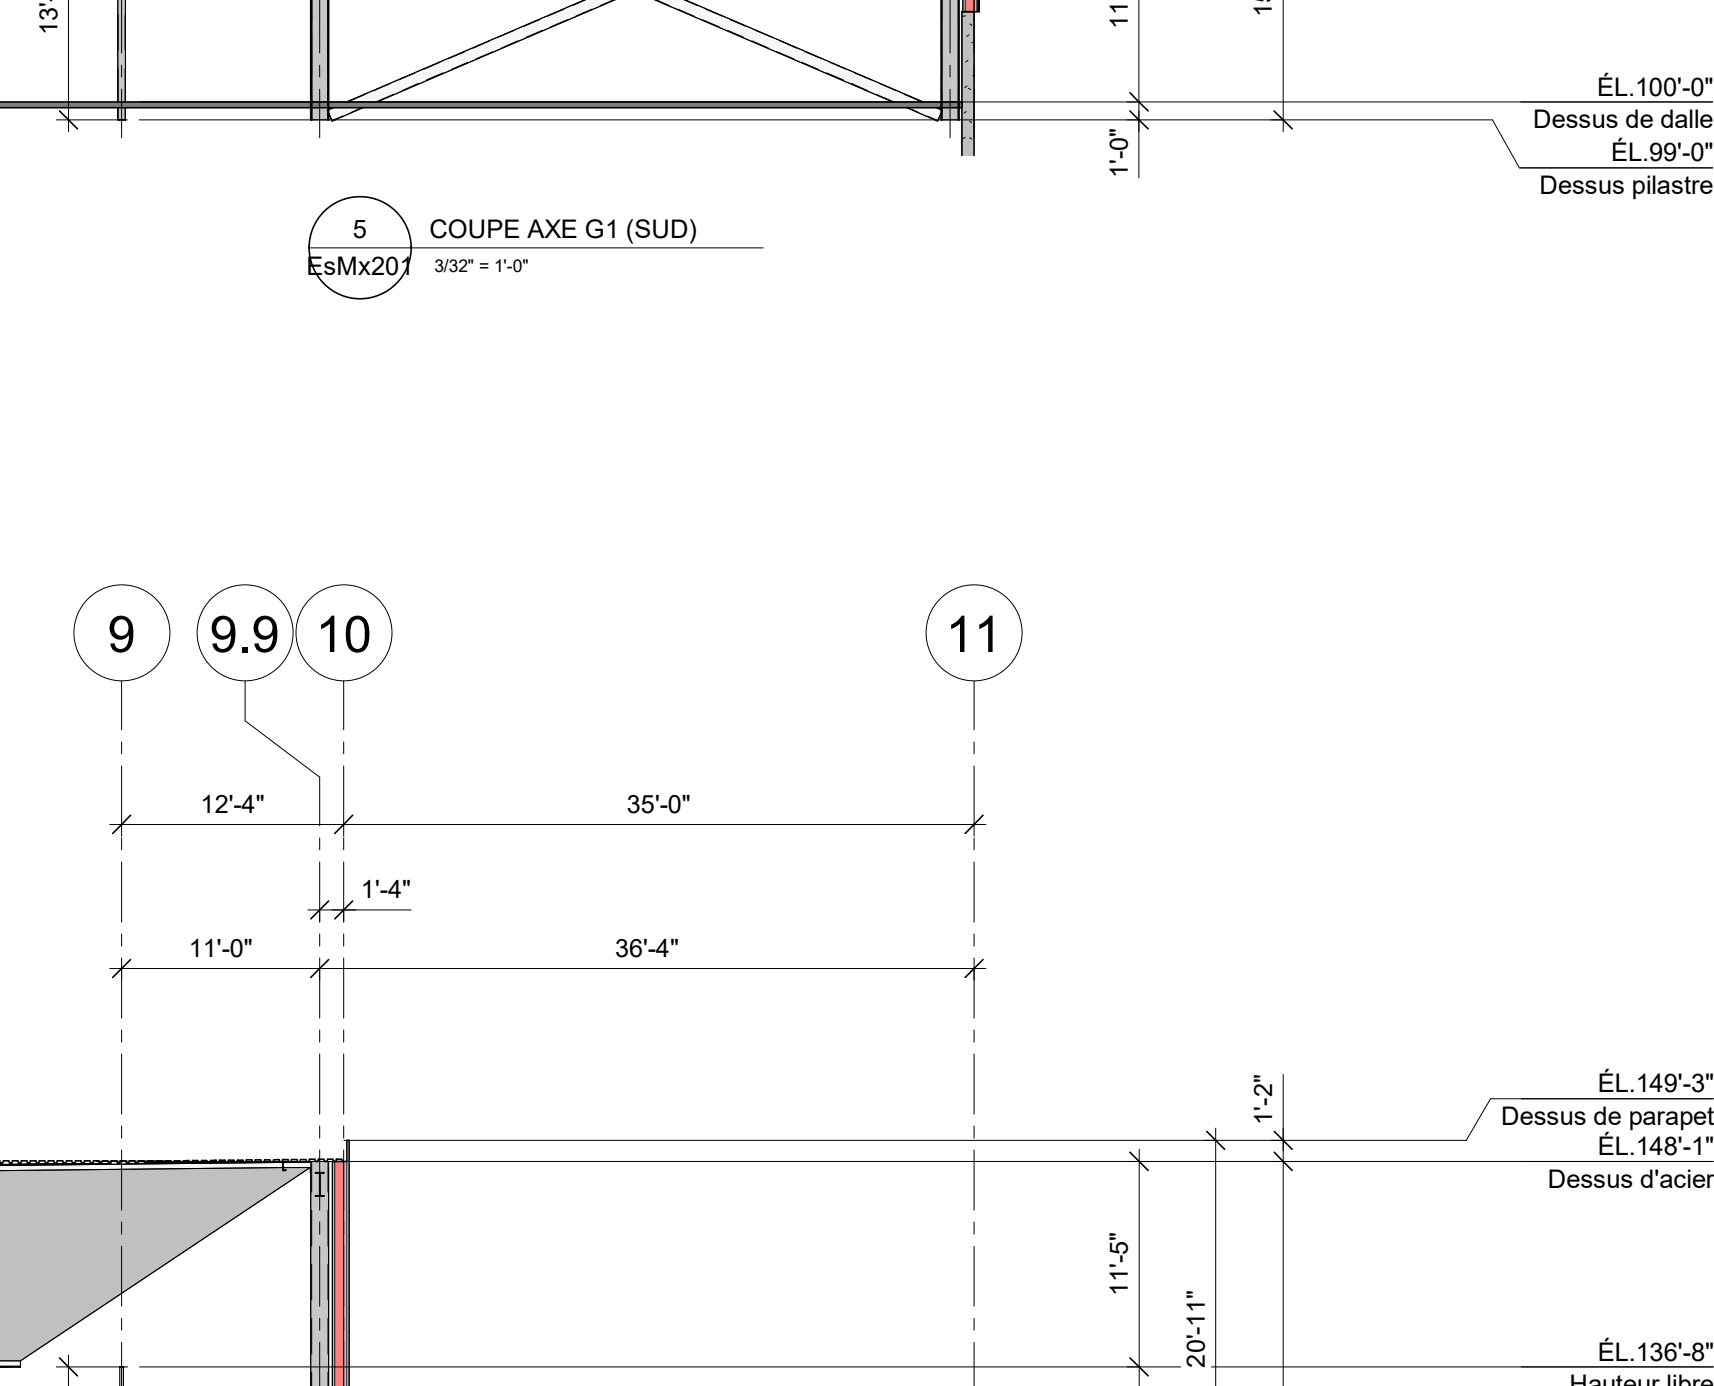
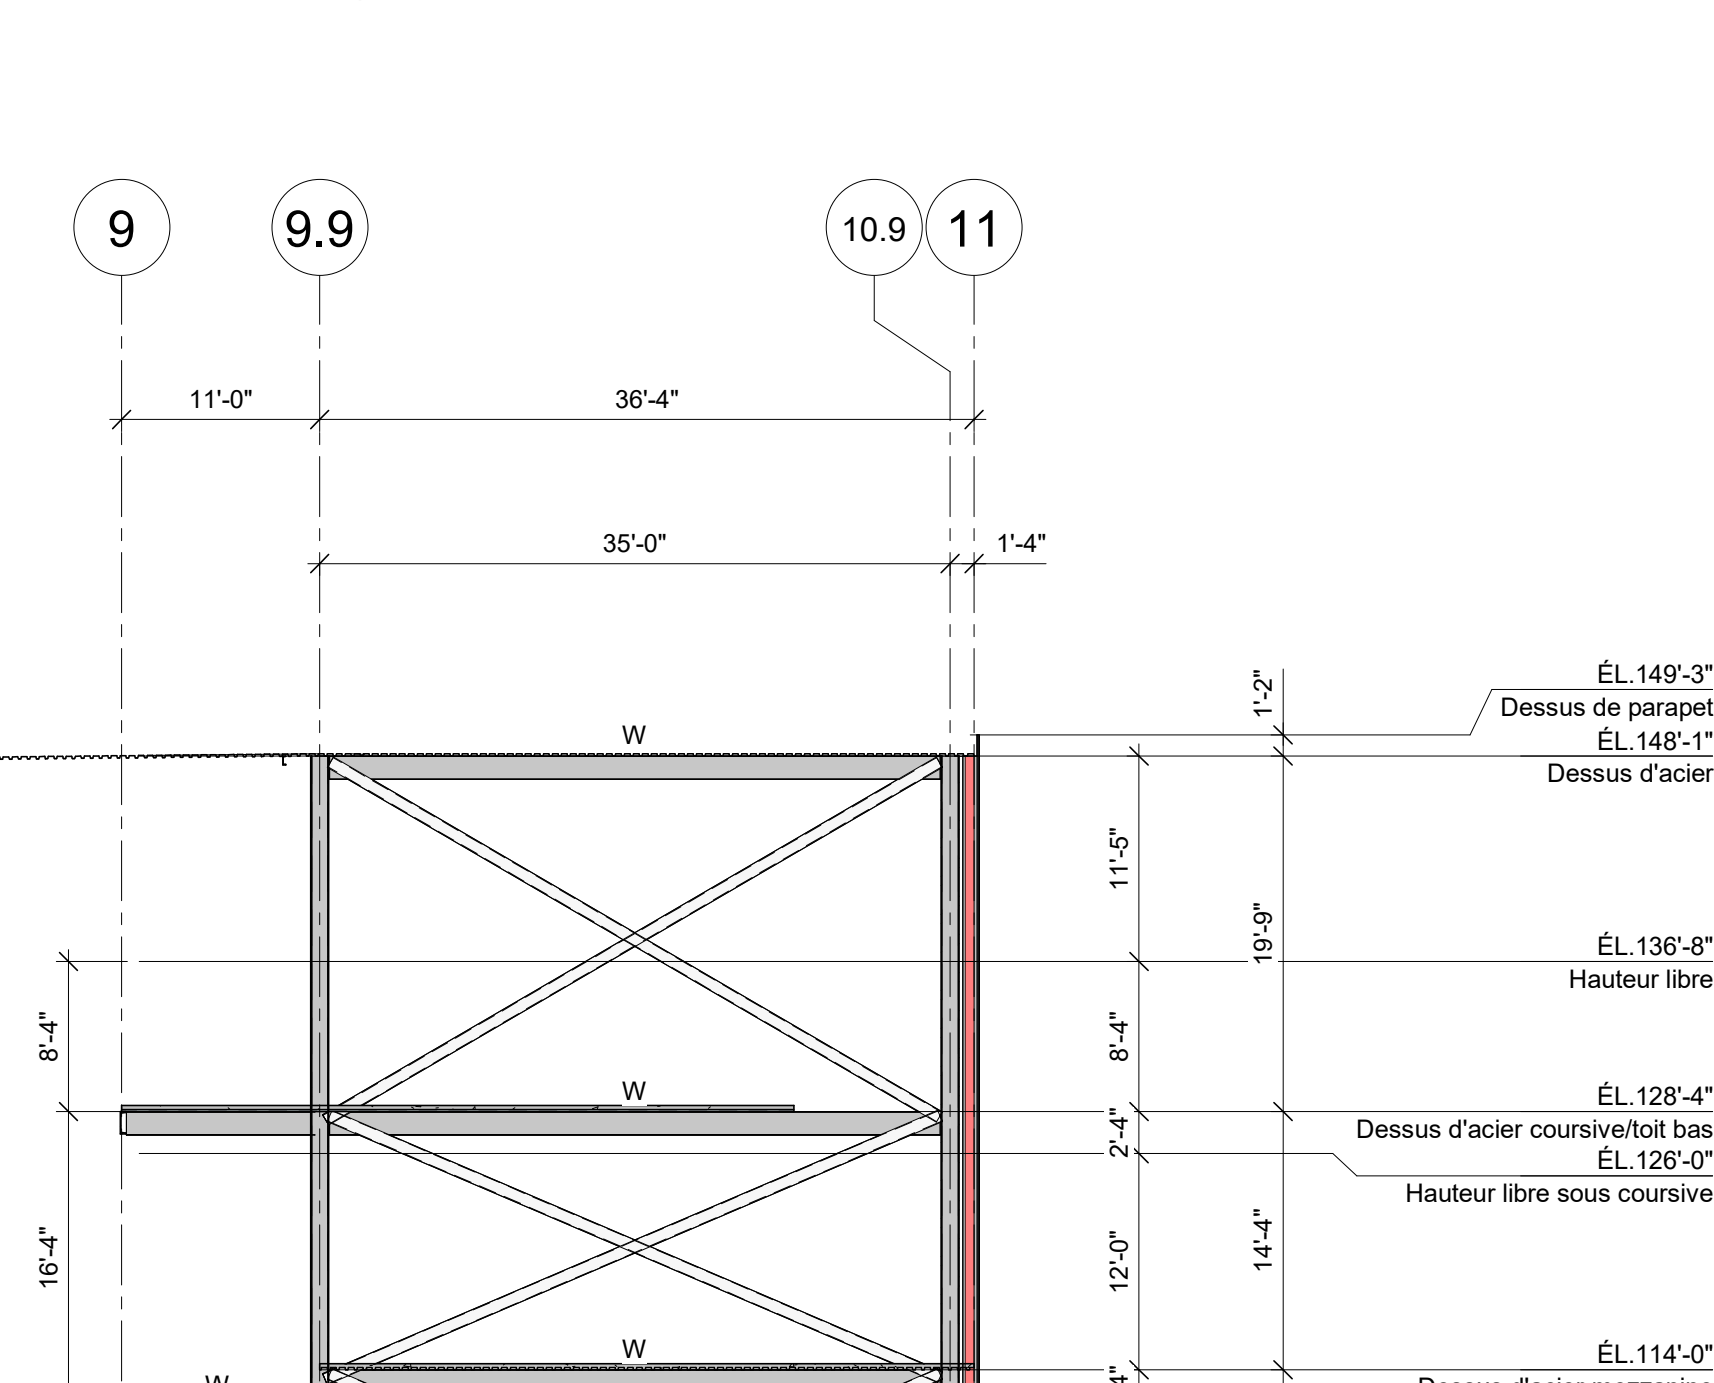
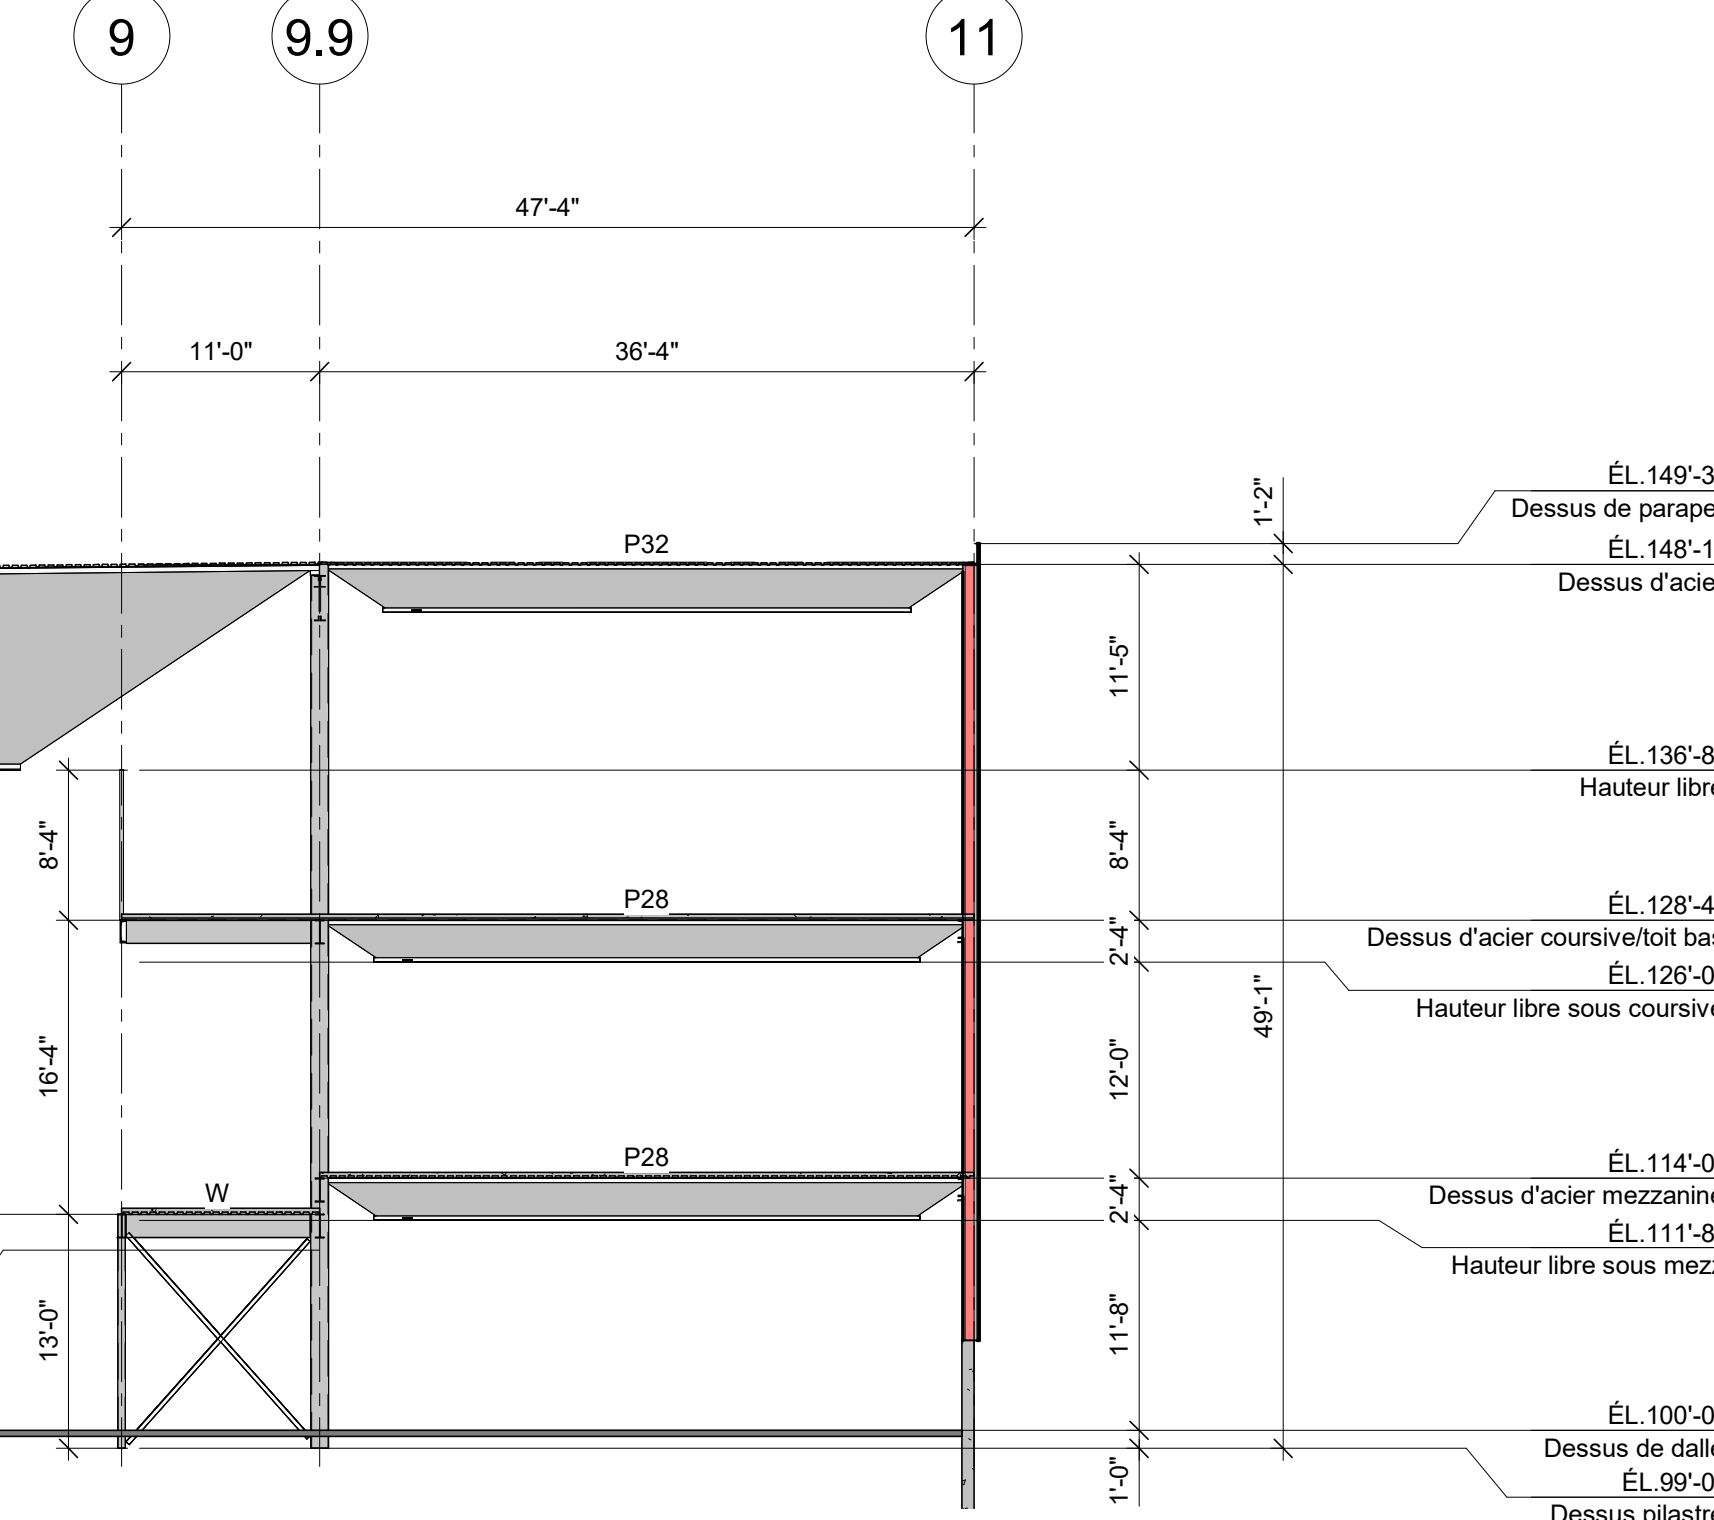
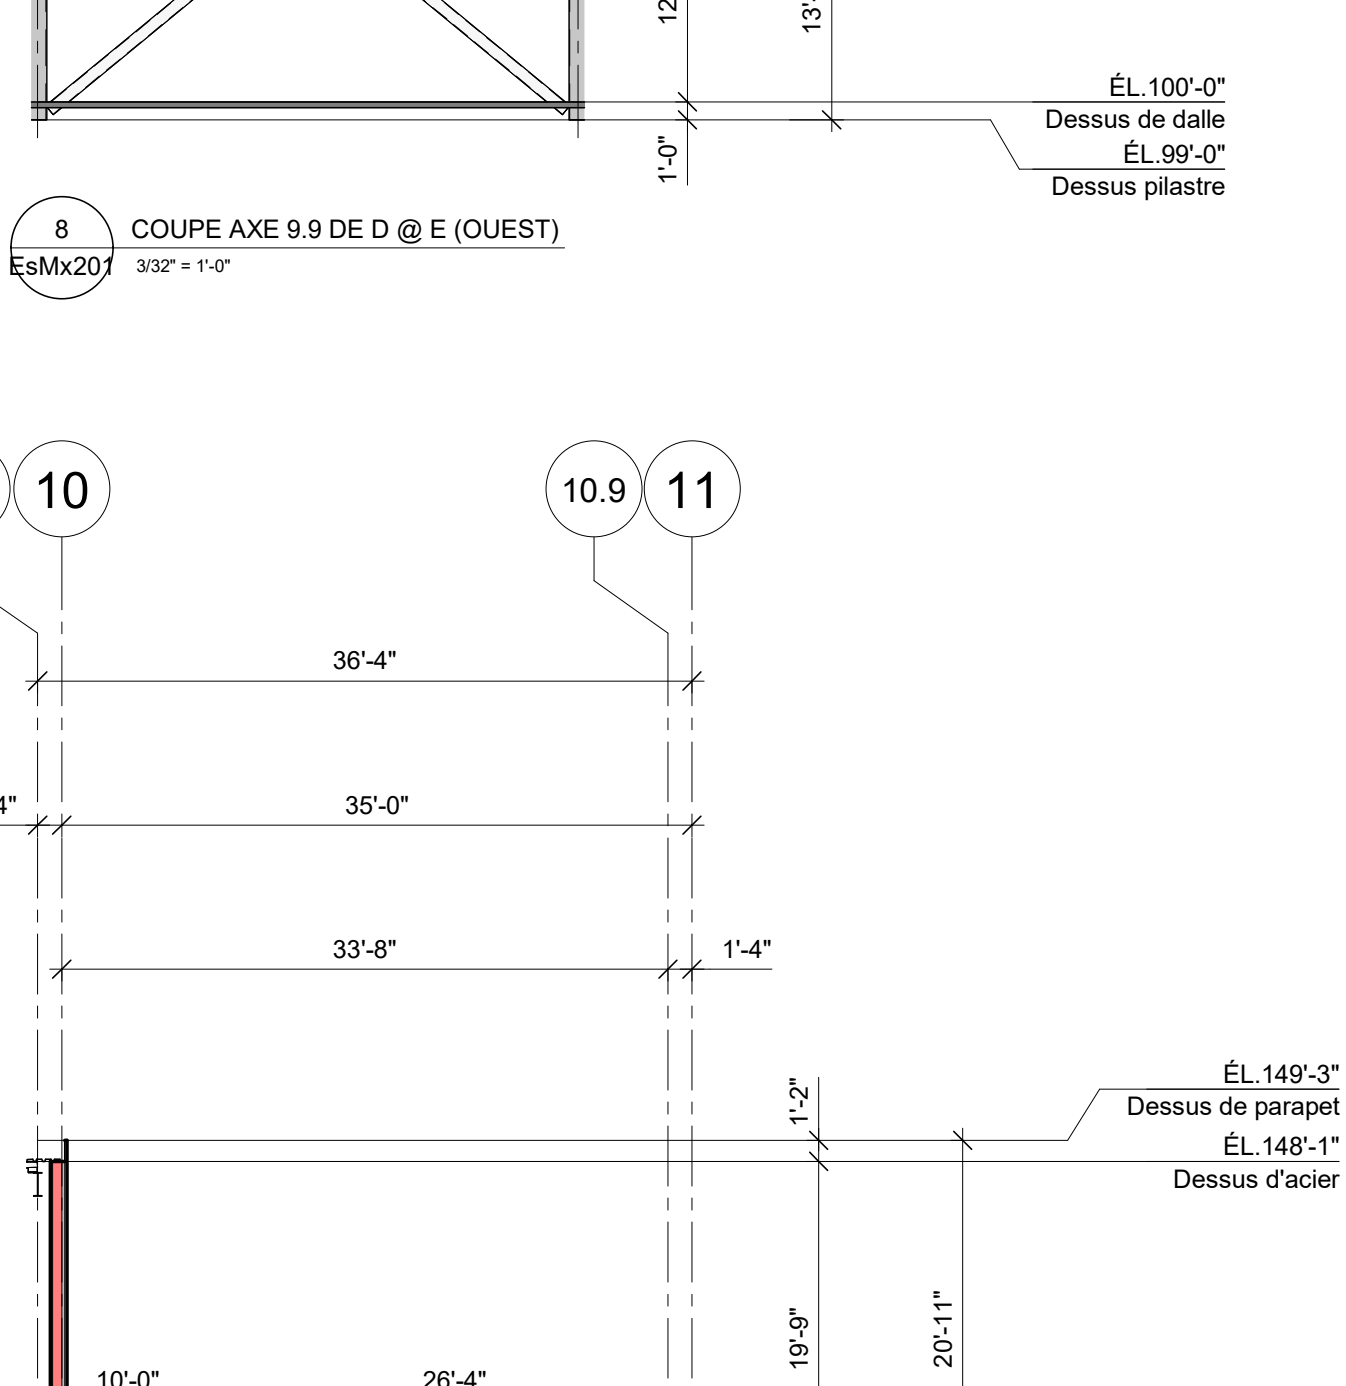
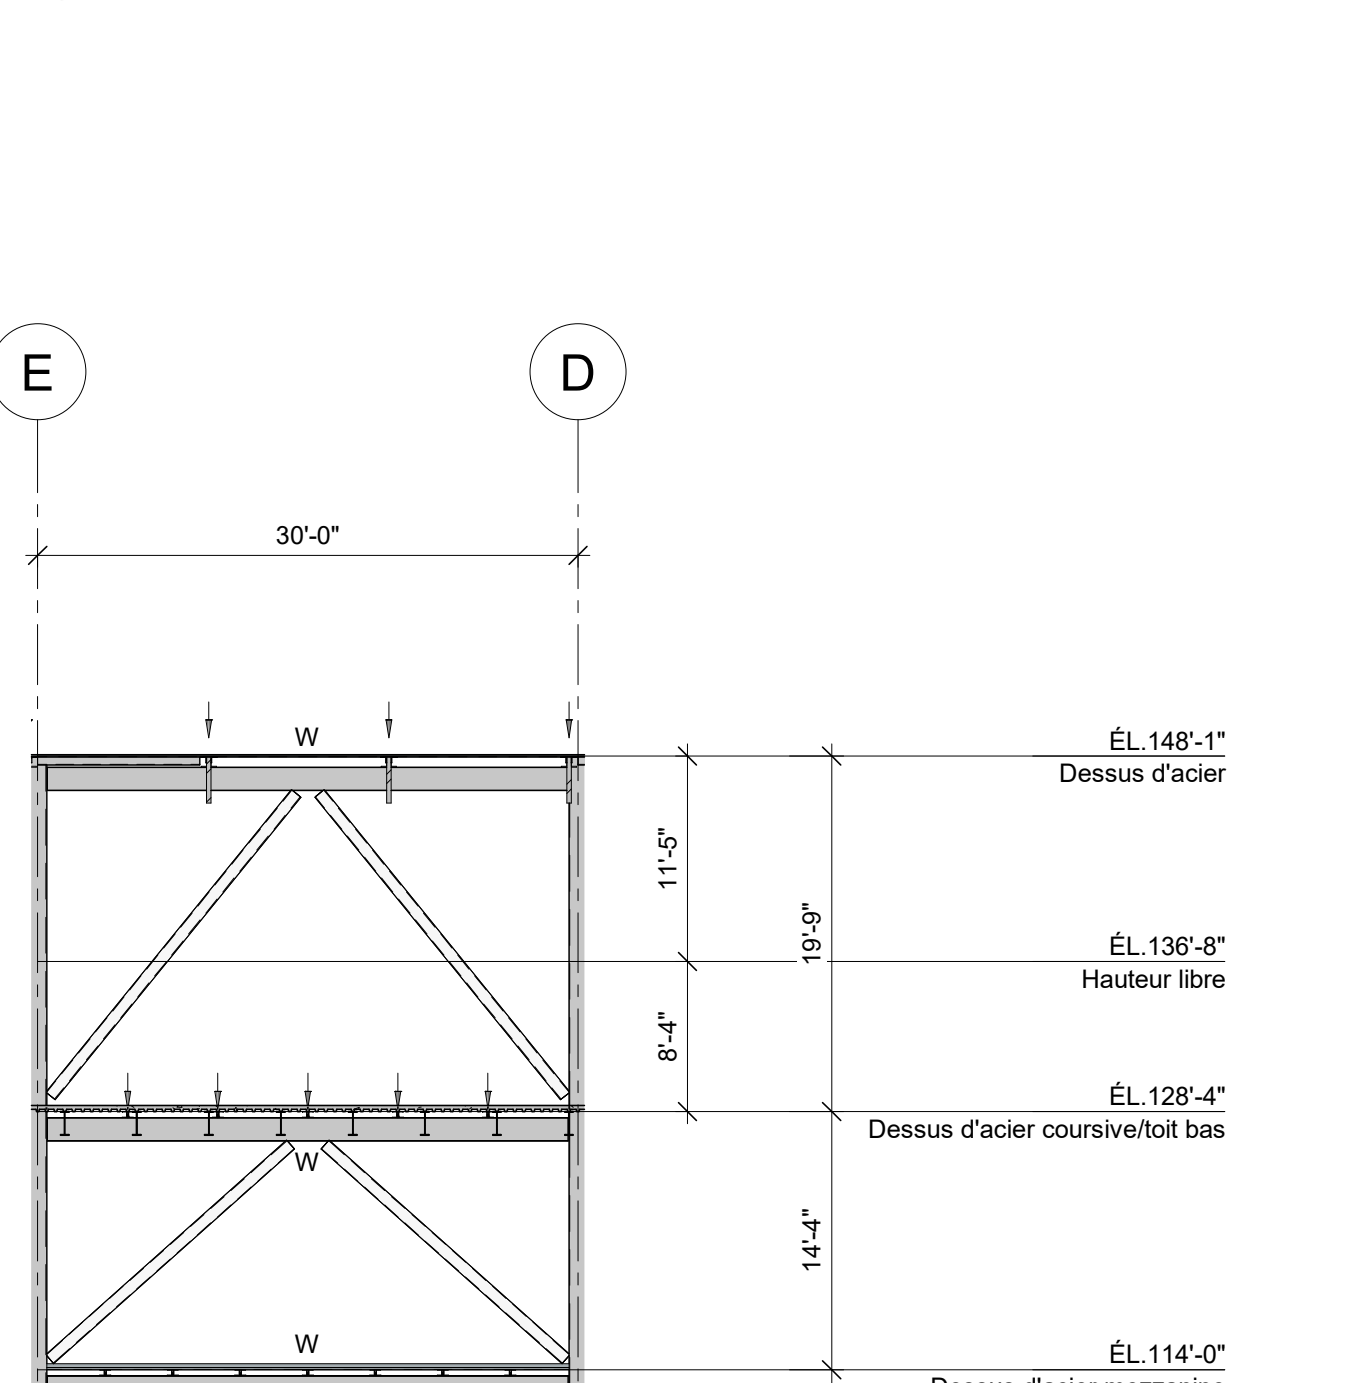
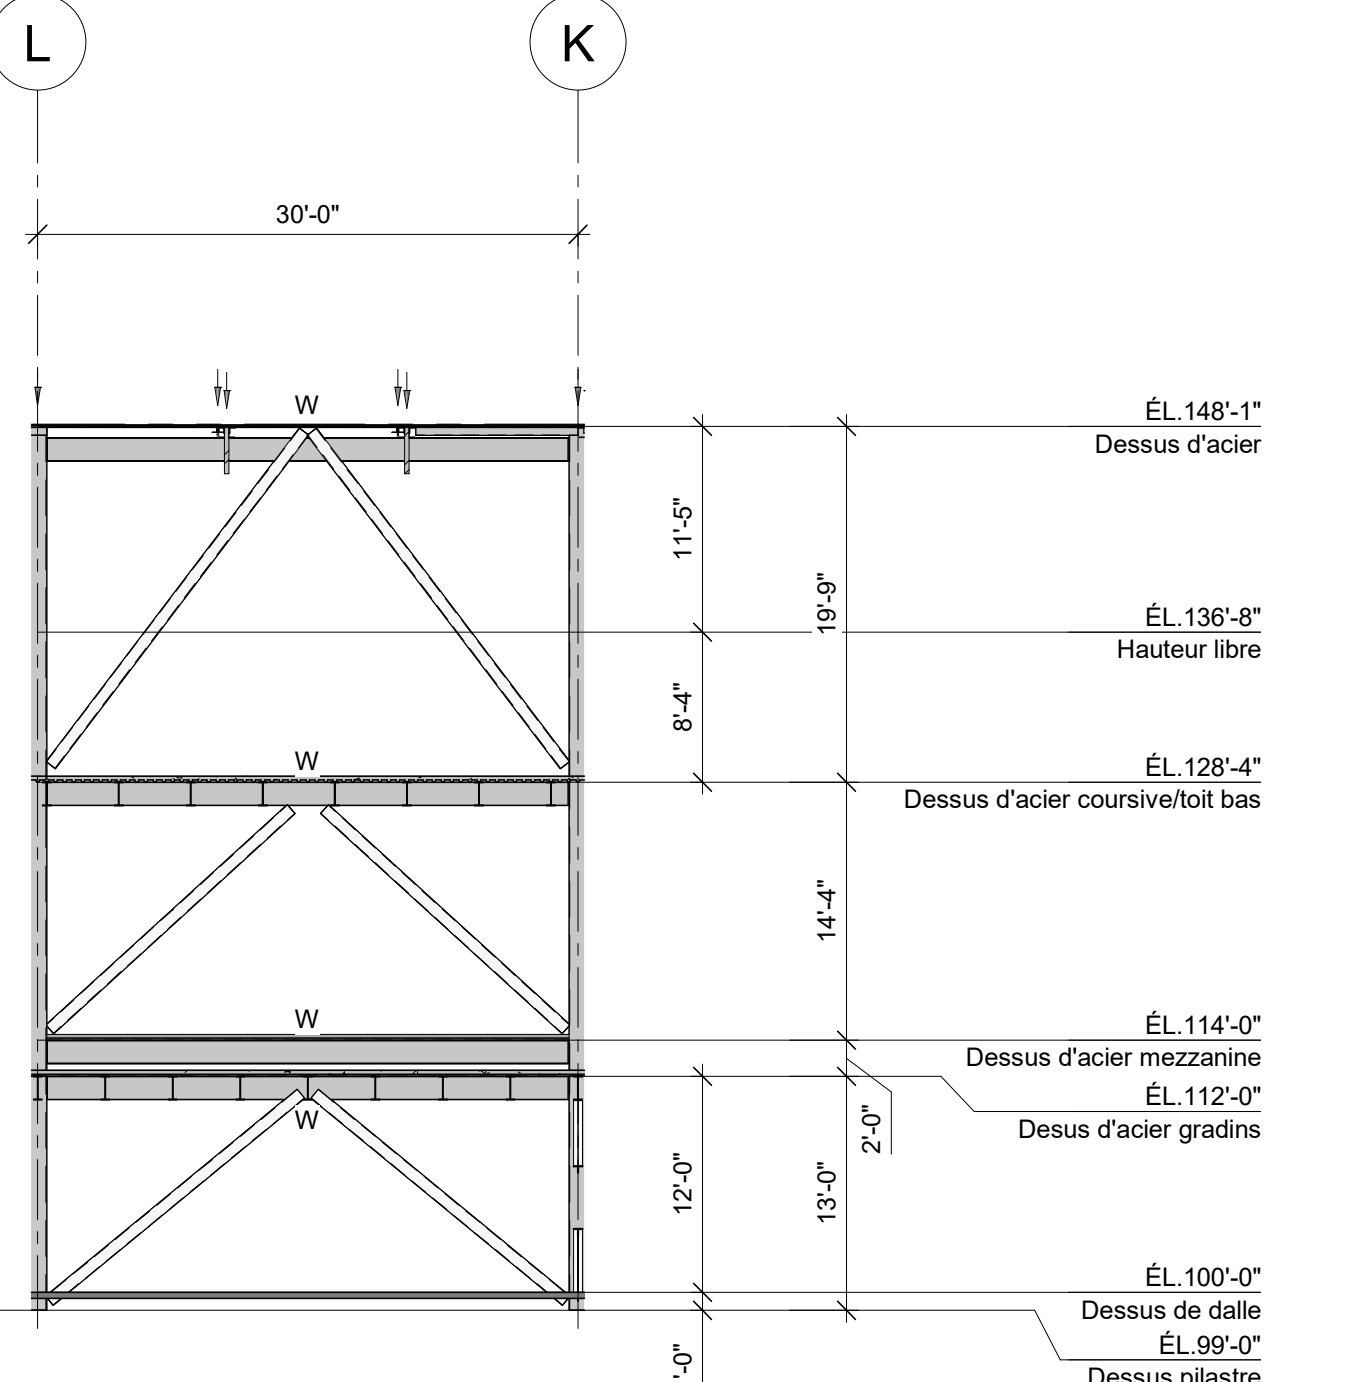
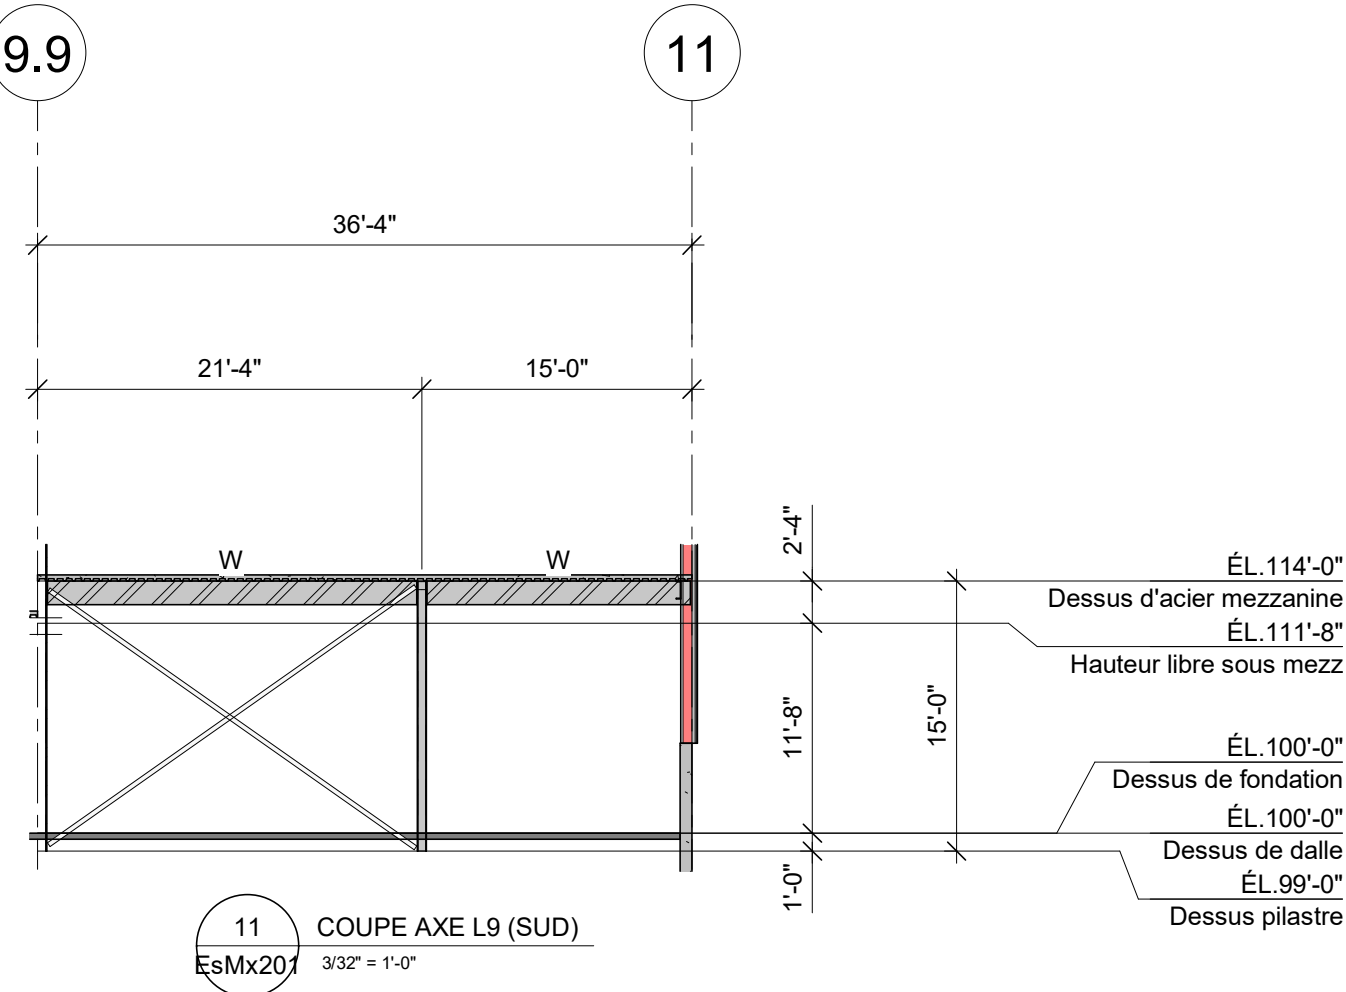


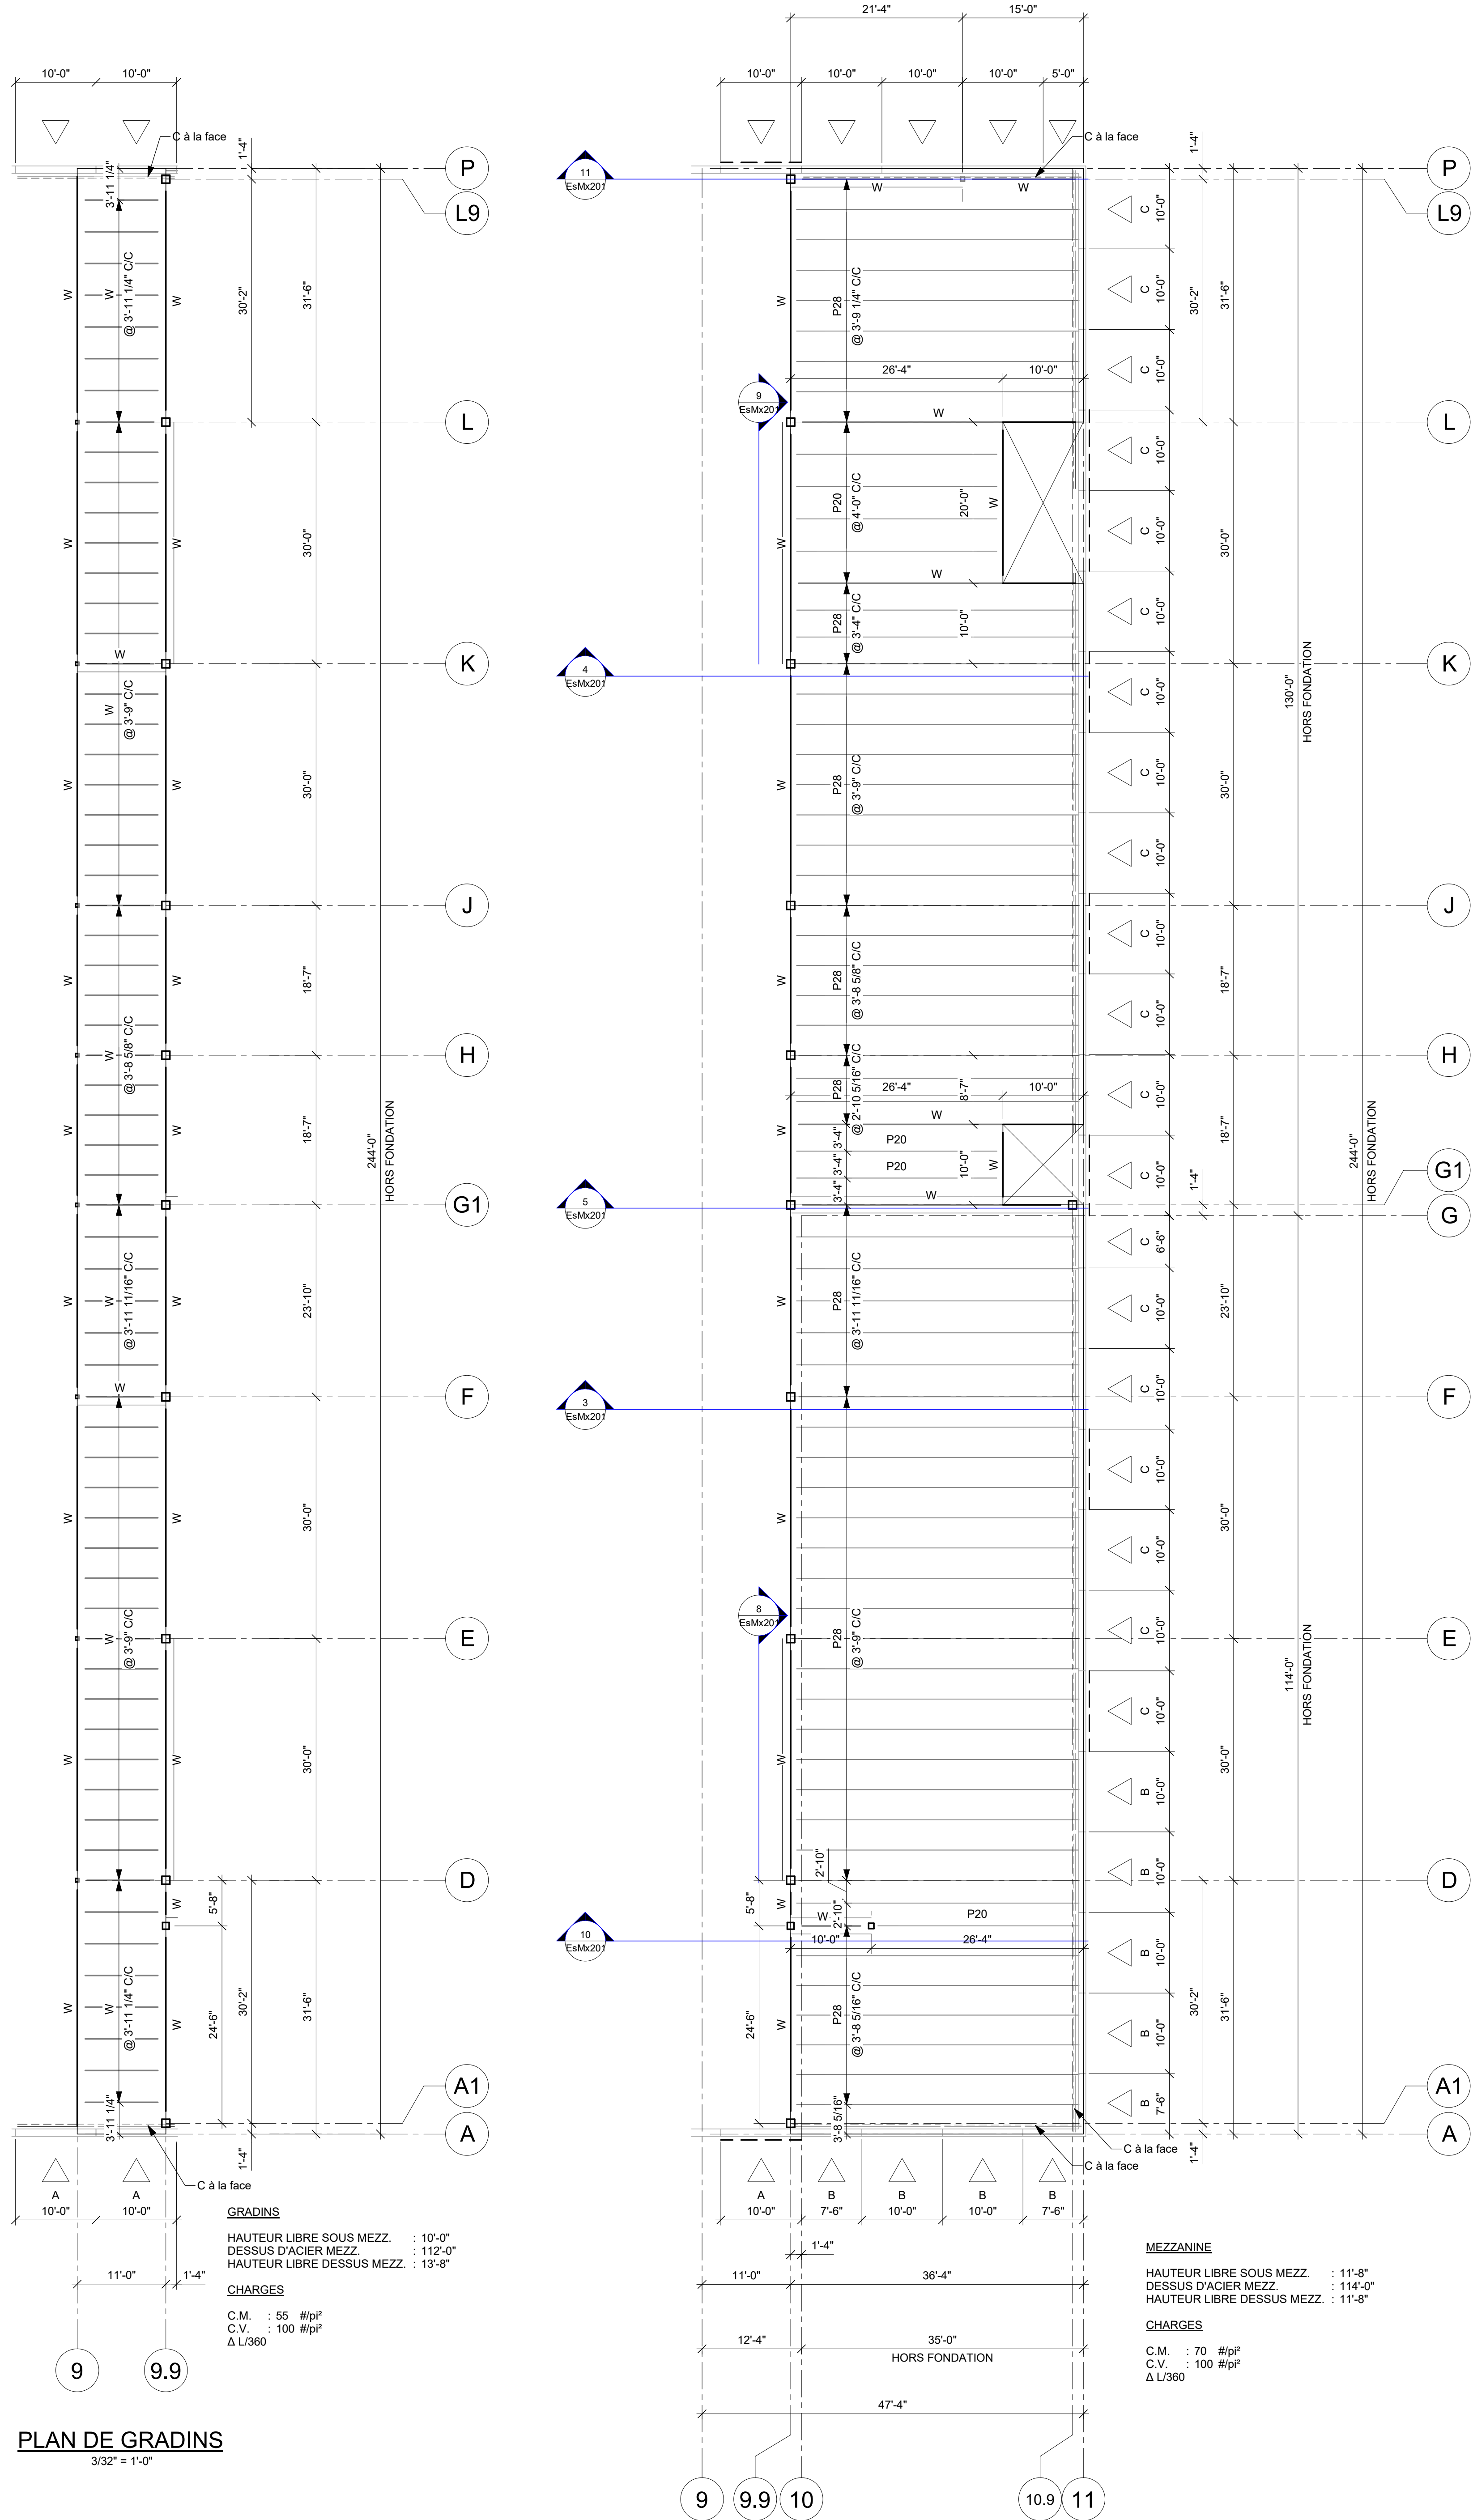

NOTE POUR LE CONTRACTEUR/ÉRECTEUR:
IL EST STRICTEMENT DÉFENDU DE MODIFIER, COPIER, REPRODUIRE OU DE DISTRIBUER CES DESSINS OU QUELQUES REPRÉSENTATIONS DE CES DESSINS, PAR TOUTES SOURCES DE MÉDIA INCLUANT ÉLECTRONIQUEMENT, SANS L'APPROBATION ÉCRITE DE GROUPE CANAM INC.

PRÉLIMINAIRE

NE DOIT PAS SERVIR À LA CONSTRUCTION

REVISION	DATE	DESCRIPTION	DESS	VER
GERANT DE PROJET				

DESSIN	CONÇU PAR	INGÉNIEUR DU PROJET	ÉCHELLE
DESSINÉ PAR	INITIALE		Comme indiqué
VÉRIFIÉ PAR	INGÉNIEURS CONSEILS / ARCHITECTES	DATE (mm/aa/jj)	

CLIENT : Urbanex Construction Inc.

CANAM
11505, 1re Avenue, bureau 500, Saint-Georges Beauce
Québec, Canada G5V 7X5
Téléphone : (418) 228-8031
Sans frais : (877) 499-8049
www.canam.com

SCAUX PROFESSIONNEL

PROJET : Centre Sportif François Bourrin
Beauport, Québec

TITRE : CROQUIS PRÉLIMINAIRE - PLAN DE MEZZANINE ET GRADINS ET COUPES

NUMÉRO CONTRAT	NUMÉRO DESSIN	DIVISION	REVISION
P2026-097	EsMx201		