

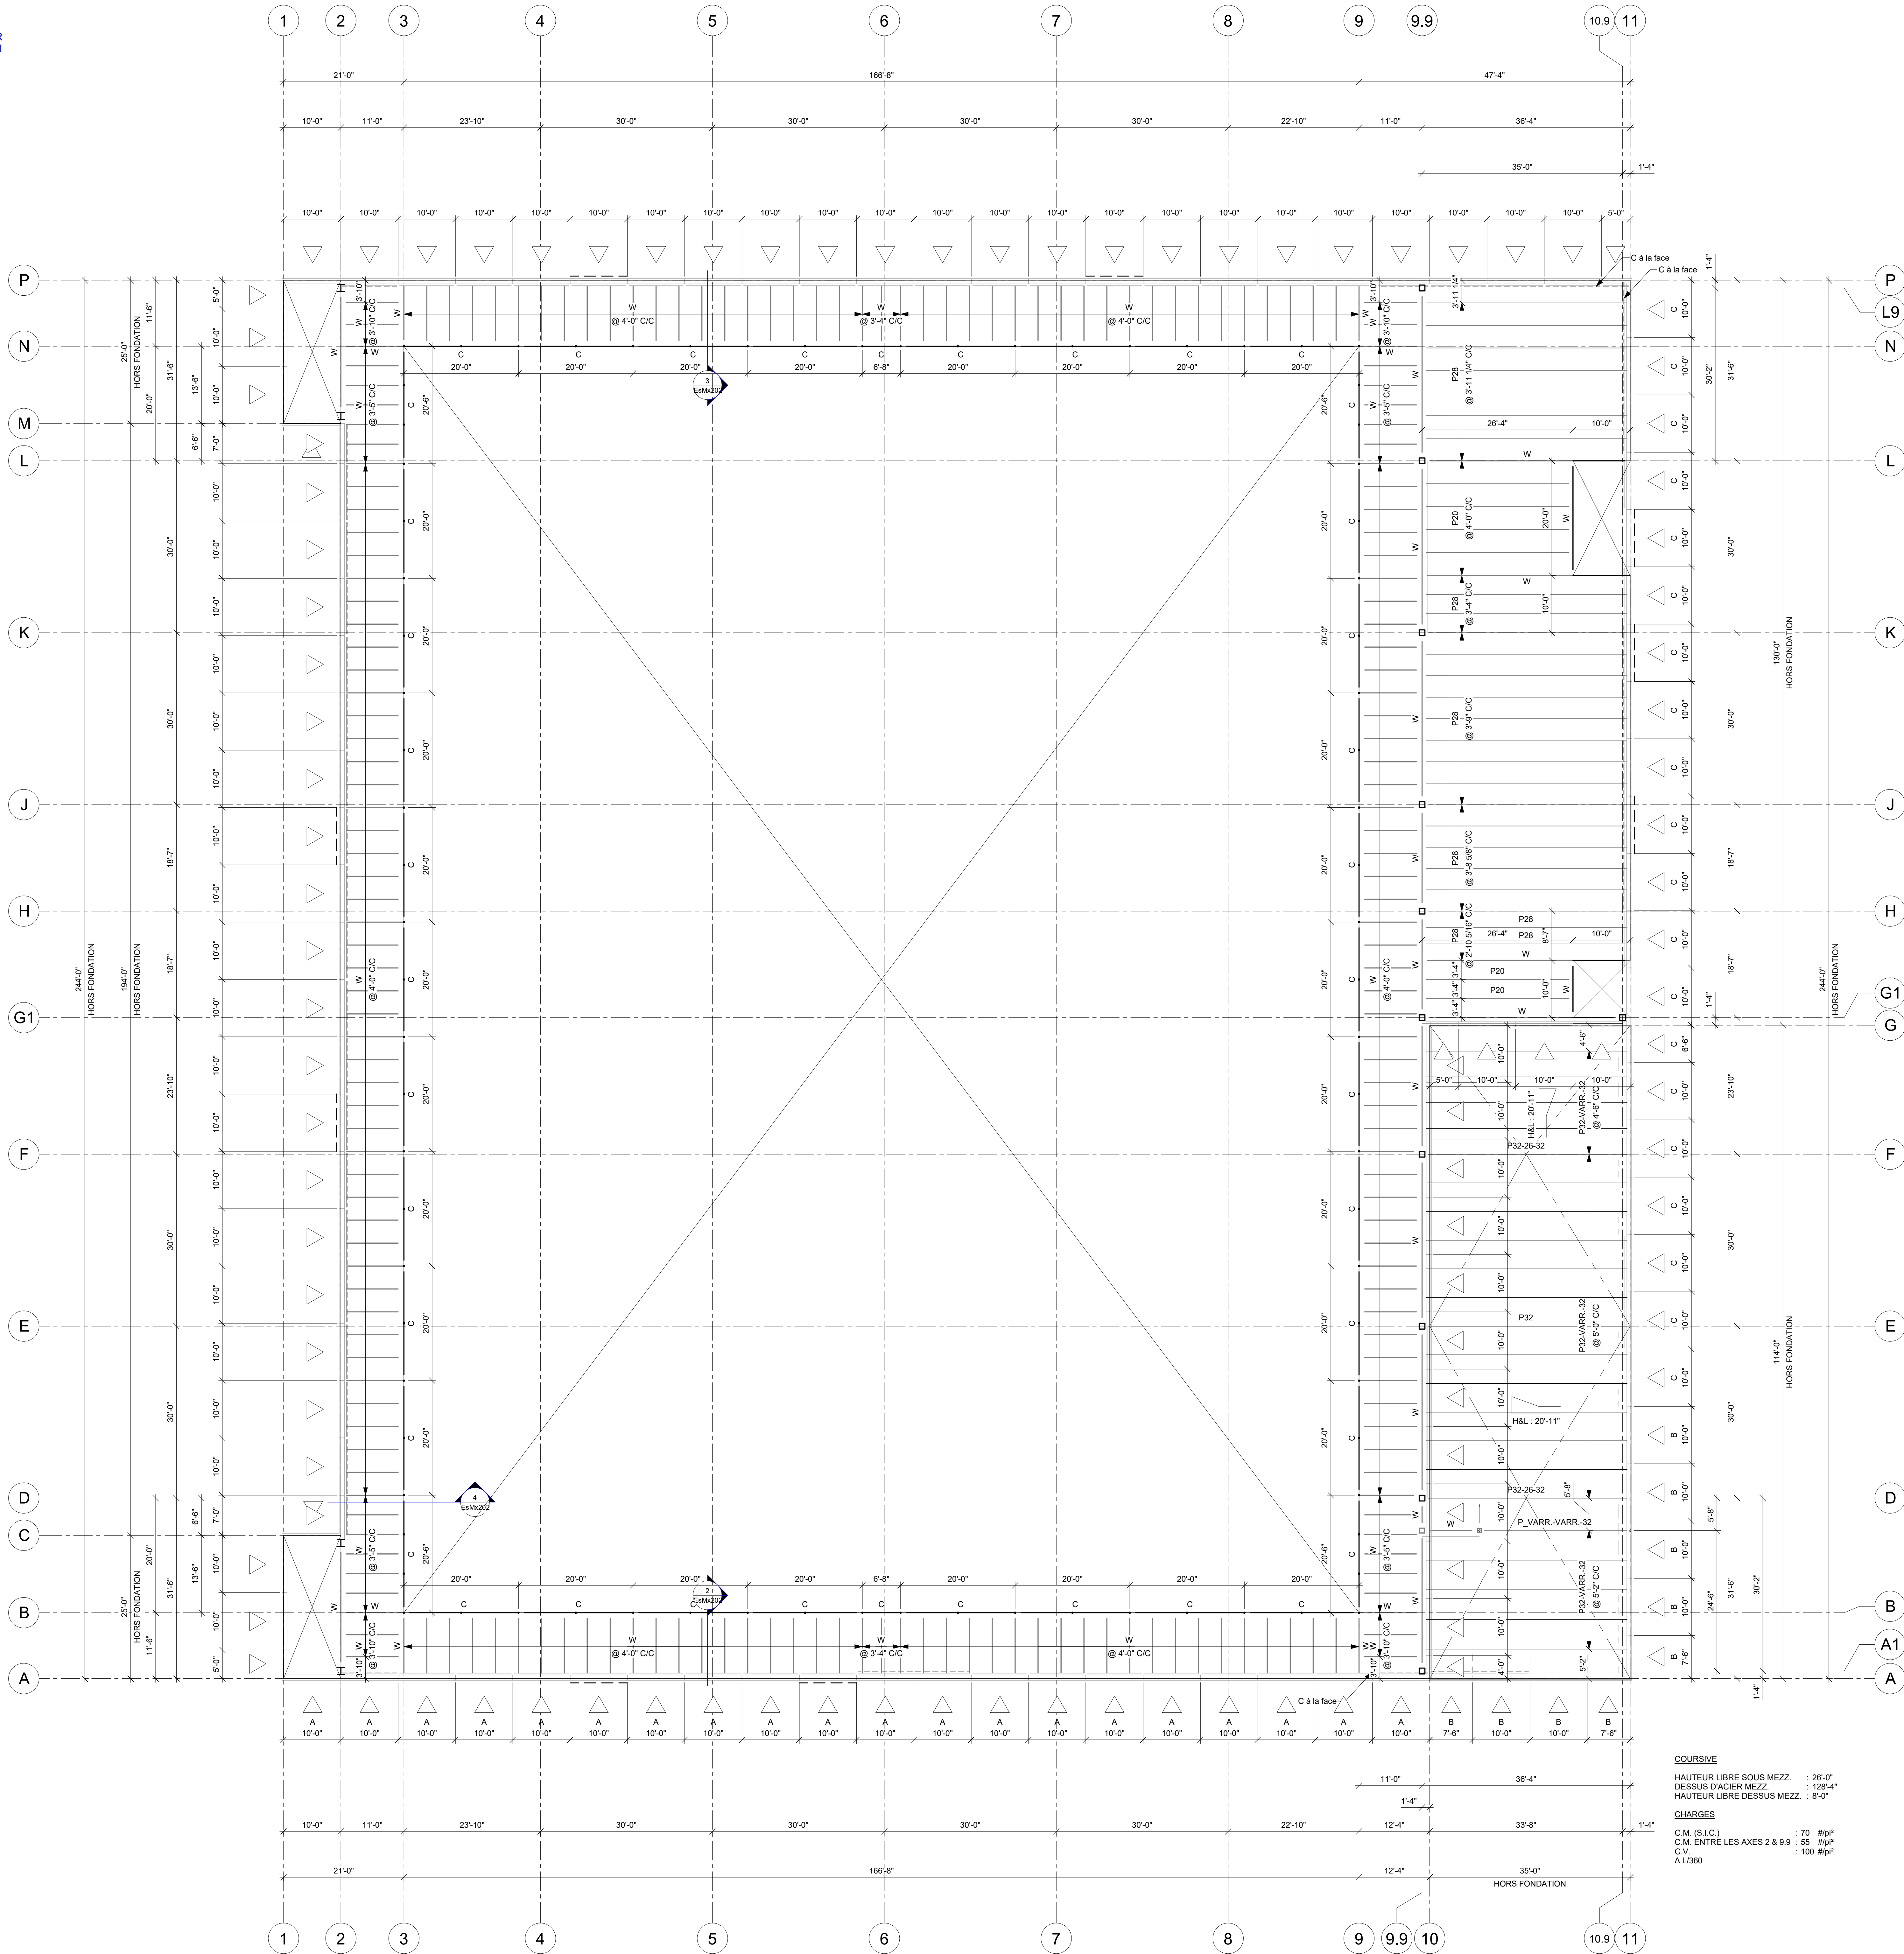
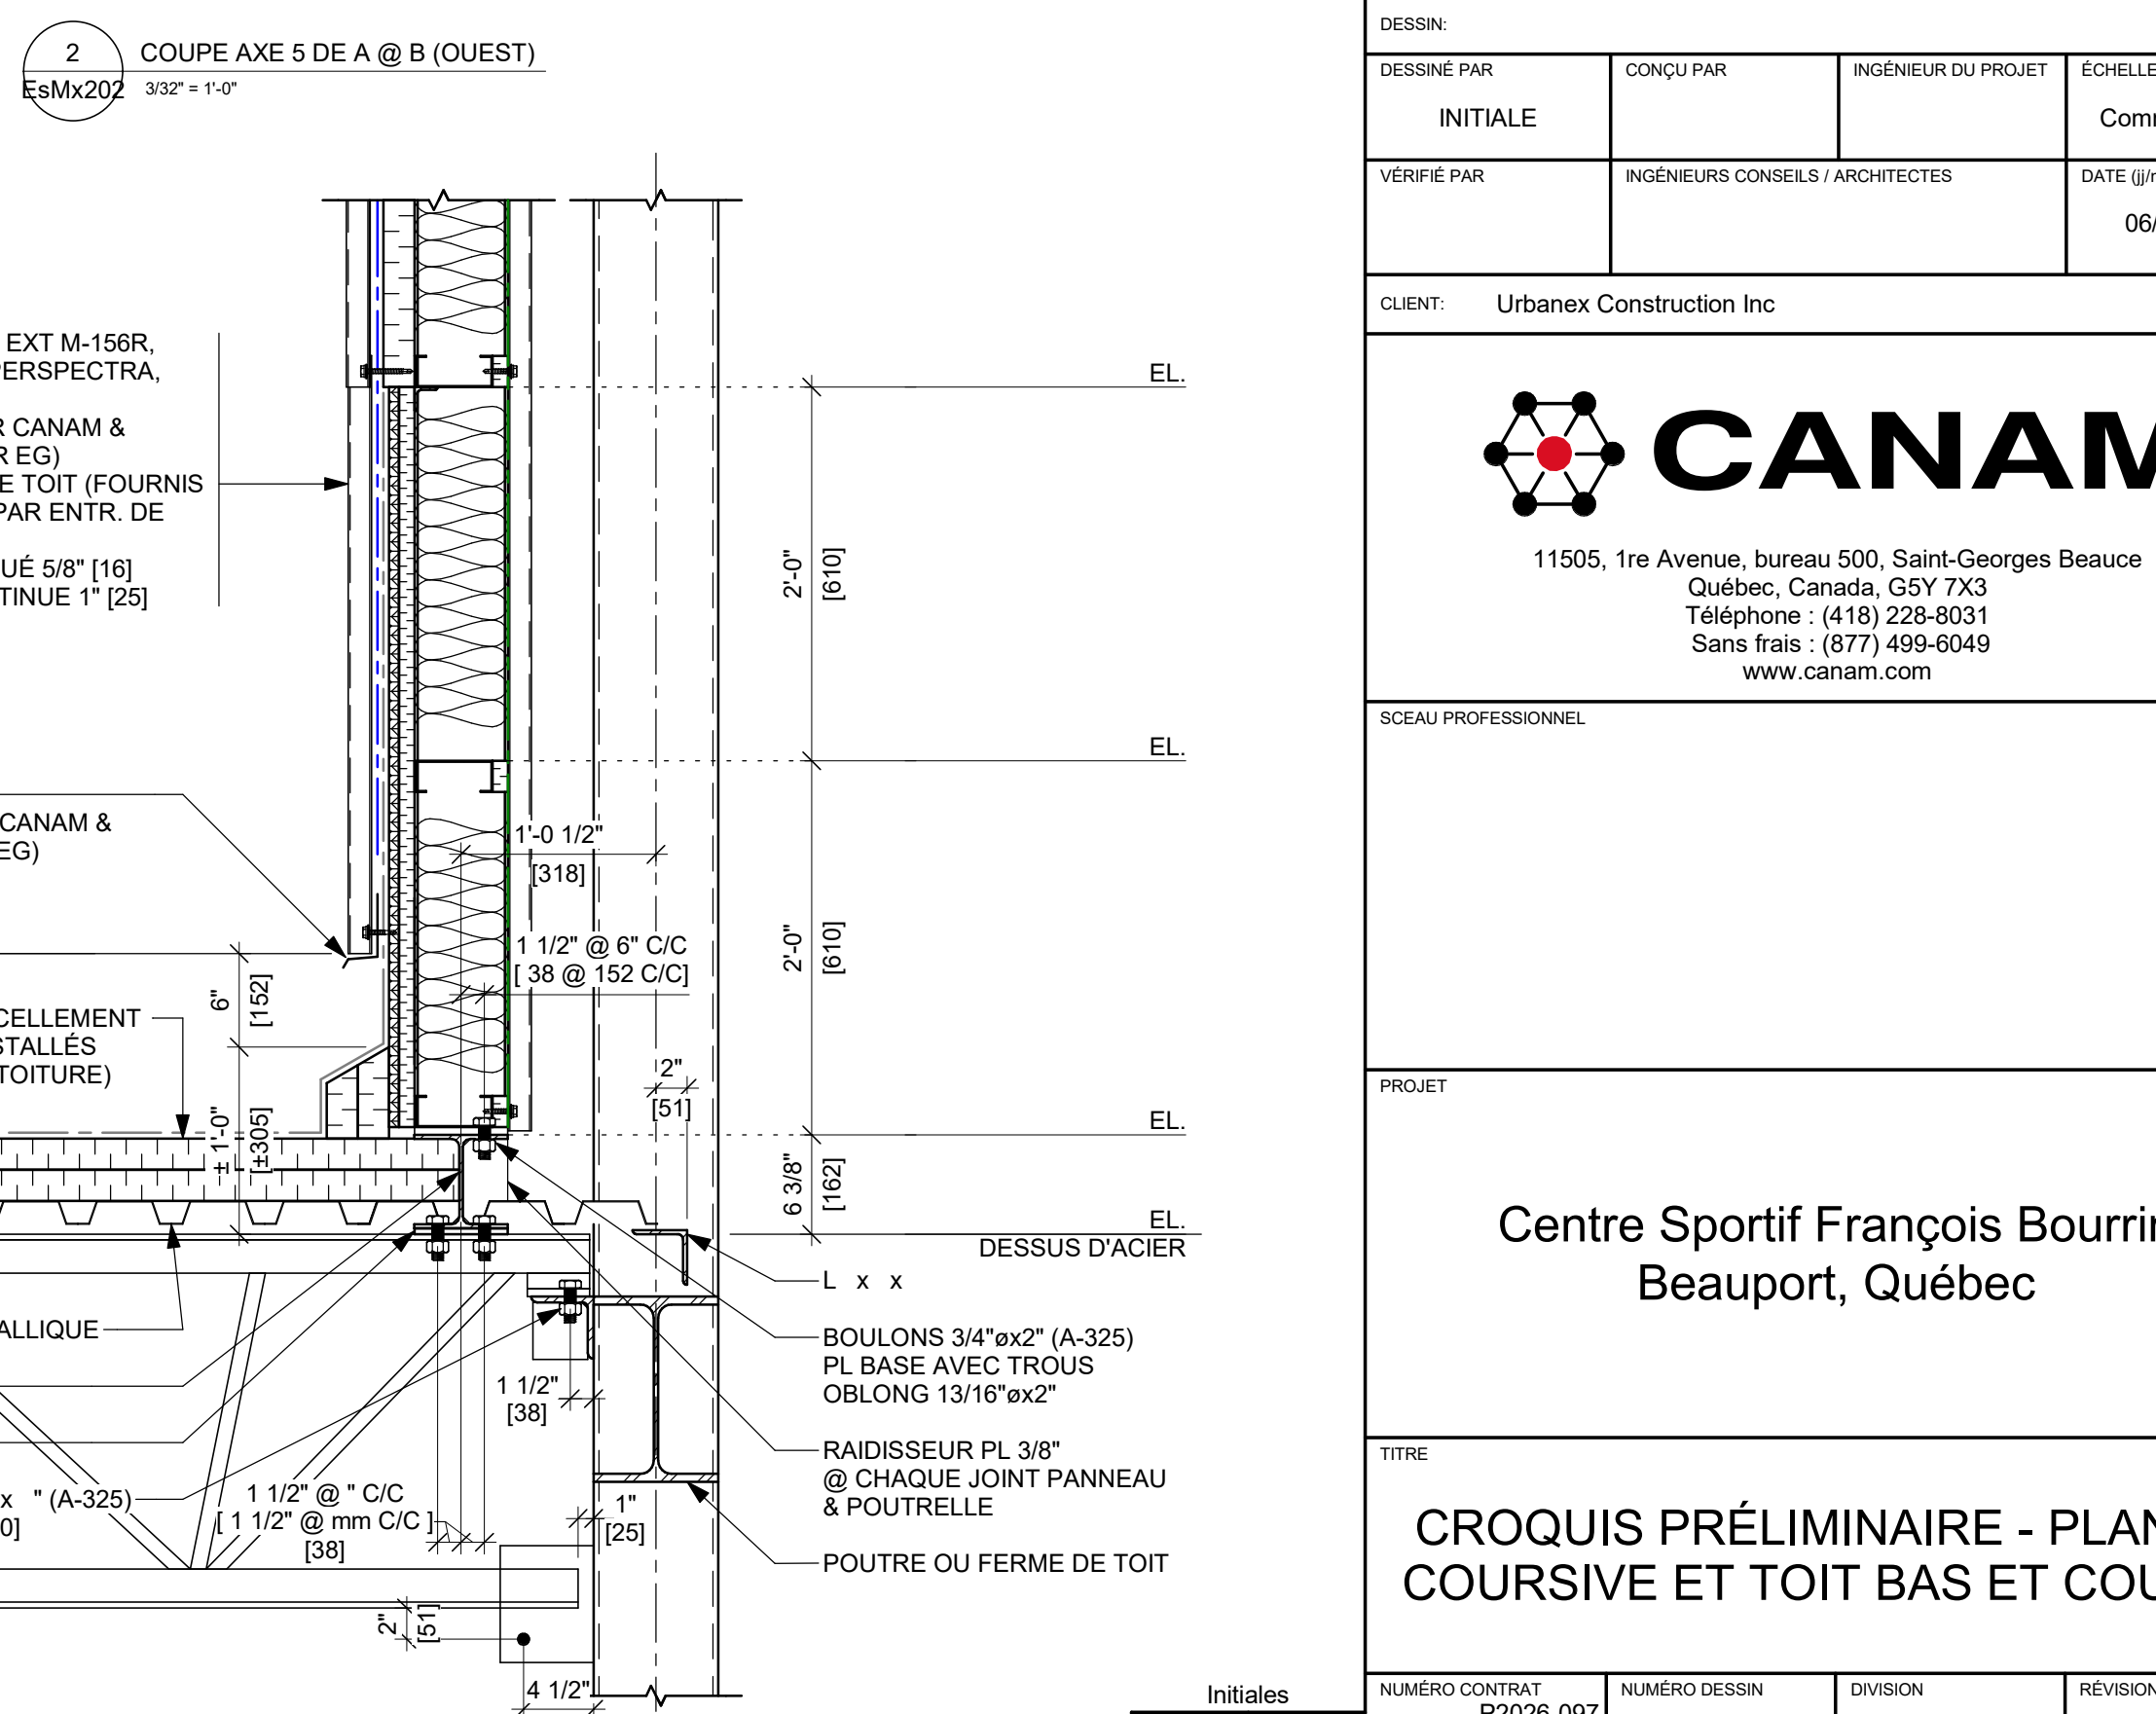
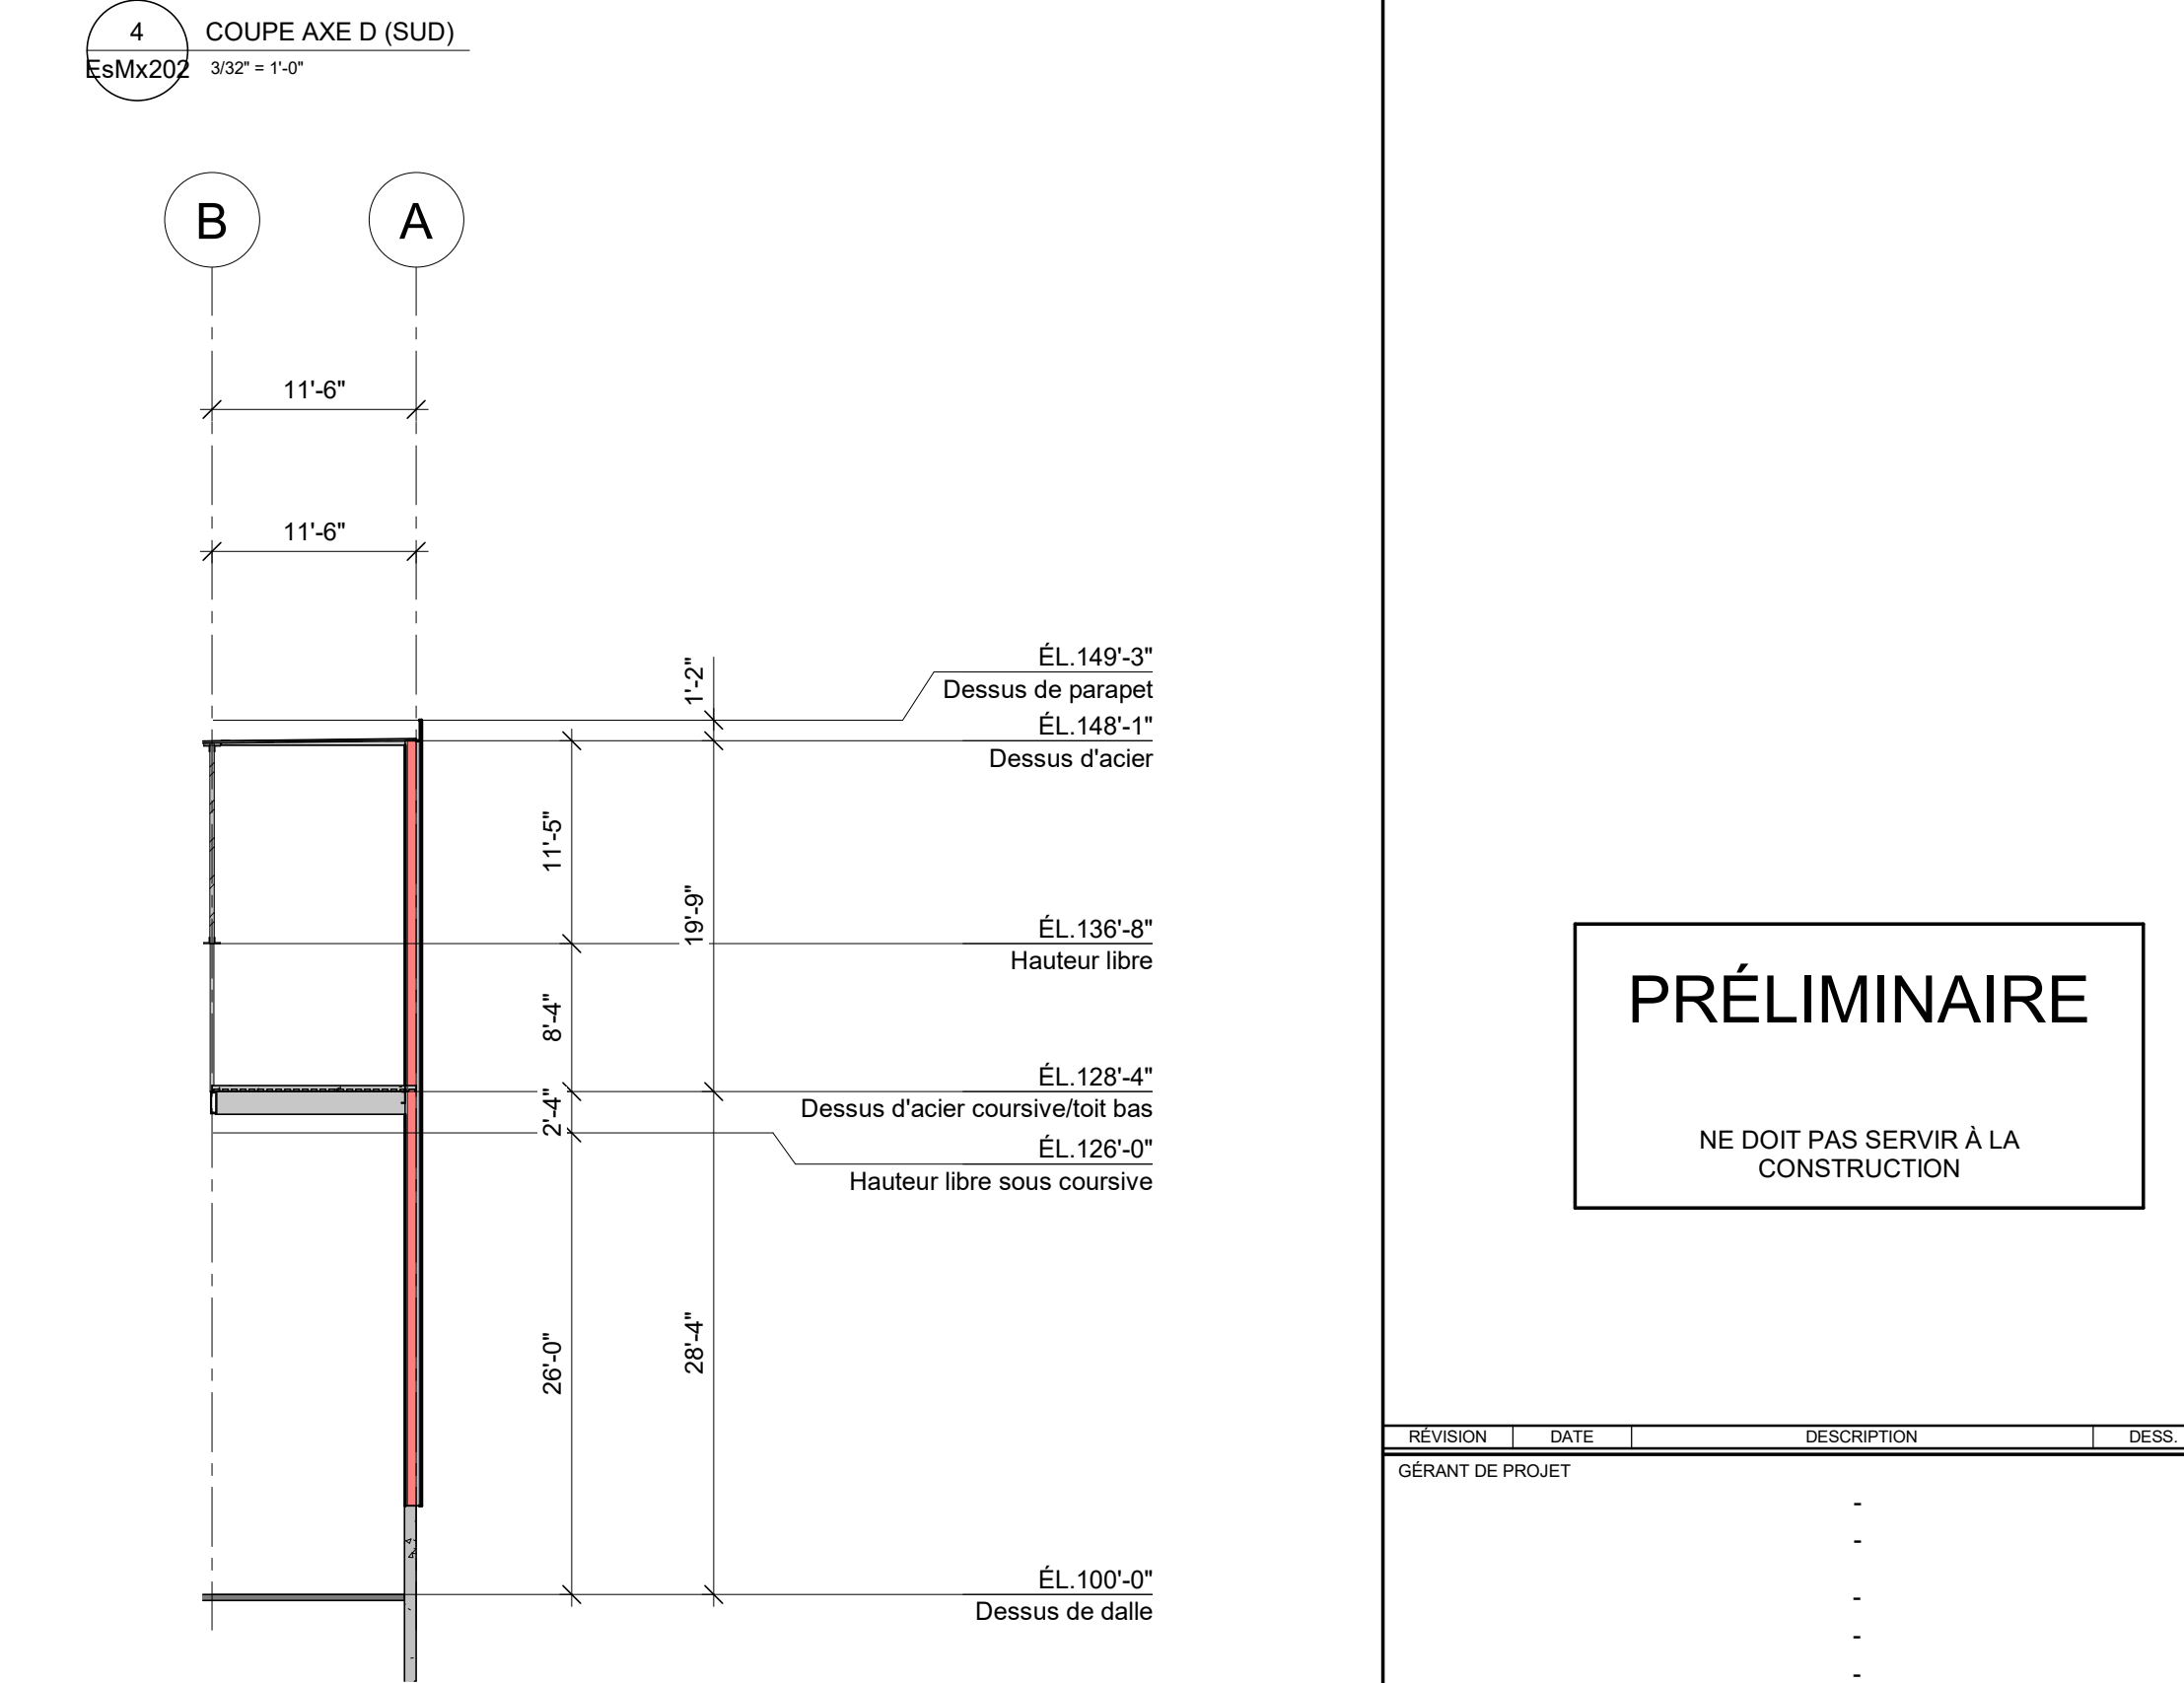


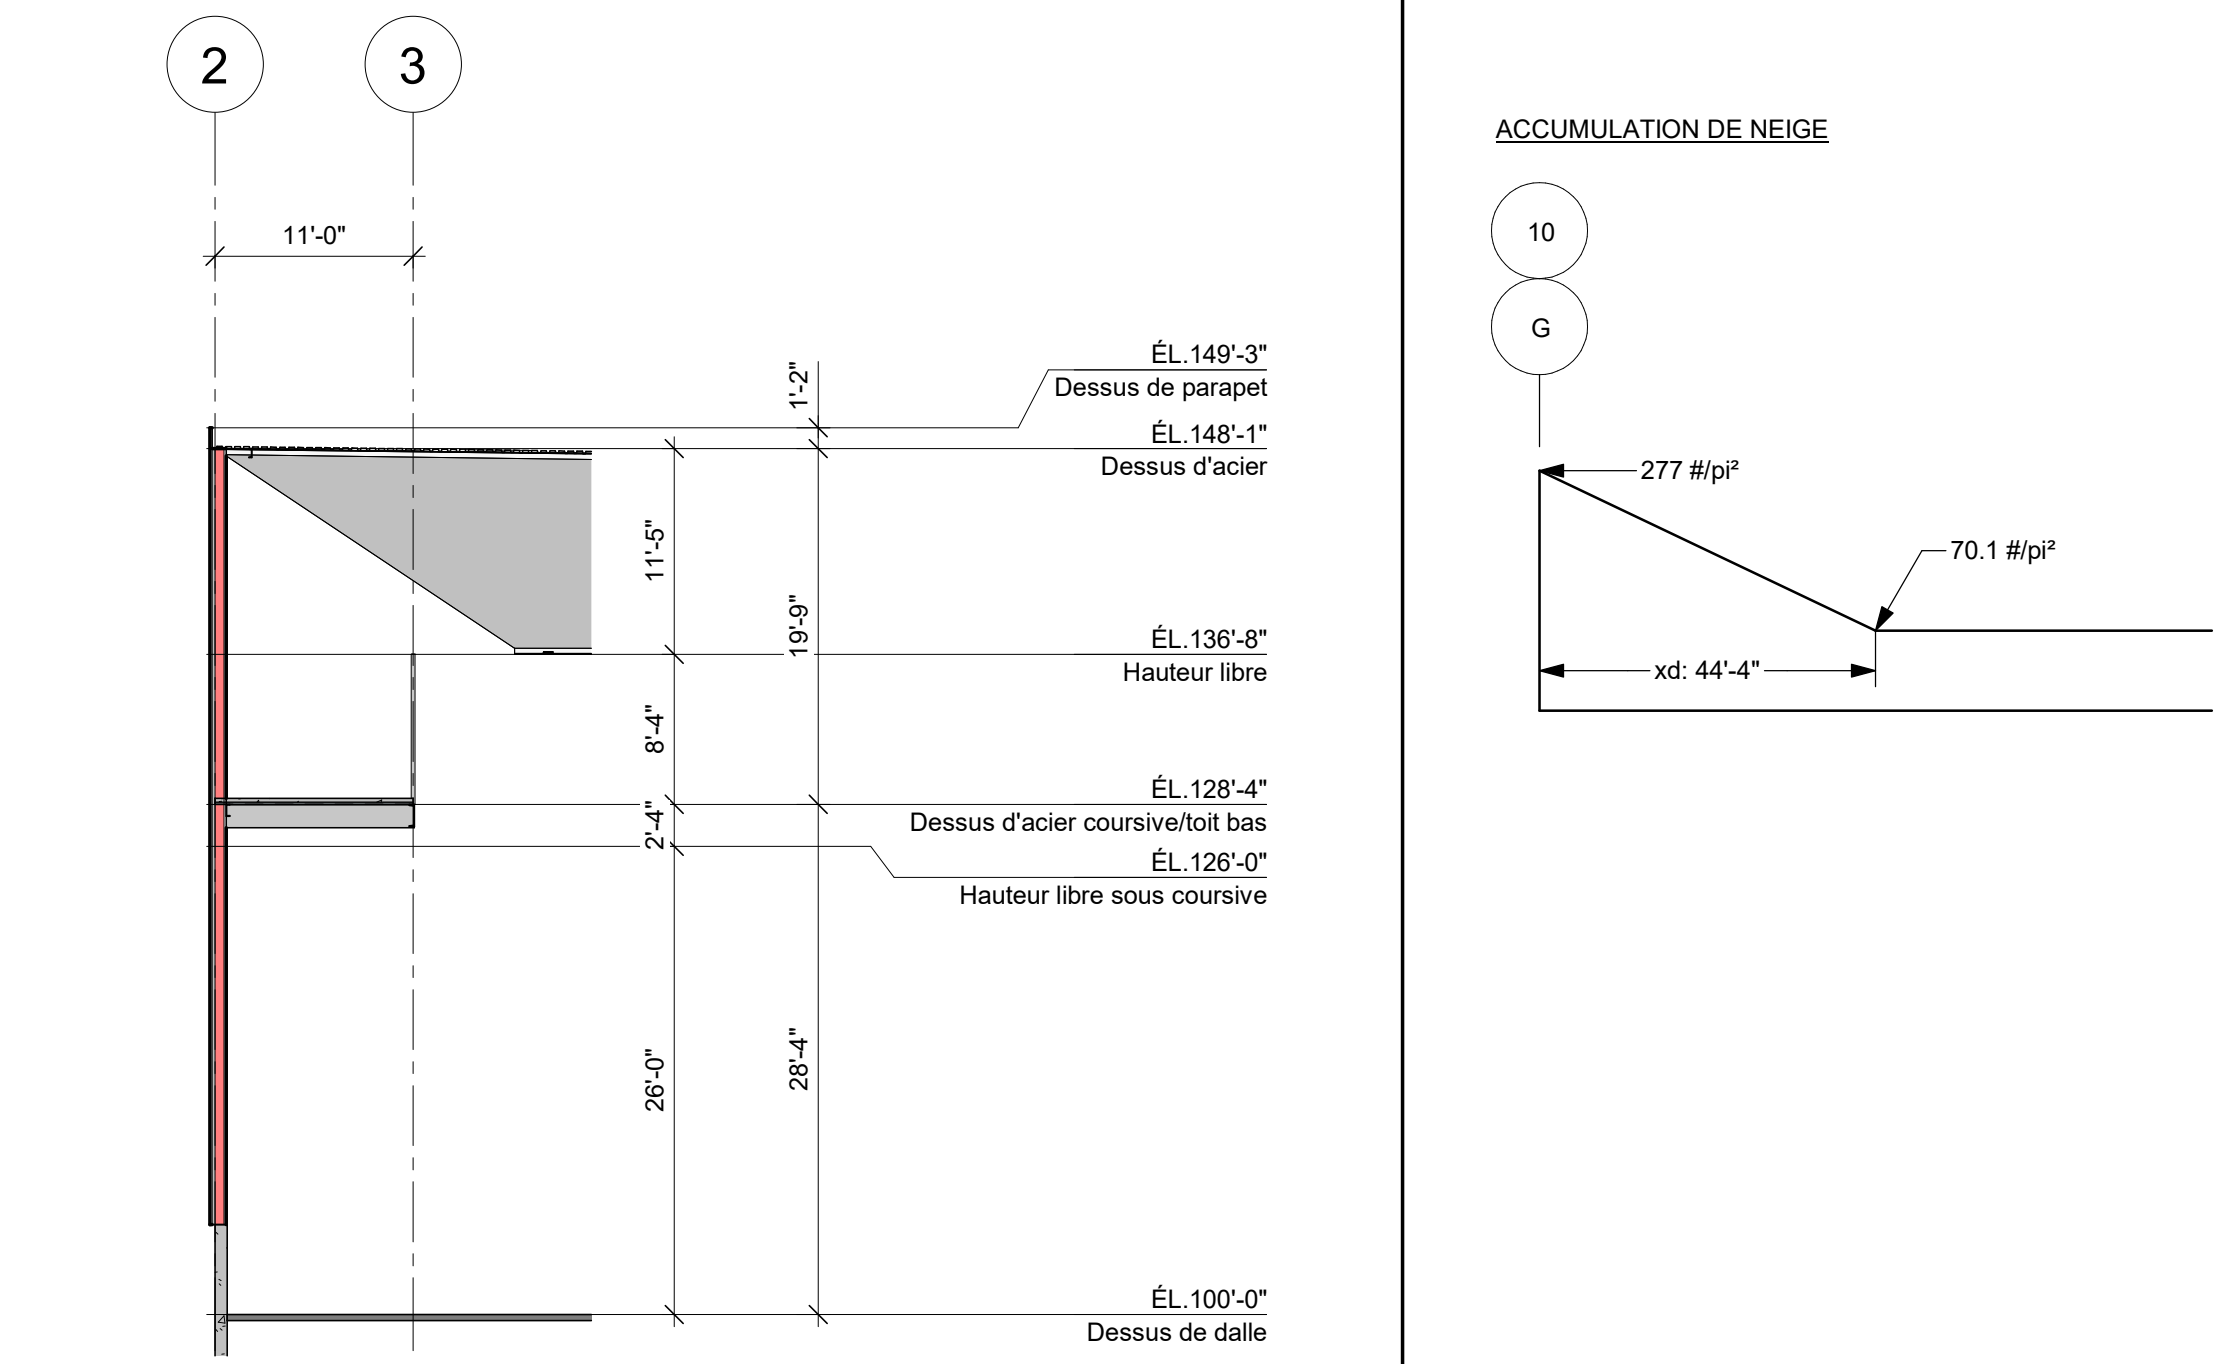

PLAN DE COURSIVE ET TOIT BAS
3/32" = 1'-0"

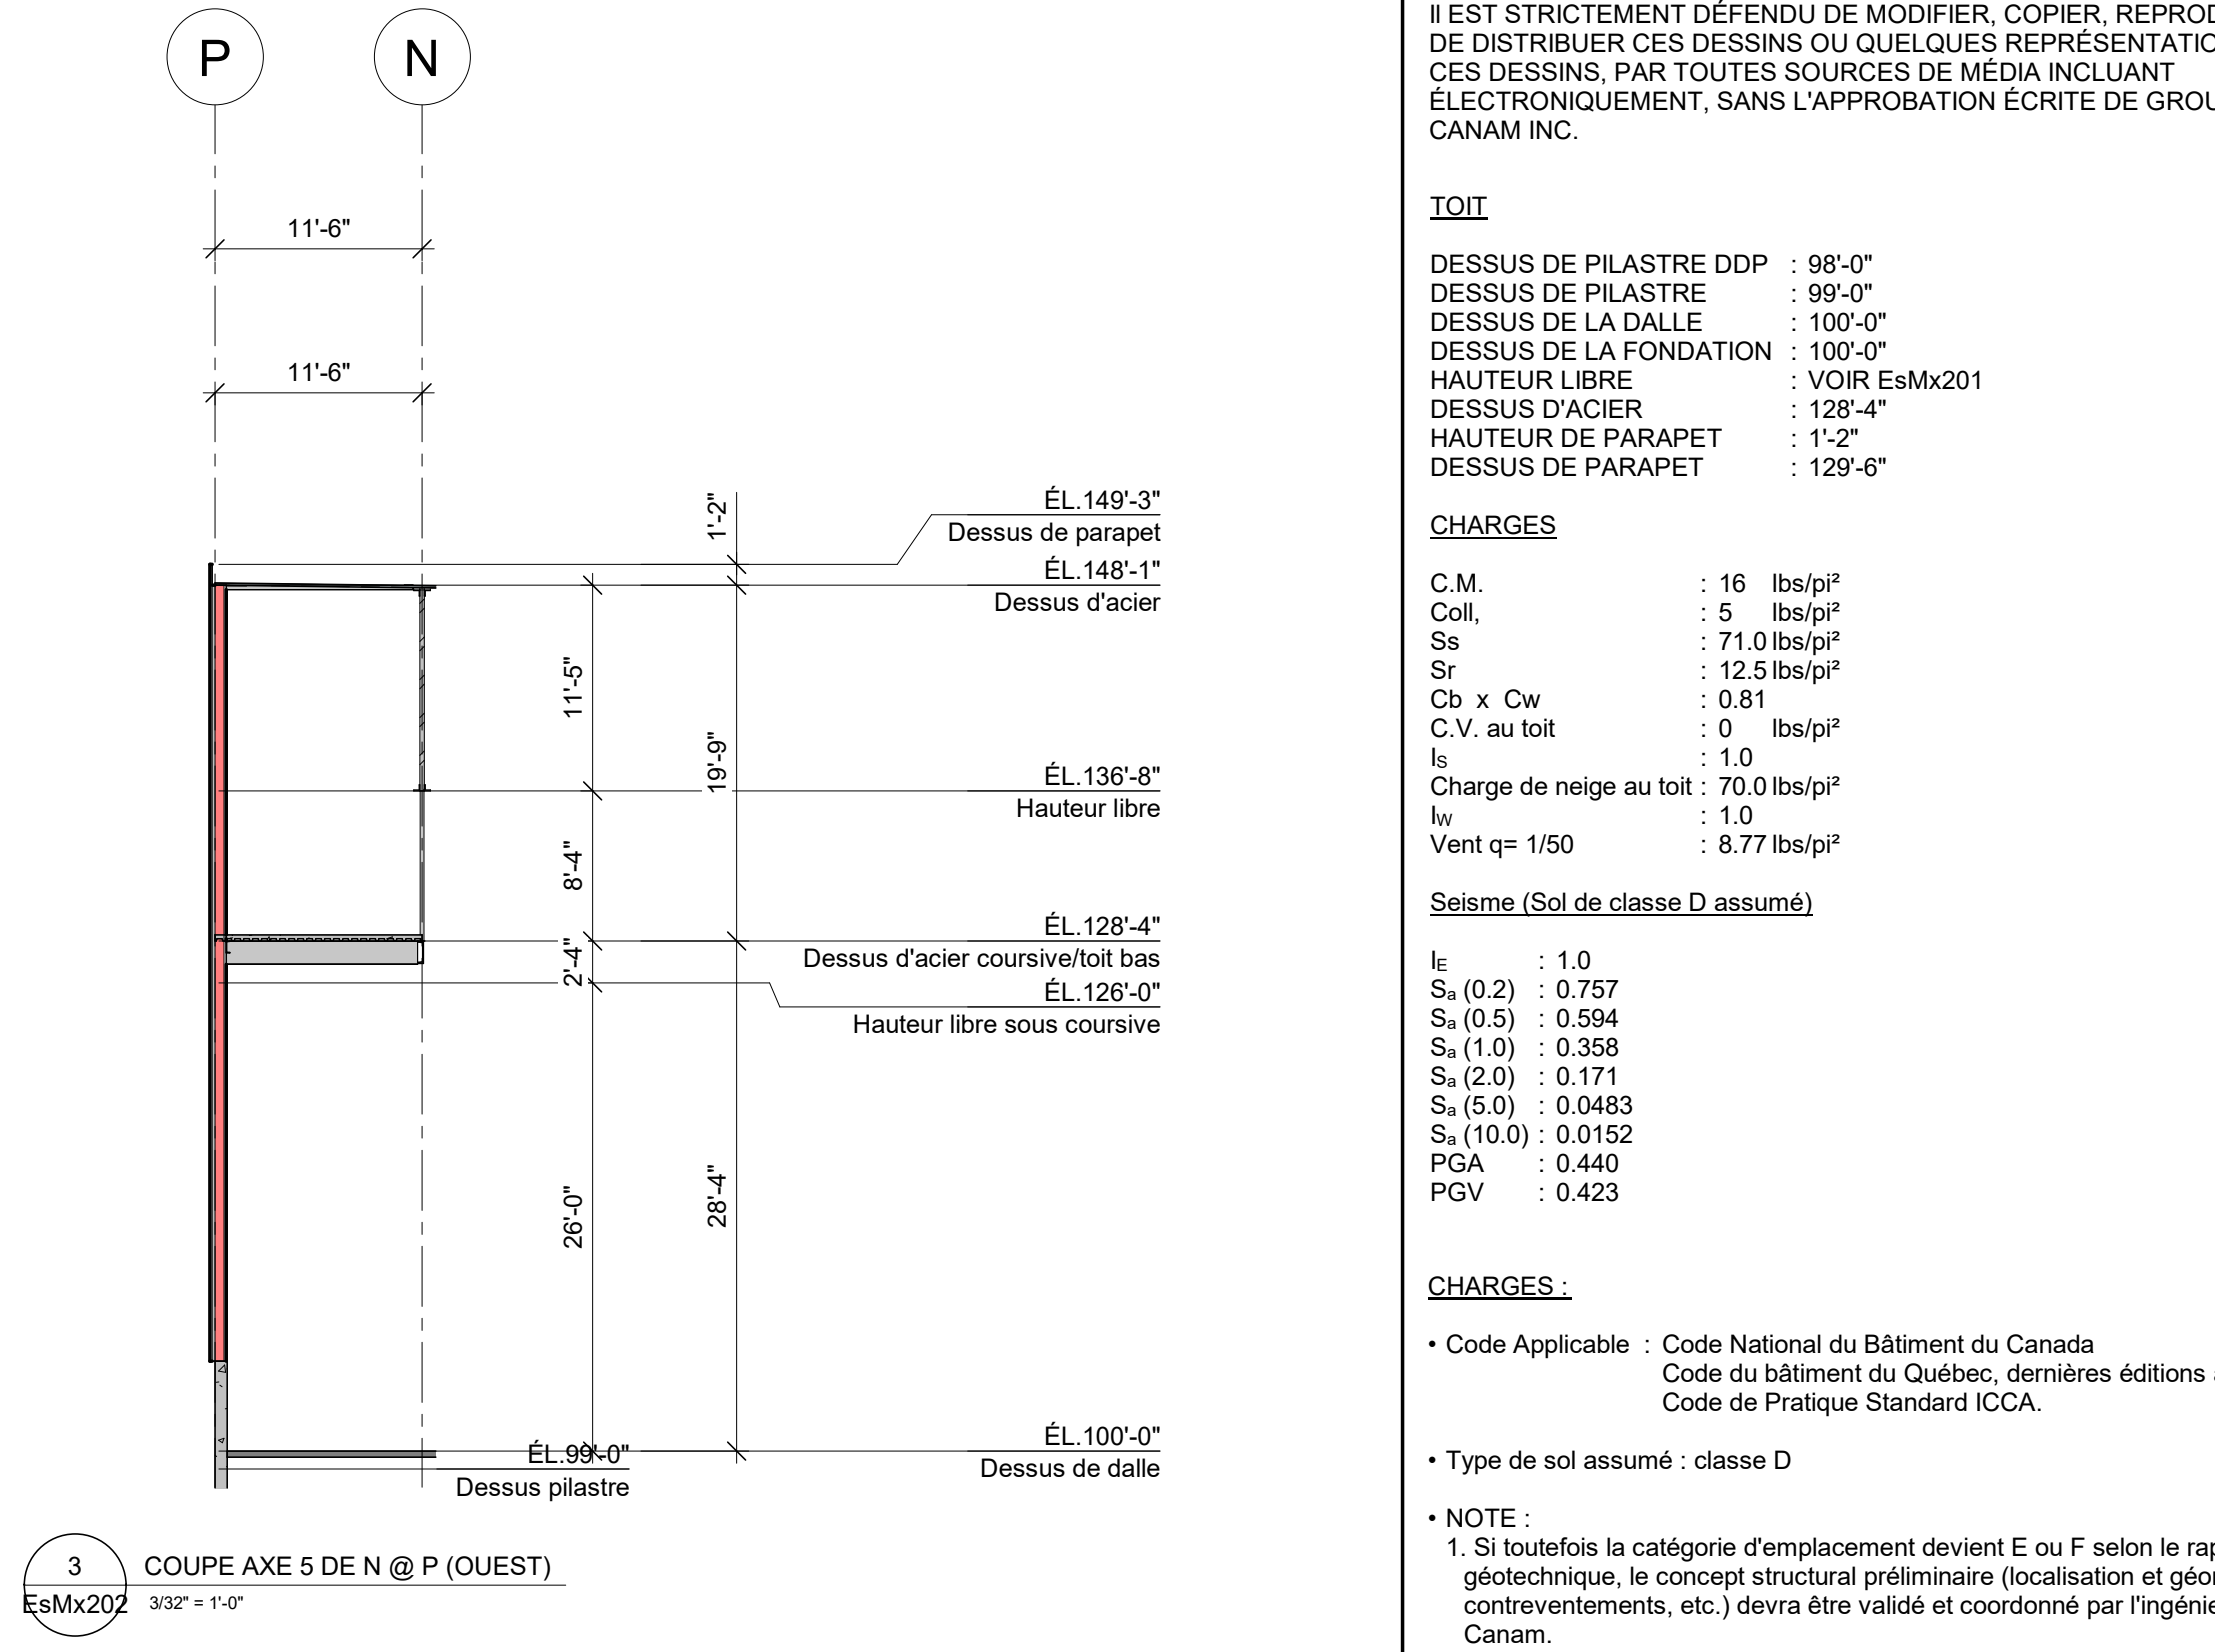

NOTE POUR LE CONTRATEUR/ÉRECTEUR:
IL EST STRICTEMENT DEFENDU DE MODIFIER, COPIER, REPRODUIRE OU DE DISTRIBUER CES DESSINS OU QUELQUES REPRÉSENTATIONS DE CES DESSINS, PAR TOUTES SOURCES DE MÉDIA INCLUANT ÉLECTRONIQUEMENT, SANS L'APPROBATION ÉCRITE DE GROUPE CANAM INC.


TOIT
DESSUS DE PILASTRE DOP : 98'-0"
DESSUS DE PLASTRE : 99'-0"
DESSUS DE LA DALLE : 100'-0"
DESSUS DE LA FONDATION : 100'-0"
HAUTEUR LIBRE : VOIR EAM201
DESSUS D'ACIER : 128'-4"
HAUTEUR DE PARAPET : 1'-2"
DESSUS DE PARAPET : 129'-8"

CHARGES
C.M. : 16 lbs/p²
Coll. : 5 lbs/p²
Sd : 71 lb/p²
Sr : 12.5 lb/p²
Cv x Cw : 0.81
C.V. au toit : 0 lbs/p²
Ch. de neige au toit : 70.0 lb/p²
Lr : 1.0
Vent qe 150 : 8.77 lb/p²
Séisme (Sol de classe D assumé)
I : 1.0
Ss (0.2) : 0.757
Ss (0.5) : 0.594
Ss (1.0) : 0.358
Ss (2.0) : 0.171
Ss (5.0) : 0.043
Ss (10.0) : 0.012
PGA : 0.440
PGV : 0.423

CHARGES :
• Code Applicable : Code National du Bâtiment du Canada
Code du bâtiment du Québec, dernières éditions adoptées
Code de Pratique Standard C.I.A.

• Type de sol assumé : classe D

• NOTE :
1. Si toutefois la catégorie d'emplacement devient E ou F selon le rapport géotechnique, le concept structural préliminaire (localisation et géométrie des contreventements, etc.) devra être validé et coordonné par l'ingénieur de Canam.

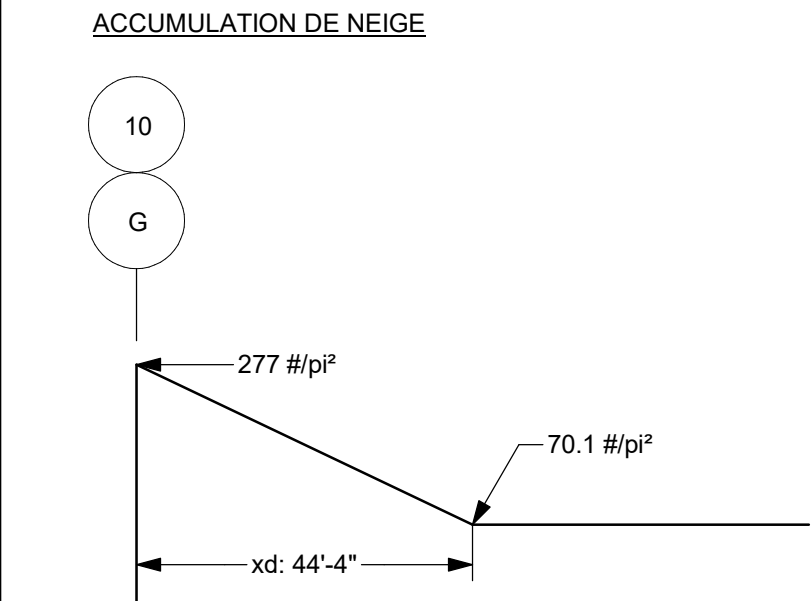

PRÉLIMINAIRE

NE DOIT PAS SERVIR À LA CONSTRUCTION

REVISION	DATE	DESCRIPTION	DESS	VER
GERANT DE PROJET				
.				
.				
