



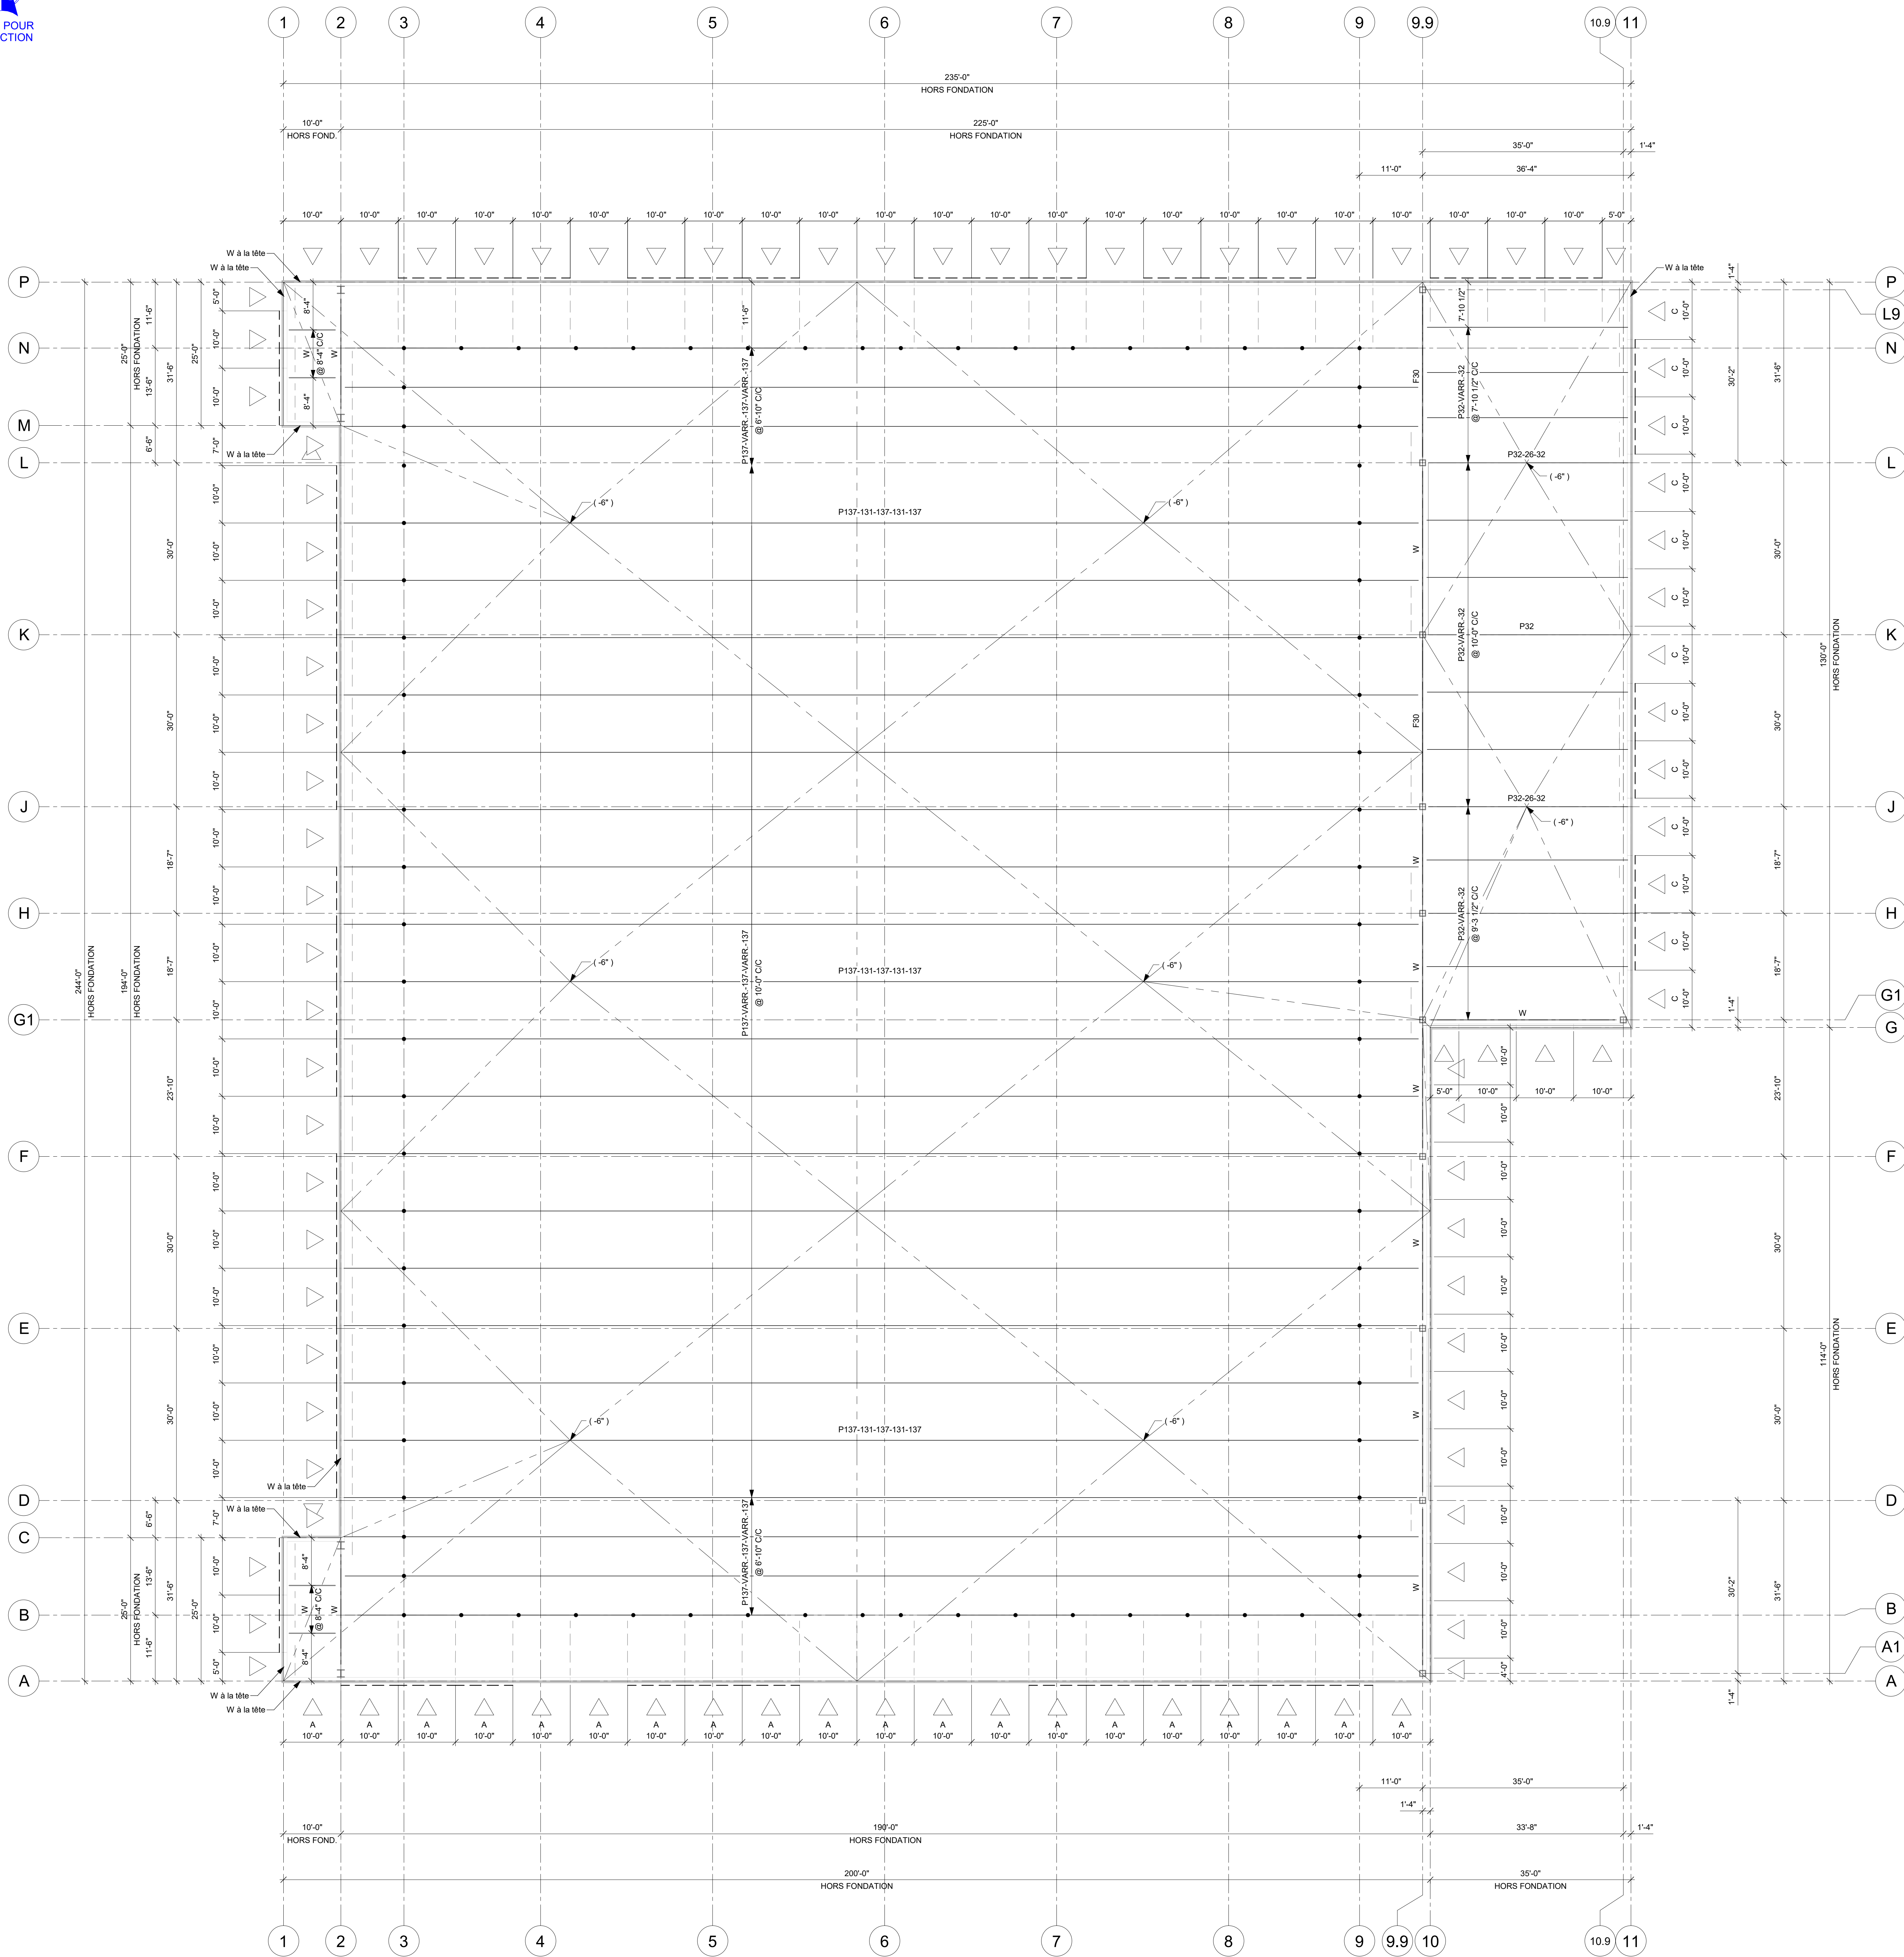

PLAN DE TOIT
3/32" = 1'-0"

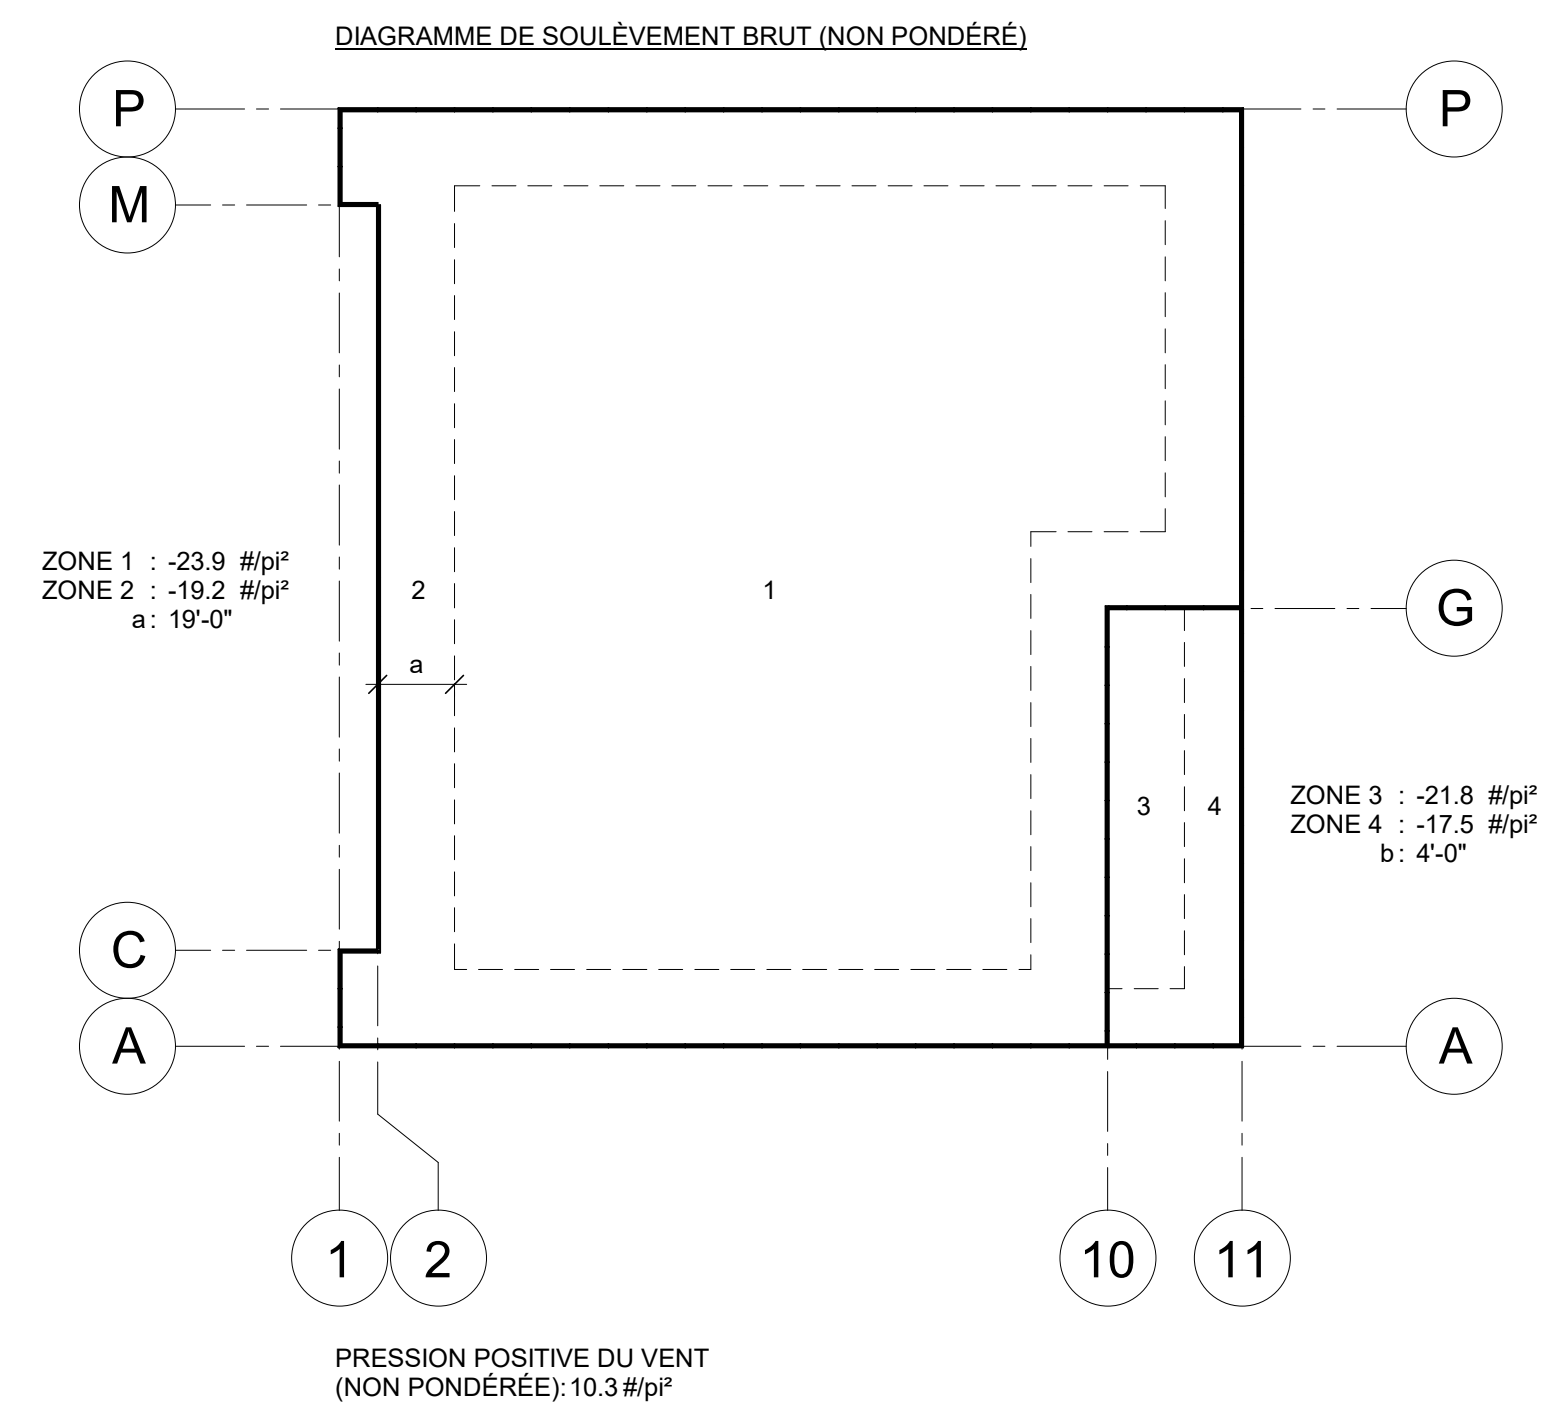

NOTE POUR LE CONTRACTEUR/ÉRECTEUR:
IL EST STRICTEMENT DÉFENDU DE MODIFIER, COPIER, REPRODUIRE OU DE DISTRIBUER CES DESSINS OU QUELQUES REPRÉSENTATIONS DE CES DESSINS, PAR TOUTES SOURCES DE MÉDIA INCLUANT ÉLECTRONIQUEMENT, SANS L'APPROBATION ÉCRITE DE GROUPE CANAM INC.

TOIT

DESSUS DE PILASTRE DOP : 98'-0"
DESSUS DE PILASTRE : 99'-0"
DESSUS DE LA DALLE : 100'-0"
DESSUS DE LA FONDATION : 105'-0"
HAUTEUR LIBRE : 38'-0"
DESSUS D'ACIER : 148'-1"
HAUTEUR DE PARAPET : 1'-2"
DESSUS DE PARAPET : 149'-3"

CHARGES

C.M. (S.I.C.) : 16 lbs/pf
C.M. ENTRE LES AXES 2 ET 9.9 : 24 lbs/pf
C.M. : 5 lbs/pf
S₀ : 71.0 lbs/pf
S₁ : 12.5 lbs/pf
C₀ x C_w : 0.8
C.V. au toit : 0 lbs/pf
Charge de neige au toit : 69.6 lbs/pf
I_s : 1.0
Vent q = 1/50 : 8.77 lbs/pf

Séisme (Sol de classe D assumé)

I_e : 1.0
S_s (0.2) : 0.757
S_s (0.5) : 0.594
S_s (1.0) : 0.358
S_s (2.0) : 0.171
S_s (5.0) : 0.0483
S_s (10.0) : 0.0152
PGA : 0.440
PGV : 0.423

CHARGES

• Code Applicable : Code National du Bâtiment du Canada
Code du bâtiment du Québec, dernières éditions adoptées
Code de Pratique Standard I.C.A.

• Type de sol assumé : classe D

• NOTE :
1. Si toutefois la catégorie d'emplacement devient E ou F selon le rapport géotechnique, le concept structural préliminaire (localisation et géométrie des contreventements, etc.) devra être validé et coordonné par l'ingénieur de Canam.

PRÉLIMINAIRE

NE DOIT PAS SERVIR À LA
CONSTRUCTION

REVISION	DATE	DESCRIPTION	DESS	VER
----------	------	-------------	------	-----

GERANT DE PROJET	-
DESIGN	-
DESIGNER	-
CONCIPI	-
INGÉNIEUR DU PROJET	-
ÉCHELLE	Comme indiqué
VERIFIÉ PAR	INGÉNIEURS CONSEILS / ARCHITECTES
DATE (mm/aa/aaaa)	06/05/2026

CLIENT:	Urbanex Construction Inc
---------	--------------------------



11505, 1^{re} Avenue, bureau 500, Saint-Georges Beauce
Québec, Canada G5Y 7X5
Téléphone : (418) 228-8031
Sans frais : (877) 459-8049
www.canam.com

SCAUX PROFESSIONNEL

PROJET
Centre Sportif François Bourrin
Beauport, Québec

TITRE
CROQUIS PRÉLIMINAIRE - PLAN DE
TOIT

NUMÉRO CONTRAT	NUMÉRO DESSIN	DIVISION	REVISION
P2026-097	EsMx401		

Initiales

