



CÉDULE DES PORTES			
Identifiant	Qté	Porte 19 in.	Remarques
P1	6	3'-0" x 7'-0"	
P2	3	20'-0" x 20'-0"	CADRE POUR PORTE MONTANTE
P3	2	5'-0" x 20'-0"	CADRE POUR PORTE MONTANTE

Quincaillerie standard du fournisseur:
- Charnières : Stanley F88 179 4.5" x 4"
- Barre panique : Von Duprin 22 x 689 avec poignée extérieure 230L
- Cylindre permanent : Schlage 20001C 626
- Ferme-porte : LCN 1261 689
- Coupe-froid de tête et des montants : Unique 1650
- Coupe-froid du bas : Unique D54
- Seul : Voir la remarque dans la "Cédule de porte"

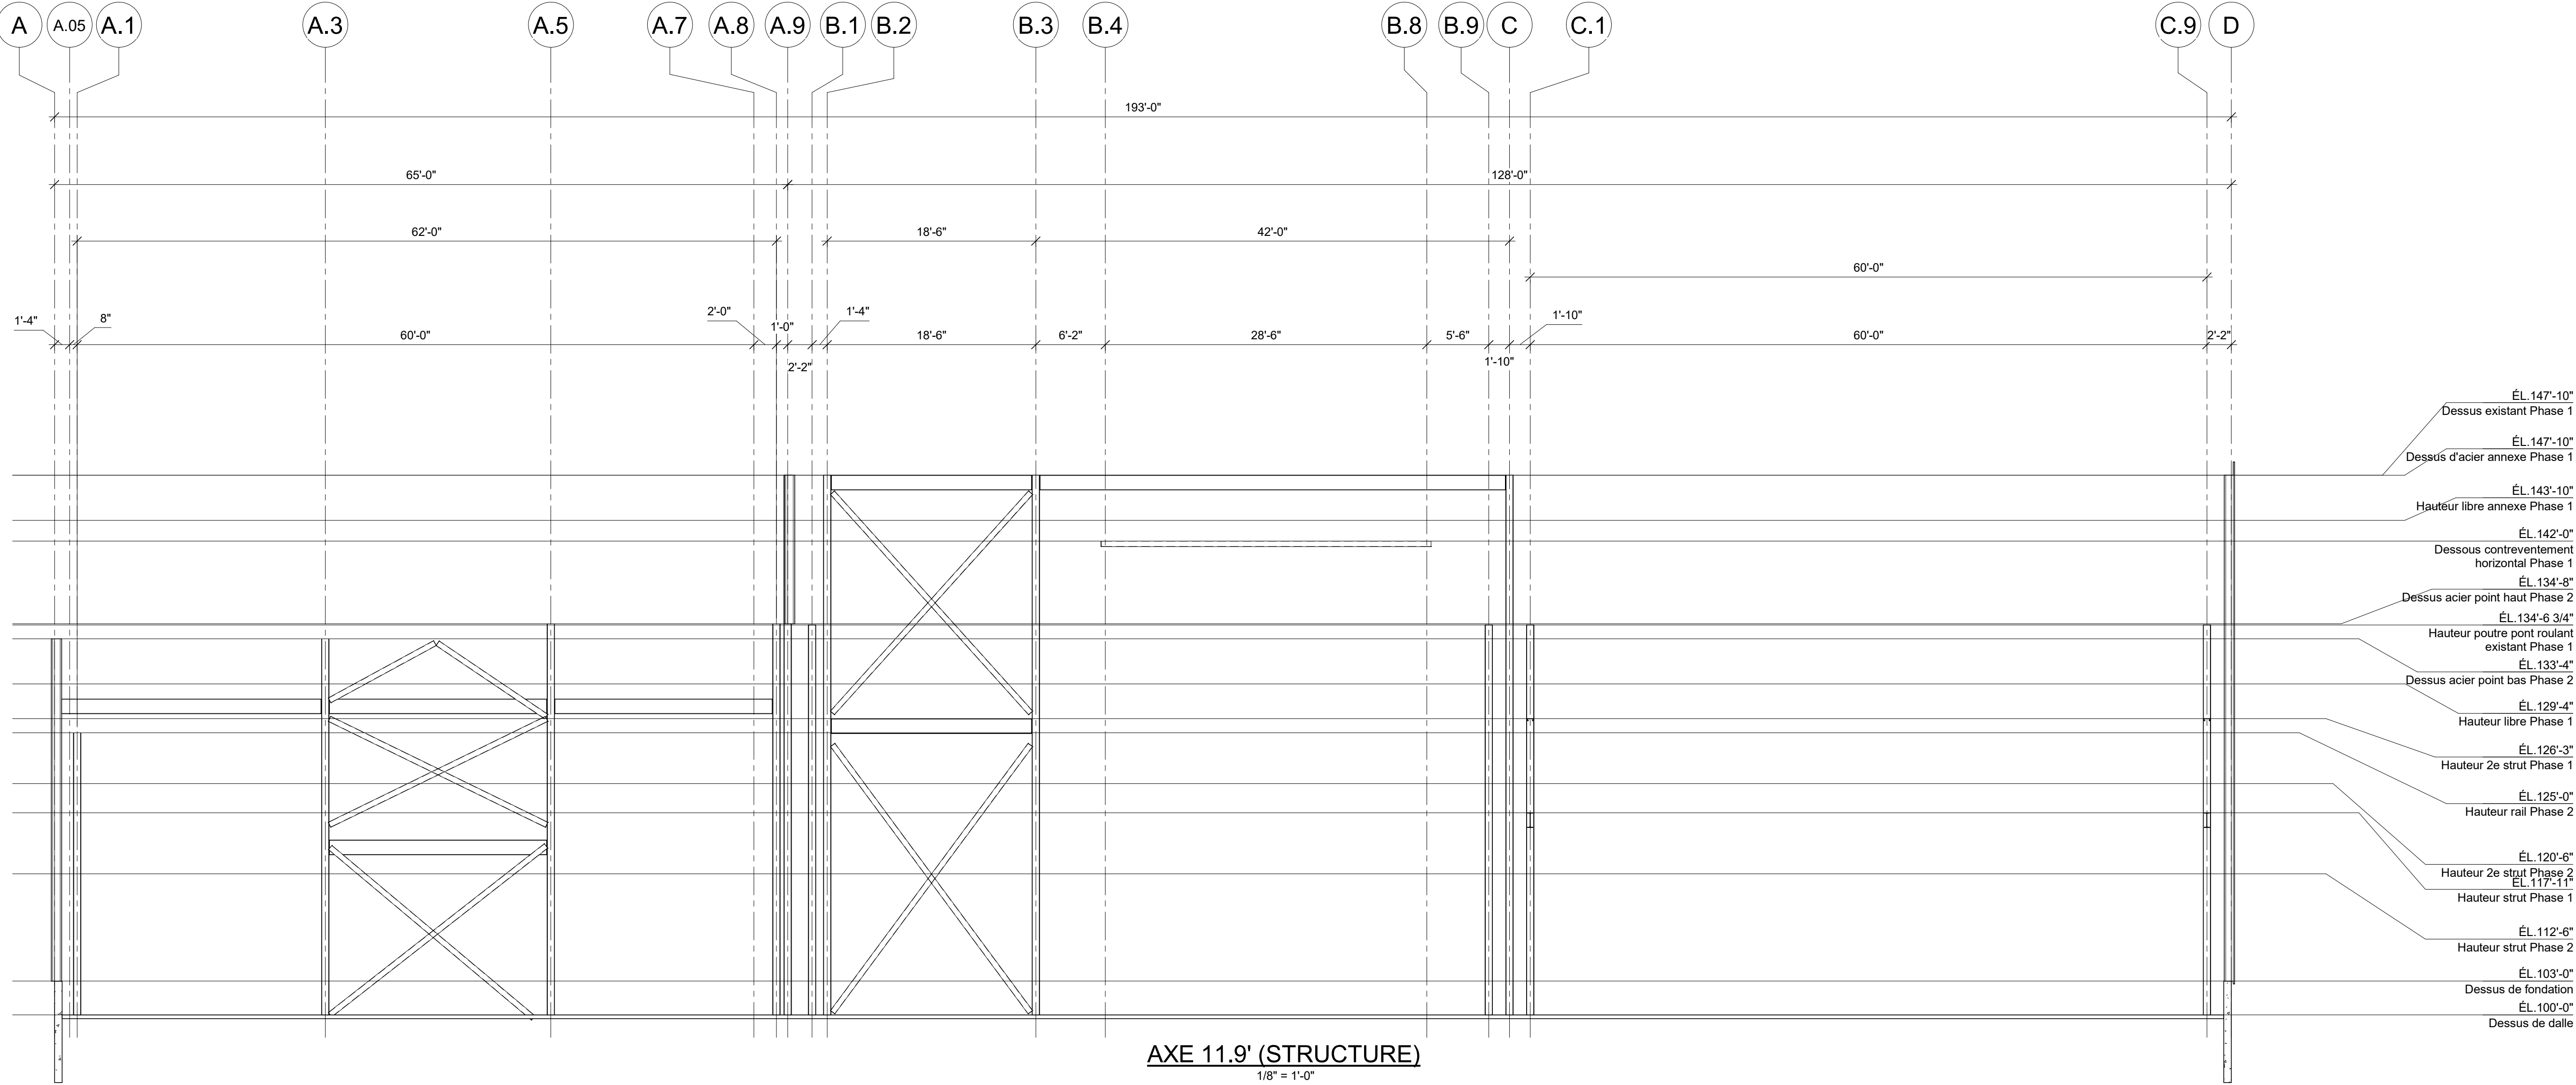


AXE 11.9' (STRUCTURE)

1/8" = 1'-0"

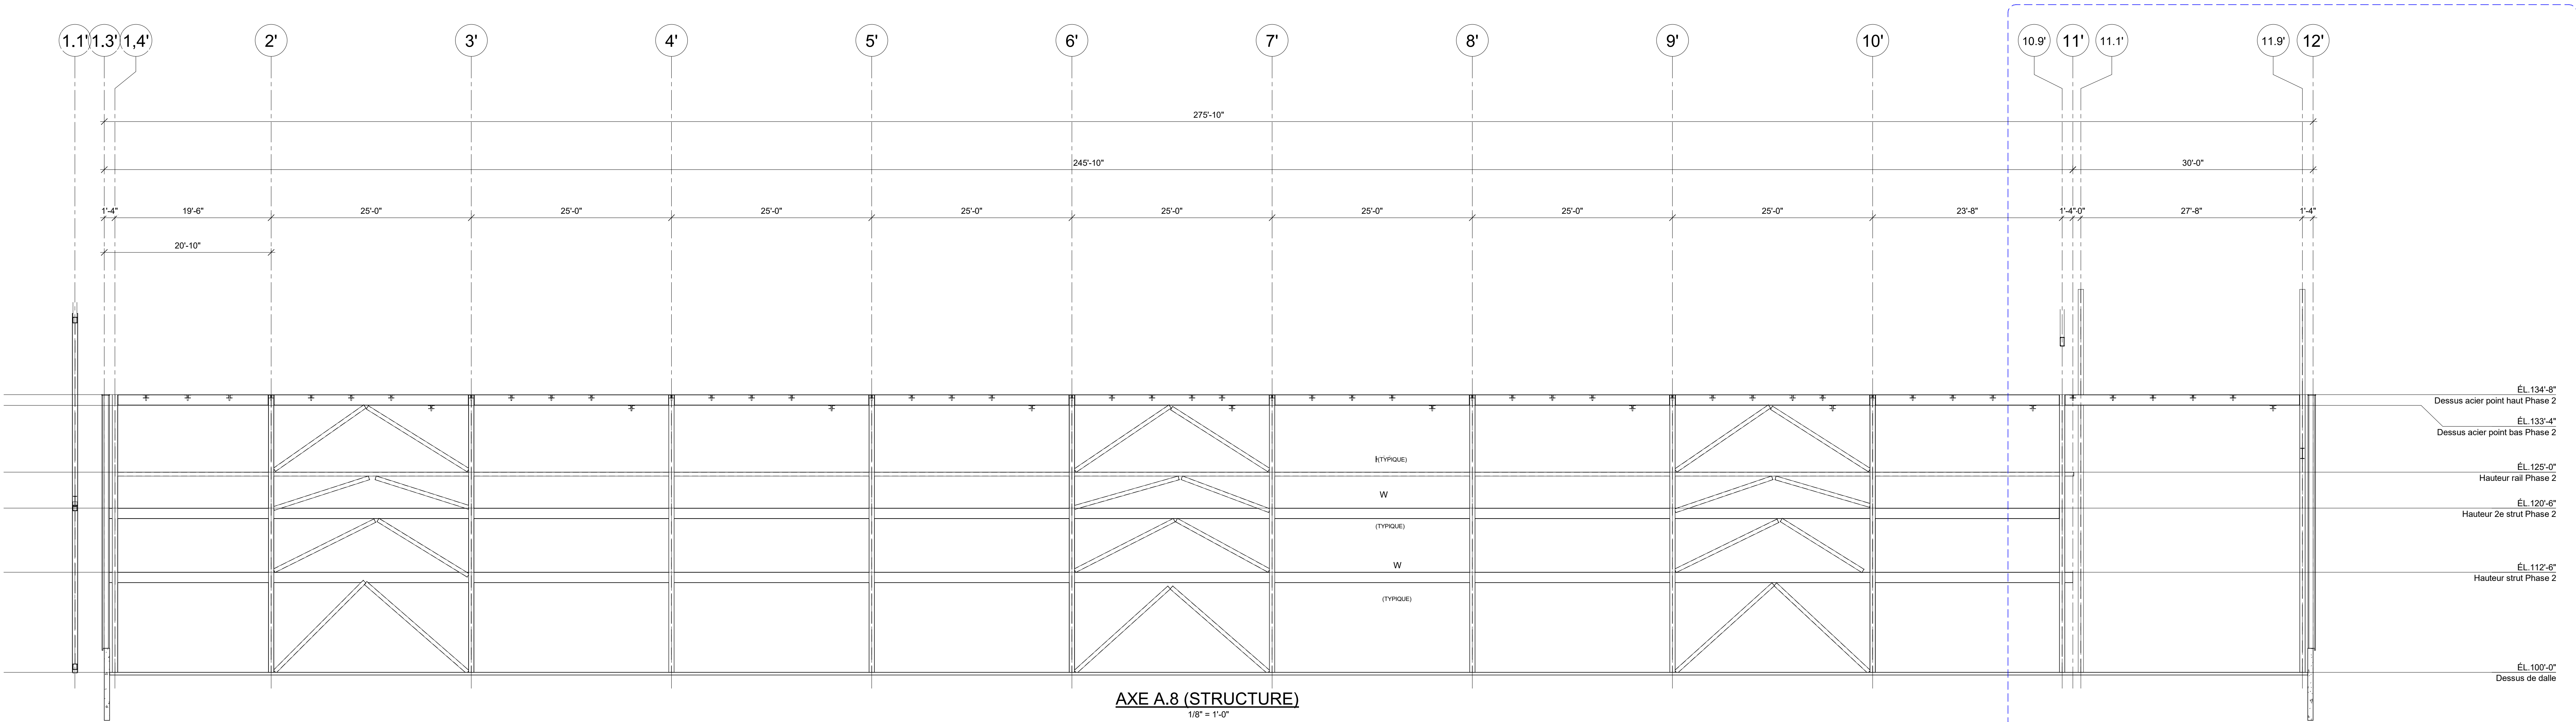

AXE A.8 (STRUCTURE)

1/8" = 1'-0"

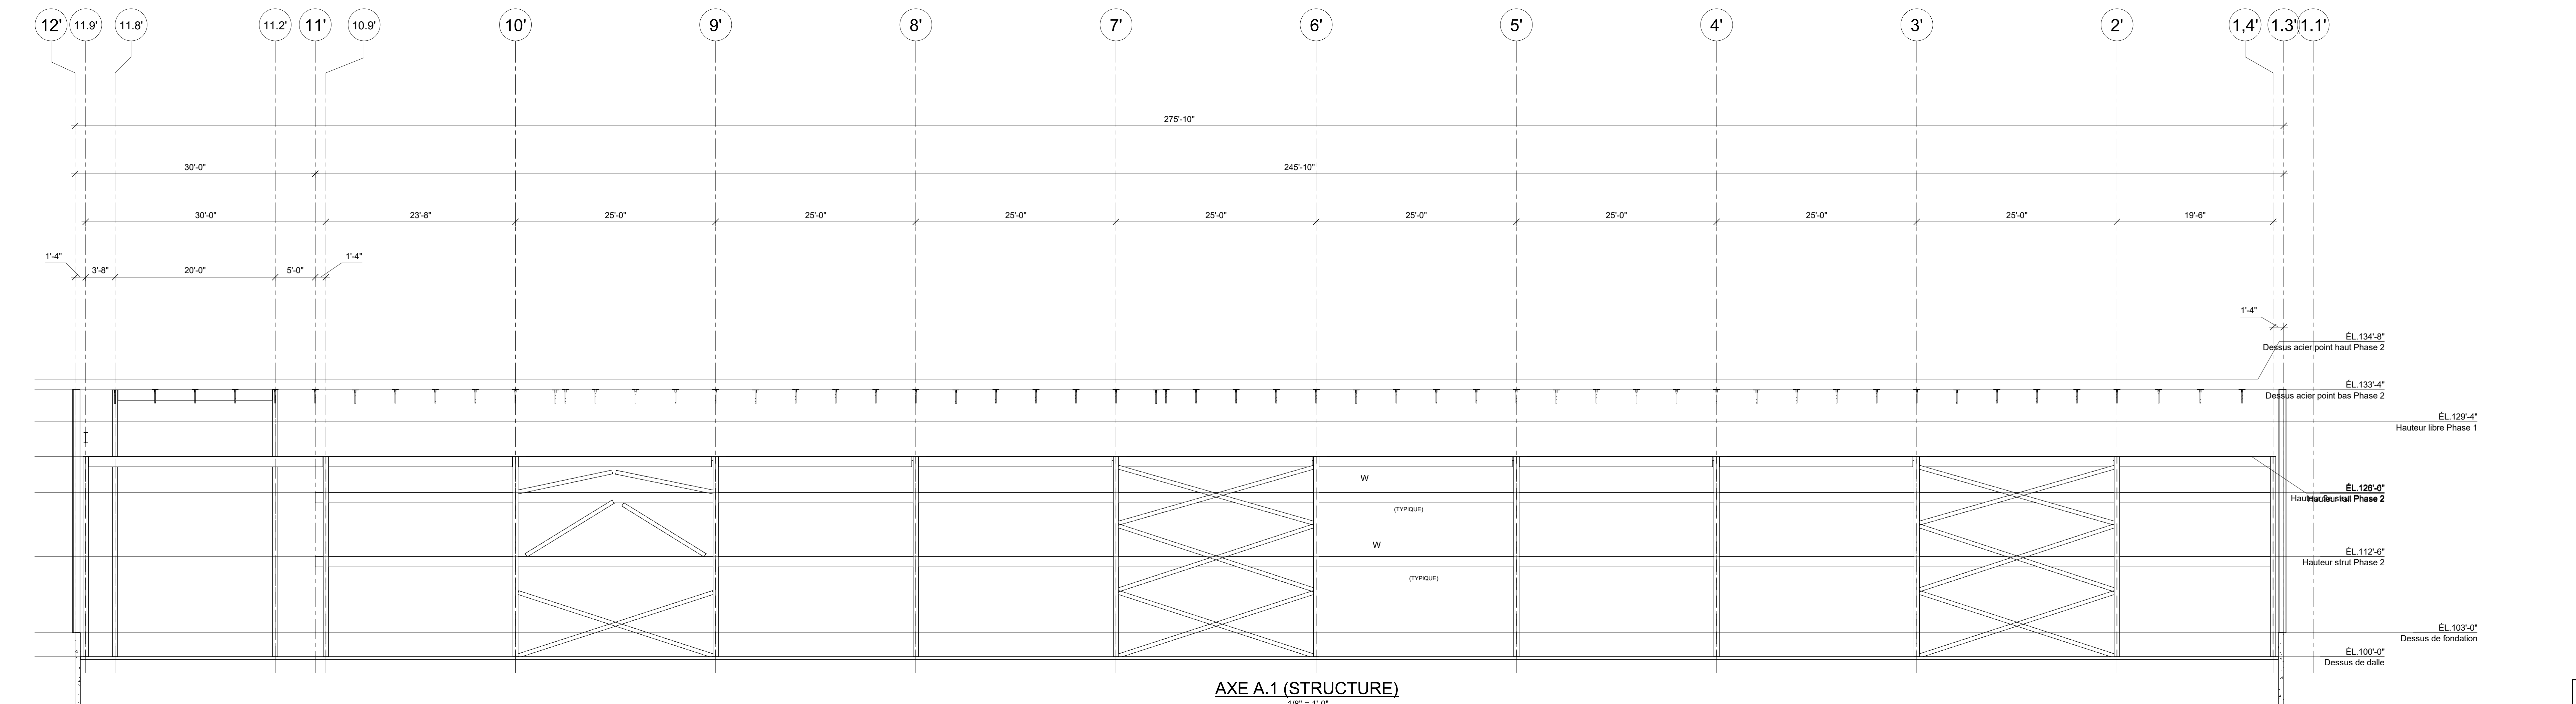

AXE A.1 (STRUCTURE)

1/8" = 1'-0"

NOTE POUR LE CONTRACTEUR/ÉRECTEUR:
IL EST STRICTEMENT DÉFENDU DE MODIFIER, COPIER, REPRODUIRE OU DE DISTRIBUER CES DESSINS OU QUELQUES REPRÉSENTATIONS DE CES DESSINS, PAR TOUTES SOURCES DE MÉDIA INCLUANT ÉLECTRONIQUEMENT, SANS L'APPROBATION ÉCRITE DE GROUPE CANAM INC.

PRÉLIMINAIRE

NE DOIT PAS SERVIR À LA CONSTRUCTION

REVISION	DATE	DESCRIPTION	DESS	VER
----------	------	-------------	------	-----

DESSIN DE PROJET	-
	-
	-

DESSIN	
--------	--

DESSINÉ PAR	CONÇU PAR	INGÉNIEUR DU PROJET	ÉCHELLE:
-------------	-----------	---------------------	----------

INITIALE			Comme indiqué
----------	--	--	---------------

VÉRIFIÉ PAR	INGÉNIEURS CONSEILS / ARCHITECTES	DATE (mm/aa/aaaa)
-------------	-----------------------------------	-------------------

		22/05/2026
--	--	------------

CLIENT:	LIXM ENTREPRENEUR GÉNÉRAL INC.
---------	--------------------------------



SCAUX PROFESSIONNEL	
---------------------	--

PROJET	
--------	--

--	--

--	--

--	--

--	--

--	--

--	--

--	--

--	--

--	--

--	--

--	--

--	--

--	--

--	--

--	--