


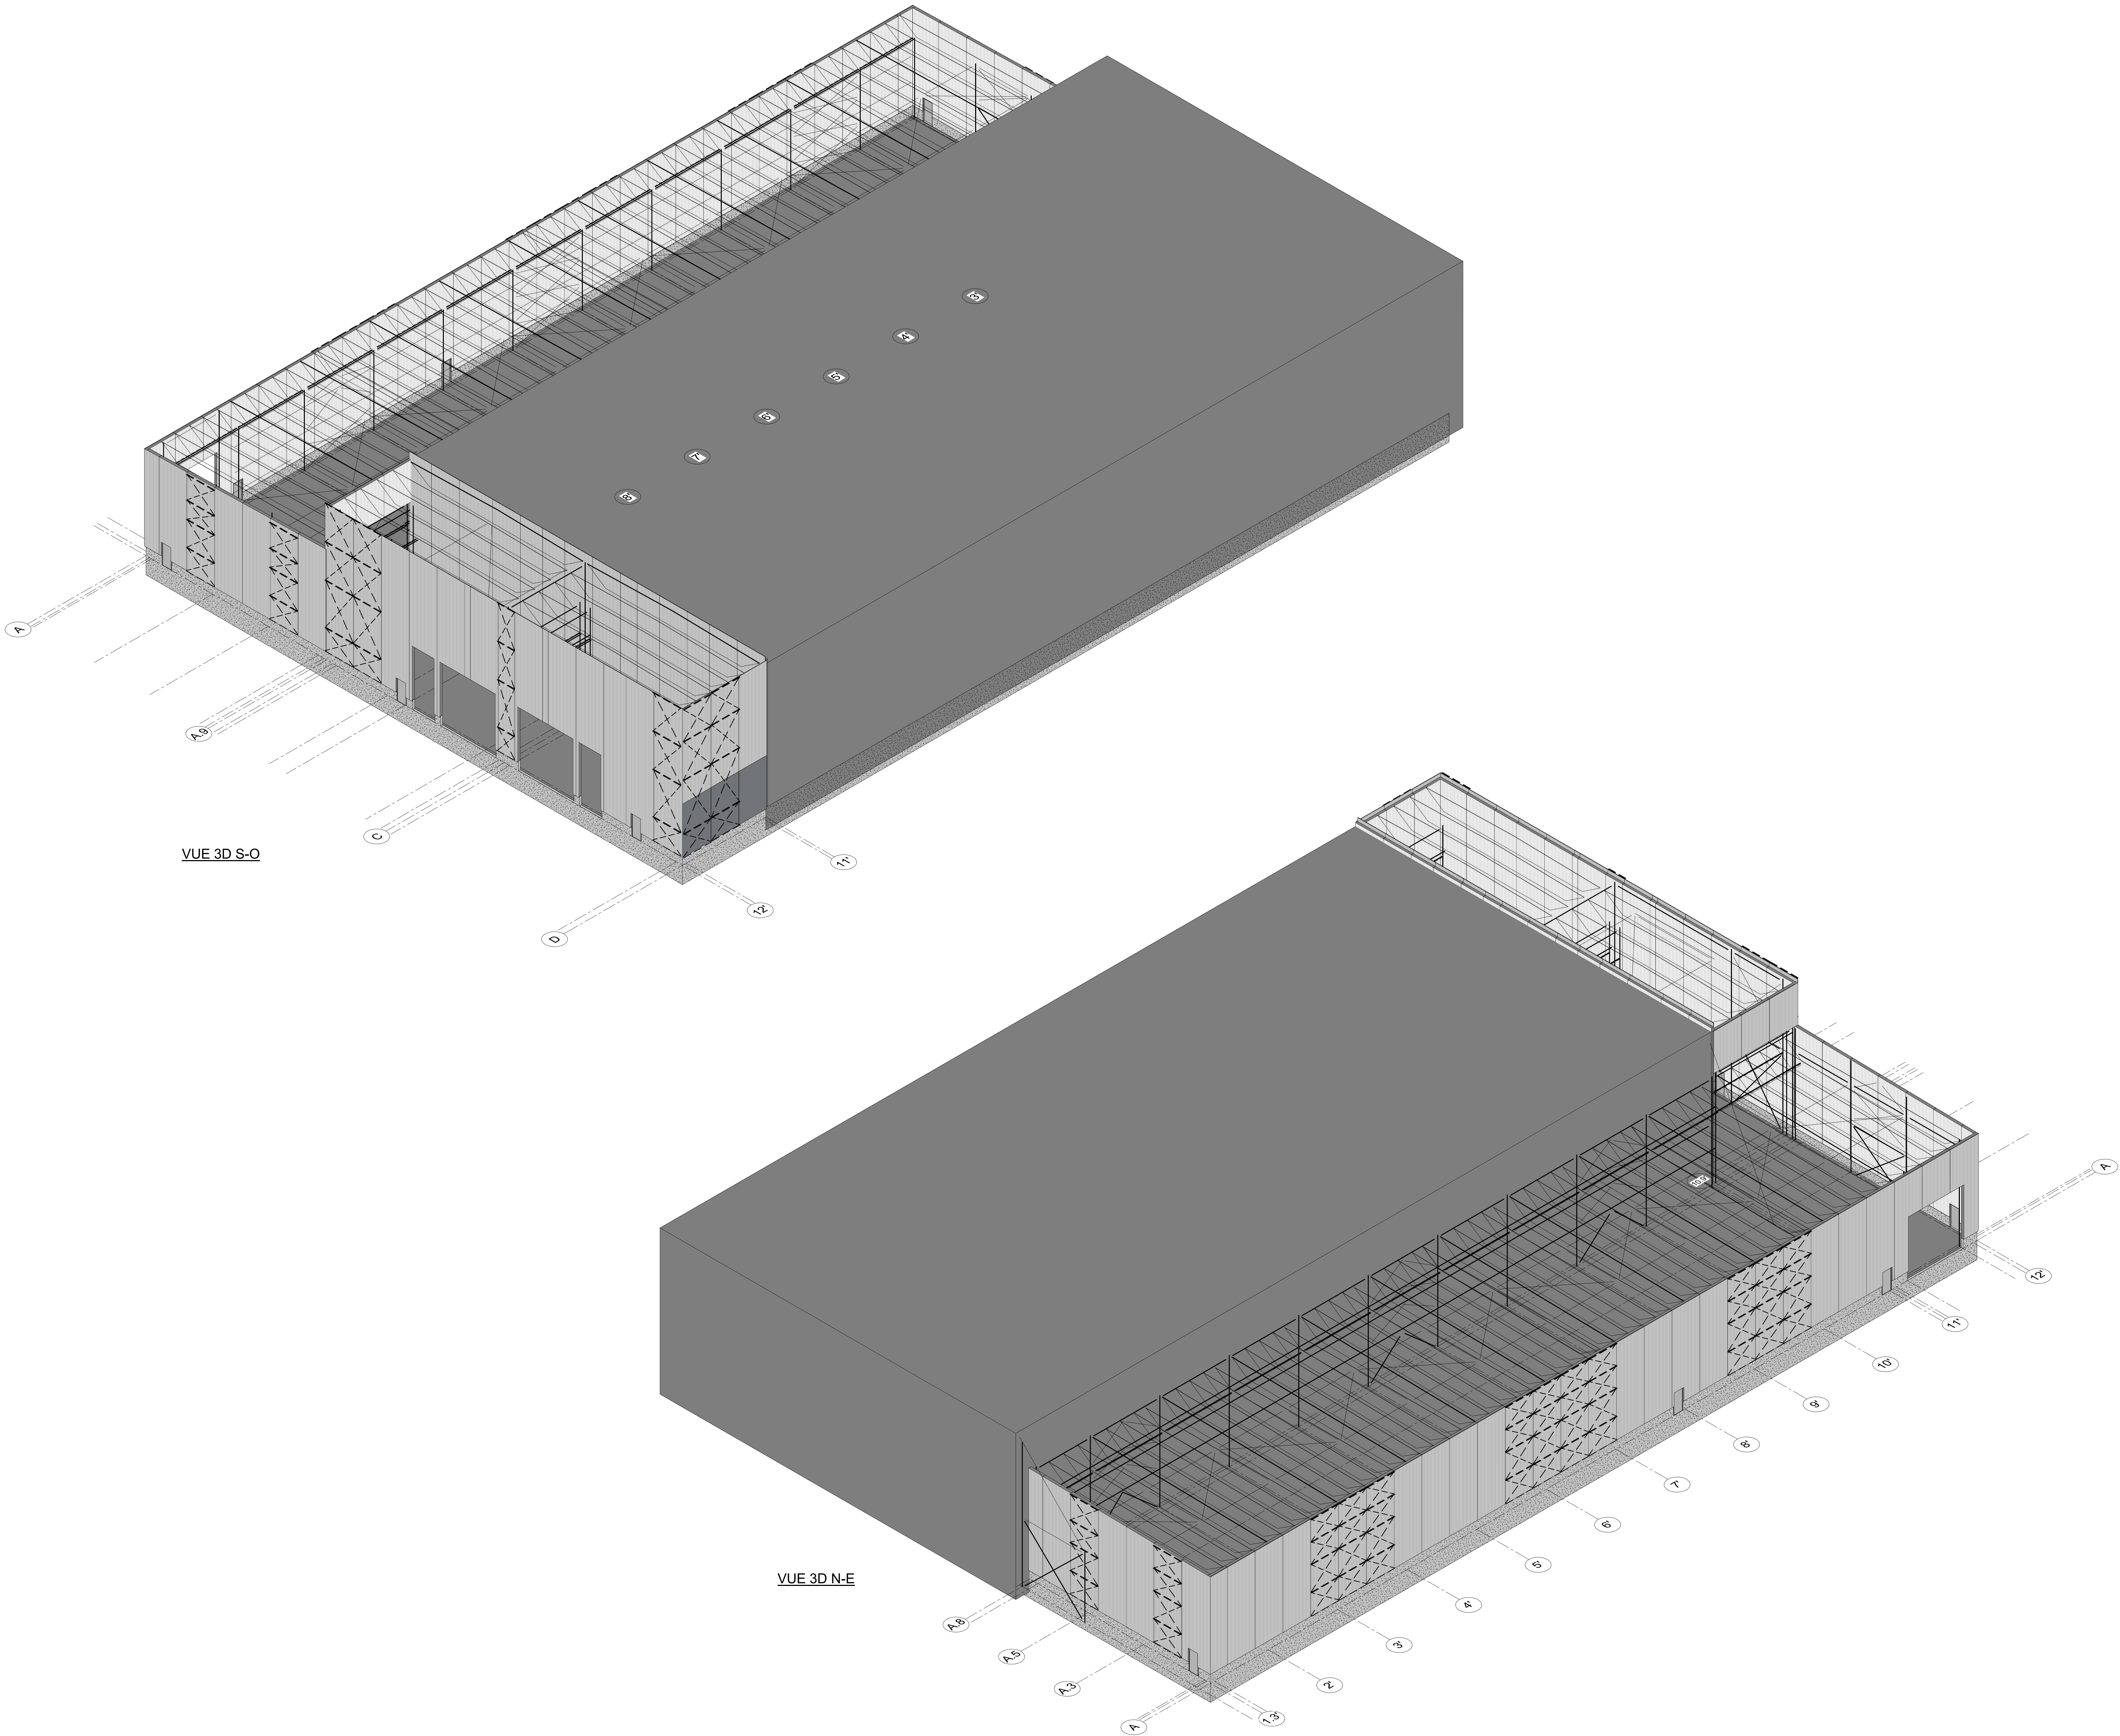

VUE 3D S-O

VUE 3D N-E

NOTE POUR LE CONTRACTEUR/ÉRECTEUR:
IL EST STRICTEMENT DÉFENDU DE MODIFIER, COPIER, REPRODUIRE OU DE DISTRIBUER CES DESSINS OU QUELQUES REPRÉSENTATIONS DE CES DESSINS, PAR TOUTES SOURCES DE MÉDIA INCLUANT ÉLECTRONIQUEMENT, SANS L'APPROBATION ÉCRITE DE GROUPE CANAM INC.


LISTE DES FEUILLES PRÉLIMINAIRES	
EsMx001	CROQUIS PRÉLIMINAIRE - VUES 3D
EsMx101	CROQUIS PRÉLIMINAIRE - PLAN D'ANCRAGE
EsMx201	CROQUIS PRÉLIMINAIRE - PLAN DE PONT ROULANT
EsMx401	CROQUIS PRÉLIMINAIRE - PLAN DE TOIT
EsMx501	CROQUIS PRÉLIMINAIRE - ÉLEVATIONS
EsMx502	CROQUIS PRÉLIMINAIRE - ÉLEVATION, COUPE DE MUR ET CÉDALES
EsMx601	CROQUIS PRÉLIMINAIRE - DÉTAILS

Cliquer ici pour modèle 3D

PRÉLIMINAIRE

NE DOIT PAS SERVIR À LA CONSTRUCTION

REVISION	DATE	DESCRIPTION	DESS	VER
GERANT DE PROJET				
		.		
		.		
		.		
		.		
		.		
DESSIN				
DESSINÉ PAR	CONÇU PAR	INGÉNIEUR DU PROJET	ECHELLE:	
SL				
VÉRIFIÉ PAR	INGÉNIEURS CONSEILS / ARCHITECTES		DATE (gg/mm/aaaa)	
			22/05/2026	
CLIENT: LIXM ENTREPRENEUR GÉNÉRAL INC.				

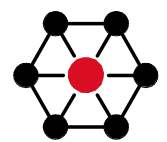**CANAM**

11505, 1re Avenue, bureau 500, Saint-Georges Beauce
Québec, Canada G5Y 7X5
Téléphone : (418) 228-8031
Sans frais : (877) 459-8049
www.canam.com

SCÉAU PROFESSIONNEL


PROJET

AGRANDISSEMENT DE JULES VACHON 2026
TROIS-RIVIÈRES, QC

TITRE

CROQUIS PRÉLIMINAIRE - VUES 3D

INITIALES	NUMÉRO CONTRAT	NUMÉRO DESSIN	DIVISION	REVISION
	P2026-098	EsMx001		

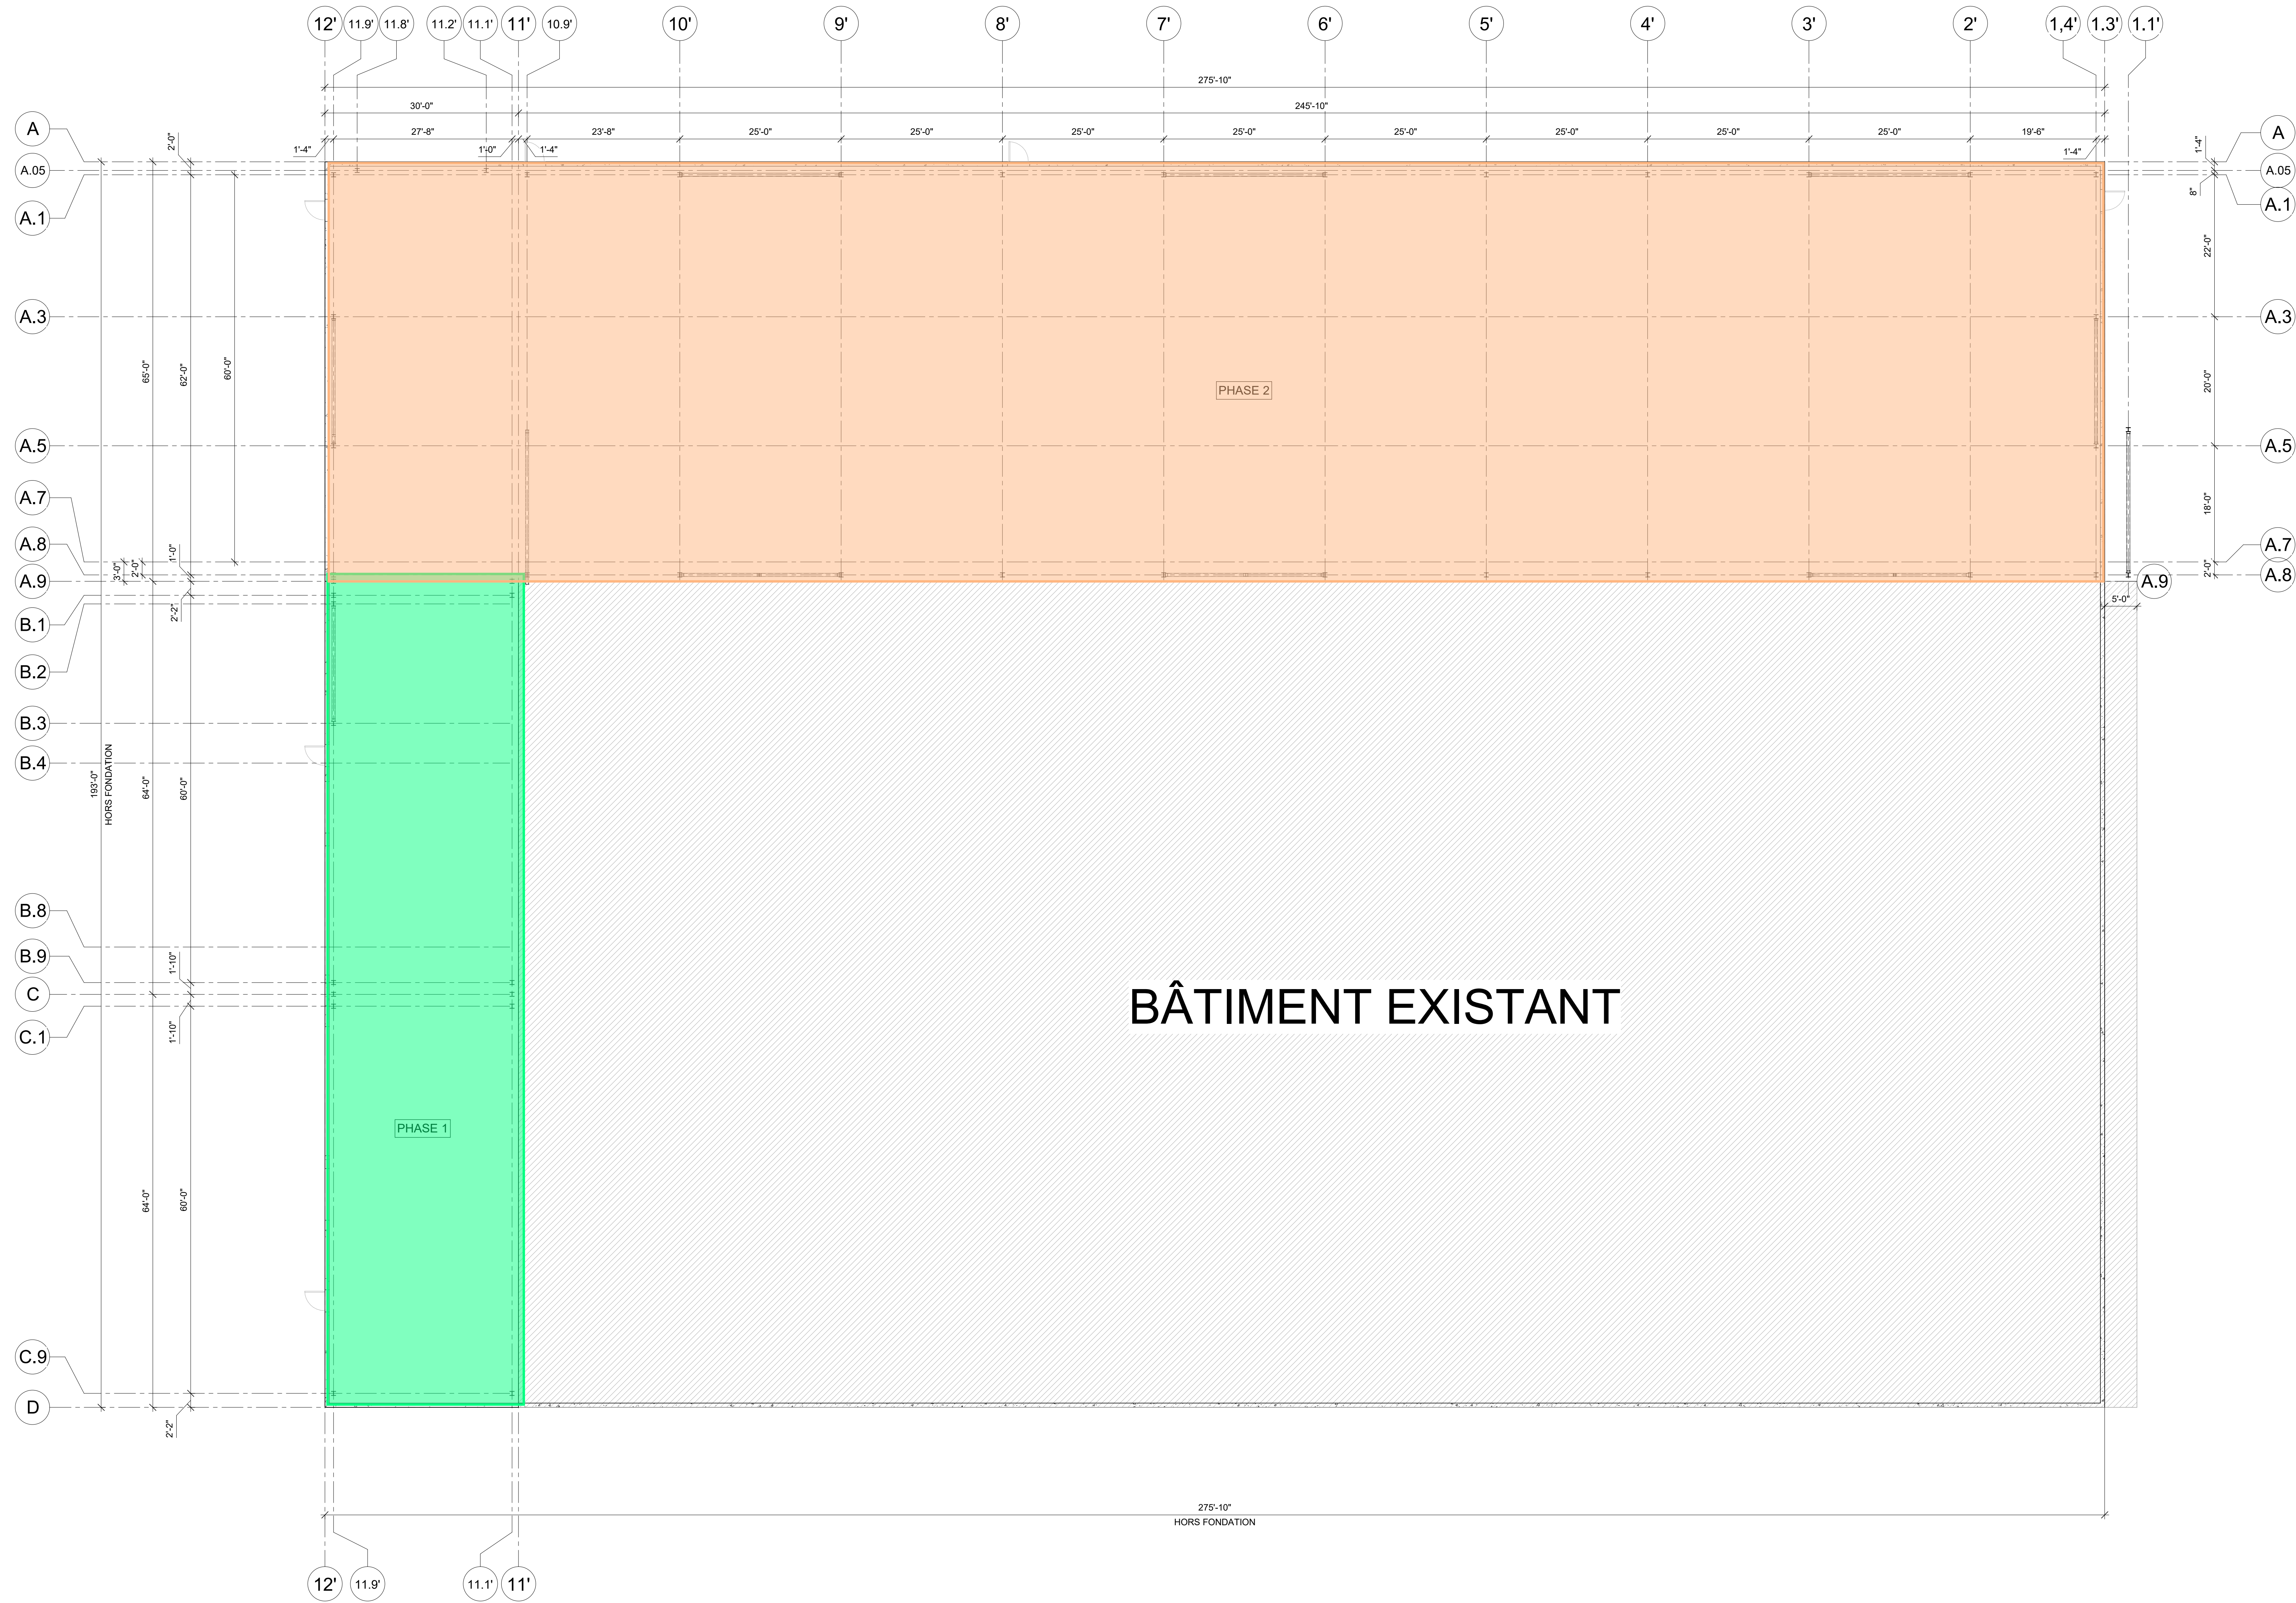

PLAN D'ANCRAGE
3/32" = 1'-0"

NOTE POUR LE CONTRACTEUR/ÉRECTEUR:
IL EST STRICTEMENT DÉFENDU DE MODIFIER, COPIER, REPRODUIRE OU DE DISTRIBUER CES DESSINS OU QUELQUES REPRÉSENTATIONS DE CES DESSINS, PAR TOUTES SOURCES DE MÉDIA INCLUANT ÉLECTRONIQUEMENT, SANS L'APPROBATION ÉCRITE DE GROUPE CANAM INC.


PRÉLIMINAIRE

NE DOIT PAS SERVIR À LA CONSTRUCTION

REVISION	DATE	DESCRIPTION	DESS	VER
GERANT DE PROJET				
		-		
		-		
		-		

DESSIN	CONÇU PAR	INGÉNIEUR DU PROJET	ÉCHELLE:
SL			3/32" = 1'-0"
VERIFIÉ PAR	INGÉNIEURS CONSEILS / ARCHITECTES	DATE (jj/mm/aaaa)	
		22/05/2026	

CLIENT: LIXM ENTREPRENEUR GÉNÉRAL INC.

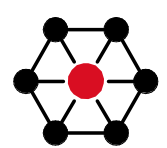**CANAM**
11505, 1re Avenue, bureau 500, Saint-Georges Beauce
Québec, Canada, G5Y 7X5
Téléphone : (418) 228-8031
Sans frais : (877) 459-8049
www.canam.com

SCAUX PROFESSIONNEL

PROJET

AGRANDISSEMENT DE JULES VACHON 2026
TROIS-RIVIÈRES, QC

TITRE
CROQUIS PRÉLIMINAIRE - PLAN D'ANCRAGE

NUMÉRO CONTRAT	NUMÉRO DESSIN	DIVISION	REVISION
P2026-098	EsMx101		

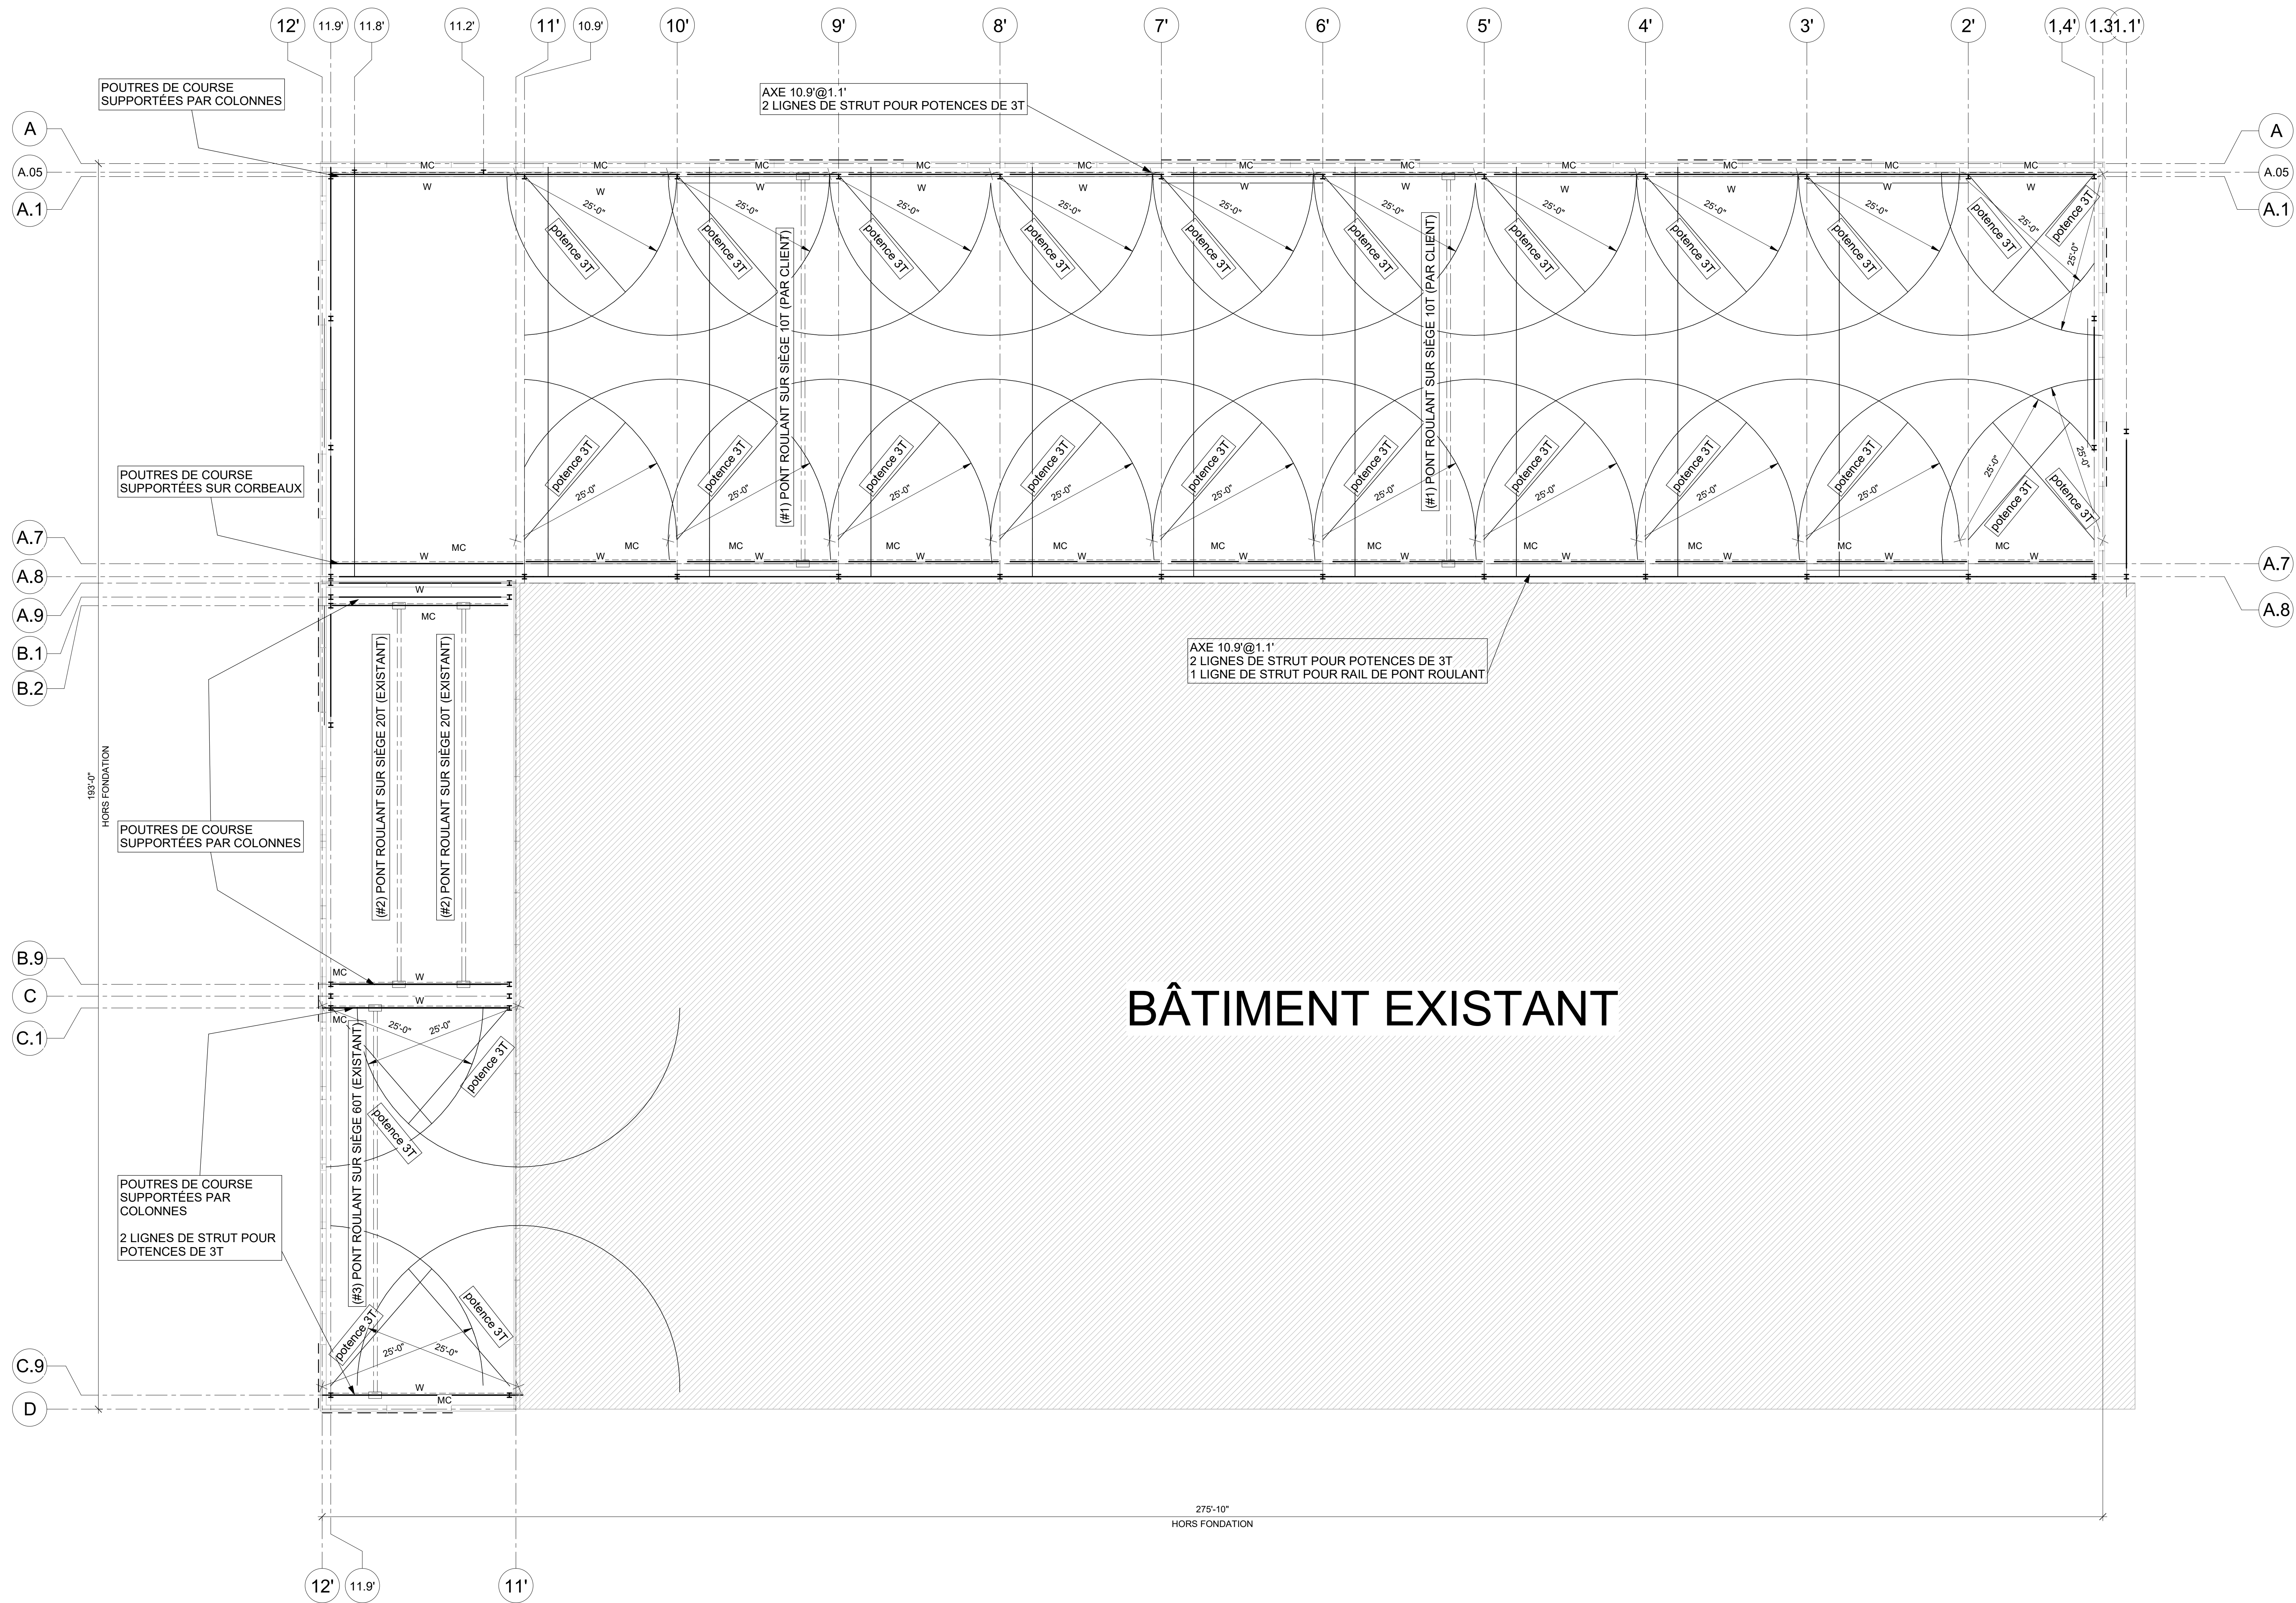


TABLEAU CHARGES PONT ROULANT				
CAPACITÉ	POIDS DU PONT	CHARIOT	CHARGE MAX. PAR ROUE (DYNAMIQUE)	ESPACEMENT DES ROUES
22000 lbs 10T (#1)	11800 lb	1400 lb	18.4 kip	9'-0"
40000 lbs 20T (#2)	27779 lb	7000 lb	39 kip	13'-0"
120000 lbs	42070 lb	12500 lb	96 kip	17'-0"

PLAN PONT ROULANT
3/32" = 1'-0"

NOTE POUR LE CONTRACTEUR/ÉRECTEUR:
IL EST STRICTEMENT DÉFENDU DE MODIFIER, COPIER, REPRODUIRE OU DE DISTRIBUER CES DESSINS OU QUELQUES REPRÉSENTATIONS DE CES DESSINS, PAR TOUTES SOURCES DE MÉDIA INCLUANT ÉLECTRONIQUEMENT, SANS L'APPROBATION ÉCRITE DE GROUPE CANAM INC.

PRÉLIMINAIRE

NE DOIT PAS SERVIR À LA
CONSTRUCTION

REVISION	DATE	DESCRIPTION	DESS	VER
----------	------	-------------	------	-----

GERANT DE PROJET	-
	-
	-
	-

DESSIN


DESSINÉ PAR	CONÇU PAR	INGÉNIEUR DU PROJET	ÉCHELLE:
-------------	-----------	---------------------	----------

SL			3/32" = 1'-0"
----	--	--	---------------

VERIFIÉ PAR	INGÉNIEURS CONSEILS / ARCHITECTES	DATE (mm/aaaa)
-------------	-----------------------------------	----------------

		22/05/2026
--	--	------------

CLIENT: LIXM ENTREPRENEUR GÉNÉRAL INC.

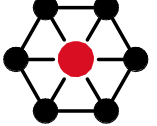 **CANAM**
11505, 1re Avenue, bureau 500, Saint-Georges Beauce
Québec, Canada, G5Y 7G3
Téléphone : (418) 228-8031
Sans frais : (877) 459-8049
www.canam.com

SCAUX PROFESSIONNEL

PROJET

AGRANDISSEMENT DE JULES
VACHON 2026
TROIS-RIVIÈRES, QC

TITRE

CROQUIS PRÉLIMINAIRE - PLAN DE
PONT ROULANT

NUMÉRO CONTRAT

P2026-098

NUMÉRO DESSIN

EsMx301

DIVISION

REVISION

Initiales



ACCUMULATION DE NEIGE


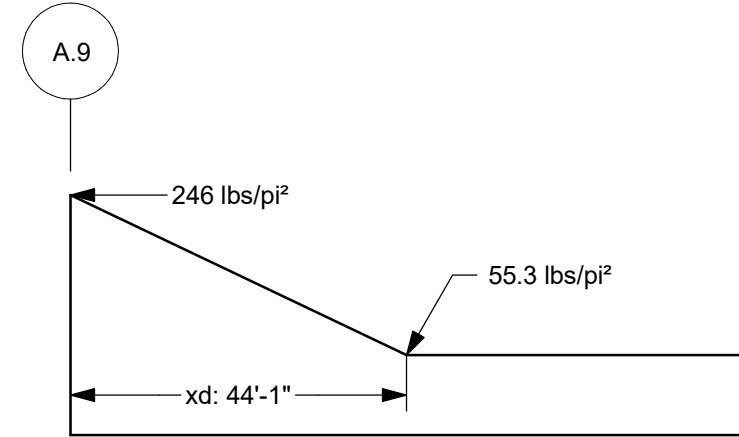


DIAGRAMME DE SOULEVEMENT BRUT (NON PONDÉRÉ)

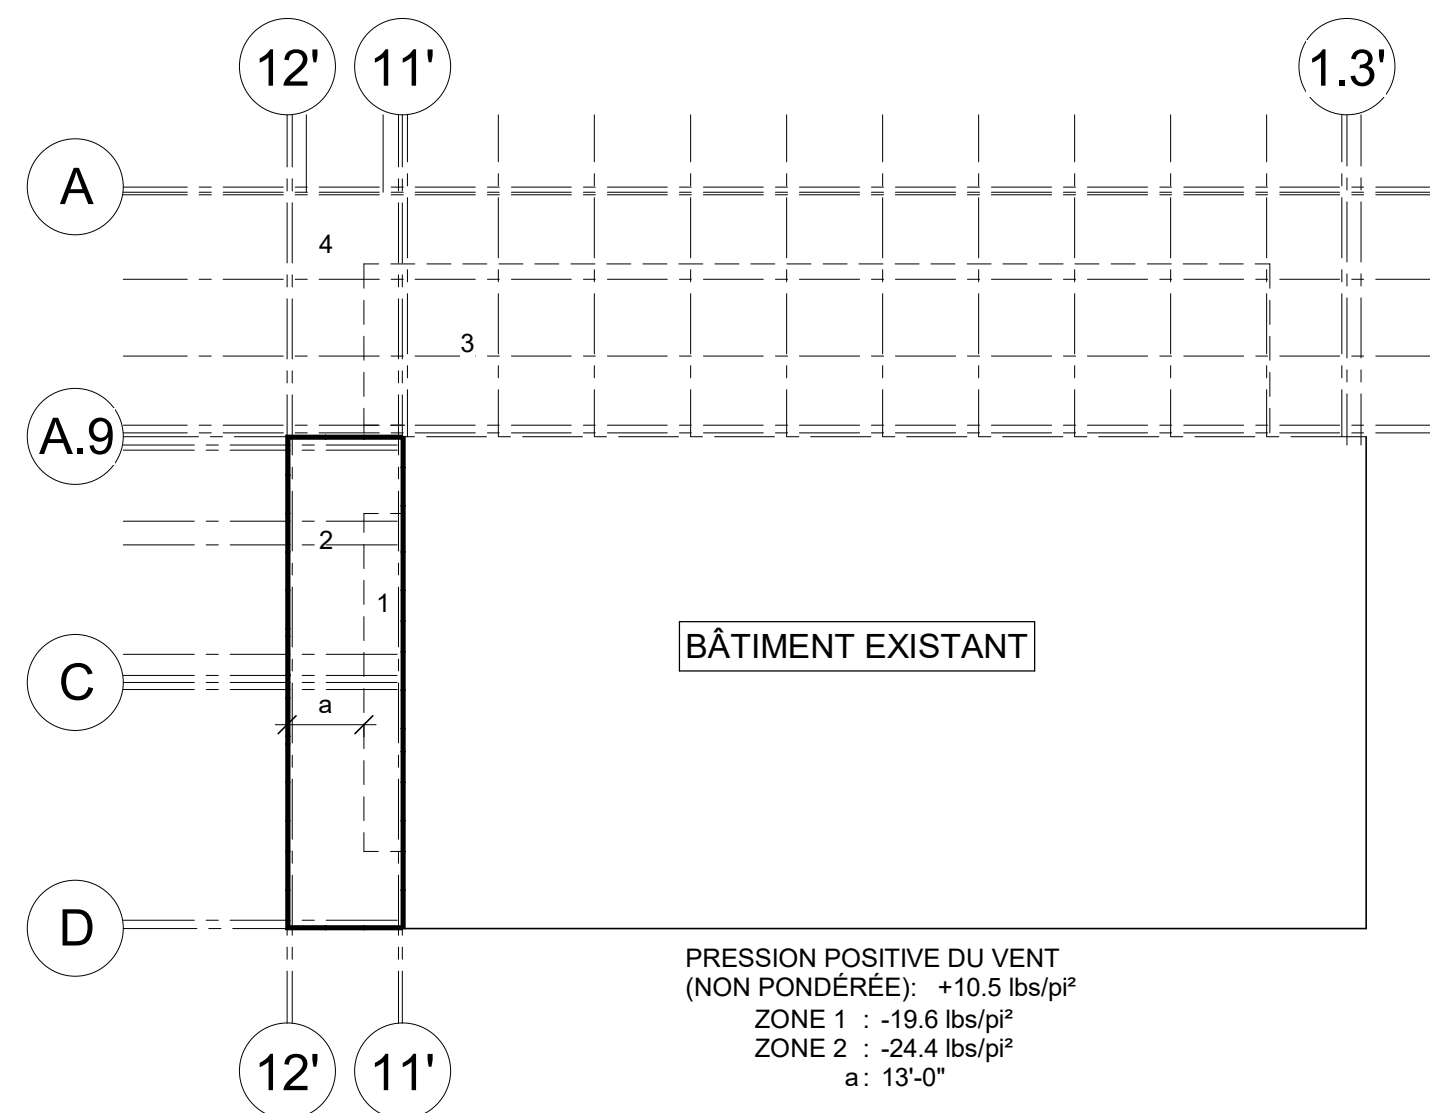

NOTE POUR LE CONTRACTEUR/ÉRECTEUR:
IL EST STRICTEMENT DÉFENDU DE MODIFIER, COPIER, REPRODUIRE OU DE DISTRIBUER CES DESSINS OU QUELQUES REPRÉSENTATIONS DE CES DESSINS, PAR TOUTES SOURCES DE MÉDIA INCLUANT ÉLECTRONIQUEMENT, SANS L'APPROBATION ÉCRITE DE GROUPE CANAM INC.

TOIT
DESSUS DE PILASTRE : 99'-0"
DESSUS DE LA DALLE : 100'-0"
DESSUS DE LA FONDATION : 103'-0"
HAUTEUR LIBRE : VOIR CROQUIS
DESSUS TACHER : VOIR CROQUIS
HAUTEUR DE PARAPET : 1'-2"
DESSUS DE PARAPET : VOIR CROQUIS

CHARGES :

C.M. : 18 lbs/ft²
C.O.L. : 5 lbs/ft²
S_u : 59.5 lbs/ft²
S_v : 8 lbs/ft²
C_b x C_w : 0.8
C.V. au toit : 0 lbs/ft²
L_v : 10
Charge de neige au toit : 55.3 lbs/ft²
L_v : 10
Vent q = 1/50 : 9 lbs/ft²
Séisme (Sol de classe D assumé)

L_v : 10
S_u (0.2) : 0.588
S_u (0.5) : 0.516
S_u (1.0) : 0.316
S_u (2.0) : 0.153
S_u (5.0) : 0.0434
S_u (10.0) : 0.017
PGA : 0.328
PGV : 0.361

CHARGES :

- Charge morte au toit (excluant charge collatérale) : lbs/ft²
- Charge collatérale : lbs/ft² (incluant éclairage et/ou mécanique et gicleurs plus petite que 4" de diamètre)
- Charge de neige au toit : lbs/ft²
- Charge vive au toit : lbs/ft²
- Charge de vent q 1/50 : lbs/ft²
- Charge de neige au sol : S_u = lbs/ft²
- Catégorie de risque : normal
- Coefficient de surcharge de neige : C_b = 0.8
- C_w = 1.0

Code Applicable : Code National du Bâtiment du Canada
Code du bâtiment du Québec, dernières éditions adoptées
Code de Pratique Standard ICCA.

Type de sol assumé : classe D

NOTE :
1. Si toutefois la catégorie d'emplacement devient E ou F selon le rapport géotechnique, le concept structural préliminaire (localisation et géométrie des contreventements, etc.) devra être validé et coordonné par l'ingénieur de Canam.

PRÉLIMINAIRE

NE DOIT PAS SERVIR À LA CONSTRUCTION

REVISION DATE DESCRIPTION DESSIN VER

DEVANT DE PROJET
-
-
-

DESSIN

DESSIN PAR CONÇU PAR INGÉNIEUR DU PROJET ÉCHELLE: Comme indiqué

VERIFIÉ PAR INGÉNIEURS CONSEILS / ARCHITECTES DATE (mm/aa/aaaa) 22/05/2026

CLIENT: LIXM ENTREPRENEUR GÉNÉRAL INC.



11505, 1^{re} Avenue, bureau 500, Saint-Georges Beauce
Québec, Canada, G5Y 7X3
Téléphone : (418) 228-8031
Sans frais : (877) 459-8049
www.canam.com

SCAUX PROFESSIONNEL

PROJET

AGRANDISSEMENT DE JULES
VACHON 2026
TROIS-RIVIÈRES, QC

TITRE

CROQUIS PRÉLIMINAIRE - PLAN DE TOIT

NUMÉRO CONTRAT NUMÉRO DESSIN DIVISION REVISION

P2026-098 EsMx401


Initiales

BÂTIMENT EXISTANT
J00571


PLAN DE TOIT

3/32" = 1'-0"


Scale

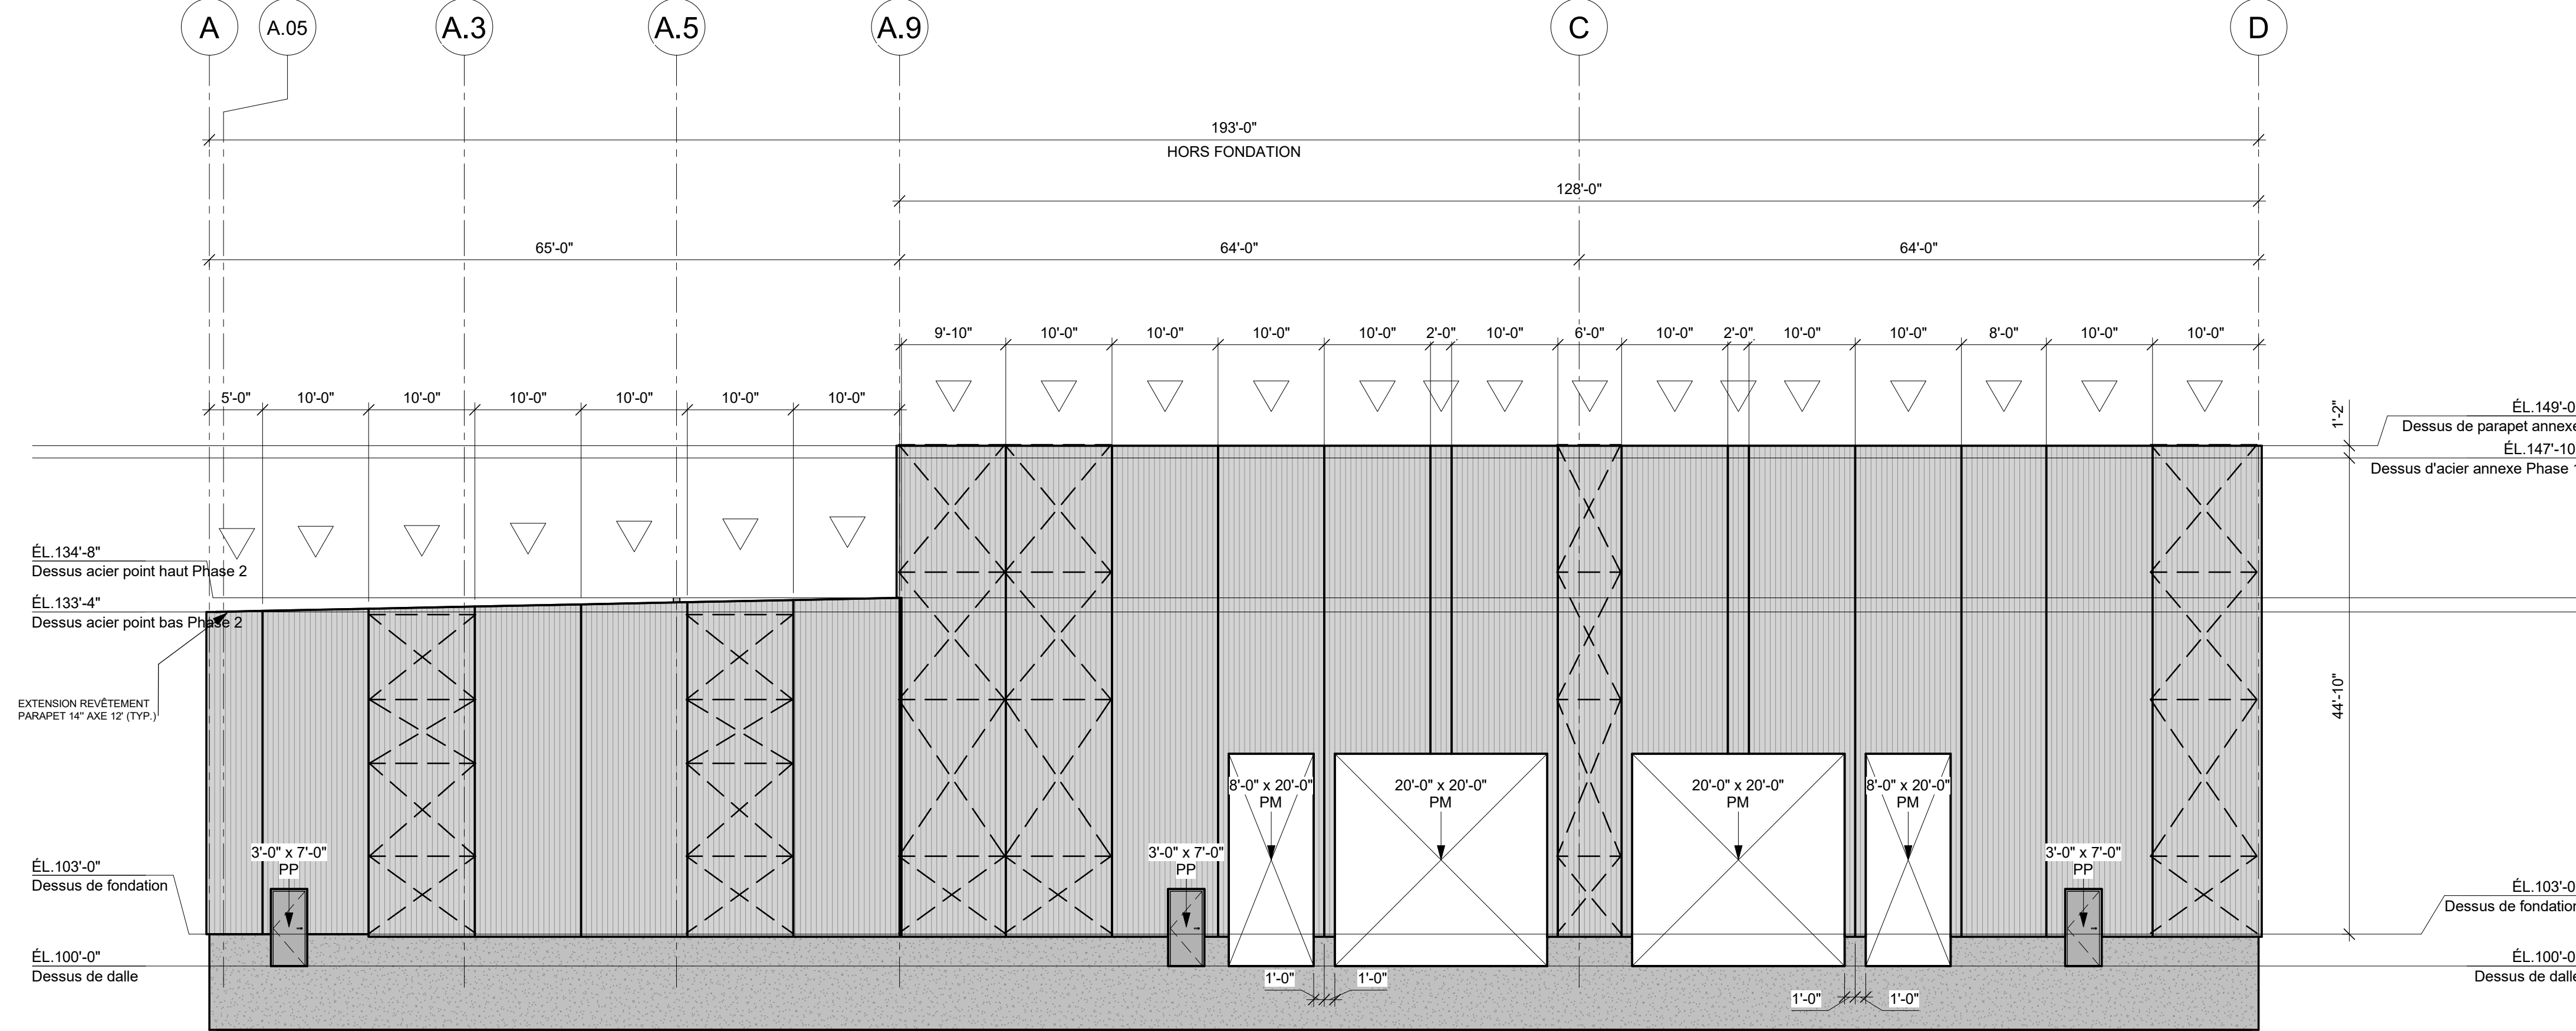


ÉLEVATION AXE 12' (OUEST)
3/32" = 1'-0"

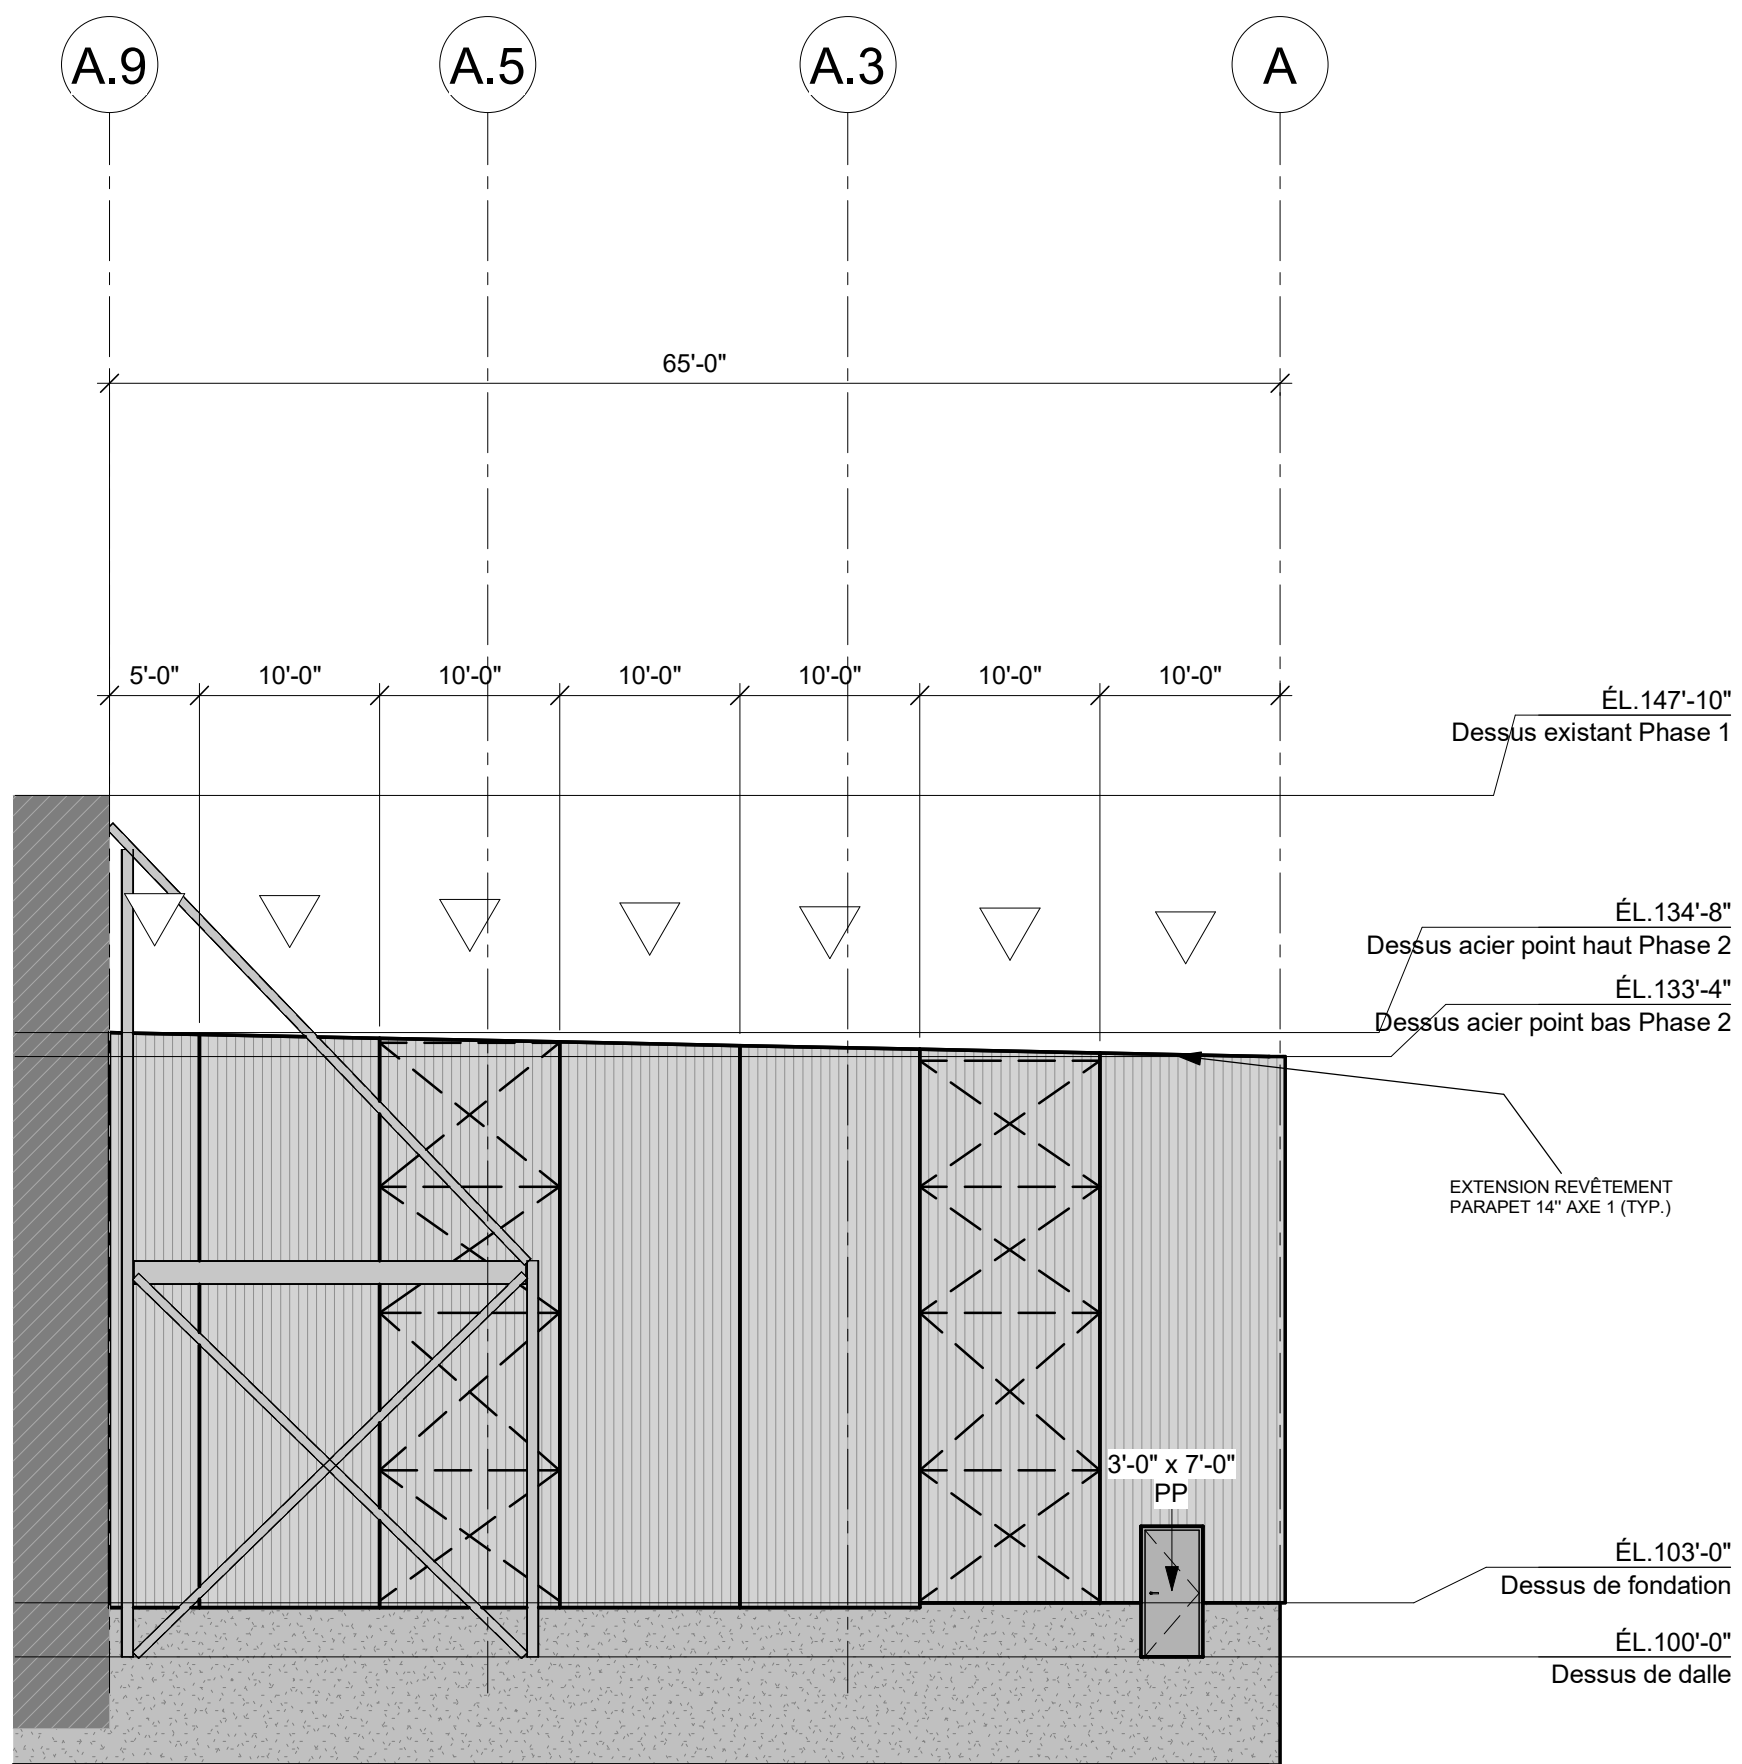


ÉLEVATION AXE 1 (EST)
3/32" = 1'-0"

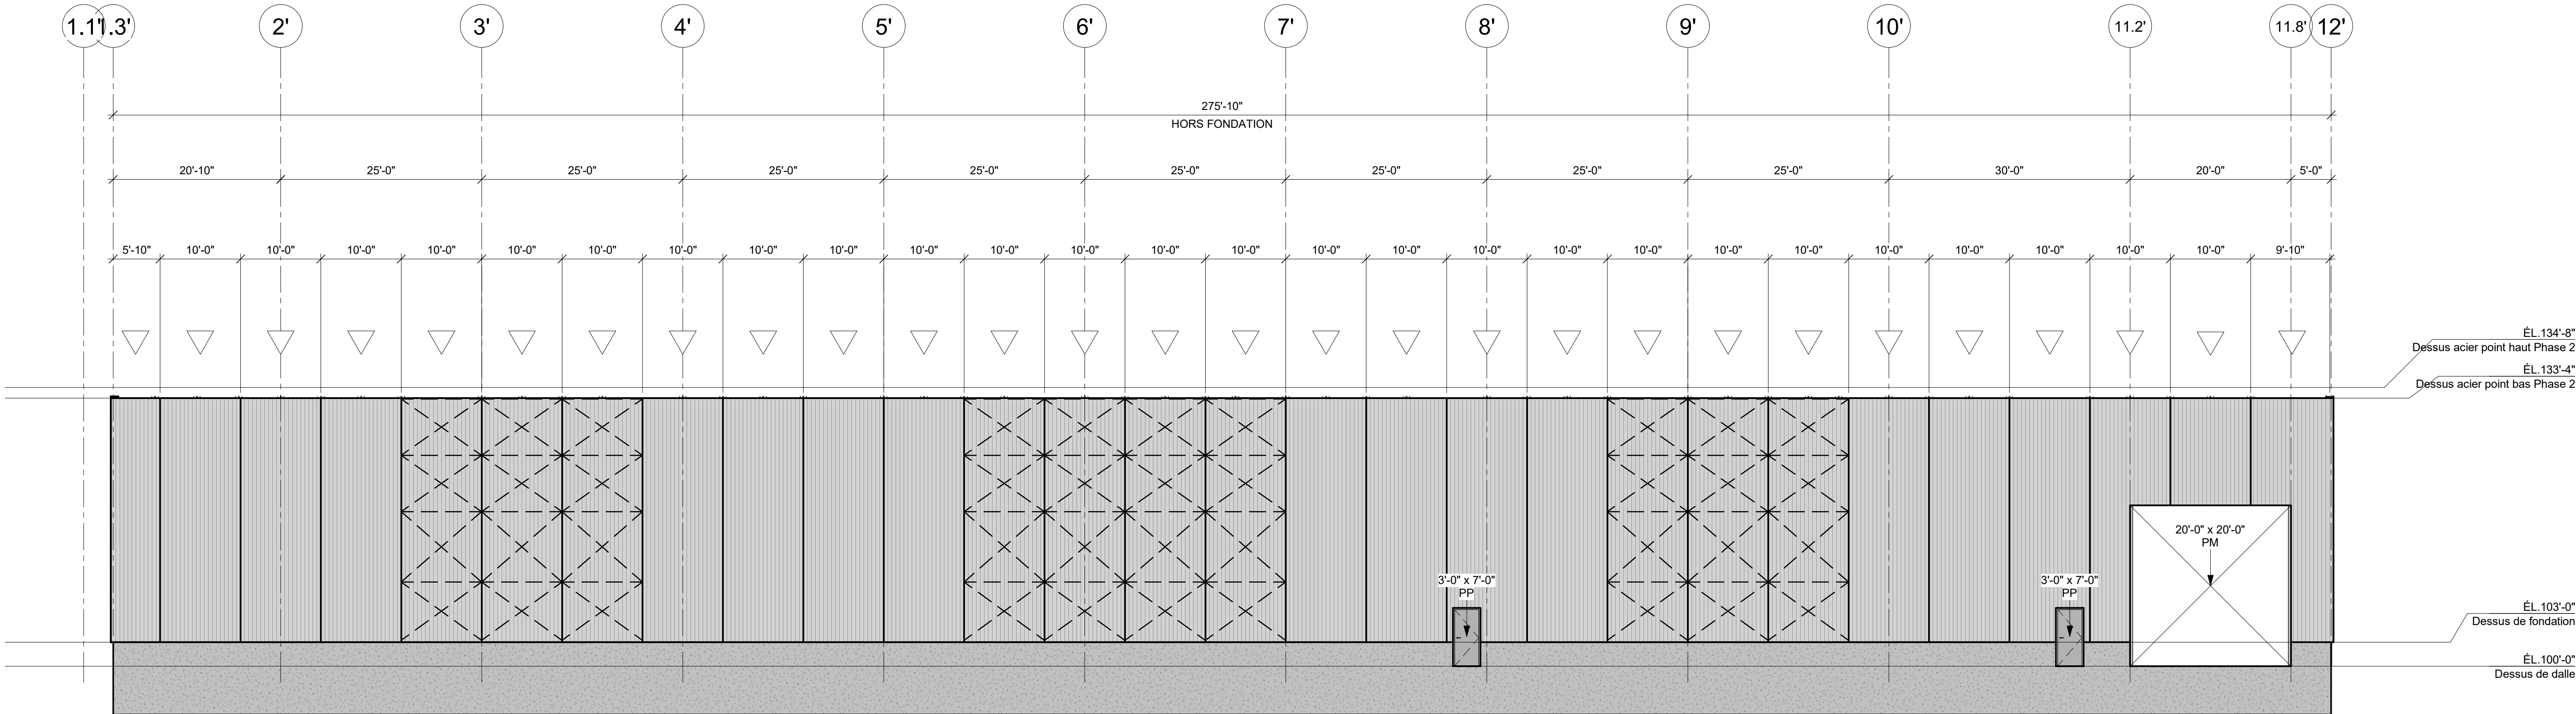


ÉLEVATION AXE A (NORD)
3/32" = 1'-0"

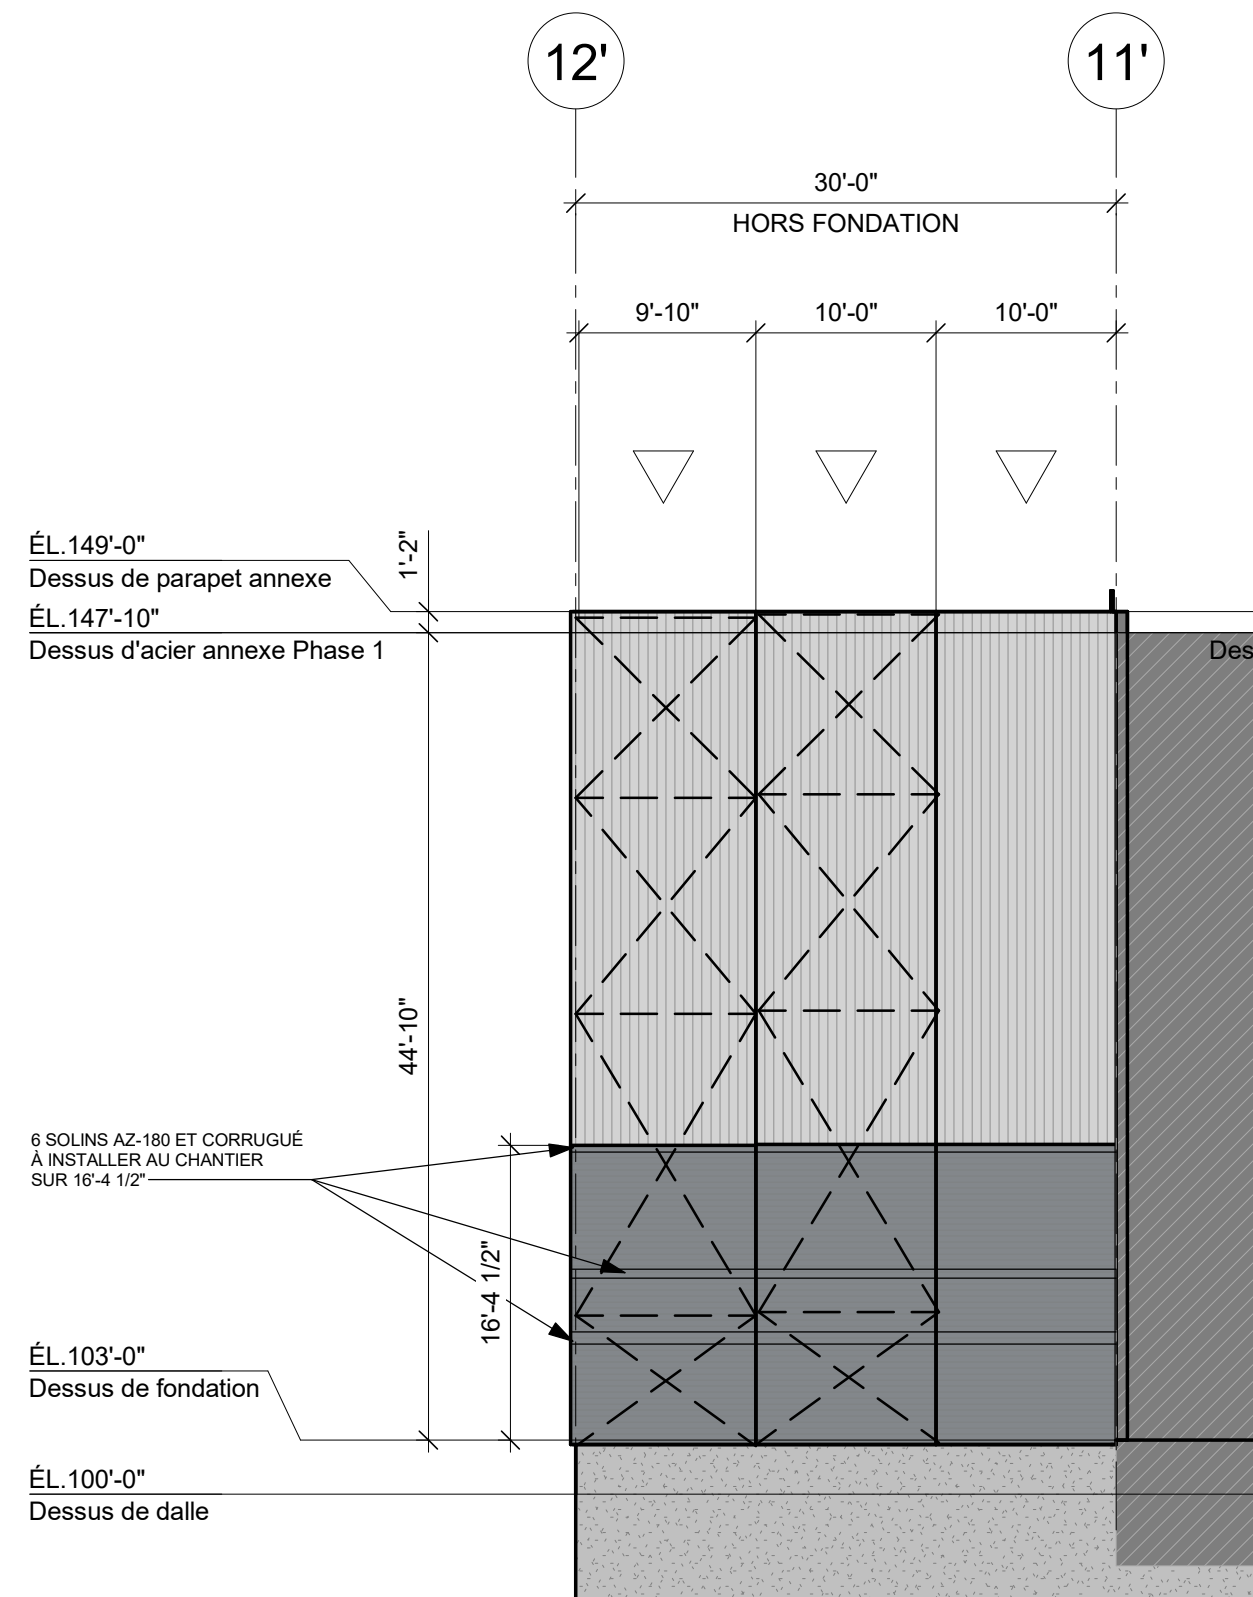


ÉLEVATION AXE D (SUD)
3/32" = 1'-0"

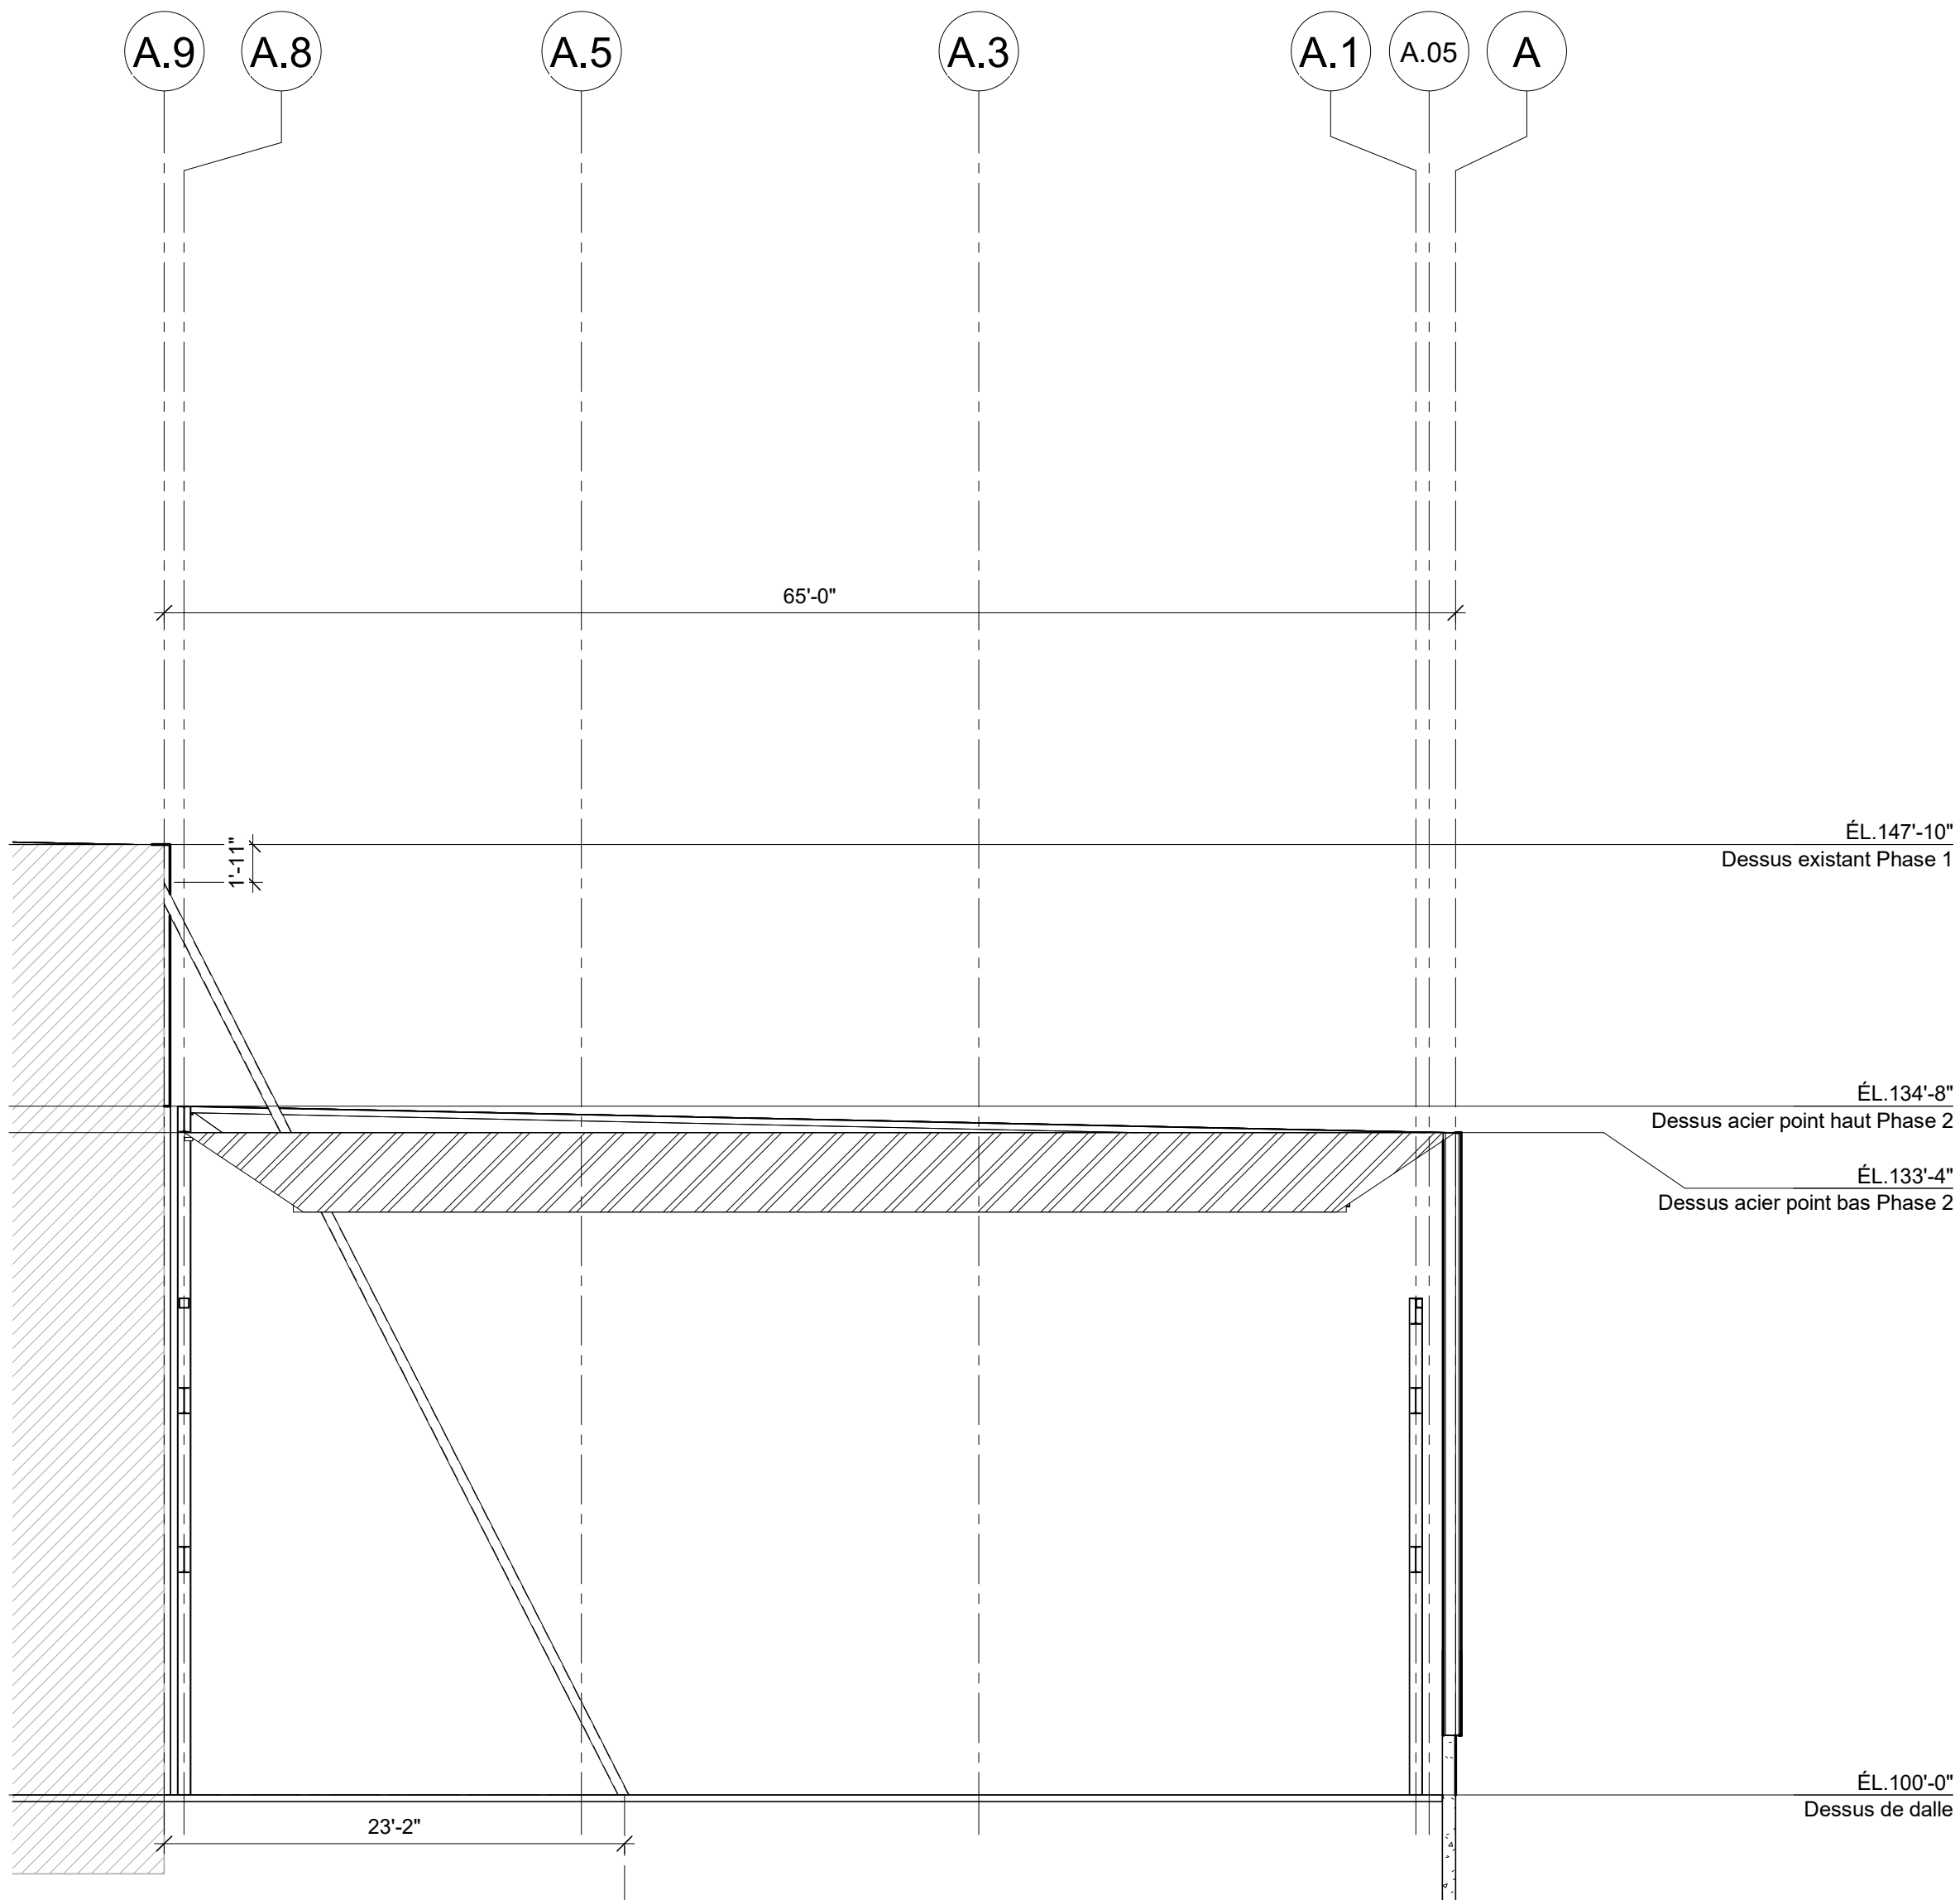

AXE 10.9 (STRUCTURE)
1/8" = 1'-0"

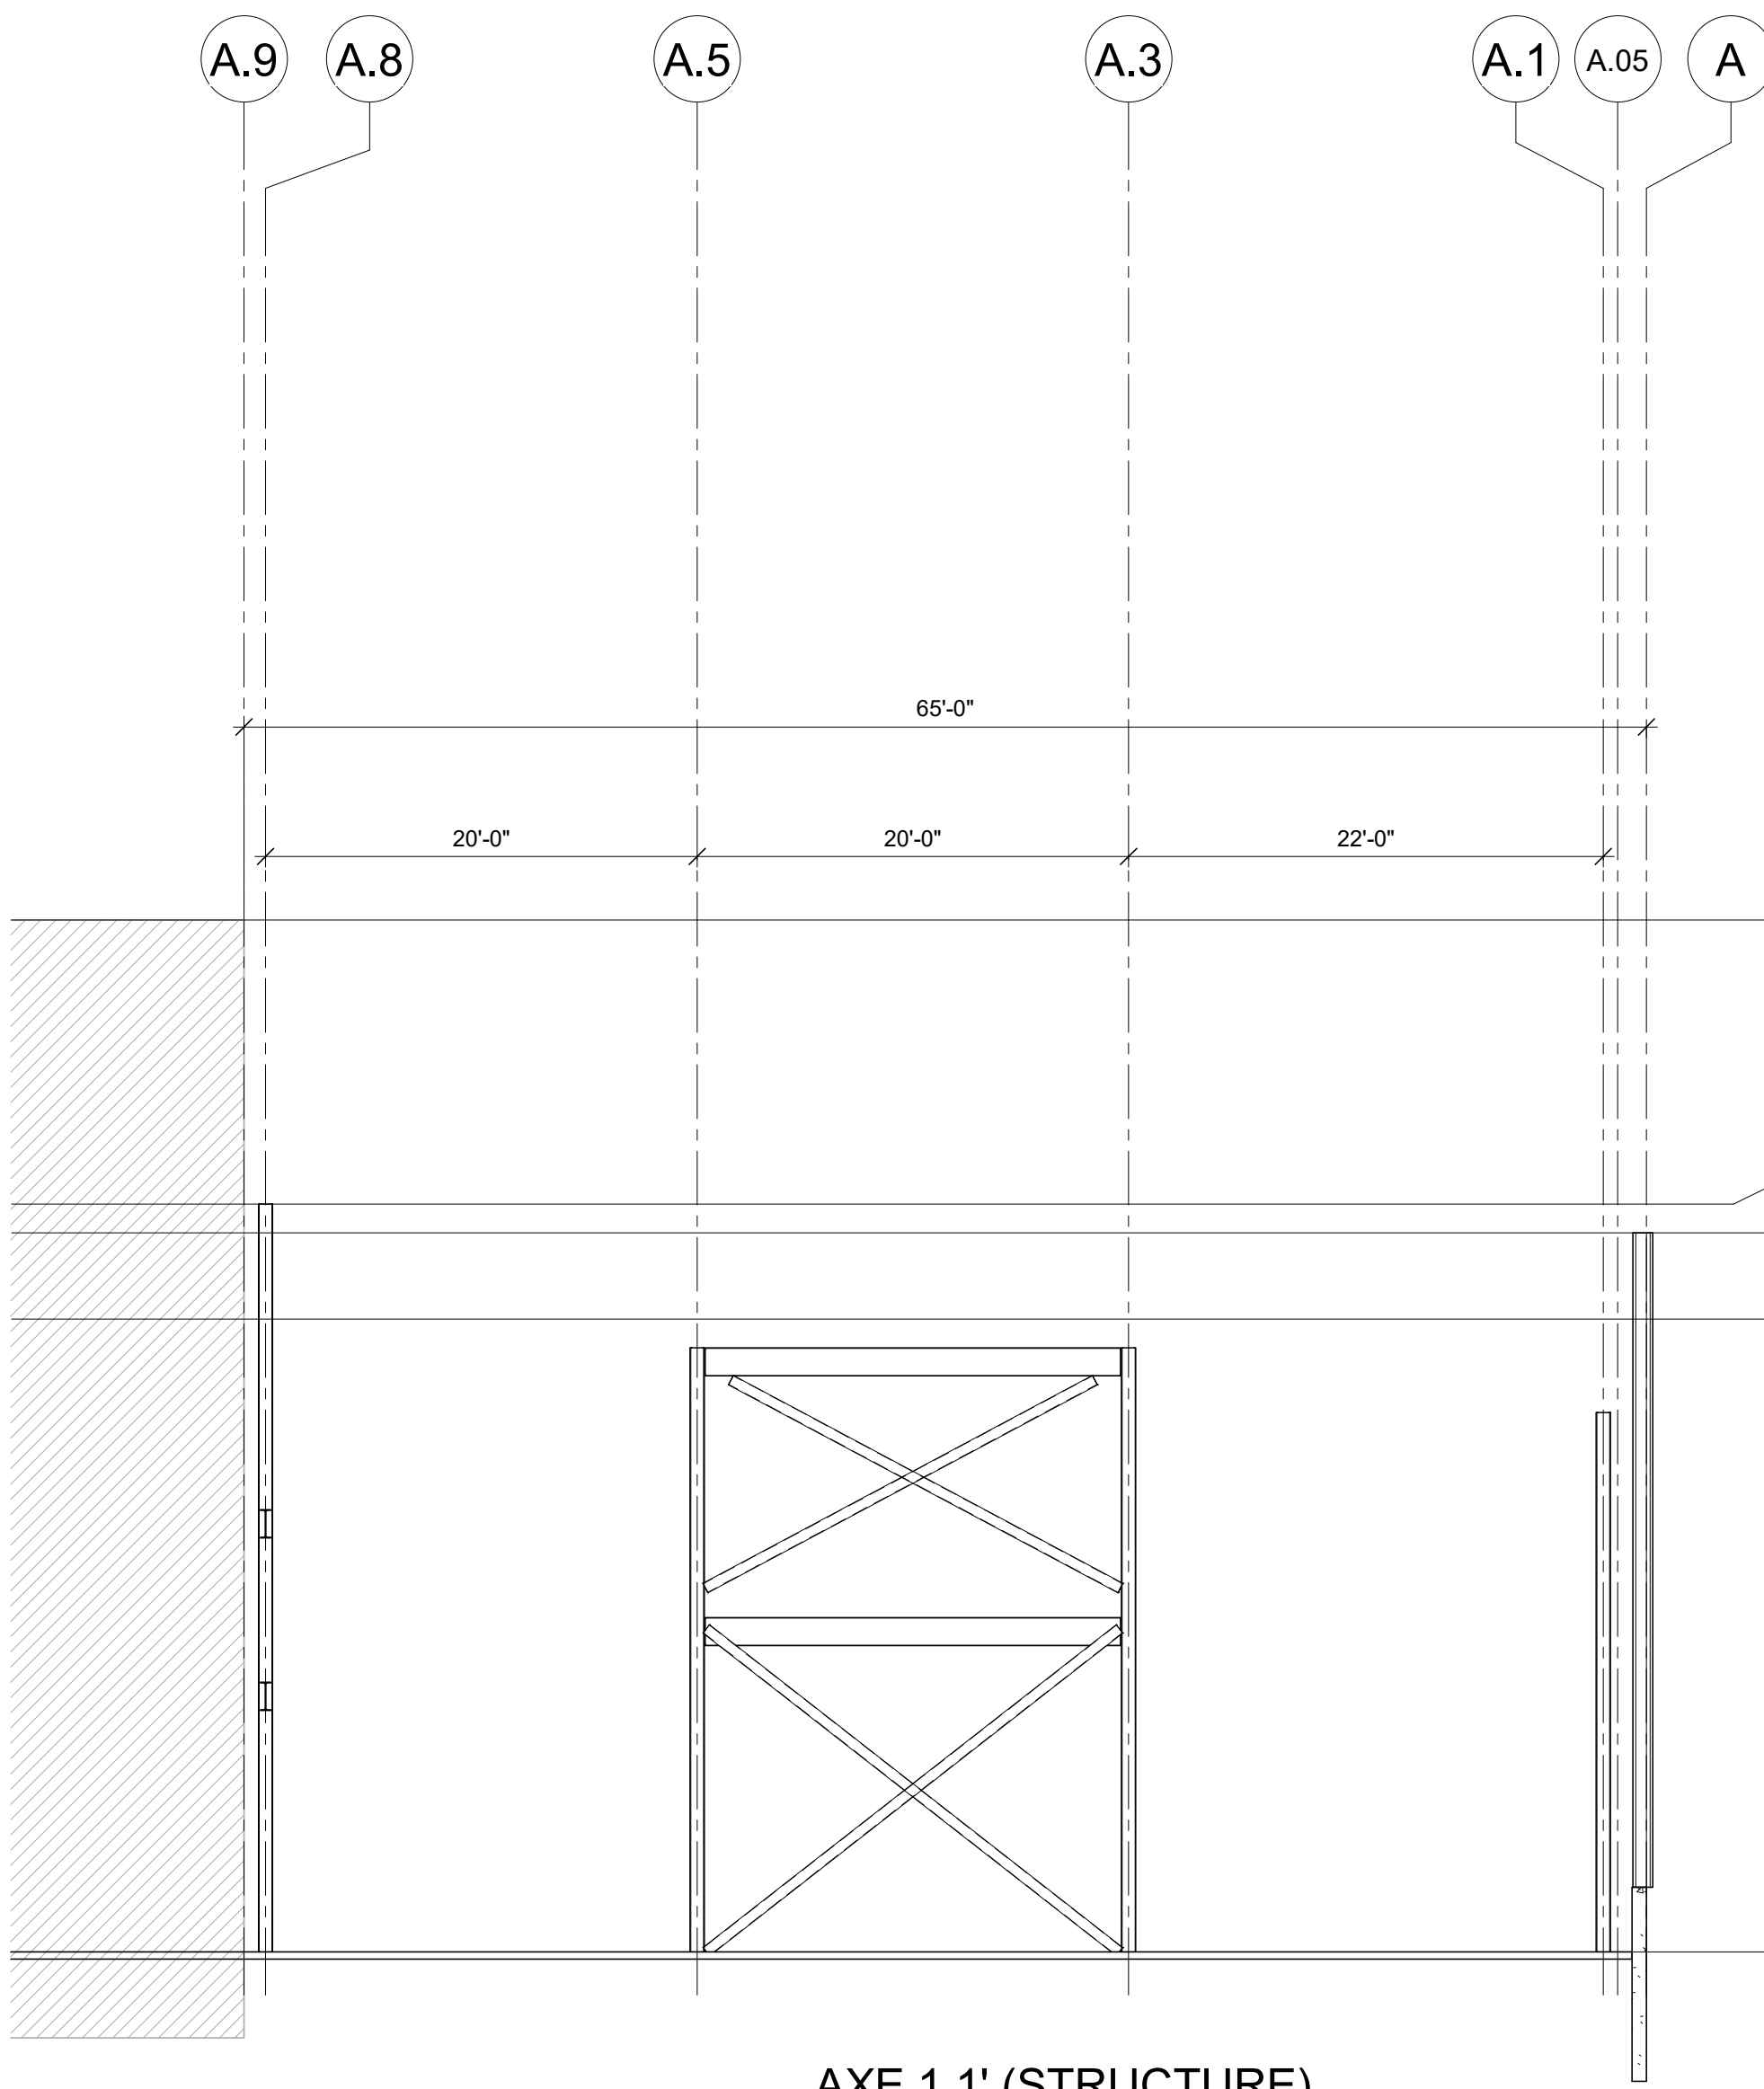

AXE 1.1' (STRUCTURE)
1/8" = 1'-0"

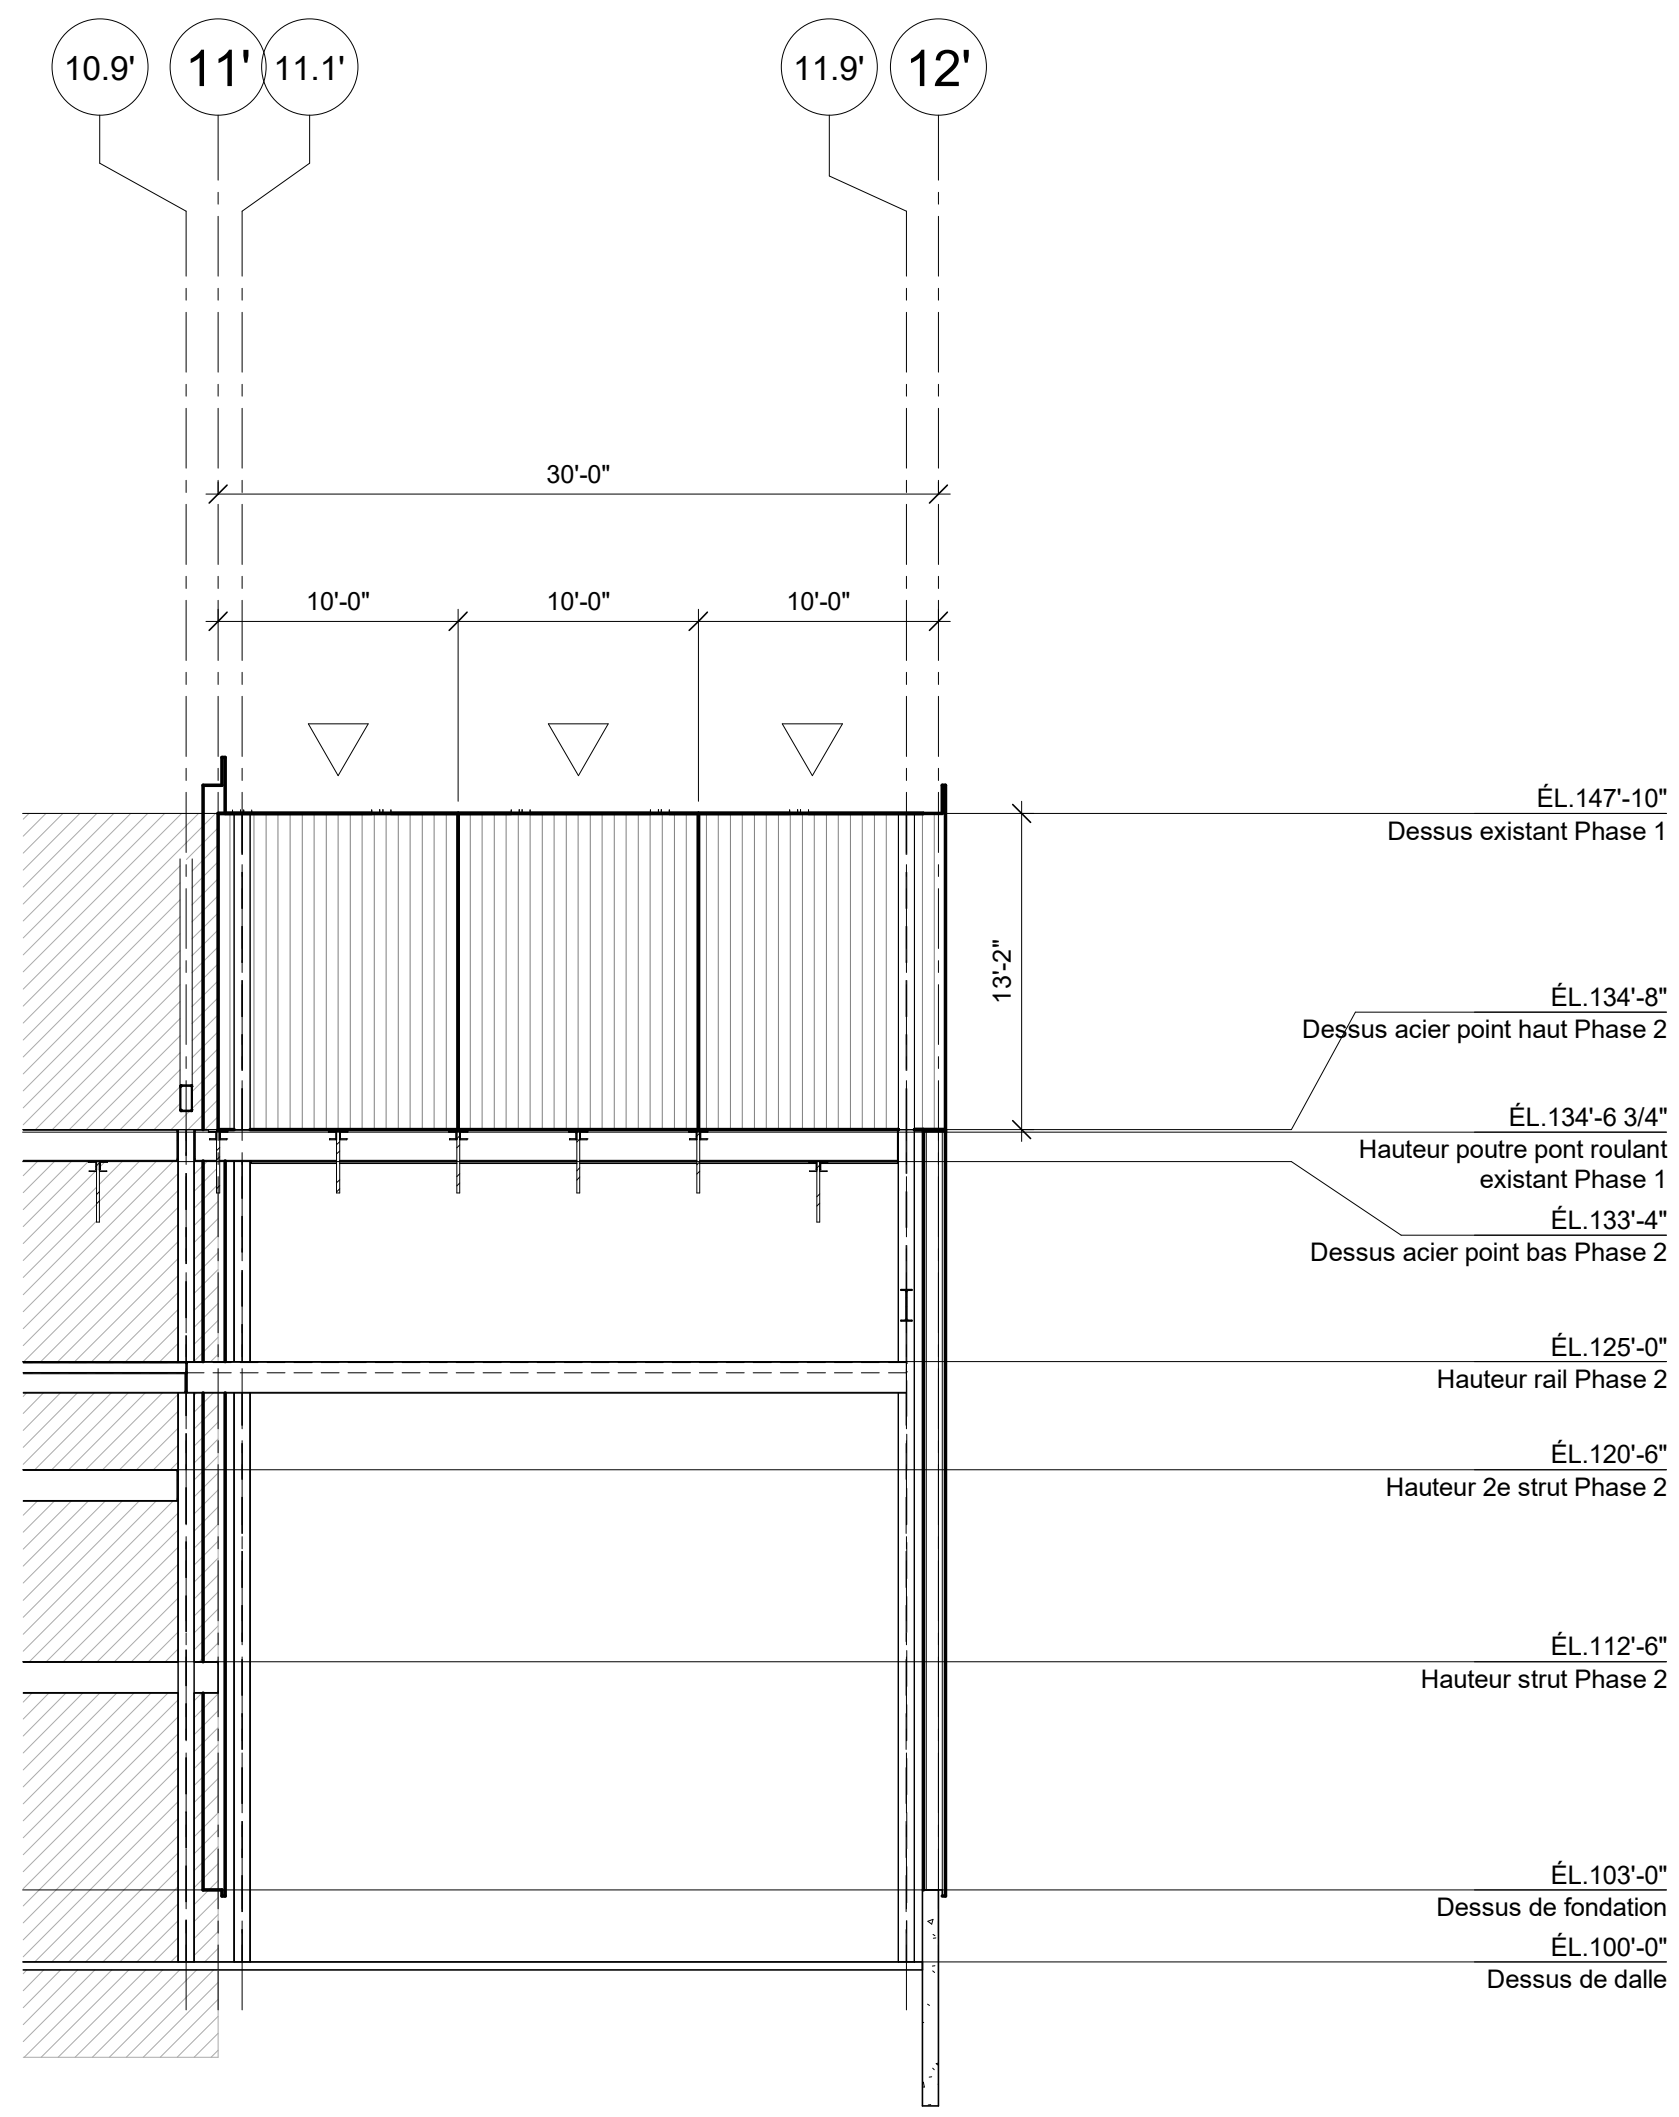

AXE A.9 (high & low)
1/8" = 1'-0"

NOTE POUR LE CONTRACTEUR/ÉRECTEUR:
IL EST STRICTEMENT DÉFENDU DE MODIFIER, COPIER, REPRODUIRE OU DE DISTRIBUER CES DESSINS OU QUELQUES REPRÉSENTATIONS DE CES DESSINS, PAR TOUTES SOURCES DE MÉDIA INCLUANT ÉLECTRONIQUEMENT, SANS L'APPROBATION ÉCRITE DE GROUPE CANAM INC.

PRÉLIMINAIRE

NE DOIT PAS SERVIR À LA CONSTRUCTION

REVISION DATE DESCRIPTION DESSIN VER

GERANT DE PROJET
-
-
-

DESSIN

DESSINÉ PAR CONÇU PAR INGÉNIEUR OU PROJET ÉCHELLE

SL Comme indiqué

VÉRIFIÉ PAR INGÉNIEURS CONSEILS / ARCHITECTES DATE (mm/aa/aaaa)

22/05/2026

CLIENT: LIXM ENTREPRENEUR GÉNÉRAL INC.



11505, 1re Avenue, bureau 500, Saint-Georges Beauce
Québec, Canada G5V 7G3
Téléphone : (418) 228-8031
Sans frais : (877) 459-8049
www.canam.com

SCAUX PROFESSIONNEL

PROJET

AGRANDISSEMENT DE JULES
VACHON 2026
TROIS-RIVIÈRES, QC

TITRE
CROQUIS PRÉLIMINAIRE -
ÉLEVATIONS


NUMÉRO CONTRAT P2026-098 NUMÉRO DESSIN EsMx501 DIVISION REVISION

Initiales




CÉDULE DES PORTES			
Identifiant	Qté	Porte 19 in.	Remarques
P1	6	3'-0" x 7'-0"	
P2	3	20'-0" x 20'-0"	CADRE POUR PORTE MONTANTE
P3	2	5'-0" x 20'-0"	CADRE POUR PORTE MONTANTE

Quincaillerie standard du fournisseur:
- Charnières : Stanley F88 179 4.5" x 4"
- Barre panique : Von Dupin 22 x 689 avec poignée extérieure 230L
- Cylindre permanent : Schlage 20001C 626
- Ferme-porte : LCN 1261 689
- Coupe-froid de tête et des montants : Unique 1650
- Coupe-froid du bas : Unique D54
- Seul : Voir la remarque dans la "Cédule de porte"

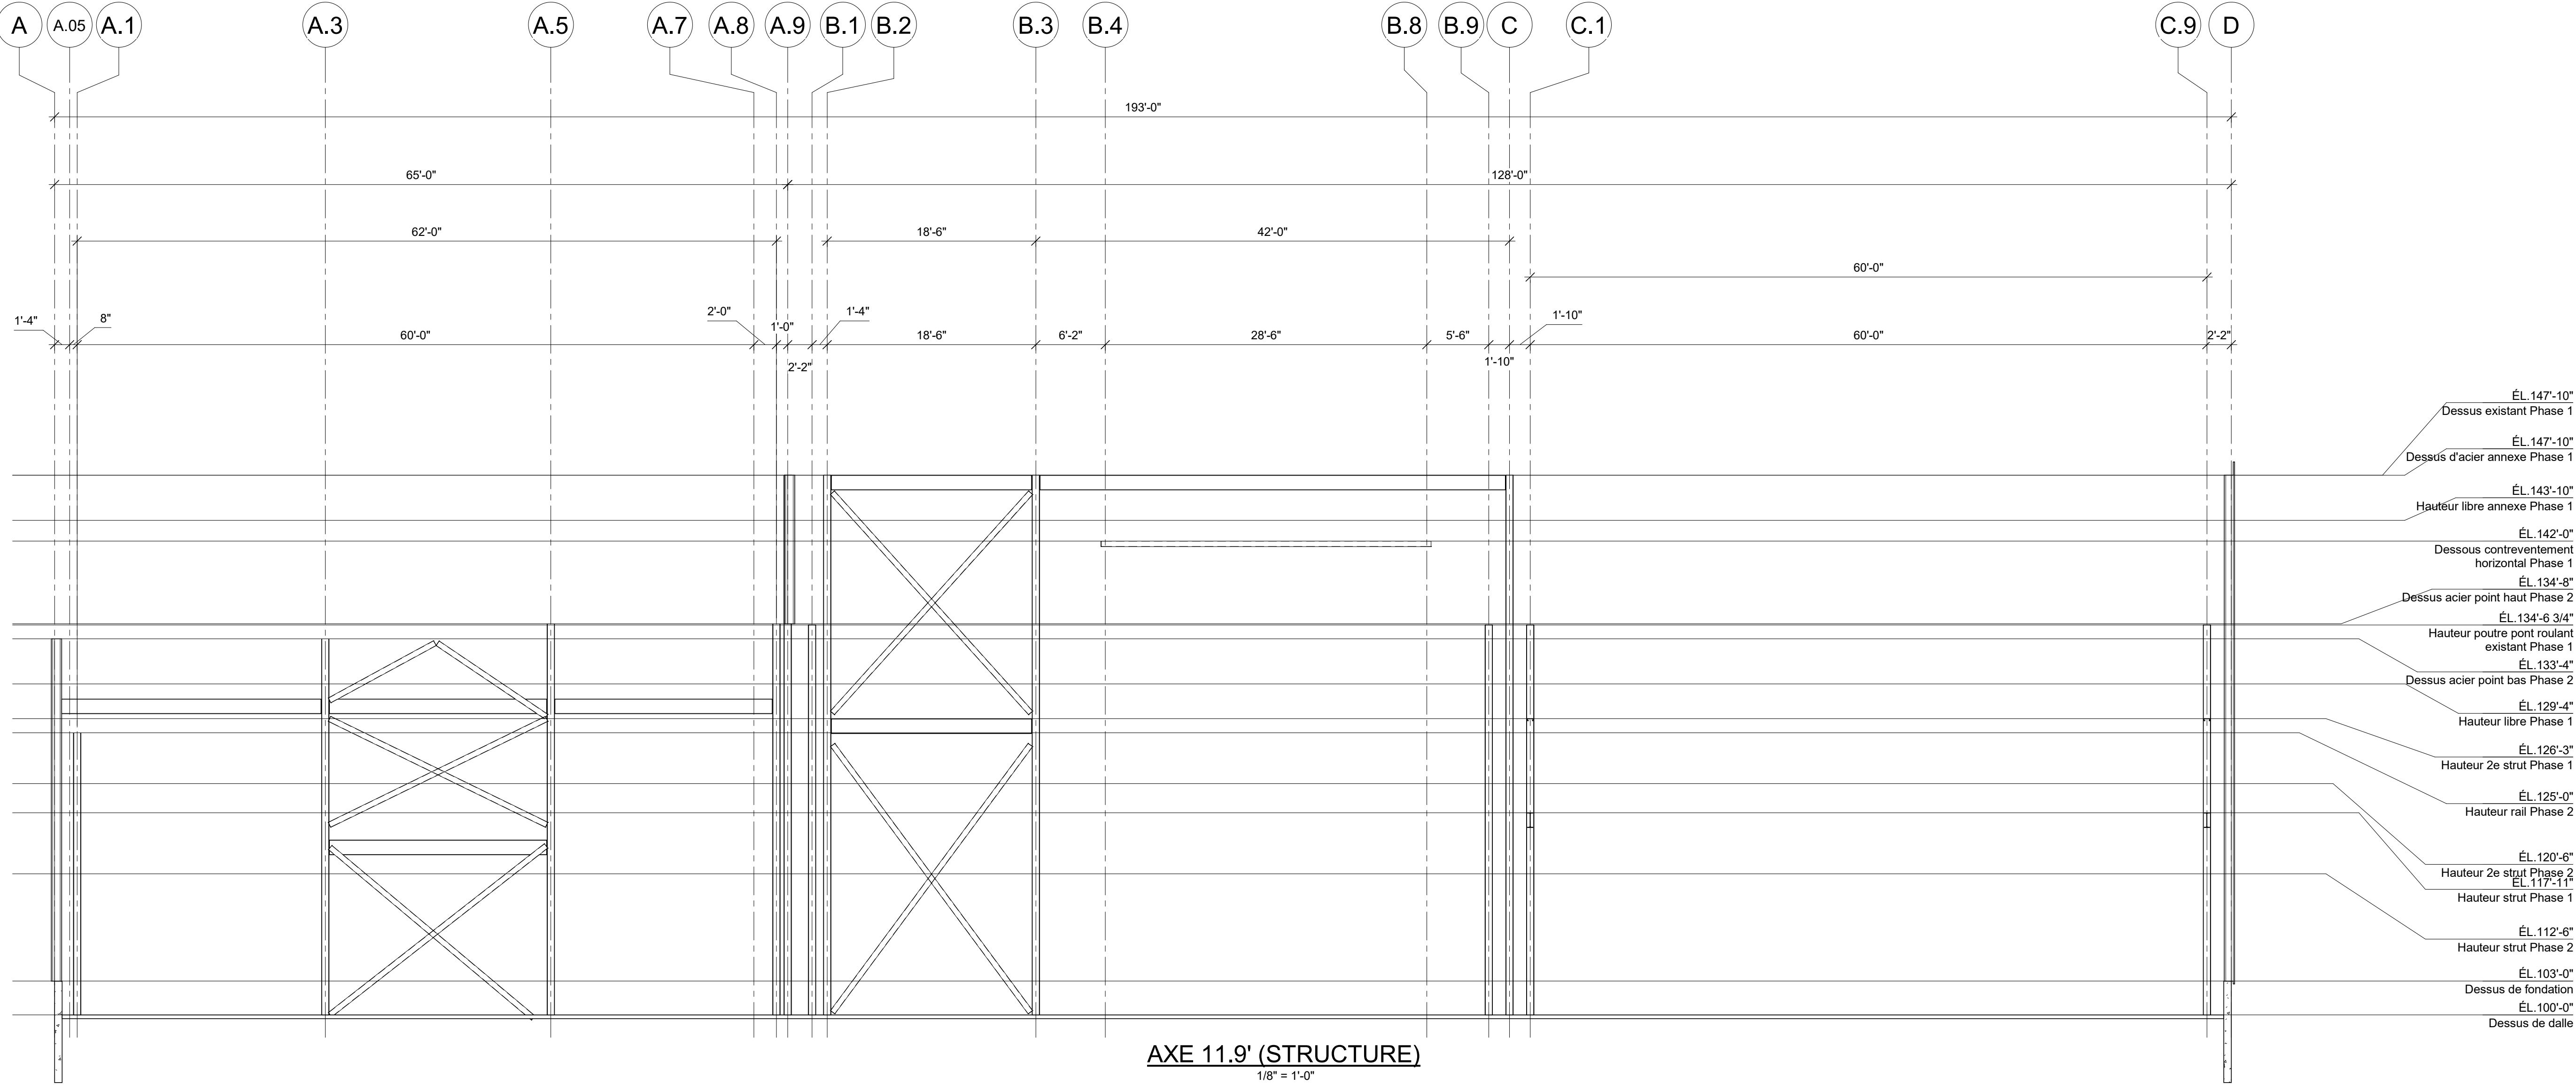


AXE 11.9' (STRUCTURE)

1/8" = 1'-0"

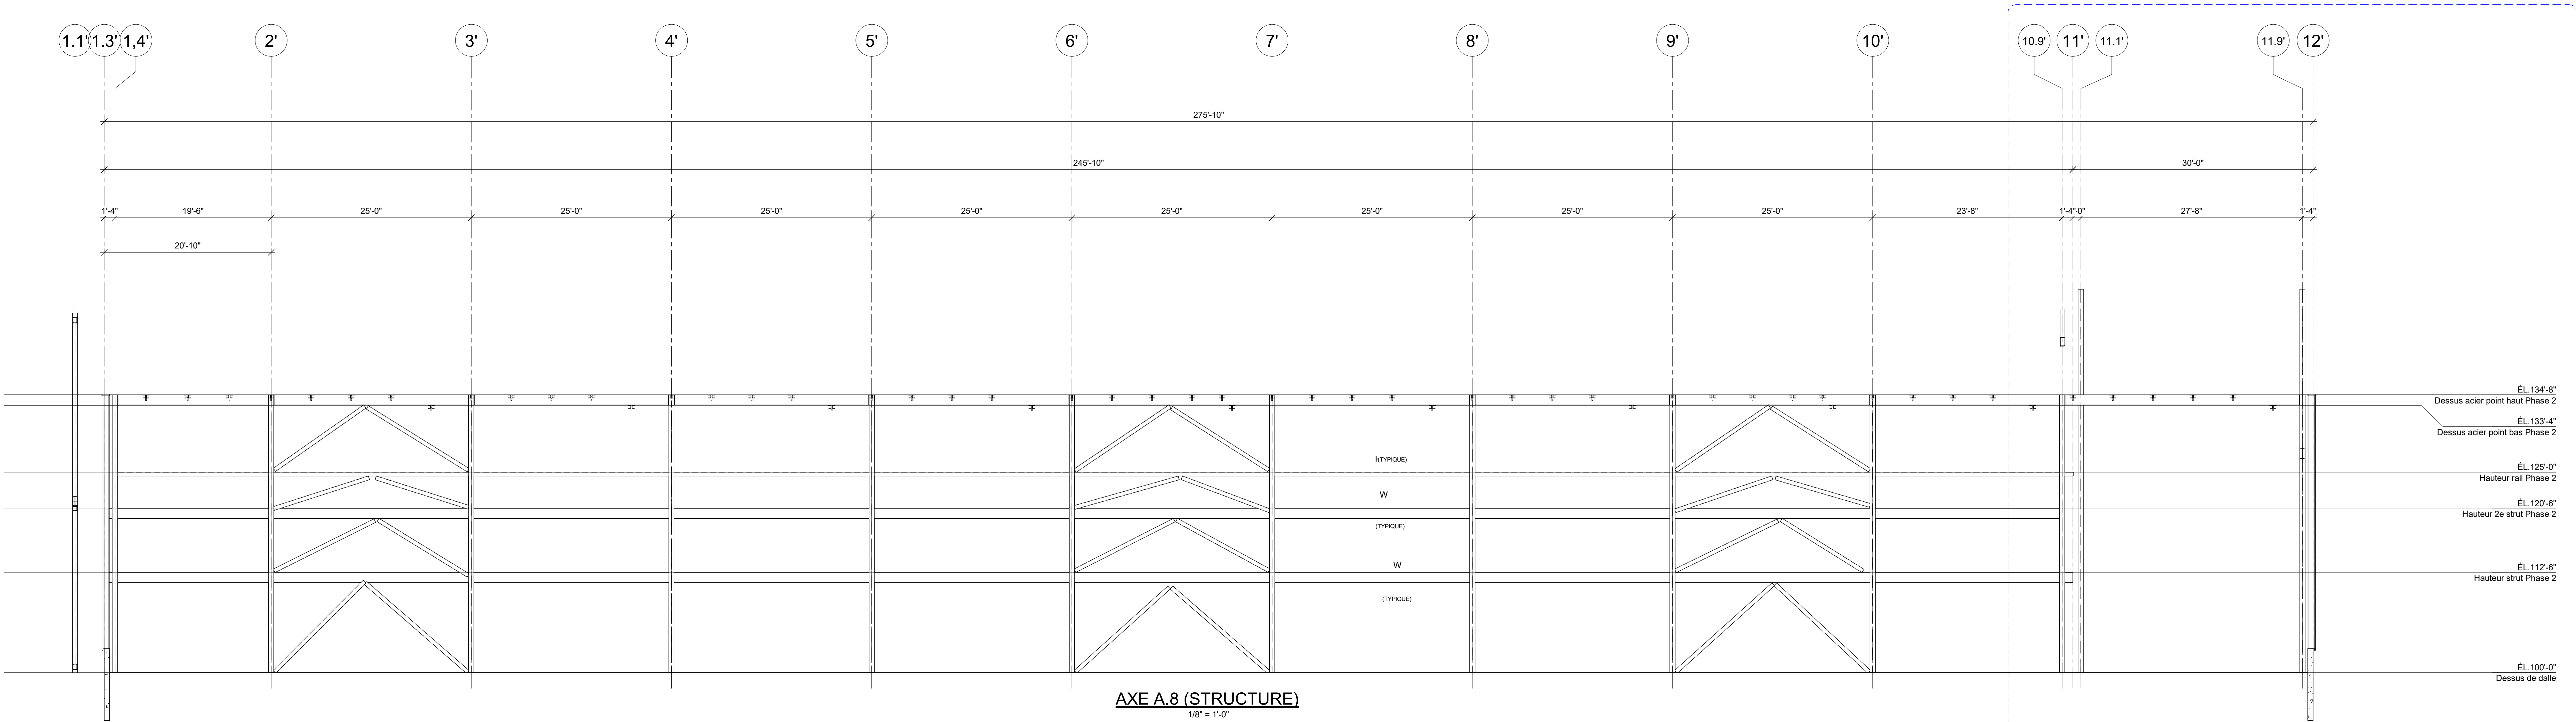

AXE A.8 (STRUCTURE)

1/8" = 1'-0"

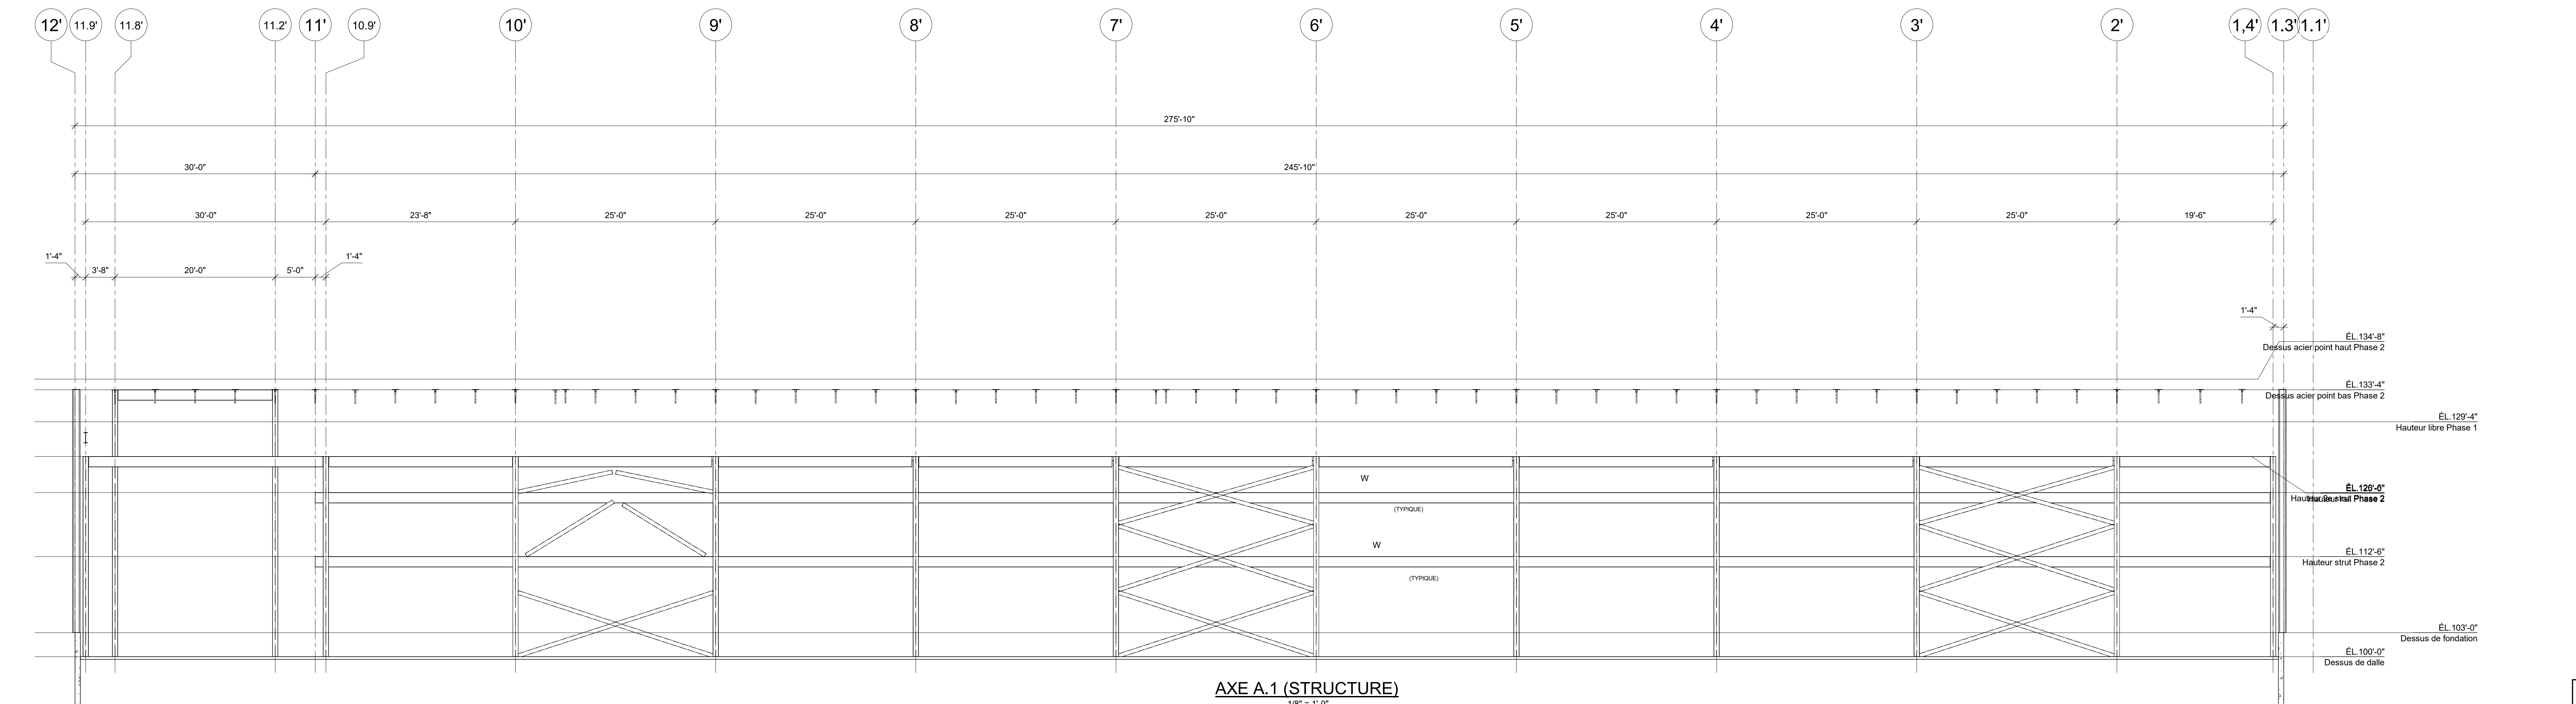

AXE A.1 (STRUCTURE)

1/8" = 1'-0"

NOTE POUR LE CONTRACTEUR/ÉRECTEUR:
IL EST STRICTEMENT DÉFENDU DE MODIFIER, COPIER, REPRODUIRE OU DE DISTRIBUER CES DESSINS OU QUELQUES REPRÉSENTATIONS DE CES DESSINS, PAR TOUTES SOURCES DE MÉDIA INCLUANT ÉLECTRONIQUEMENT, SANS L'APPROBATION ÉCRITE DE GROUPE CANAM INC.

PRÉLIMINAIRE

NE DOIT PAS SERVIR À LA CONSTRUCTION

REVISION	DATE	DESCRIPTION	DESS	VER
----------	------	-------------	------	-----

GERANT DE PROJET	-
	-
	-

DESSIN	
--------	--

DESSINÉ PAR	CONÇU PAR	INGÉNIEUR DU PROJET	ÉCHELLE:
-------------	-----------	---------------------	----------

INITIALE			Comme indiqué
----------	--	--	---------------

VÉRIFIÉ PAR	INGÉNIEURS CONSEILS / ARCHITECTES	DATE (mm/aa/aaaa)
-------------	-----------------------------------	-------------------

CLIENT:	LIXM ENTREPRENEUR GÉNÉRAL INC.
---------	--------------------------------


11505, 1re Avenue, bureau 500, Saint-Georges Beauce
Québec, Canada G5Y 7X5
Téléphone : (418) 228-8031
Sans frais : (877) 459-8049
www.canam.com



SCAUX PROFESSIONNEL

PROJET
AGRANDISSEMENT DE JULES VACHON 2026
TROIS-RIVIÈRES, QC

TITRE
CROQUIS PRÉLIMINAIRE - ÉLEVATION, COUPE DE MUR ET CÉDULES

NUMÉRO CONTRAT	NUMÉRO DESSIN	DIVISION	REVISION
----------------	---------------	----------	----------

P2026-098	EsMx502		
-----------	---------	--	--

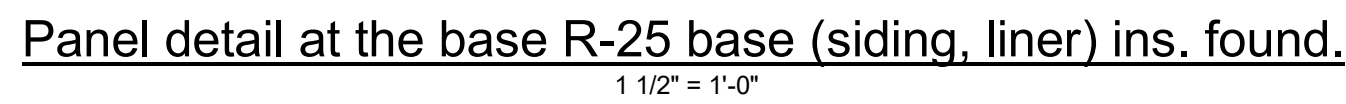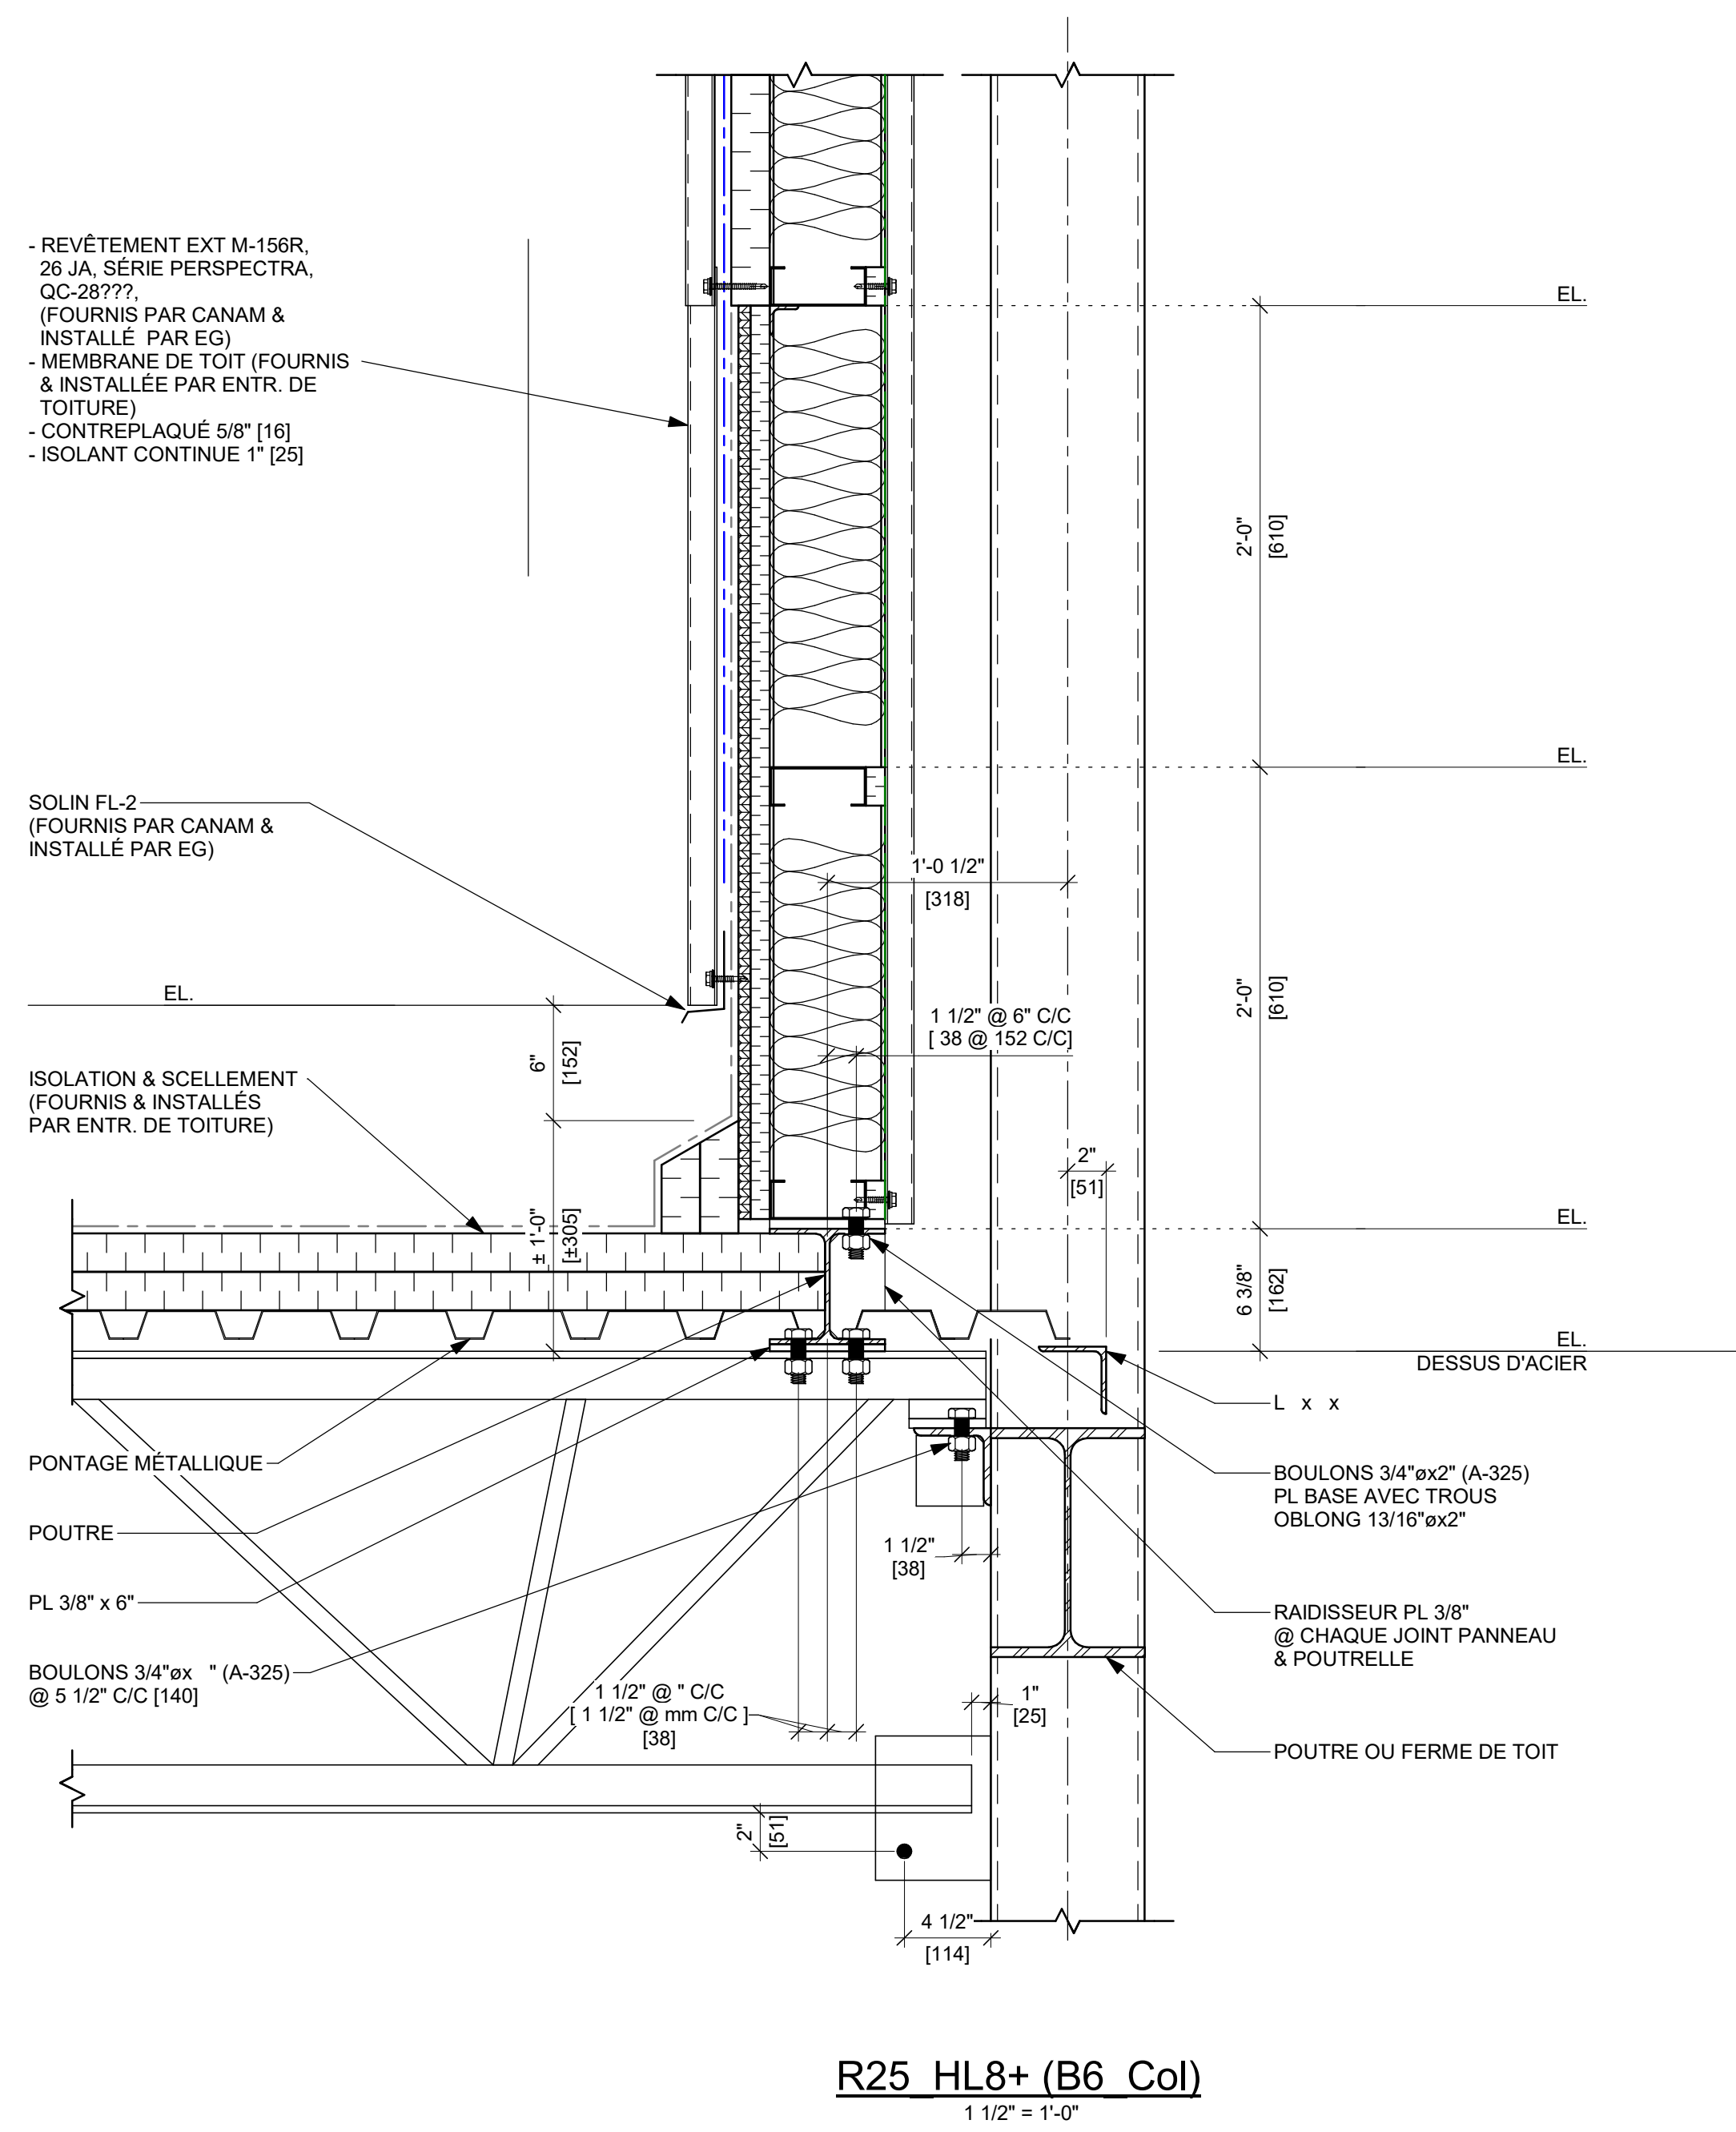

NE DOIT PAS SERVIR À LA
CONSTRUCTION

REVISION	DATE	DESCRIPTION	DESS.	VER.
----------	------	-------------	-------	------

GERANT DE PROJET	-
	-
	-
	-
	-

DESSIN :			
DESSINÉ PAR	CONÇU PAR	INGÉNIEUR DU PROJET	ÉCHELLE :
INITIALE			Comme indiqué
VÉRIFIÉ PAR	INGÉNIEURS CONSEILS / ARCHITECTES		DATE (jj/mm/aaaa) :
			22/05/2026

CLIENT: LIXM ENTREPRENEUR GÉNÉRAL INC.



BOEAO PROFESSIONNEL

PROJET

AGRANDISSEMENT DE JULES
VACHON 2026
TROIS-RIVIÈRES, QC

CROQUIS PRÉLIMINAIRE - DÉTAILS

NUMERO CONTRAT P2026-098	NUMERO DESSIN EsMx601	DIVISION	REVISION 
-----------------------------	--------------------------	----------	---

