




NOTE POUR LE CONTRACTEUR/ÉRECTEUR:  
IL EST STRICTEMENT DÉFENDU DE MODIFIER, COPIER, REPRODUIRE OU DE DISTRIBUER CES DESSINS OU QUELQUES REPRÉSENTATIONS DE CES DESSINS, PAR TOUTES SOURCES DE MÉDIA INCLUANT ÉLECTRONIQUEMENT, SANS L'APPROBATION ÉCRITE DE GROUPE CANAM INC.

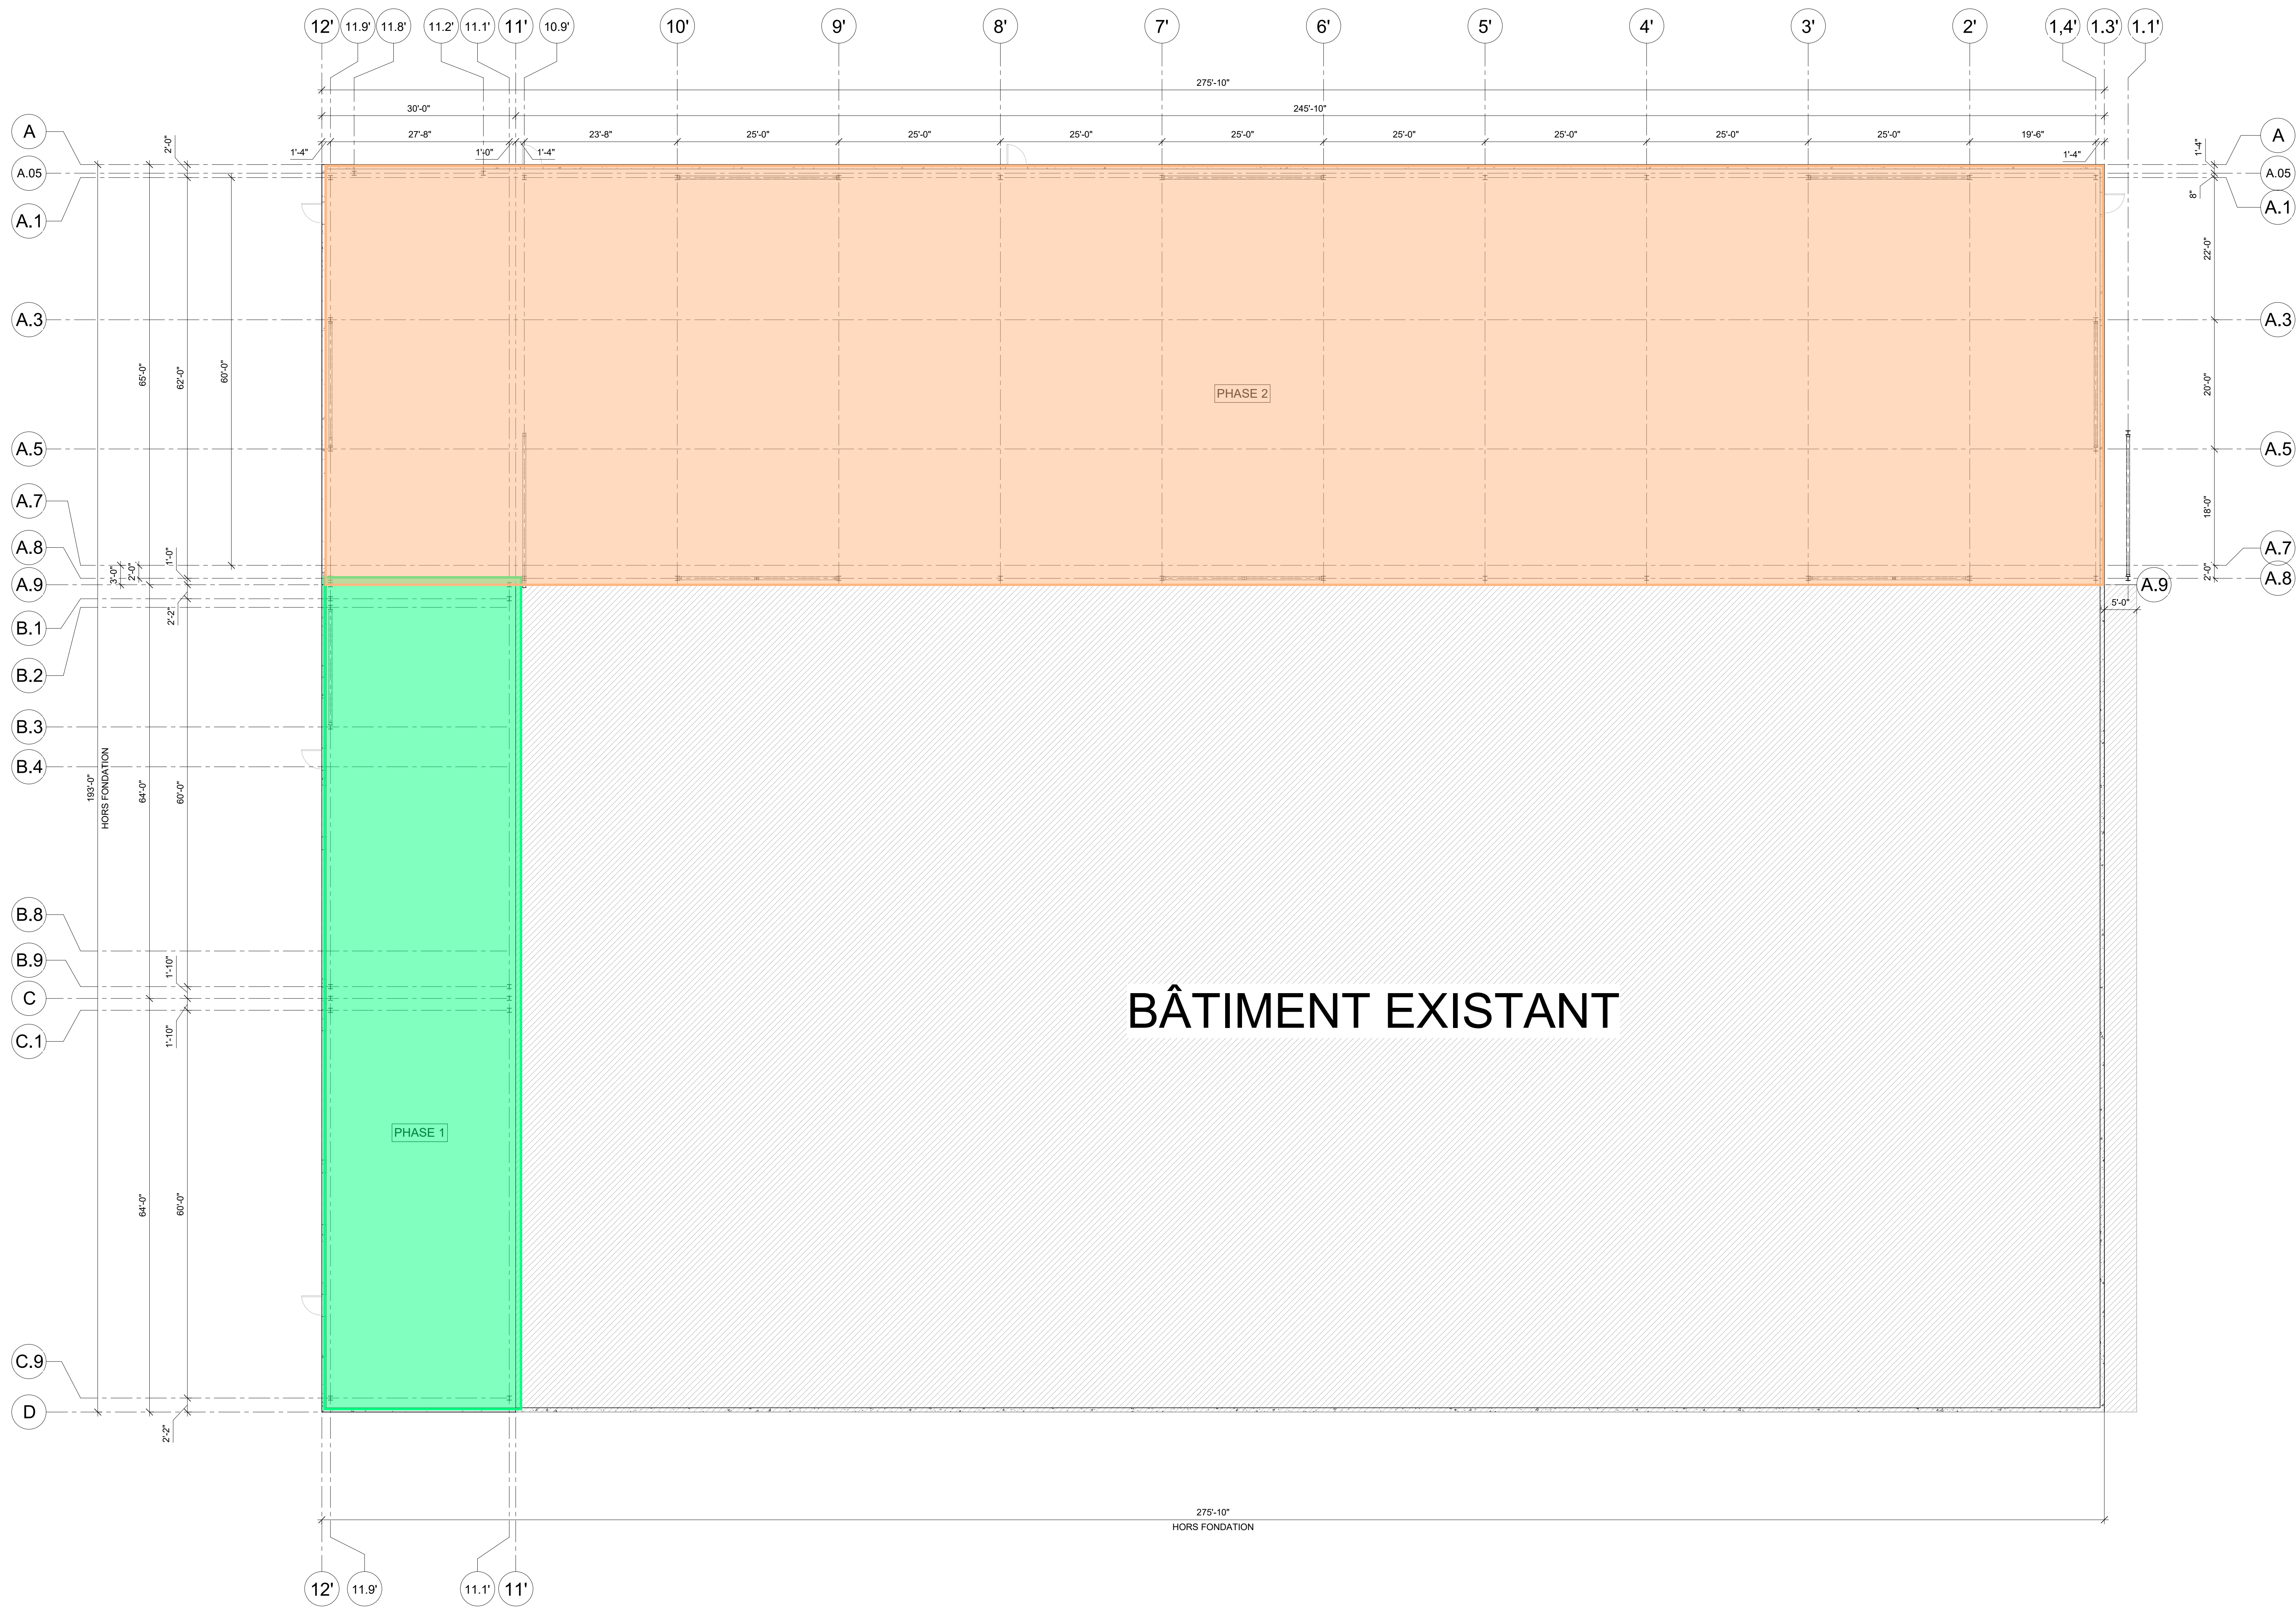

PLAN D'ANCRAGE  
3/32" = 1'-0"

PRÉLIMINAIRE

NE DOIT PAS SERVIR À LA  
CONSTRUCTION

| REVISION         | DATE | DESCRIPTION | DESS | VER |
|------------------|------|-------------|------|-----|
| GERANT DE PROJET |      |             |      |     |
|                  |      |             |      |     |
|                  |      |             |      |     |
|                  |      |             |      |     |

|             |                                   |                     |               |
|-------------|-----------------------------------|---------------------|---------------|
| DESSIN      | CONÇU PAR                         | INGÉNIEUR DU PROJET | ÉCHELLE:      |
| SL          |                                   |                     | 3/32" = 1'-0" |
| VÉRIFIÉ PAR | INGÉNIEURS CONSEILS / ARCHITECTES | DATE (jj/mm/aaaa)   |               |
|             |                                   | 22/05/2026          |               |

CLIENT: LXM ENTREPRENEUR GÉNÉRAL INC.



|                      |
|----------------------|
| SCAUX PROFESSIONNELS |
|                      |
|                      |
|                      |

PROJET  
AGRANDISSEMENT DE JULES  
VACHON 2026  
TROIS-RIVIÈRES, QC

TITRE  
CROQUIS PRÉLIMINAIRE - PLAN  
D'ANCRAGE

|                             |                          |          |          |
|-----------------------------|--------------------------|----------|----------|
| NUMÉRO CONTRAT<br>P2026-098 | NUMÉRO DESSIN<br>EsMx101 | DIVISION | REVISION |
|                             |                          |          |          |