

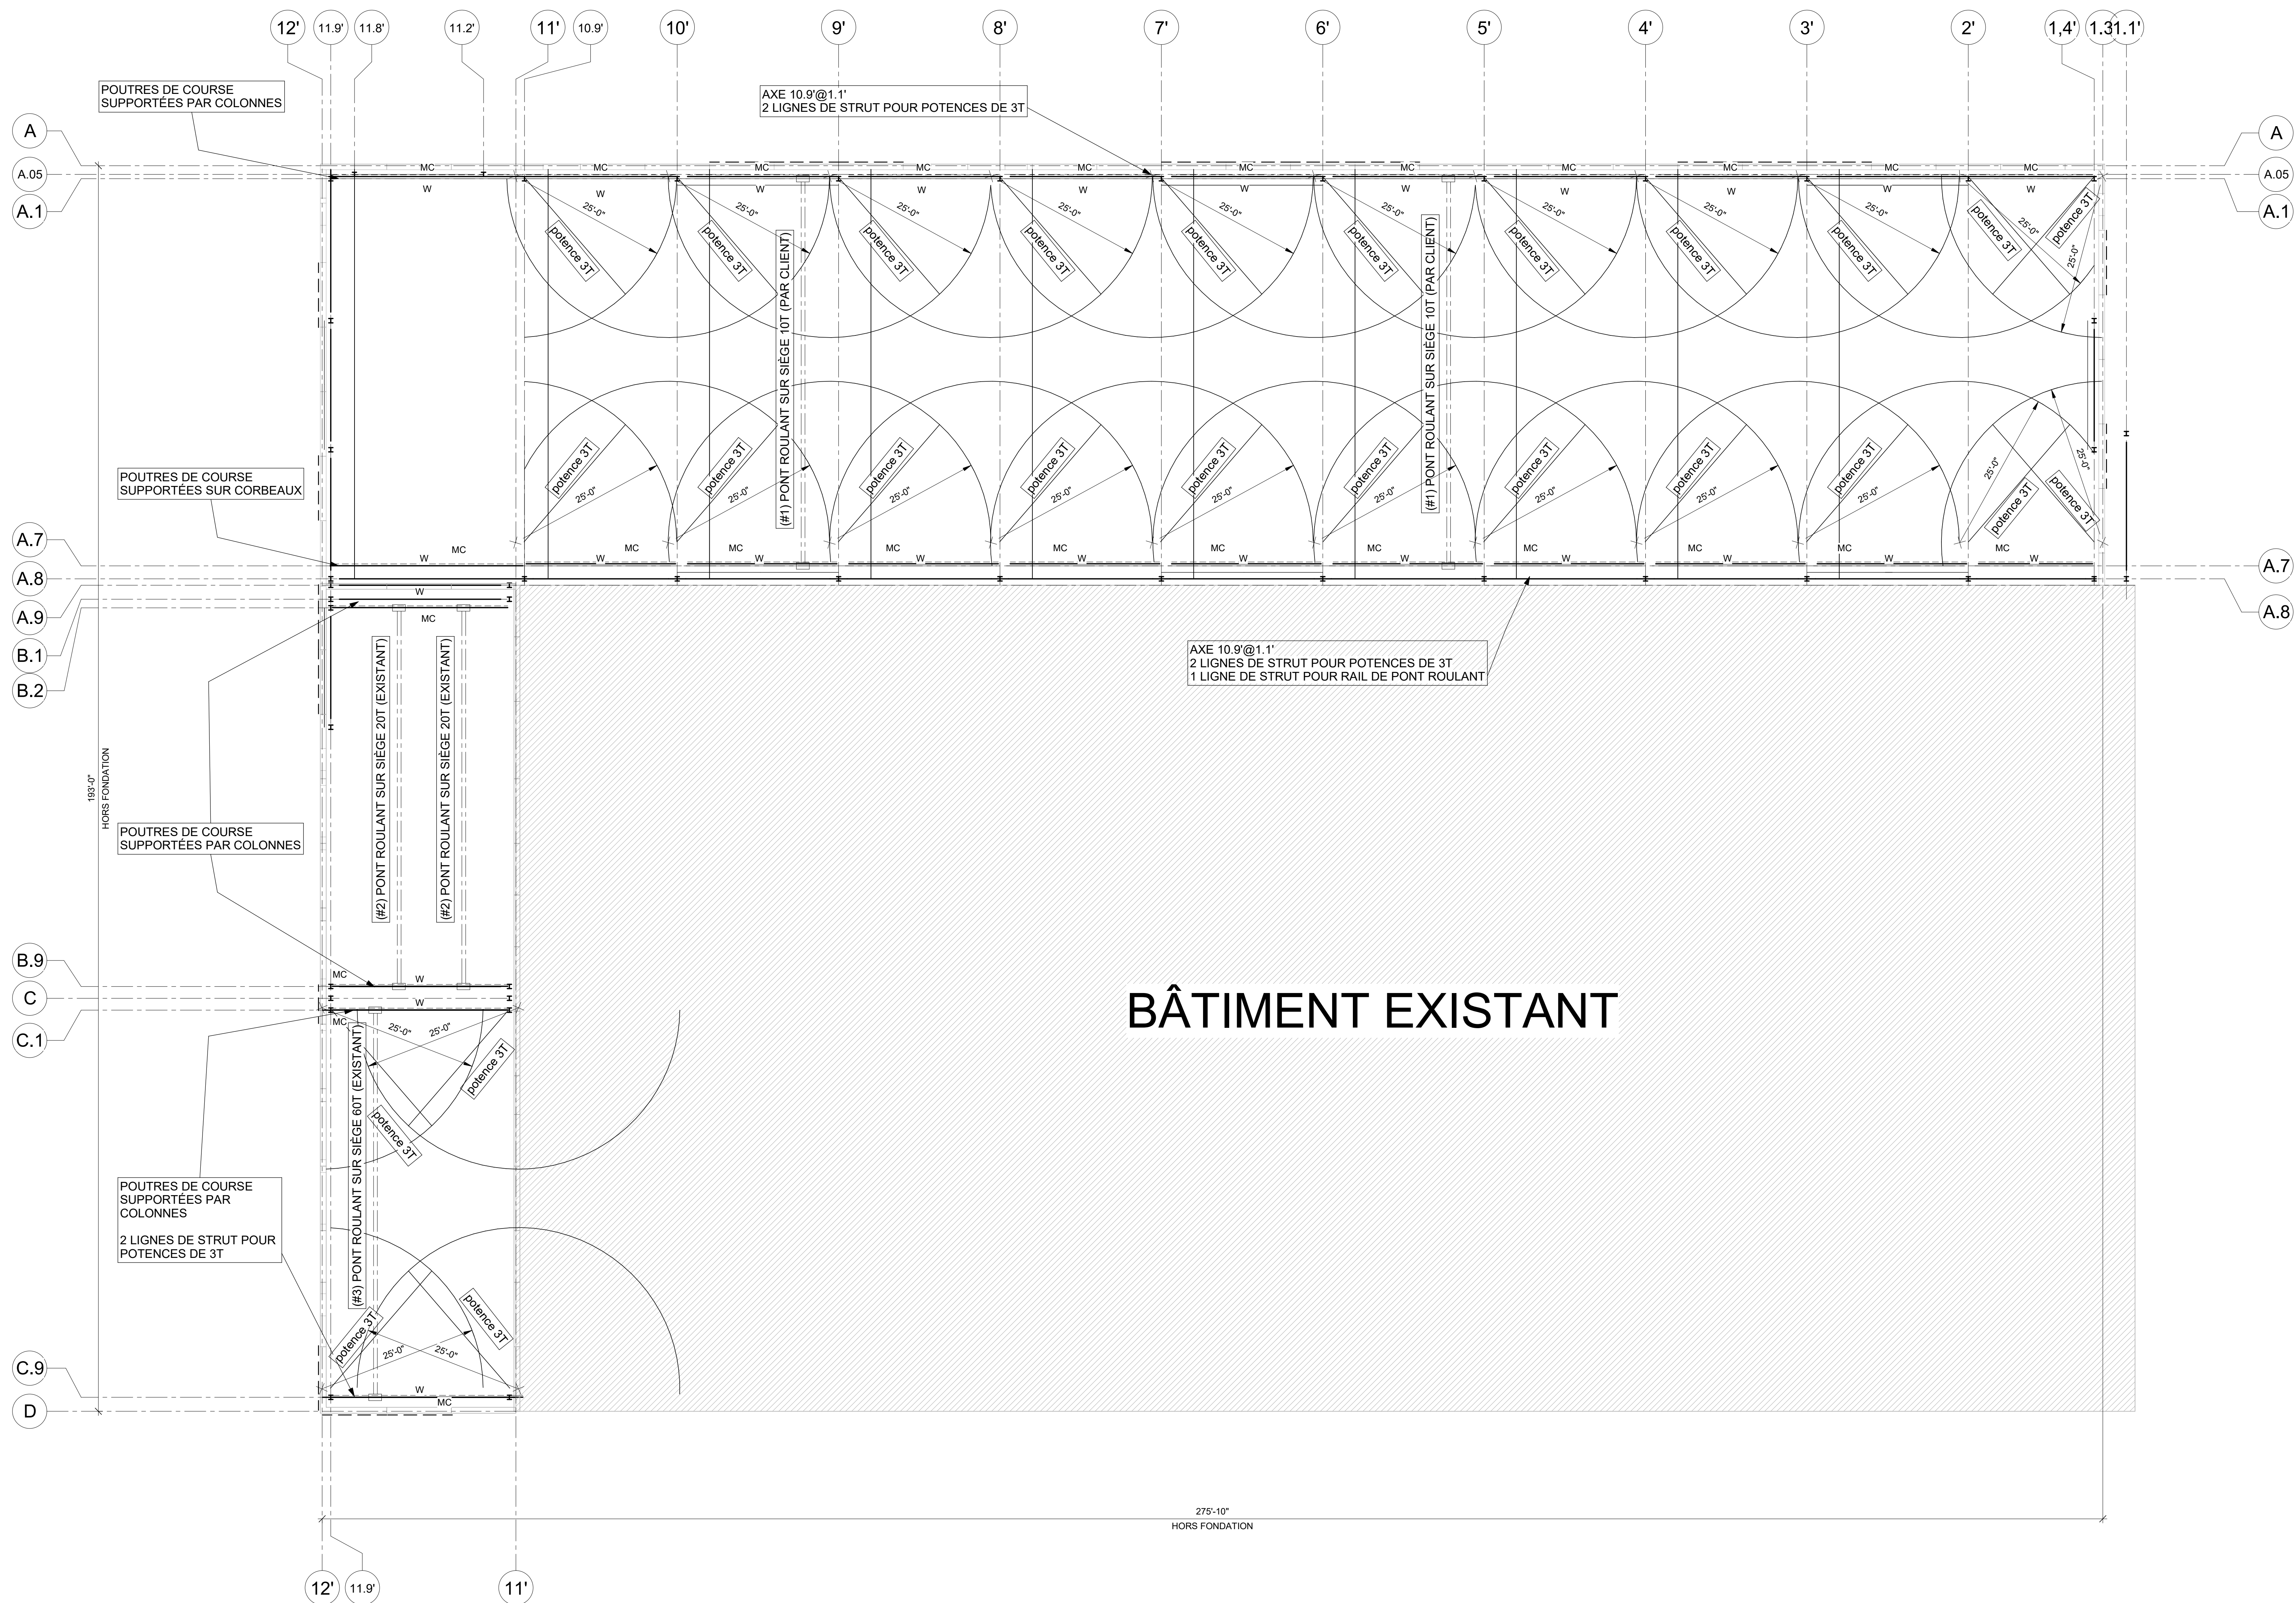


TABLEAU CHARGES PONT ROULANT				
CAPACITÉ	POIDS DU PONT	CHARIOT	CHARGE MAX. PAR ROUE (DYNAMIQUE)	ESPACEMENT DES ROUES
22000 lbs 10T (#1)	11800 lb	1400 lb	18.4 kip	9'-0"
40000 lbs 20T (#2)	27779 lb	7000 lb	39 kip	13'-0"
120000 lbs	42070 lb	12500 lb	96 kip	17'-0"

PLAN PONT ROULANT
3/32" = 1'-0"

NOTE POUR LE CONTRACTEUR/ÉRECTEUR:
IL EST STRICTEMENT DÉFENDU DE MODIFIER, COPIER, REPRODUIRE OU DE DISTRIBUER CES DESSINS OU QUELQUES REPRÉSENTATIONS DE CES DESSINS, PAR TOUTES SOURCES DE MÉDIA INCLUANT ÉLECTRONIQUEMENT, SANS L'APPROBATION ÉCRITE DE GROUPE CANAM INC.

PRÉLIMINAIRE

NE DOIT PAS SERVIR À LA
CONSTRUCTION

REVISION	DATE	DESCRIPTION	DESS	VER
----------	------	-------------	------	-----

GERANT DE PROJET	-
	-
	-
	-

DESSIN

DESSINÉ PAR	CONÇU PAR	INGÉNIEUR DU PROJET	ÉCHELLE
SL			3/32" = 1'-0"

VÉRIFIÉ PAR	INGÉNIEURS CONSEILS / ARCHITECTES	DATE (mm/aaaa)
		22/05/2026

CLIENT: LIXM ENTREPRENEUR GÉNÉRAL INC.

CANAM
11505, 1re Avenue, bureau 500, Saint-Georges Beauce
Québec, Canada, G5Y 7X3
Téléphone : (418) 228-8031
Sans frais : (877) 459-8049
www.canam.com

SCAUX PROFESSIONNEL

PROJET
AGRANDISSEMENT DE JULES
VACHON 2026
TROIS-RIVIÈRES, QC

TITRE
CROQUIS PRÉLIMINAIRE - PLAN DE
PONT ROULANT

NUMÉRO CONTRAT	NUMÉRO DESSIN	DIVISION	REVISION
P2026-098	EsMx301		