



ACCUMULATION DE NEIGE


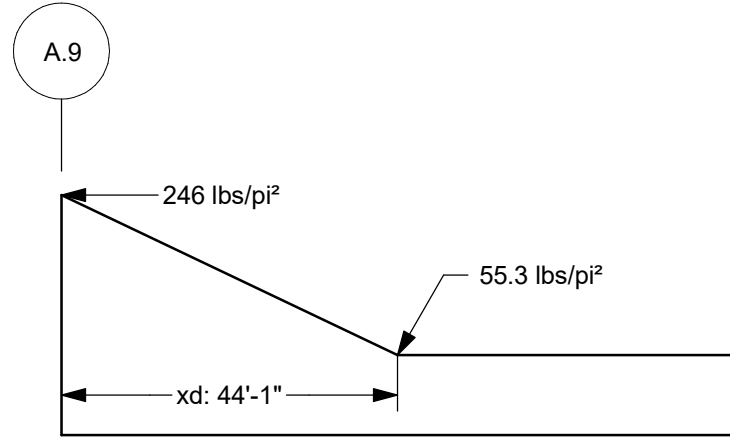


DIAGRAMME DE SOULEVEMENT BRUT (NON PONDÉRÉ)

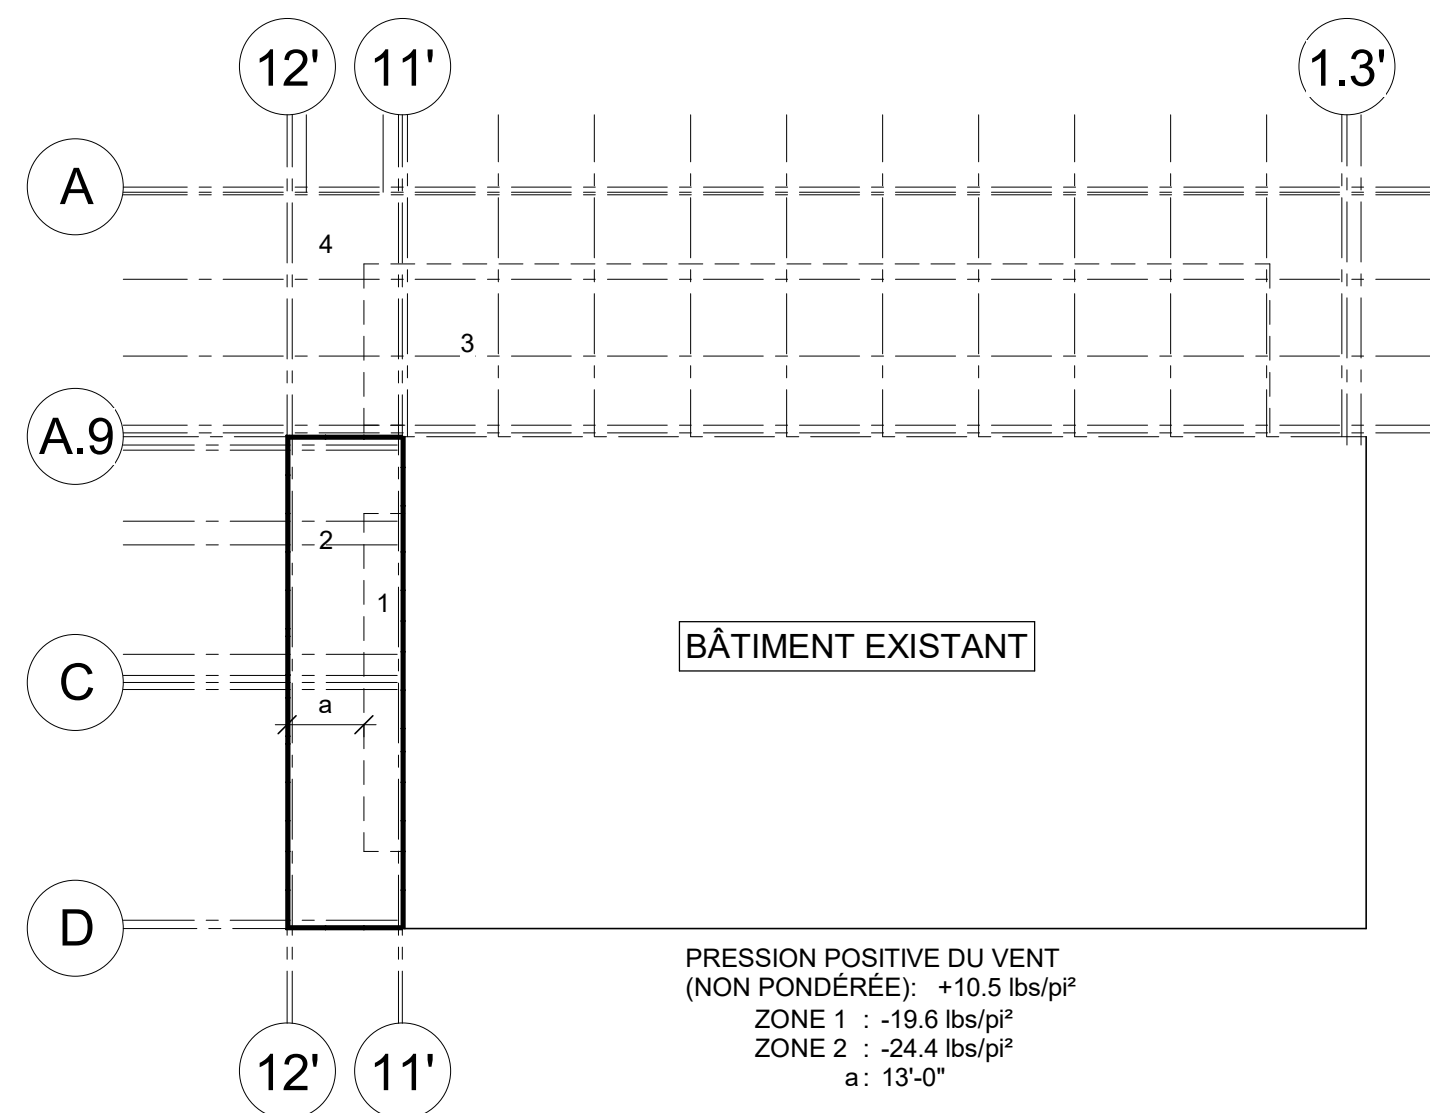

NOTE POUR LE CONTRACTEUR/ÉRECTEUR:
IL EST STRICTEMENT DÉFENDU DE MODIFIER, COPIER, REPRODUIRE OU DE DISTRIBUER CES DESSINS OU QUELQUES REPRÉSENTATIONS DE CES DESSINS, PAR TOUTES SOURCES DE MÉDIA INCLUANT ÉLECTRONIQUEMENT, SANS L'APPROBATION ÉCRITE DE GROUPE CANAM INC.

TOIT
DESSUS DE PILASTRE : 99'-0"
DESSUS DE LA DALLE : 100'-0"
DESSUS DE LA FONDATION : 103'-0"
HAUTEUR LIBRE : VOIR CROQUIS
DESSUS TACHER : VOIR CROQUIS
HAUTEUR DE PARAPET : 1'-2"
DESSUS DE PARAPET : VOIR CROQUIS

CHARGES

C.M. : 18 lbs/ft²
C.O.L. : 5 lbs/ft²
S_u : 59.5 lbs/ft²
S_v : 8 lbs/ft²
C_b x C_w : 0.8
C.V. au toit : 0 lbs/ft²
L_v : 1.0
Charge de neige au toit : 55.3 lbs/ft²
L_v : 1.0
Vent q = 1/50 : 9 lbs/ft²
Séisme (Sol de classe D assumé)

L_v : 1.0
S_u (0.2) : 0.588
S_u (0.5) : 0.516
S_u (1.0) : 0.316
S_u (2.0) : 0.153
S_u (5.0) : 0.0434
S_u (10.0) : 0.137
PGA : 0.328
PGV : 0.361

CHARGES :

- Charge morte au toit (excluant charge collatérale) : lbs/ft²
- Charge collatérale : lbs/ft² (incluant éclairage et/ou mécanique et gicleurs plus petite que 4" de diamètre)
- Charge de neige au toit : lbs/ft²
- Charge vive au toit : lbs/ft²
- Charge de vent q 1/50 : lbs/ft²
- Charge de neige au sol : S_u = lbs/ft²
- Catégorie de risque : normal
- Coefficient de surcharge de neige : C_b = 0.8
- C_w = 1.0

• Code Applicable : Code National du Bâtiment du Canada
Code du bâtiment du Québec, dernières éditions adoptées
Code de Pratique Standard ICCA.

• Type de sol assumé : classe D

• NOTE :
1. Si toutefois la catégorie d'emplacement devient E ou F selon le rapport géotechnique, le concept structural préliminaire (localisation et géométrie des contreventements, etc.) devra être validé et coordonné par l'ingénieur de Canam.

PRÉLIMINAIRE

NE DOIT PAS SERVIR À LA CONSTRUCTION

REVISION DATE DESCRIPTION DESSIN VER

DEVANT DE PROJET
-
-
-

DESSIN

DESSIN PAR SL CONÇU PAR INGÉNIEUR DU PROJET ÉCHELLE: Comme indiqué

VÉRIFIÉ PAR INGÉNIEURS CONSEILS / ARCHITECTES DATE (mm/aa/aaaa) 22/05/2026

CLIENT: LIXM ENTREPRENEUR GÉNÉRAL INC.



11505, 1^{re} Avenue, bureau 500, Saint-Georges Beauce
Québec, Canada, G5Y 7X3
Téléphone : (418) 228-8031
Sans frais : (877) 459-8049
www.canam.com

SCAUX PROFESSIONNEL

PROJET


AGRANDISSEMENT DE JULES
VACHON 2026
TROIS-RIVIÈRES, QC

TITRE

CROQUIS PRÉLIMINAIRE - PLAN DE TOIT

NUMÉRO CONTRAT P2026-098 NUMÉRO DESSIN EsMx401 DIVISION REVISION

Initiales

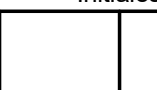

BÂTIMENT EXISTANT
J00571

PLAN DE TOIT
3/32" = 1'-0"