

IONS

[illegible]


DRAWN BY
Author

NAME

LOW ROOF FRAMING PLAN

NUMBER | REVISION

-202

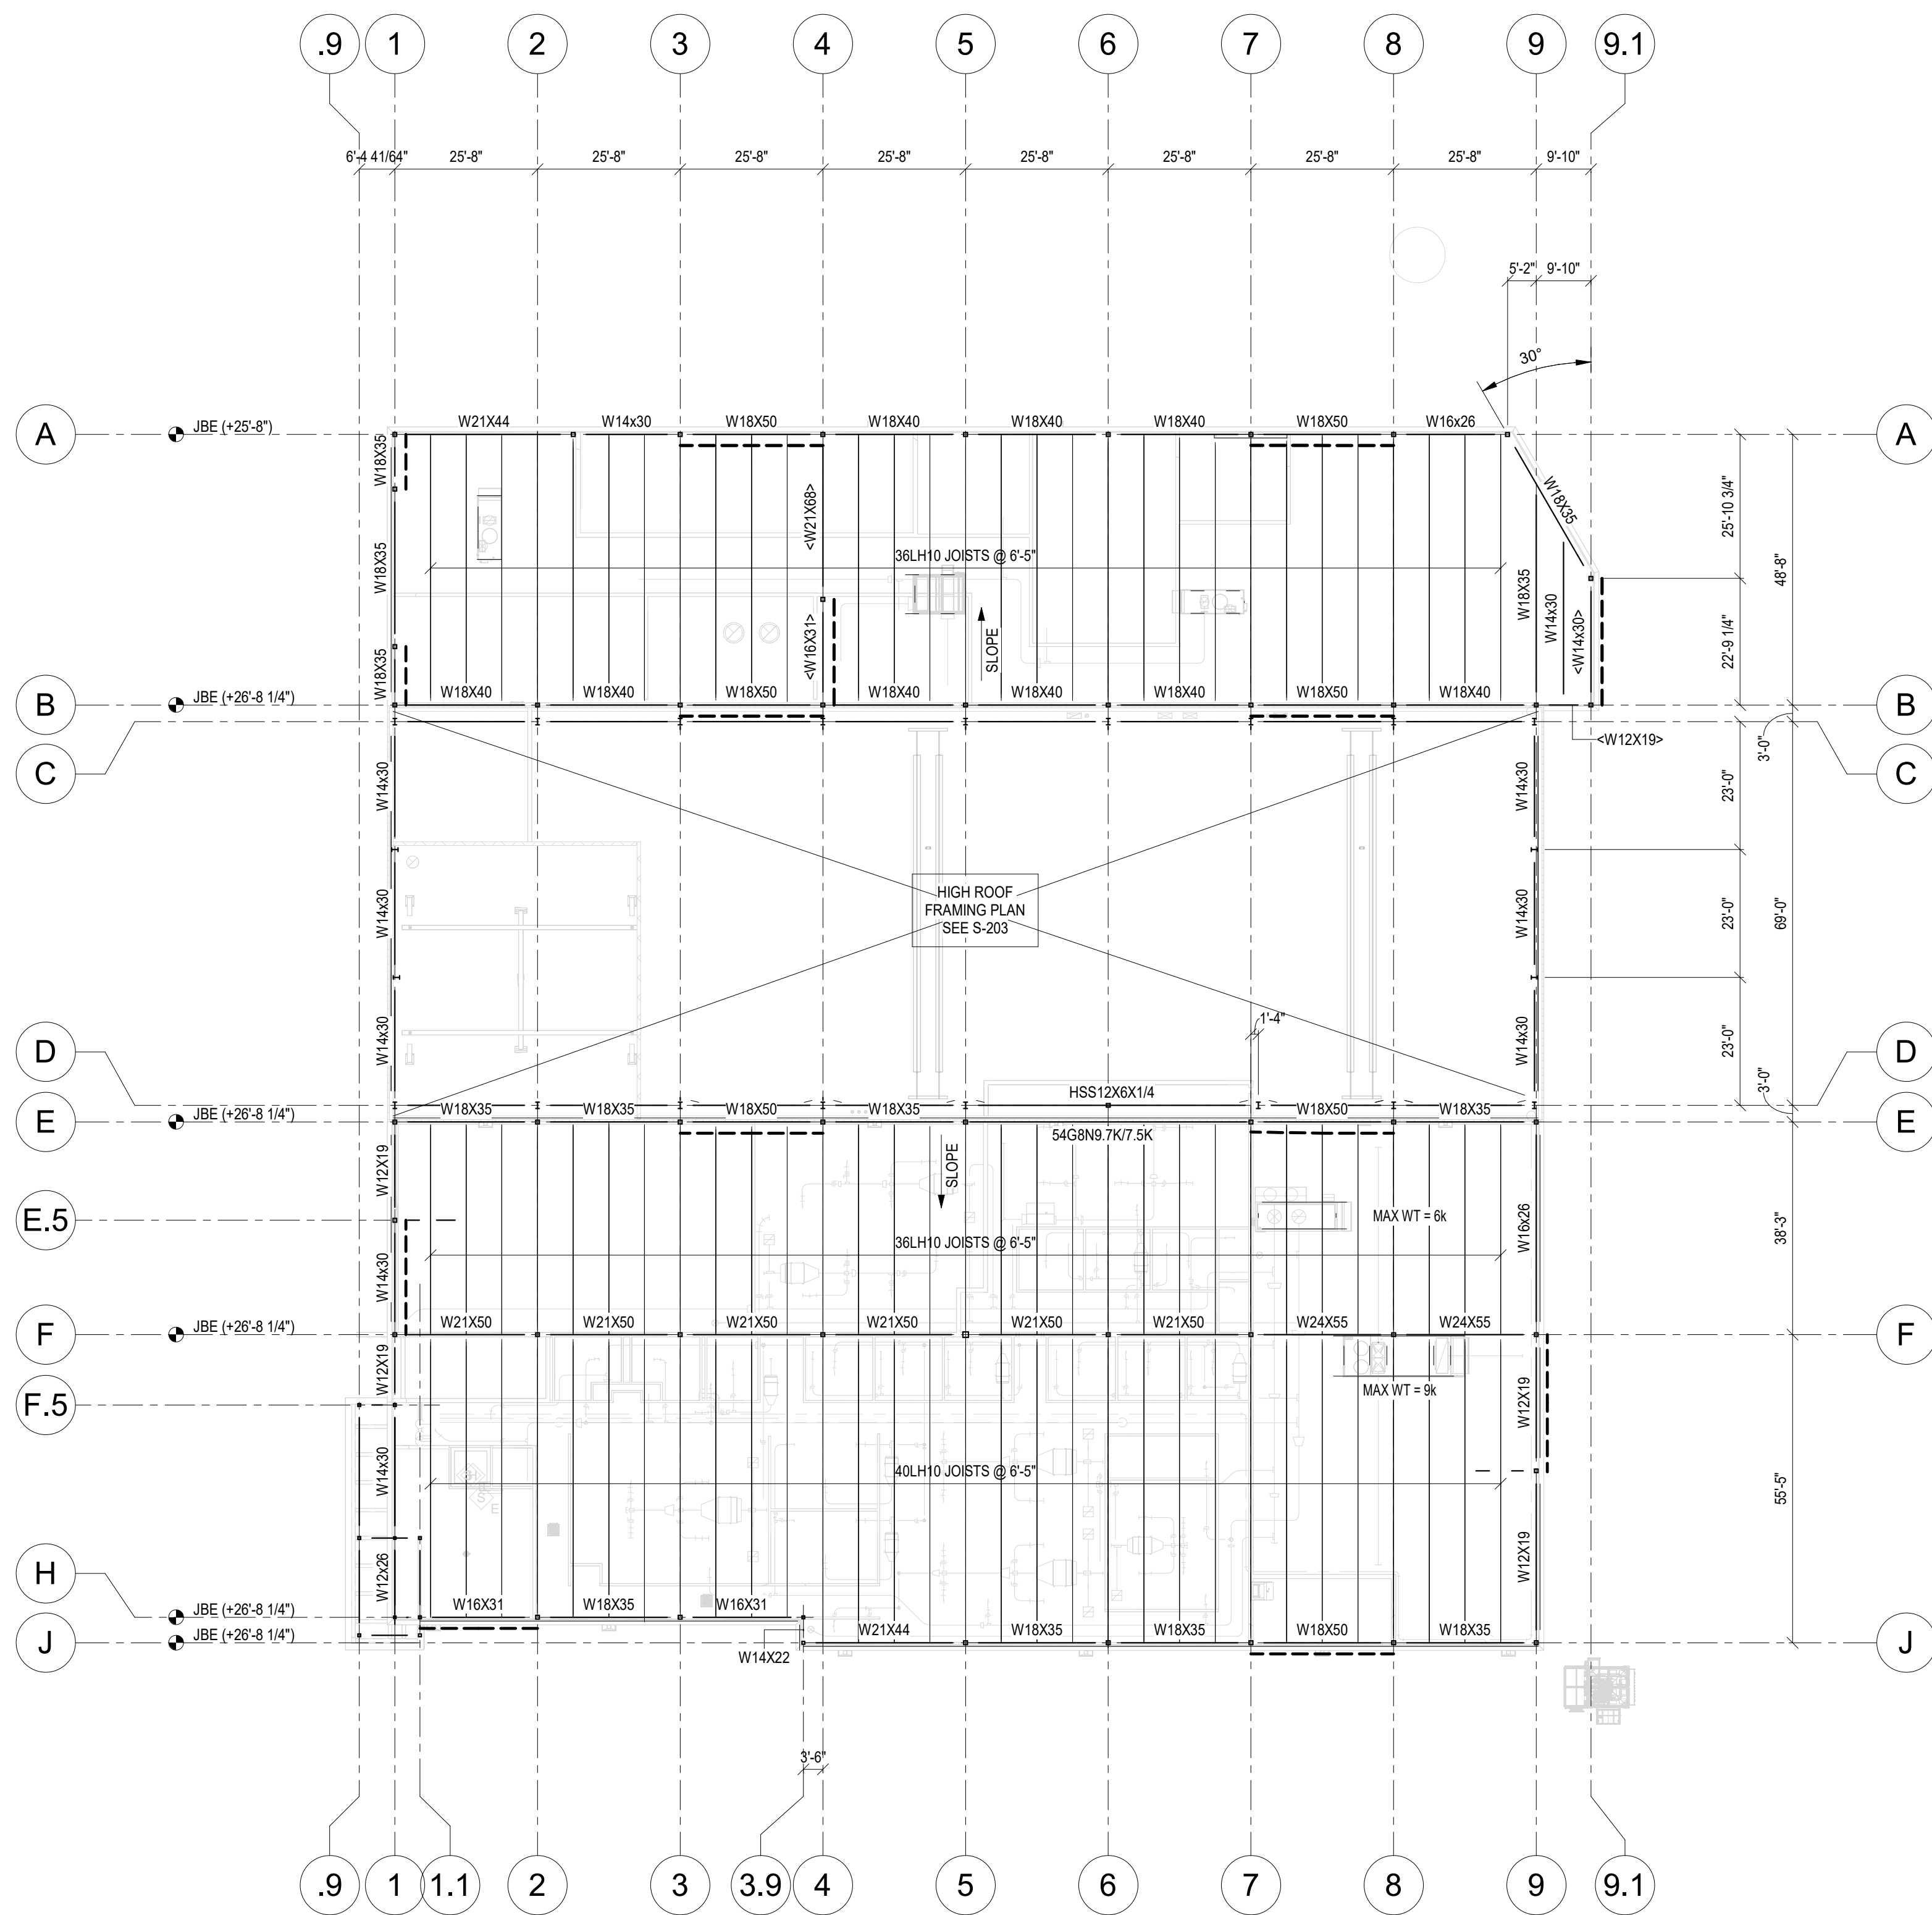

1 ROOF FRAMING PLAN
S-202 3/64" = 1'-0"

FLOOR FRAMING PLAN SYMBOL LEGEND

- | | |
|---|---|
|  | INDICATES DIRECTION OF SPAN OF COMPOSITE CONCRETE FLOOR SLAB. STRUCTURAL SLAB TO BE 3" LIGHT WEIGHT CONCRETE OVER 2" 20 GA COMPOSITE METAL DECK. (TOTAL THICKNESS = 5" 4") REINFORCED WITH #6-1/2 BW@2'9" W/WF. |
|  | INDICATES DIRECTION OF SPAN OF K" DEEP, X GAGE, WIDE RIB, GALVANIZED METAL ROOF DECK. SEE SPECIFICATIONS. |
|  | INDICATES DIRECTION OF SPAN OF W" RIB, GALVANIZED, METAL ROOF DECK. SEE SPECIFICATIONS. |
|  | INDICATES COORDINATE FINAL DIMENSIONS WITH ARCHITECTURAL DRAWINGS, EQUIPMENT SUPPLIER, AND EQUIPMENT CONTRACTOR. |
|  | INDICATES MOMENT CONNECTION TO DEVELOP FULL BENDING AND SHEAR CAPACITY OF BEAM OR GIRDER, UNLESS OTHERWISE NOTED. |
|  | INDICATES FULL DEPTH FITTED STIFFENER CONNECTION, SEE "X/SX". |
|  | INDICATES CONCRETE HOUSEKEEPING SLAB, COORDINATE QUANTITY, SIZE, AND LOCATION WITH MEP DRAWINGS, SEE "X/SX". |