

**NOT FOR
CONSTRUCTION**

not for permits, pricing or other official purposes. This document
is not been completed or checked and is for general information
or comment only.

ISSUE DATE	DESCRIPTION
5/15/2026	60% DESIGN

1-12-000

PROJECT PANDORA

GRIFFIN ROAD SOUTH, BLOOMFIELD,
 06002

REVISIONS

[illegible]


CHECKED BY	DRAWN BY
Checker	Author

SHEET NAME

SLAB ON GRADE PLAN

SHEET NUMBER | **REVISION**

S-101

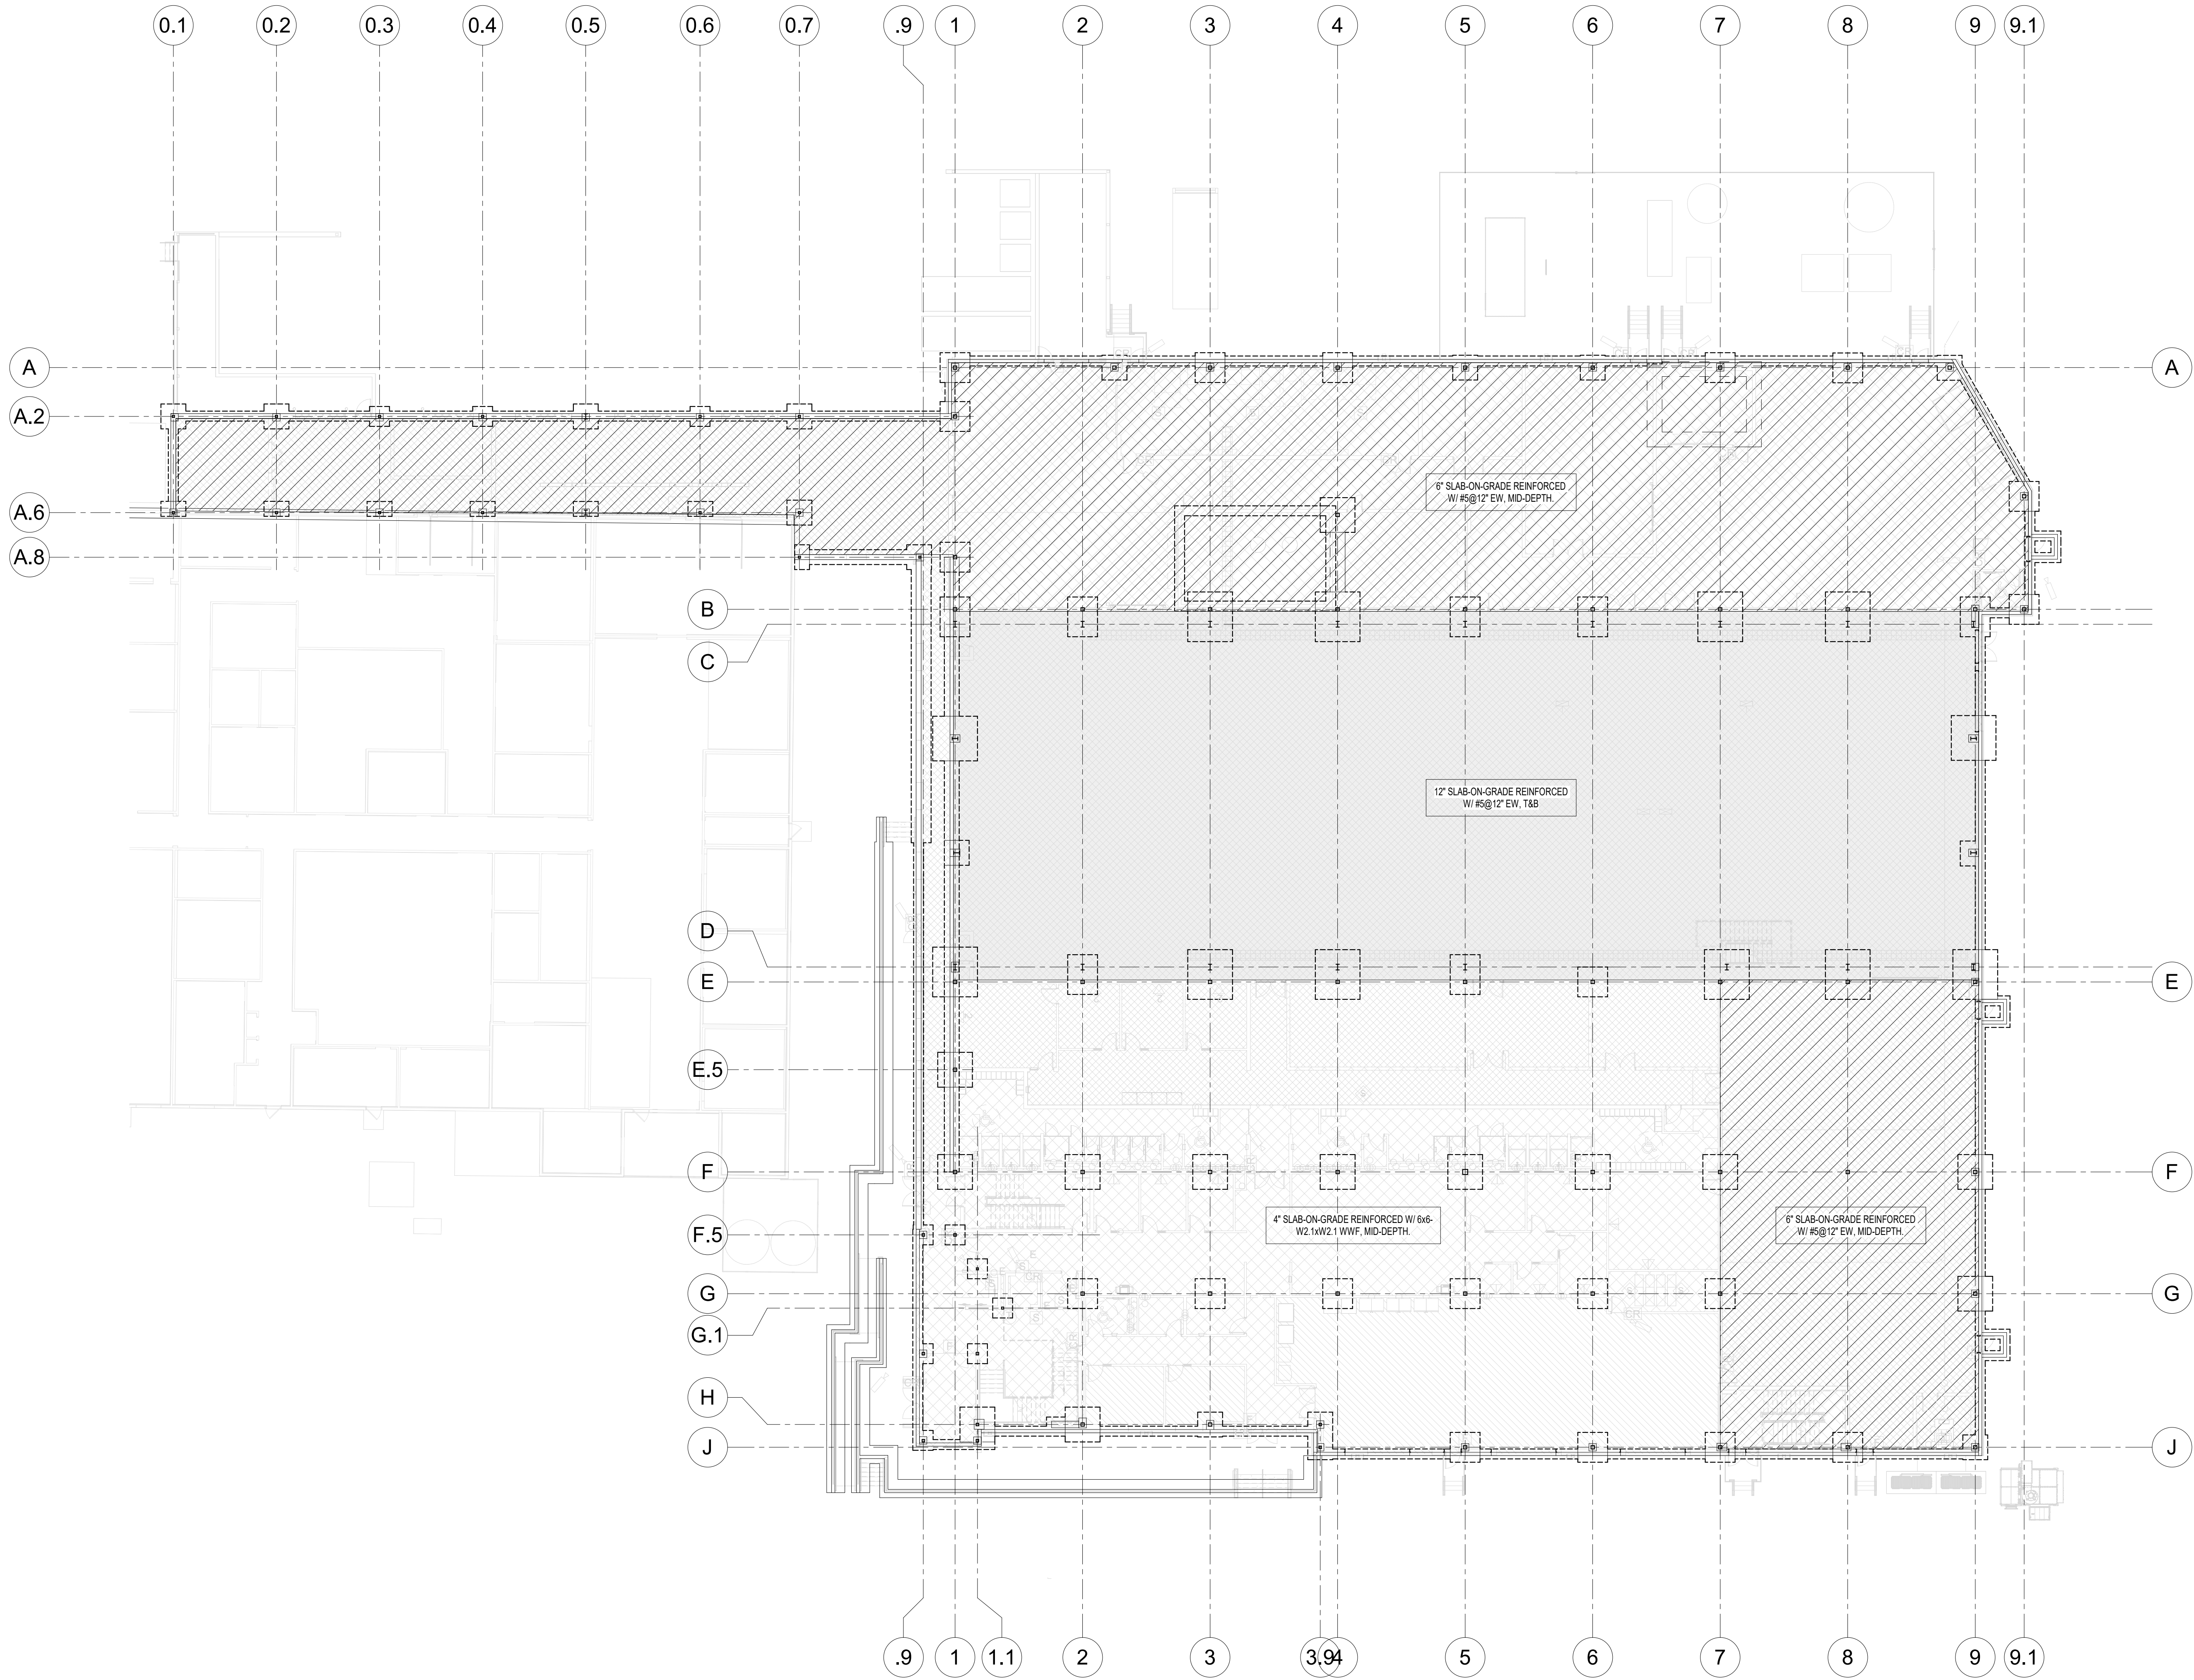

SLAB ON GRADE PLAN NOTES

1. FOR ADDITIONAL INFORMATION AND REQUIREMENTS, SEE FOUNDATION PLAN AND FOUNDATION PLAN NOTES.
2. PROVIDE (1)-#5 x 4'-0" LONG DIAGONAL IN CONCRETE SLABS AT ALL RE-ENTRY CORNERS AND (2)-#5 x 4'-0" LONG DIAGONAL EACH FACE AT VERTICAL STEPS IN FOUNDATION WALLS AND SITE WALLS.
3. FOR ALL SLAB DEPRESSION REQUIREMENTS AND LOCATIONS, SEE ARCHITECTURAL DRAWINGS.
4. CONTRACTOR TO SUBMIT SLAB CONSTRUCTION JOINT AND CONTROL JOINT LAYOUTS FOR APPROVAL IF PATTERN INDICATED ON DRAWINGS IS ALTERED.

1 SLAB-ON-GRADE PLAN
S-101 1/16" = 1'-0"