



CÉDULE DES PORTES					
Identifiant	Qté.	Porte 18 ja.	Vitrage		Remarques
		Dimensions	Largeur	Hauteur	
P1	1	3'-0" x 7'-0"	5"	1'-8"	CADRE POUR PORTE MONTANTE
P2	2	12'-0" x 14'-0"			

Quincaillerie standard du fournisseur:


- Charnière : Stanley FBM179 4.5" x 4"
- Barre panique : Von Duprin 22 x 689 avec poignée extérieure 230L
- Cylindre permanent : Schlage 20001C 626
- Ferme-porte : LCN 1261 689
- Coupe-froid de tête et des montants : Unique 1650
- Coupe-froid du bas : Unique DS4
- Seul : Voir la remarque dans la "Cédule de porte"

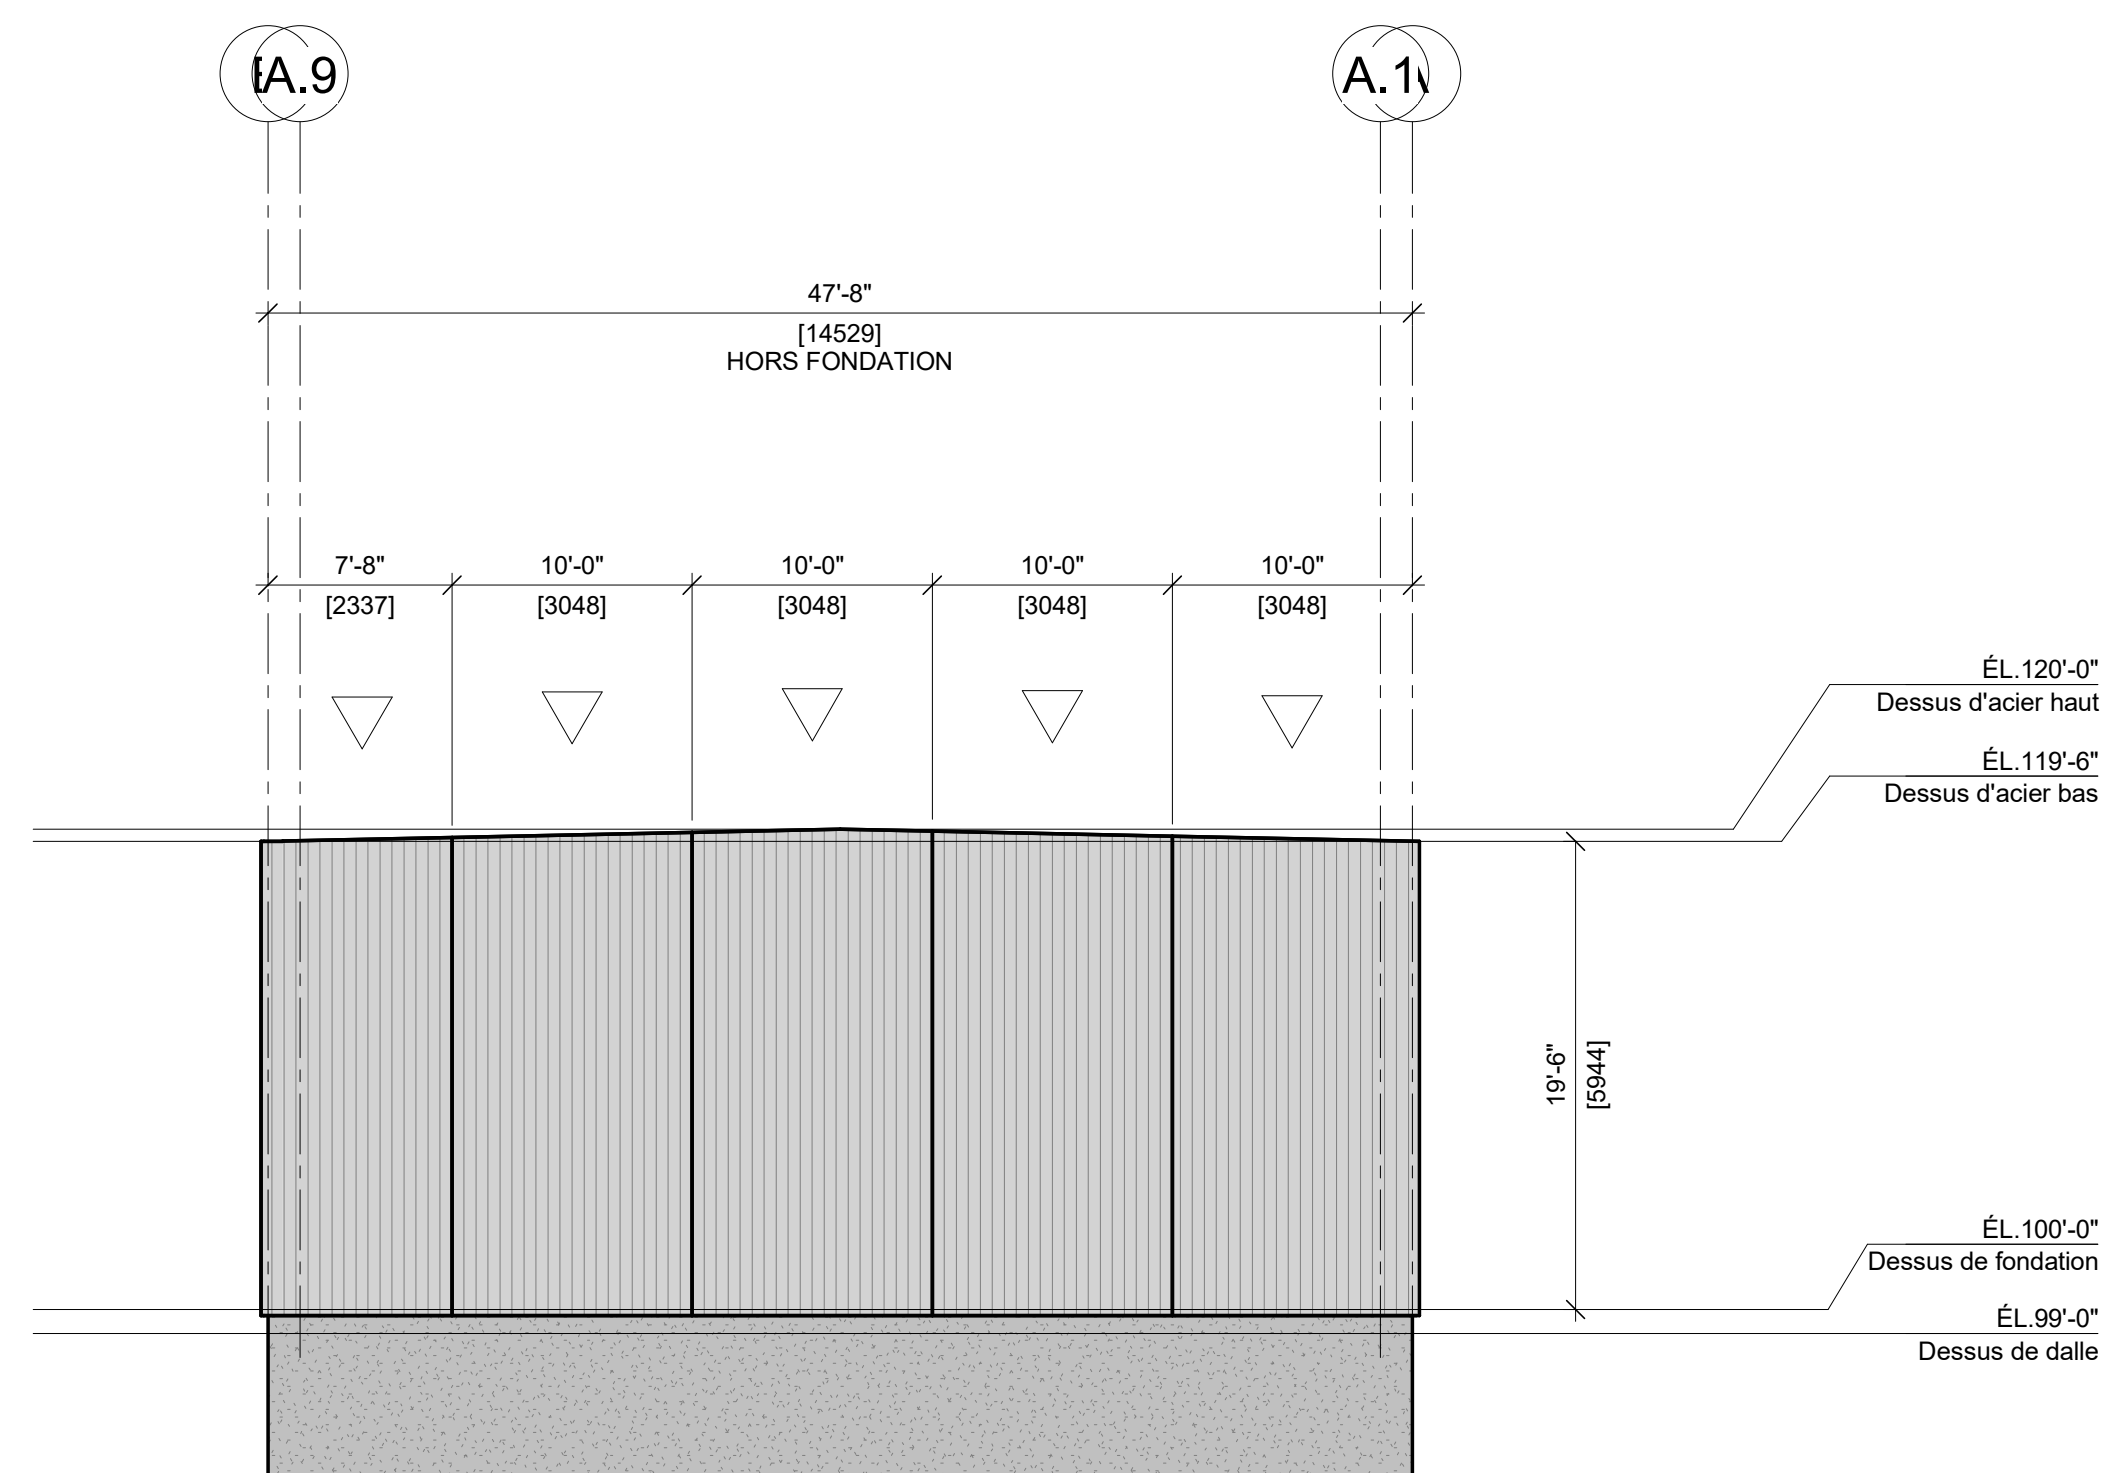


ÉLÉVATION AXE 1 (OUEST)
1/8" = 1'-0"

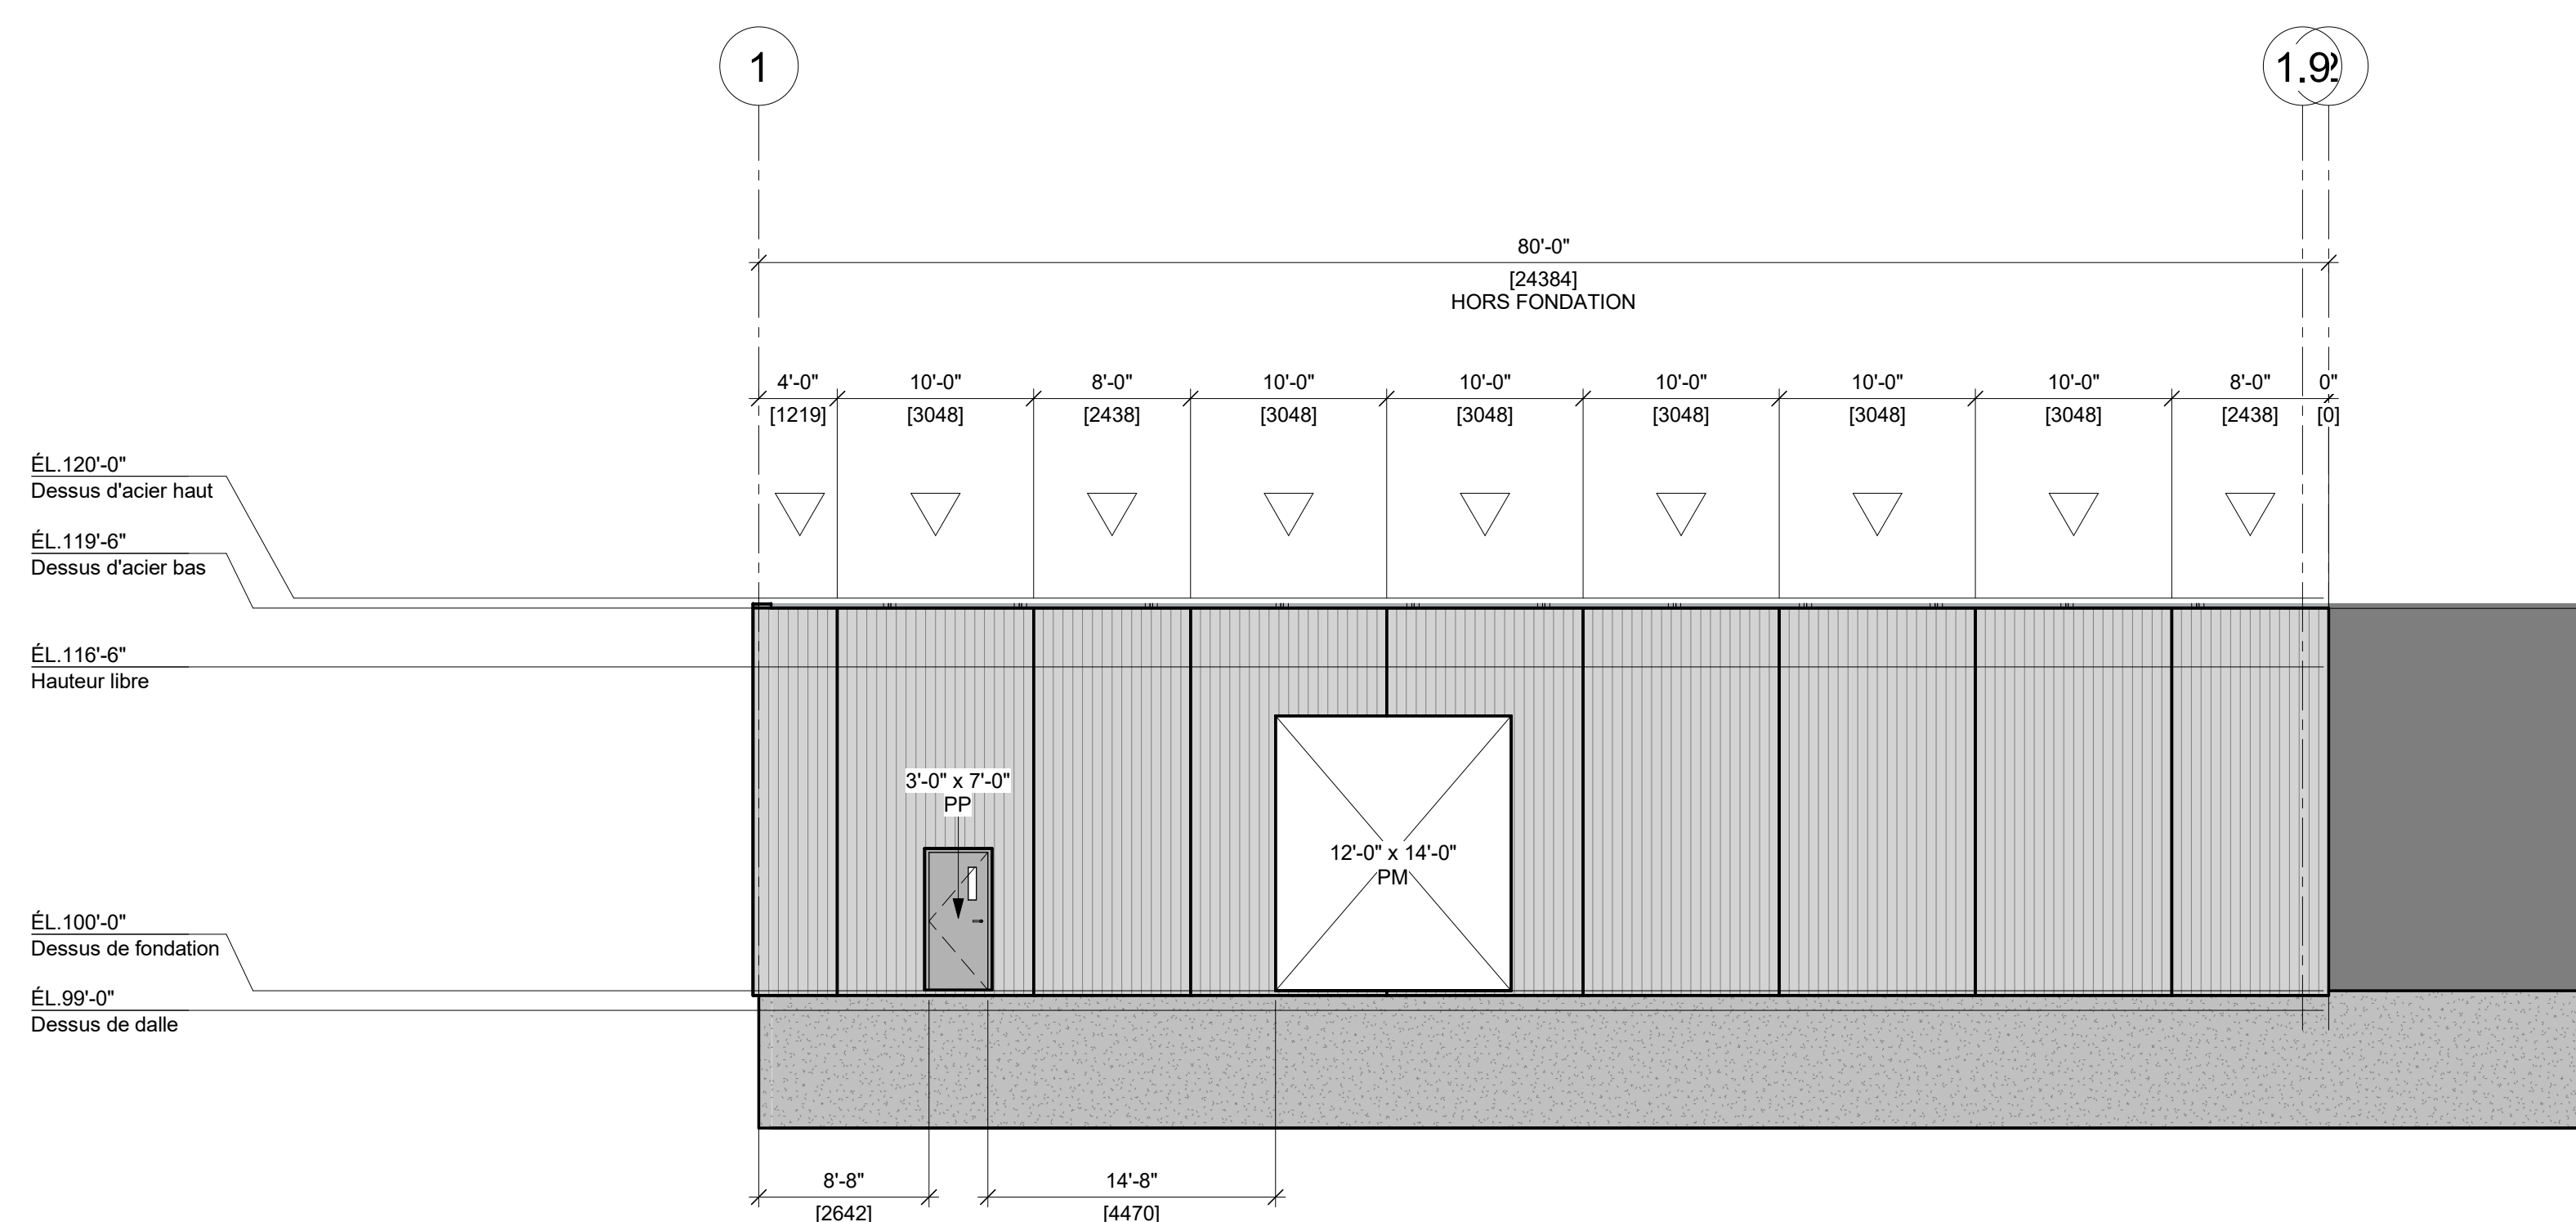



ÉLÉVATION AXE A (SUD)
1/8" = 1'-0"

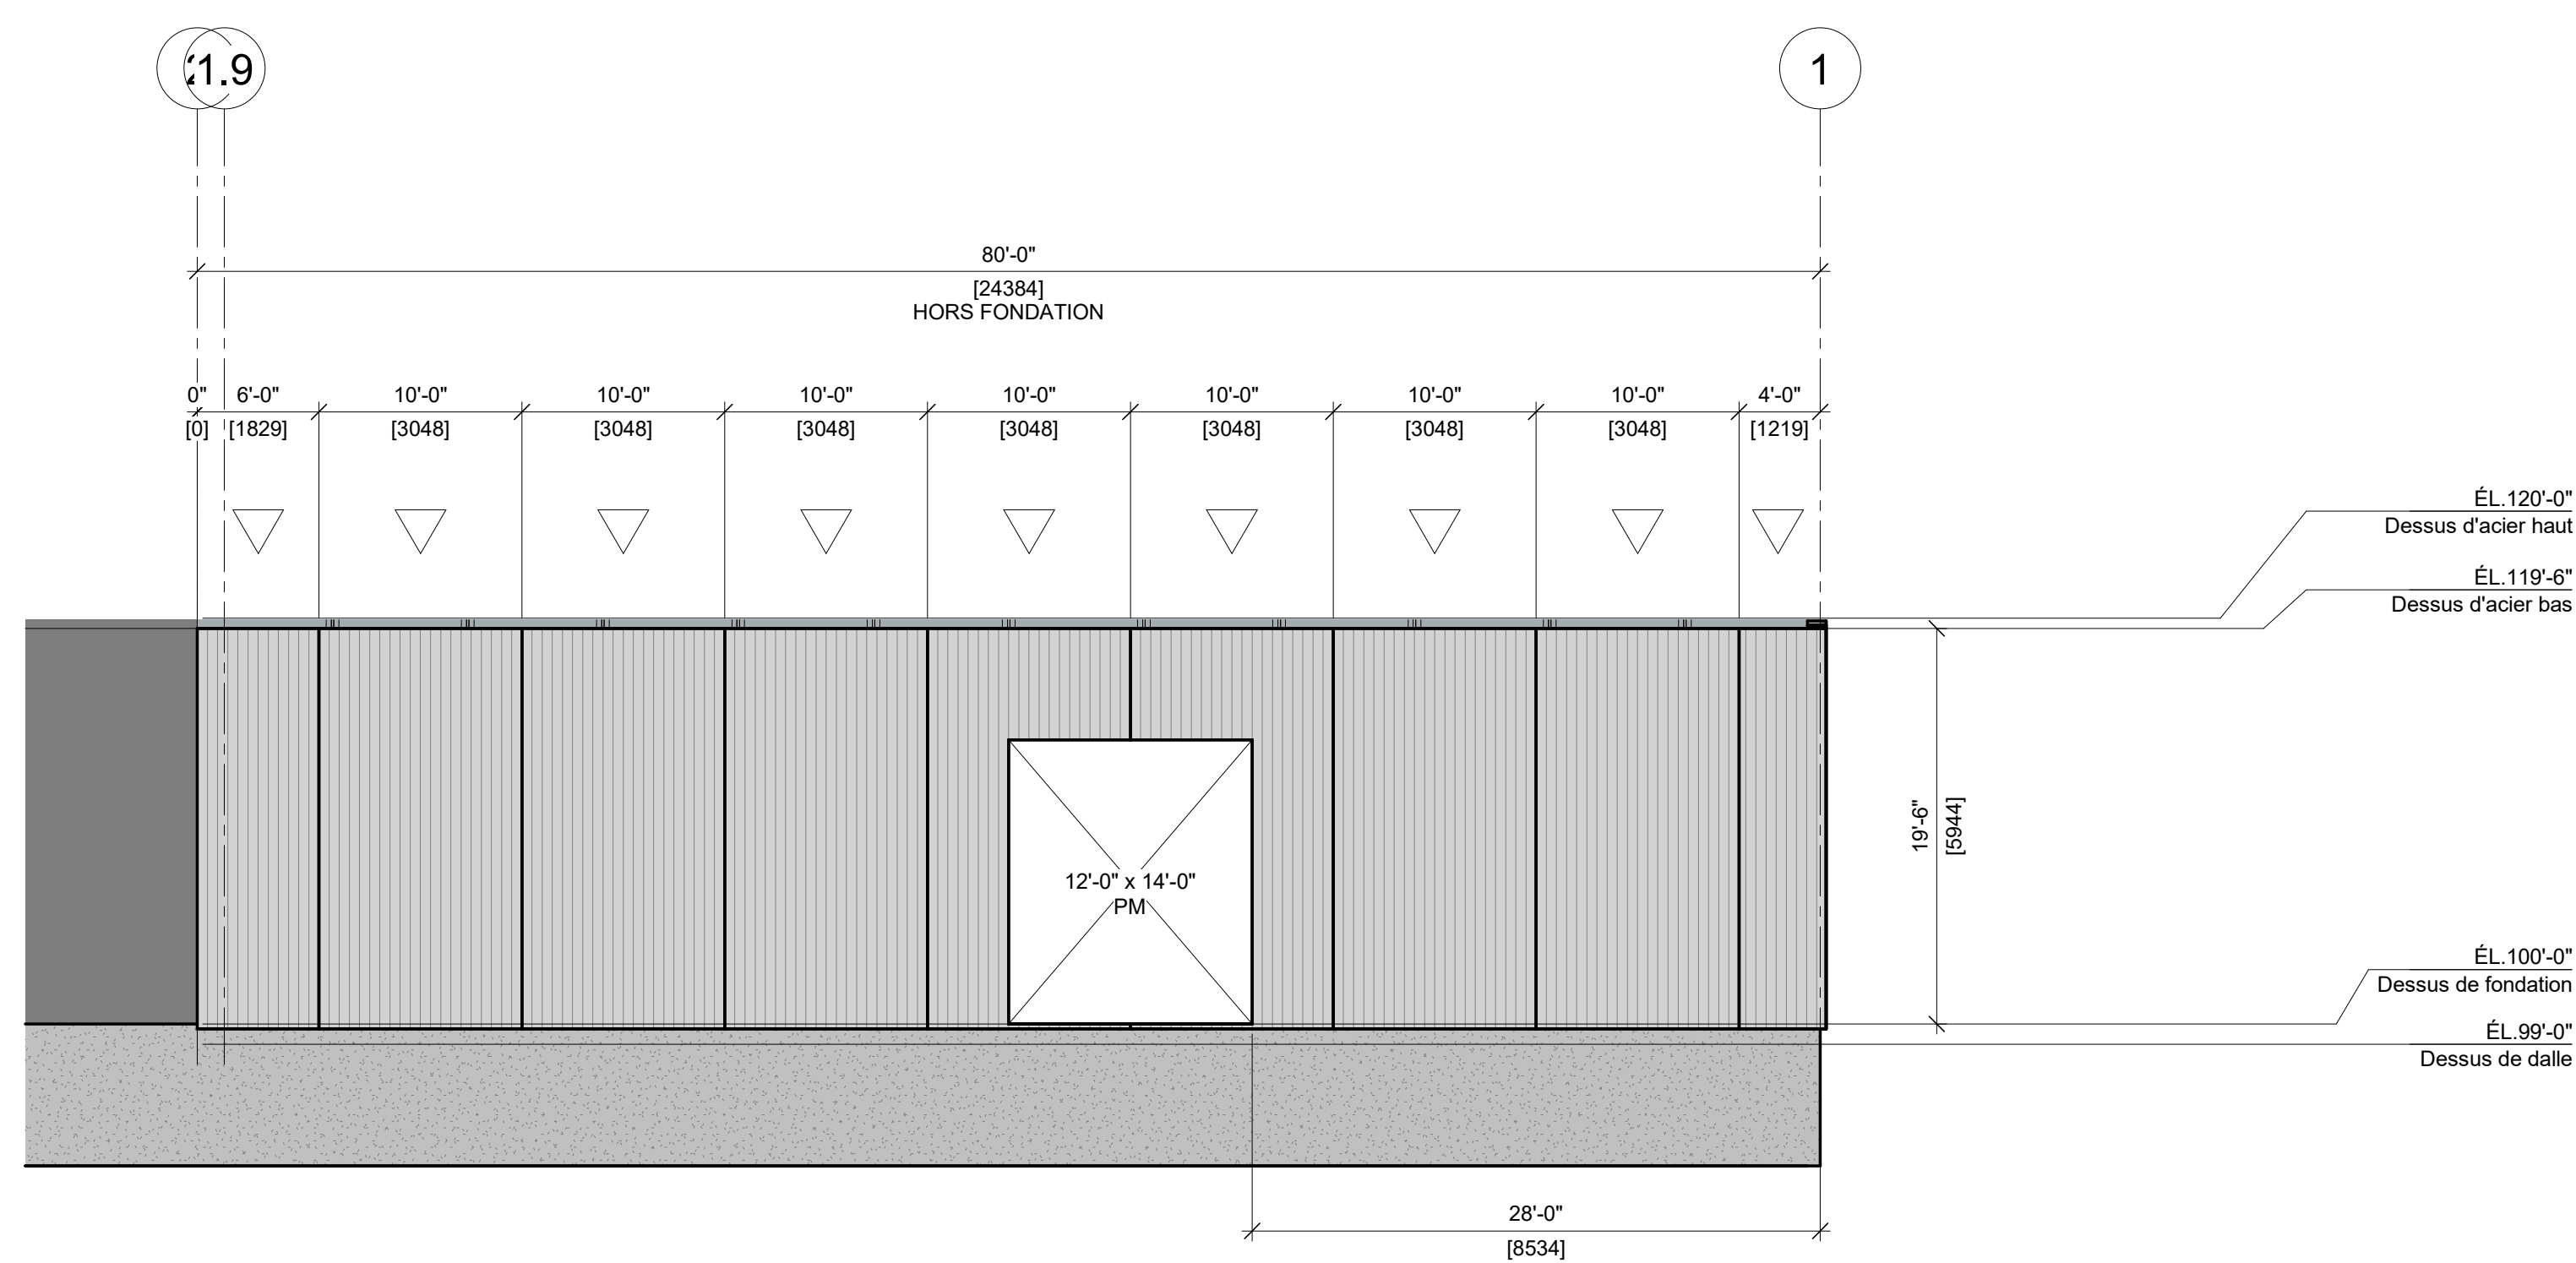

ÉLÉVATION AXE B (NORD)
1/8" = 1'-0"

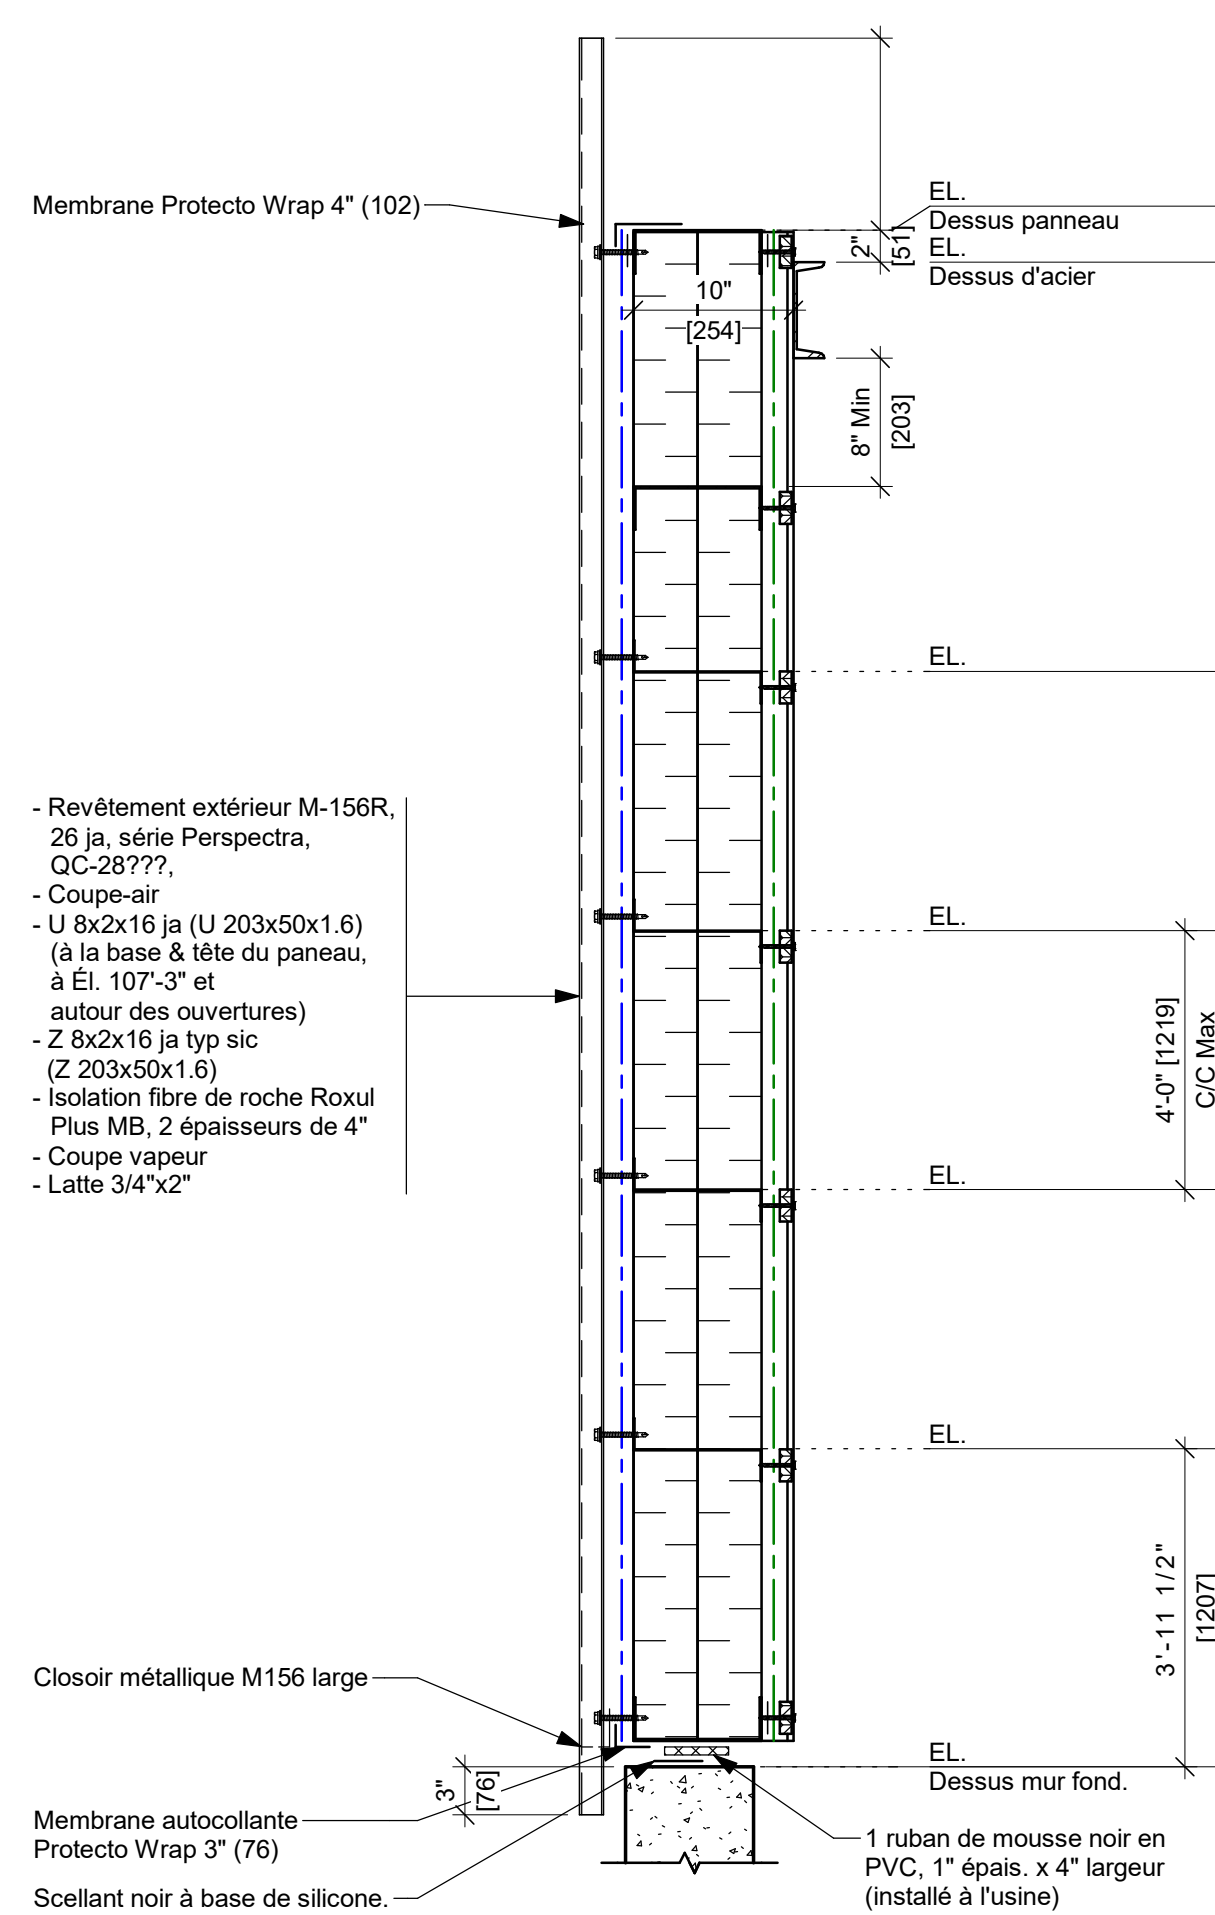

COUPE DE MUR PROPOSÉE
1" = 1'-0"

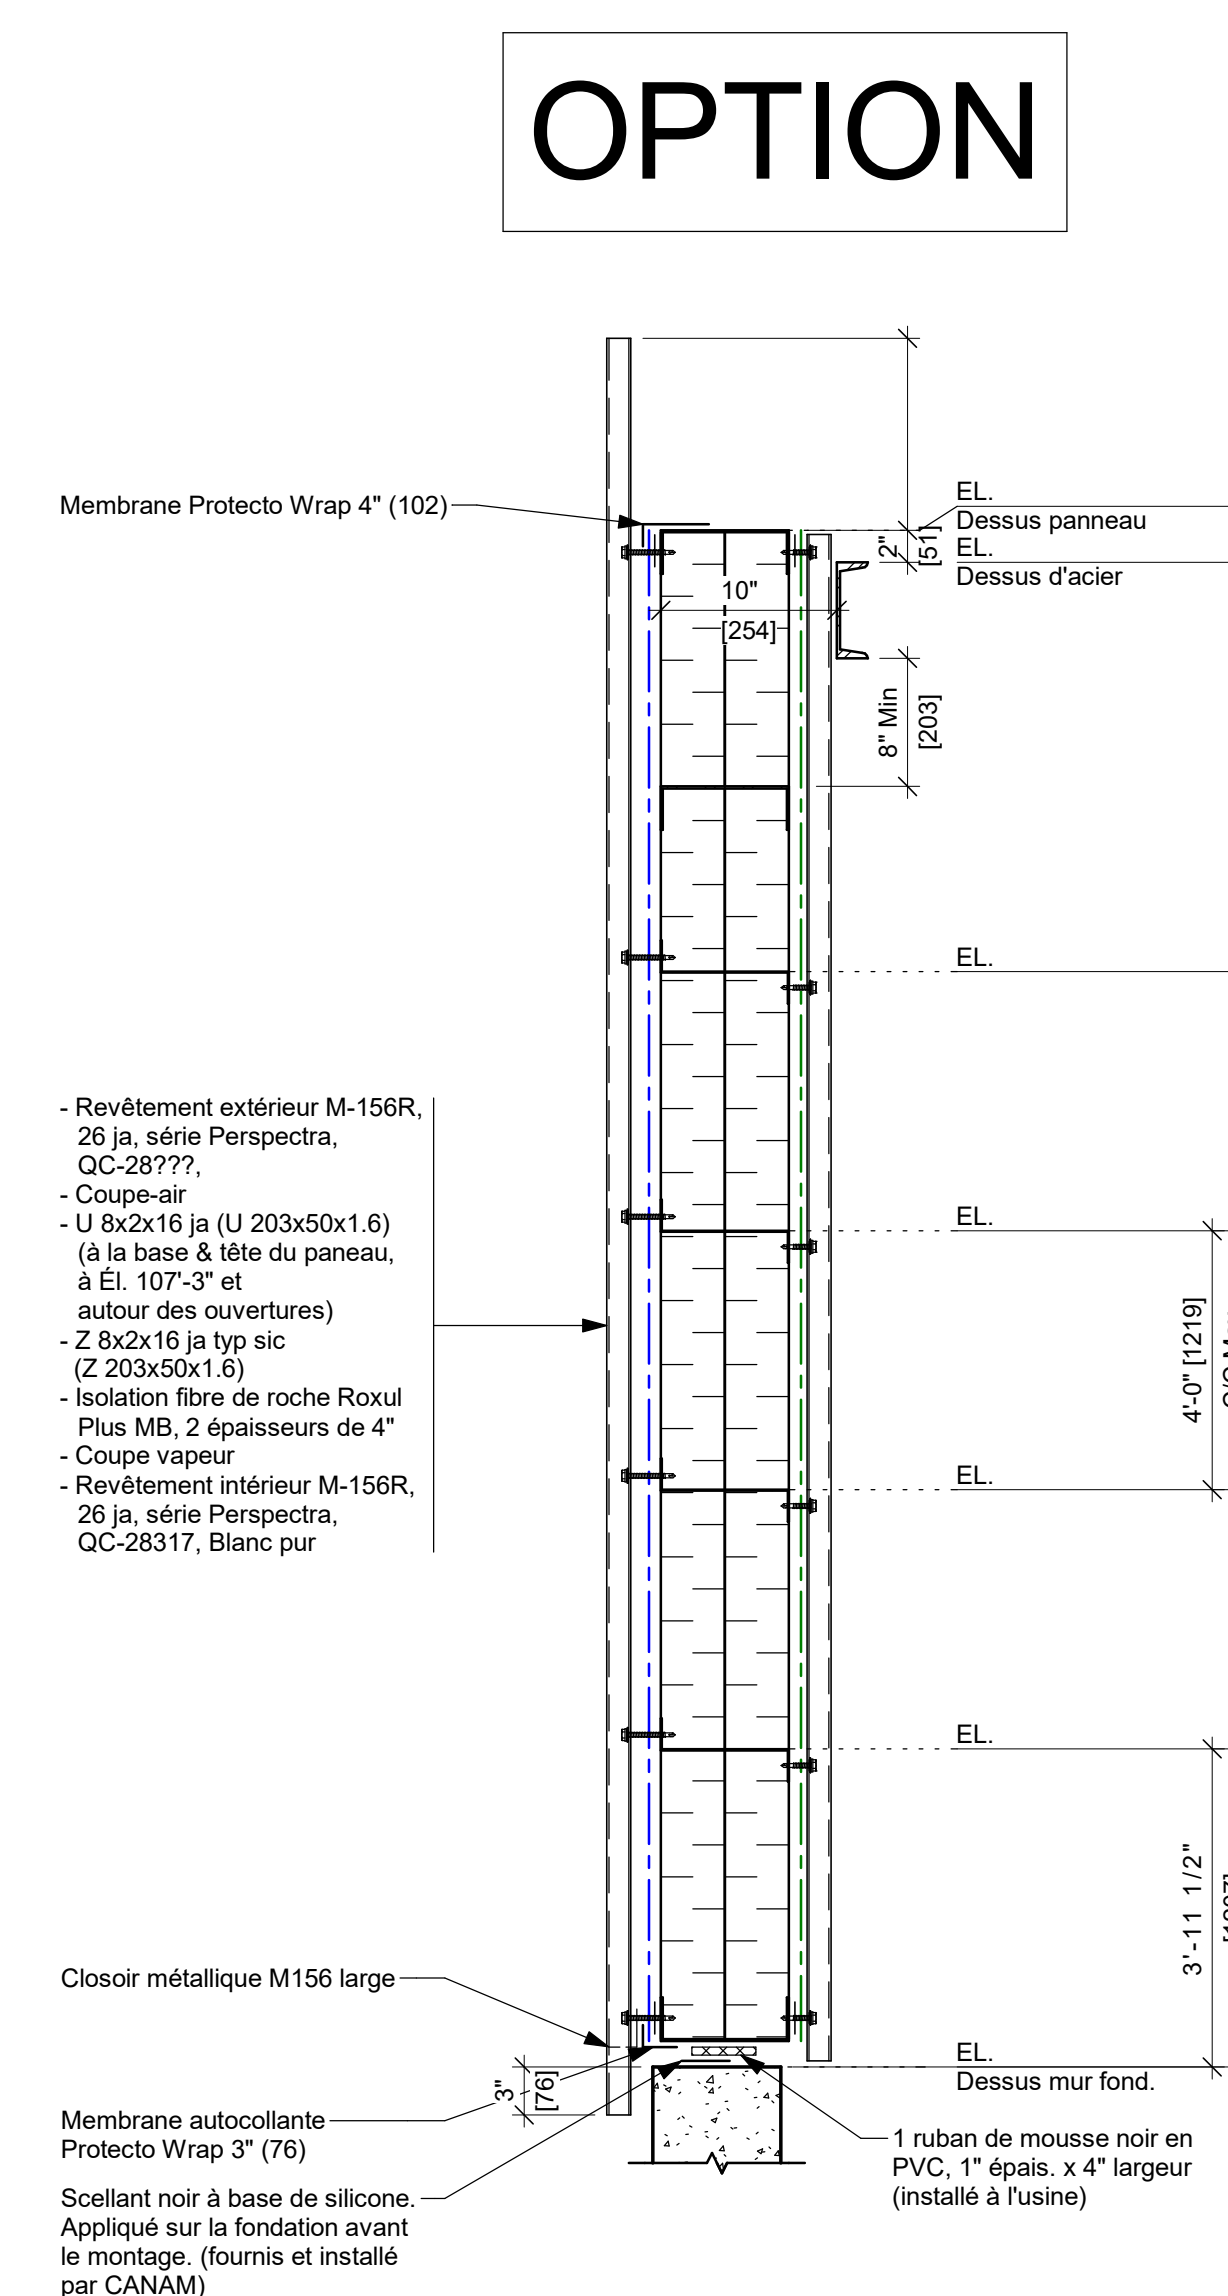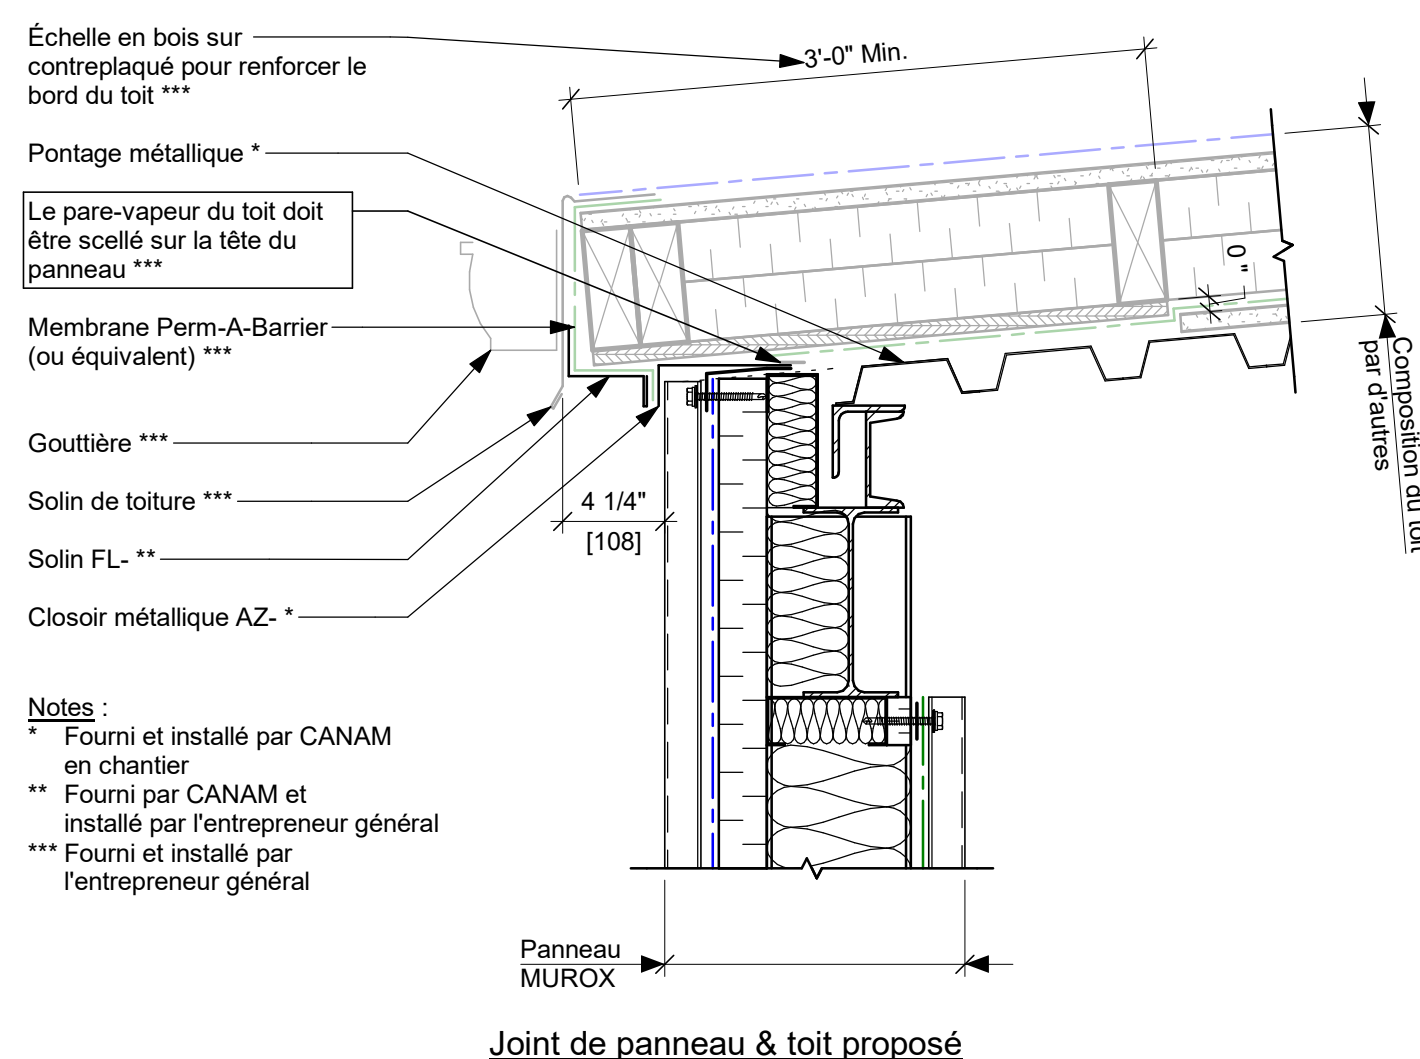

COUPE DE MUR EN OPTION
1" = 1'-0"

NOTE POUR LE CONTRACTEUR/ÉRECTEUR:

■ EST STRICTEMENT DÉFENDU DE MODIFIER, COPIER, REPRODUIRE OU DE DISTRIBUER CES DESSINS OU QUELQUES REPRÉSENTATIONS DE CES DESSINS, PAR TOUTES SOURCES DE MÉDIA INCLUANT ÉLECTRONIQUEMENT, SANS L'APPROBATION ÉCRITE DE GROUPE CANAM INC.

PRÉLIMINAIRE

NE DOIT PAS SERVIR À LA
CONSTRUCTION

RÉVISION	DATE	DESCRIPTION	DESS.	VÉR.
CÉDANT DE PROJET				

GEOMETRIE DER PUNKTE	-
	-
	-
	-
	-

DESSIN :			
DESSINÉ PAR SL	CONÇU PAR	INGÉNIEUR DU PROJET	ECHELLE: Comme indiqué
VÉRIFIÉ PAR	INGÉNIEURS CONSEILS / ARCHITECTES		DATE (jj/mm/aaaa) : 12/06/2026

CLIENT: MOREAU INDUSTRIES



11505, 1re Avenue, bureau 500, Saint-Georges Beauce
Québec, Canada, G5Y 7X3
Téléphone : (418) 228-8031
Sans frais : (877) 499-6049
www.canam.com

SCAU PROFESSIONNEL

BÂTIMENT VENTILATEUR
VAL-D'OR, QUÉBEC

CROQUIS PRÉLIMINAIRE -
ÉLÉVATION, COUPE DE MUR ET
CÉDULES

NUMERO CONTRAT P2026-120	NUMERO DESIGN EsMx502	DIVISION	REVISION 
-----------------------------	--------------------------	----------	---