



CÉDULE DES PORTES					
Identifiant	Qté	Porte 18 ja.	Dimensions	Vitrage	Remarques
P1	1	3'-0" x 7'-0"	2"	1'-6"	
P2	2	12'-0" x 14'-0"			CADRE POUR PORTE MONTANTE


Quincaillerie standard du fournisseur:
- Charnières : Stanley P380 19 4 5" x 4"
- Barre panique : Von Duprin 22 x 680 avec poignée extérieure 230L
- Cylindre permanent : Schlage 20001C 626
- Ferme-porte : LCN 1261 669
- Coupe-froid de lête et des montants : Unique 1650
- Coupe-froid du bas : Unique D54
- Seuil : Voir la remarque dans la "Cédule de porte"

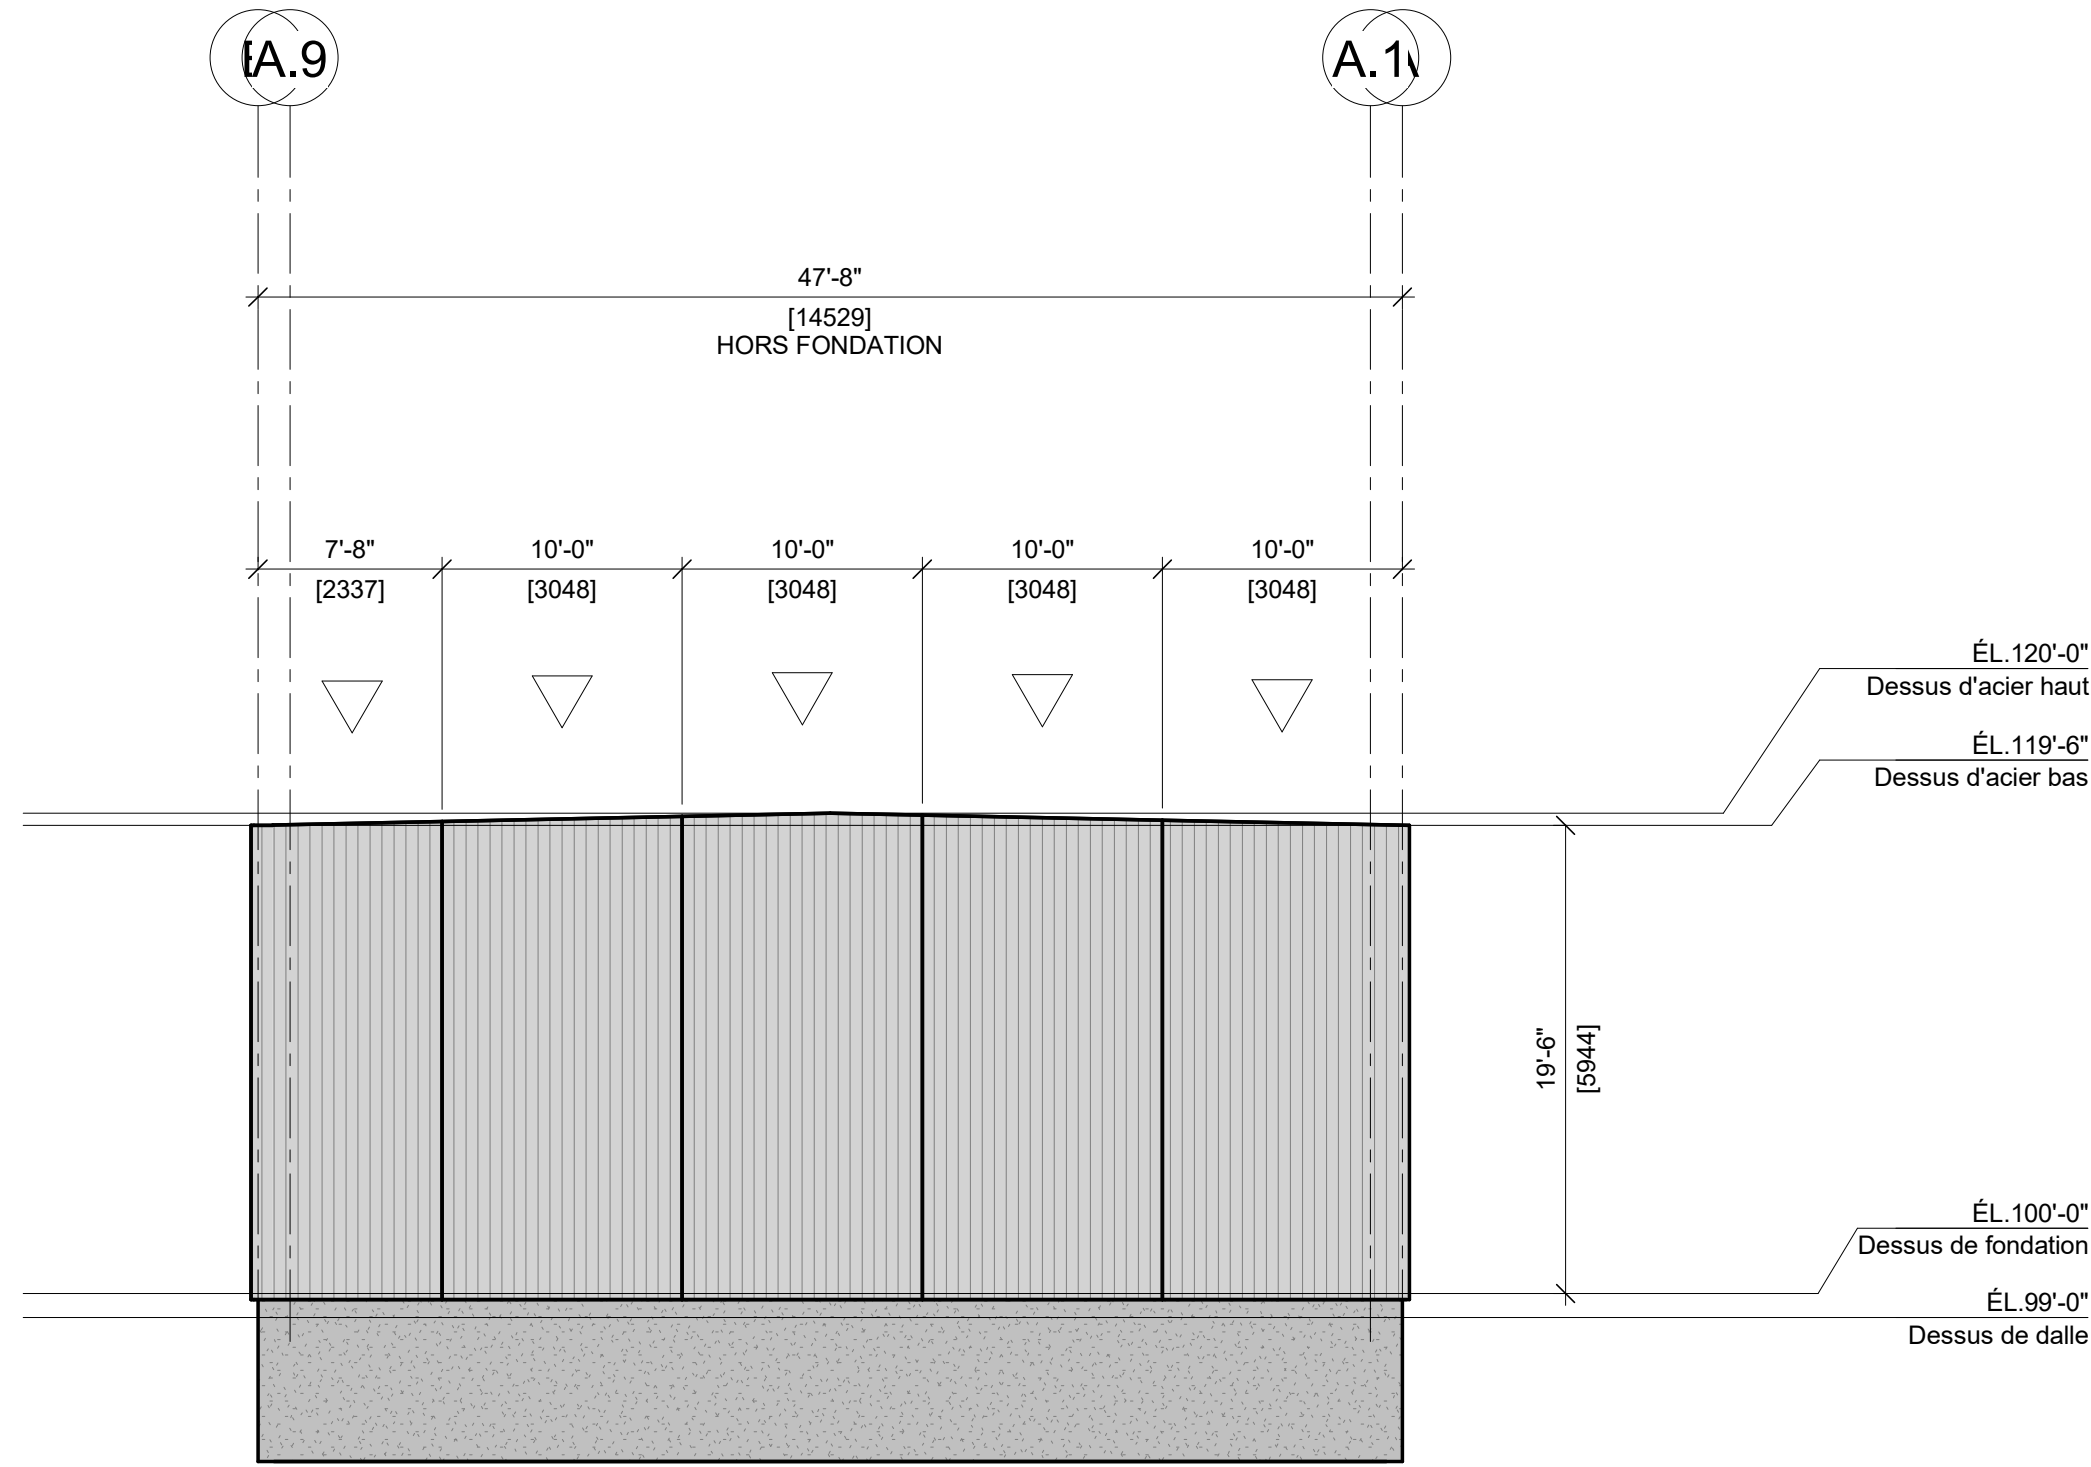


ÉLÉVATION AXE 1 (OUEST)
1/8" = 1'-0"

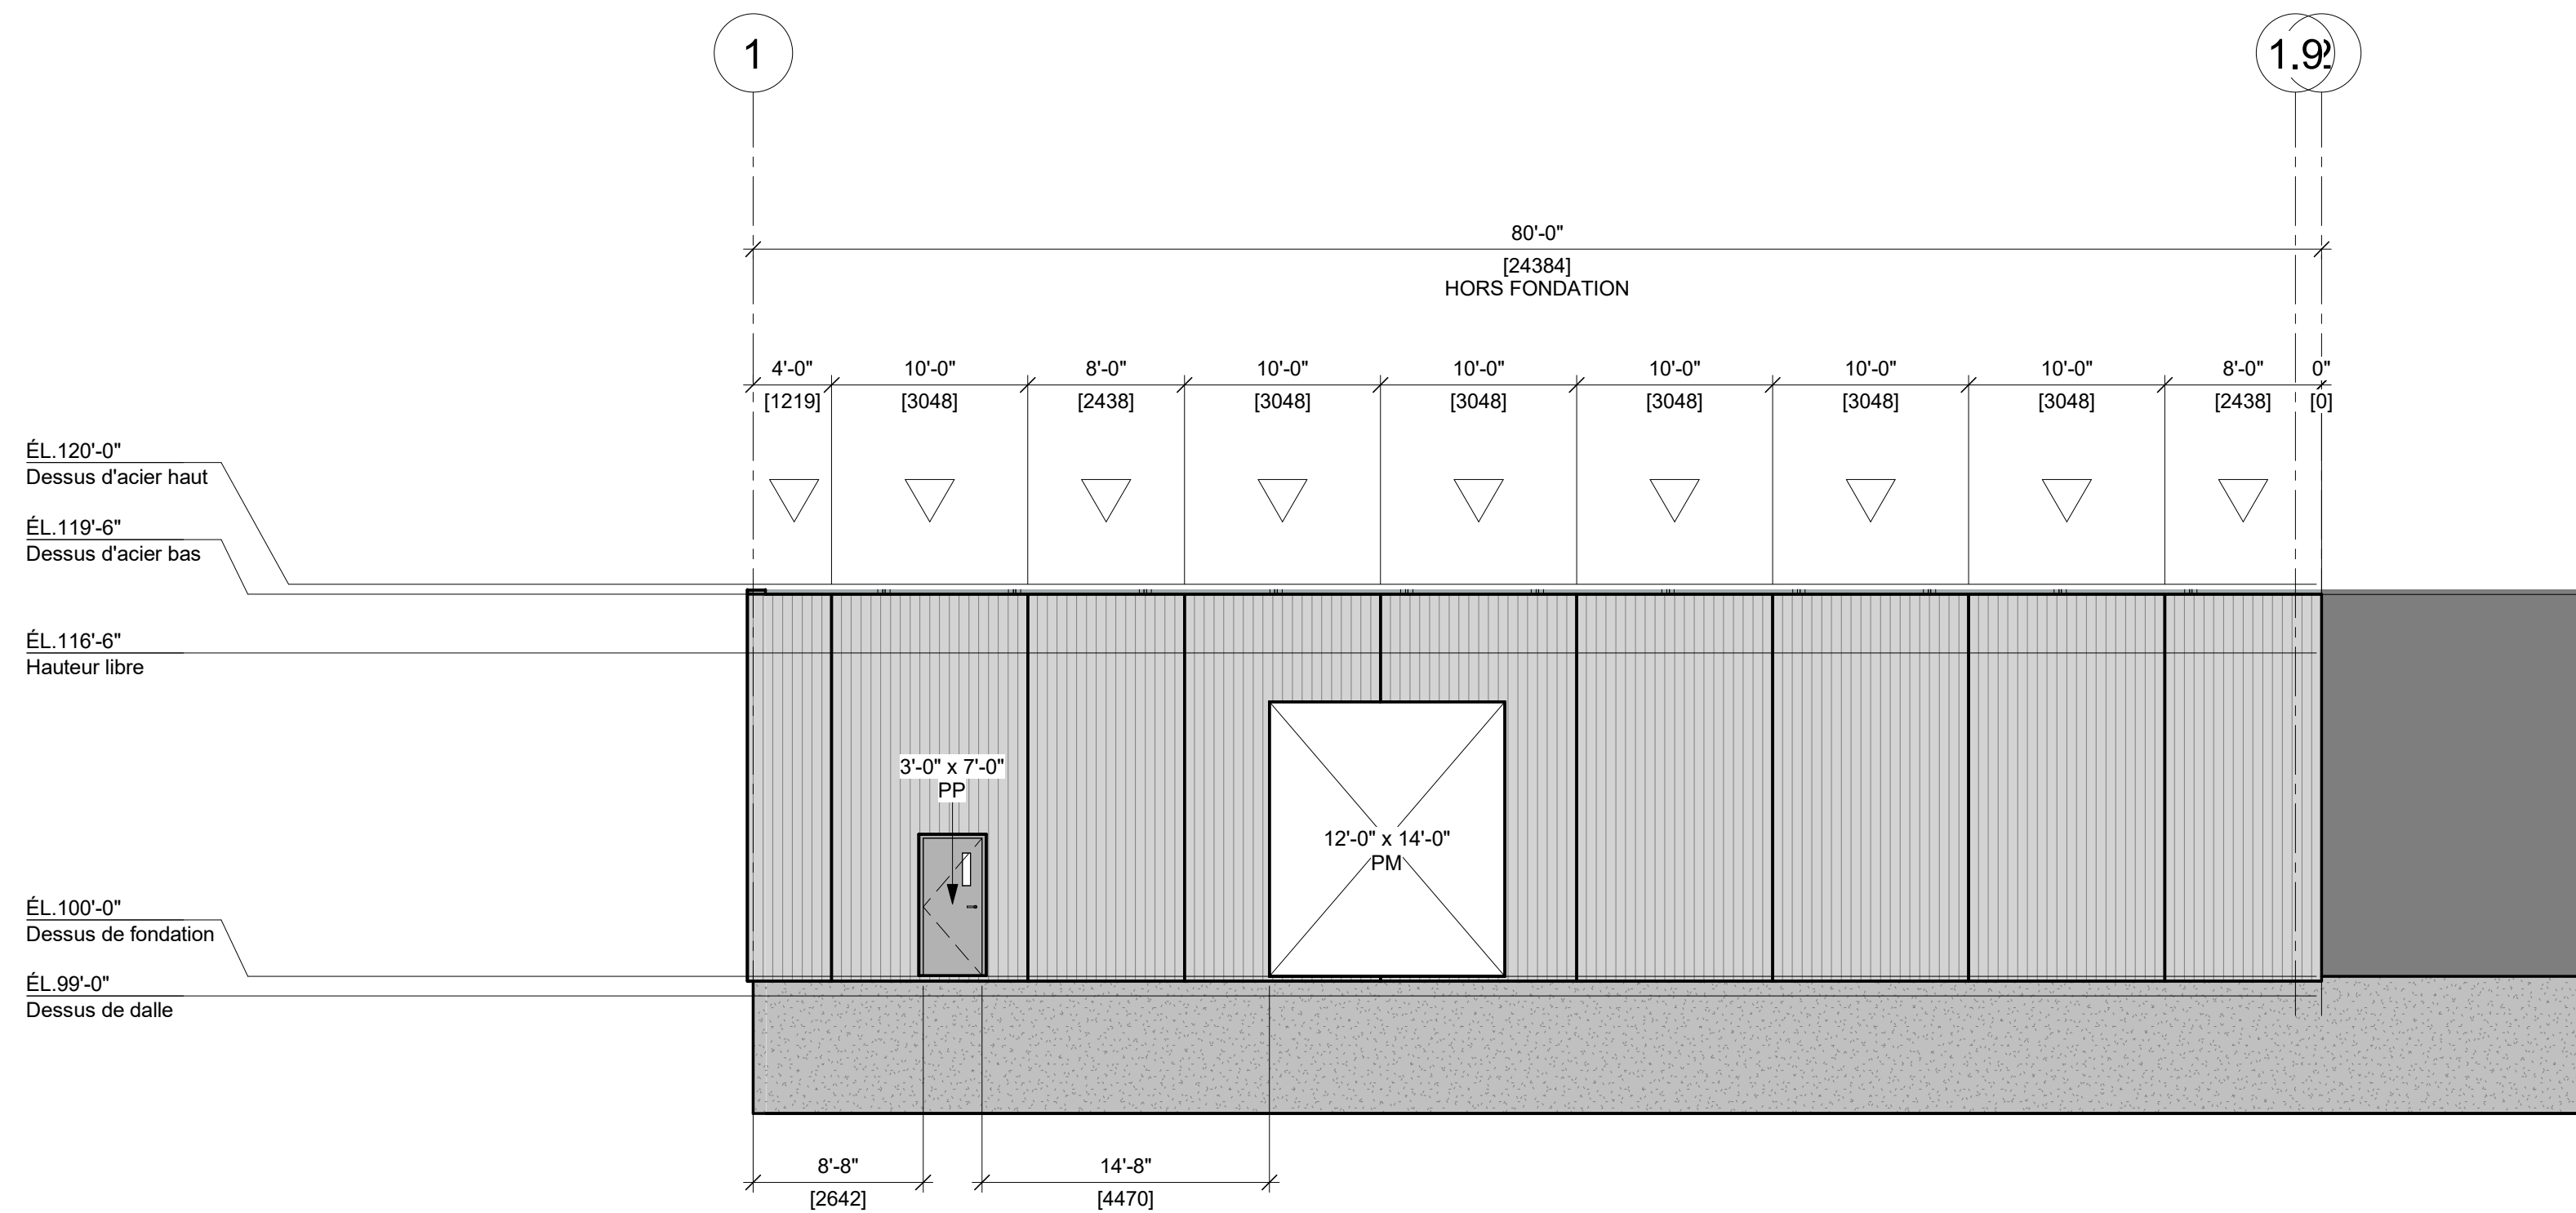


ÉLÉVATION AXE A (SUD)
1/8" = 1'-0"

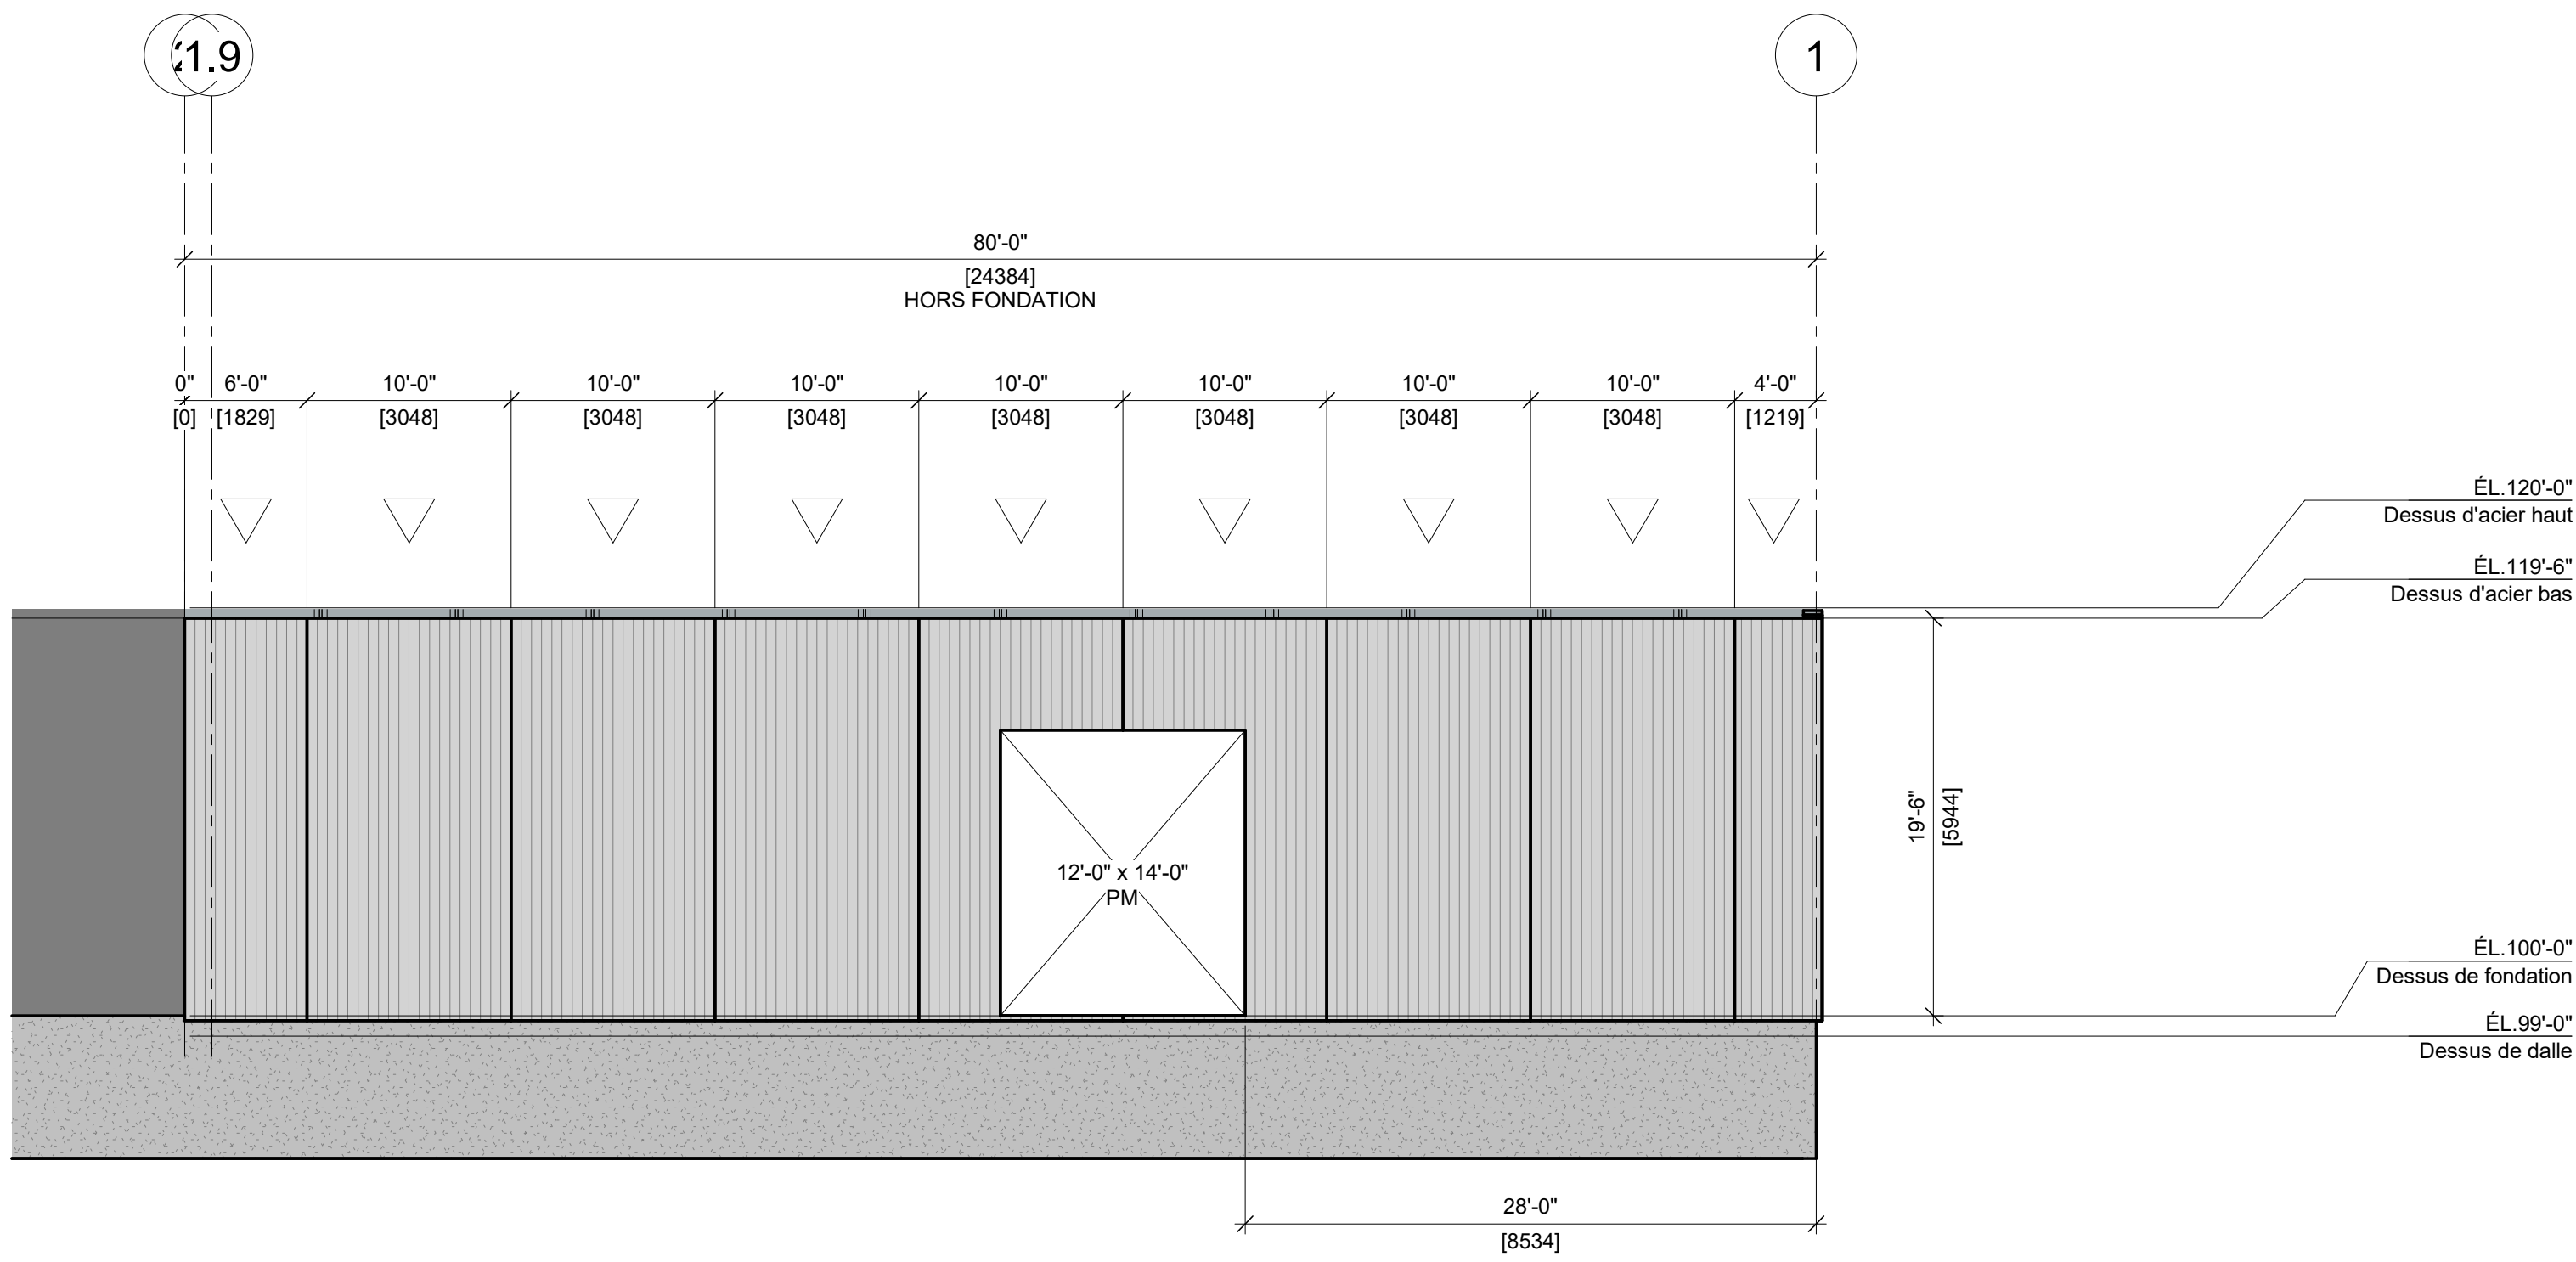


ÉLÉVATION AXE B (NORD)
1/8" = 1'-0"

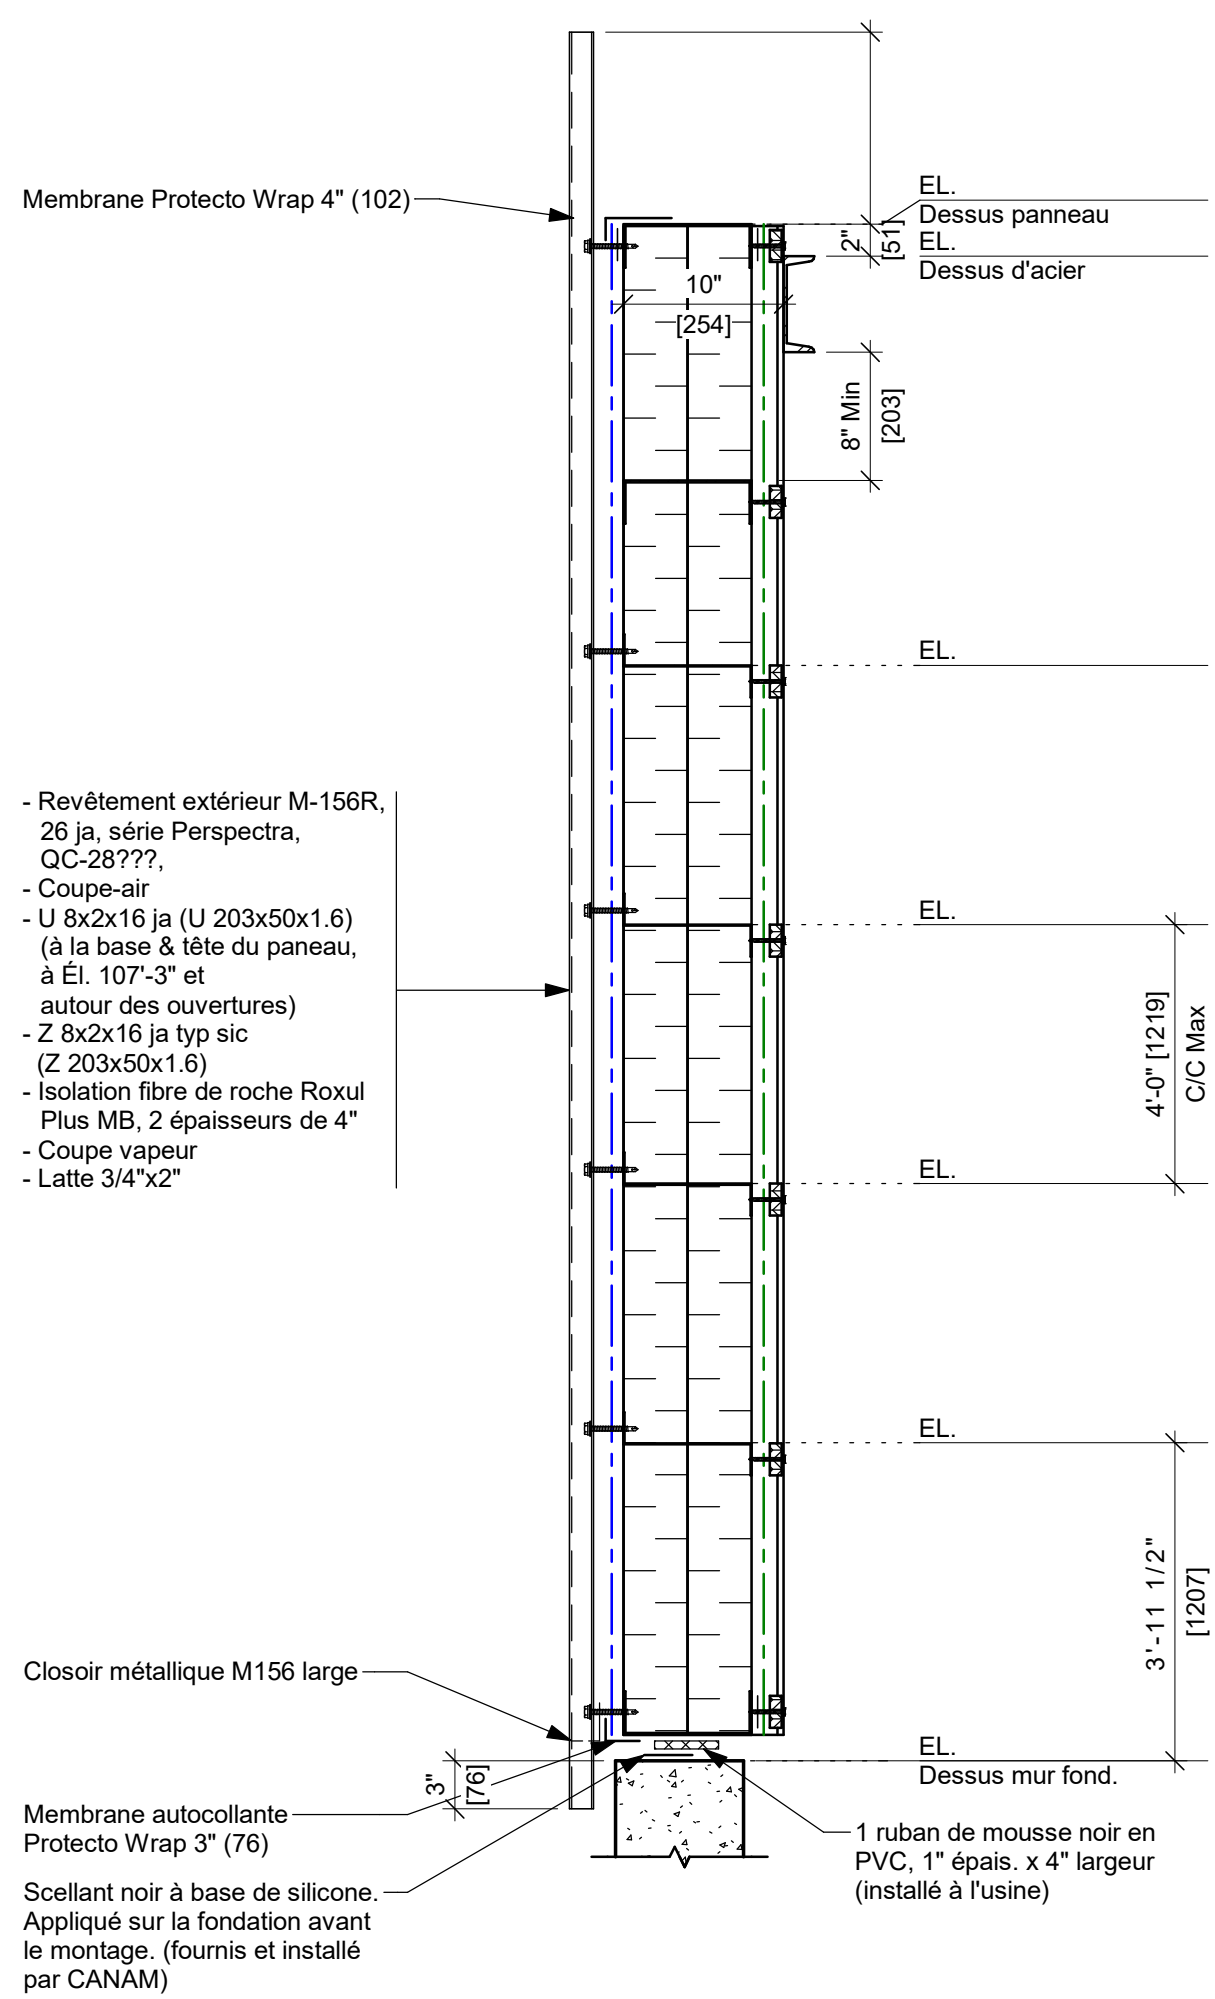

COUPE DE MUR PROPOSÉE
1" = 1'-0"

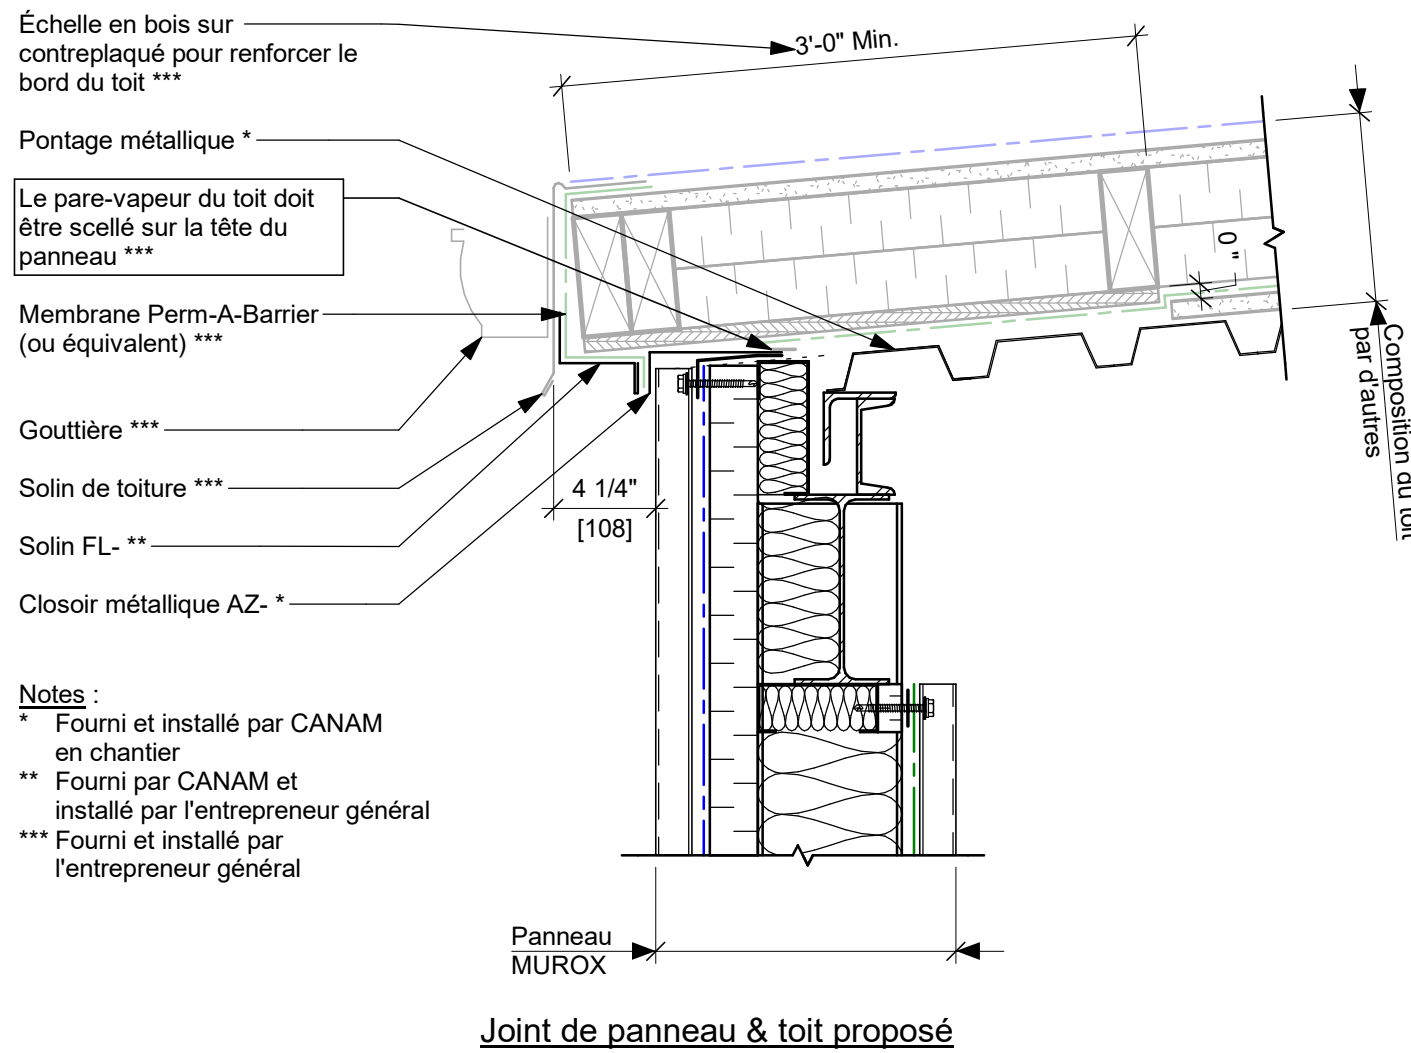


OPTION

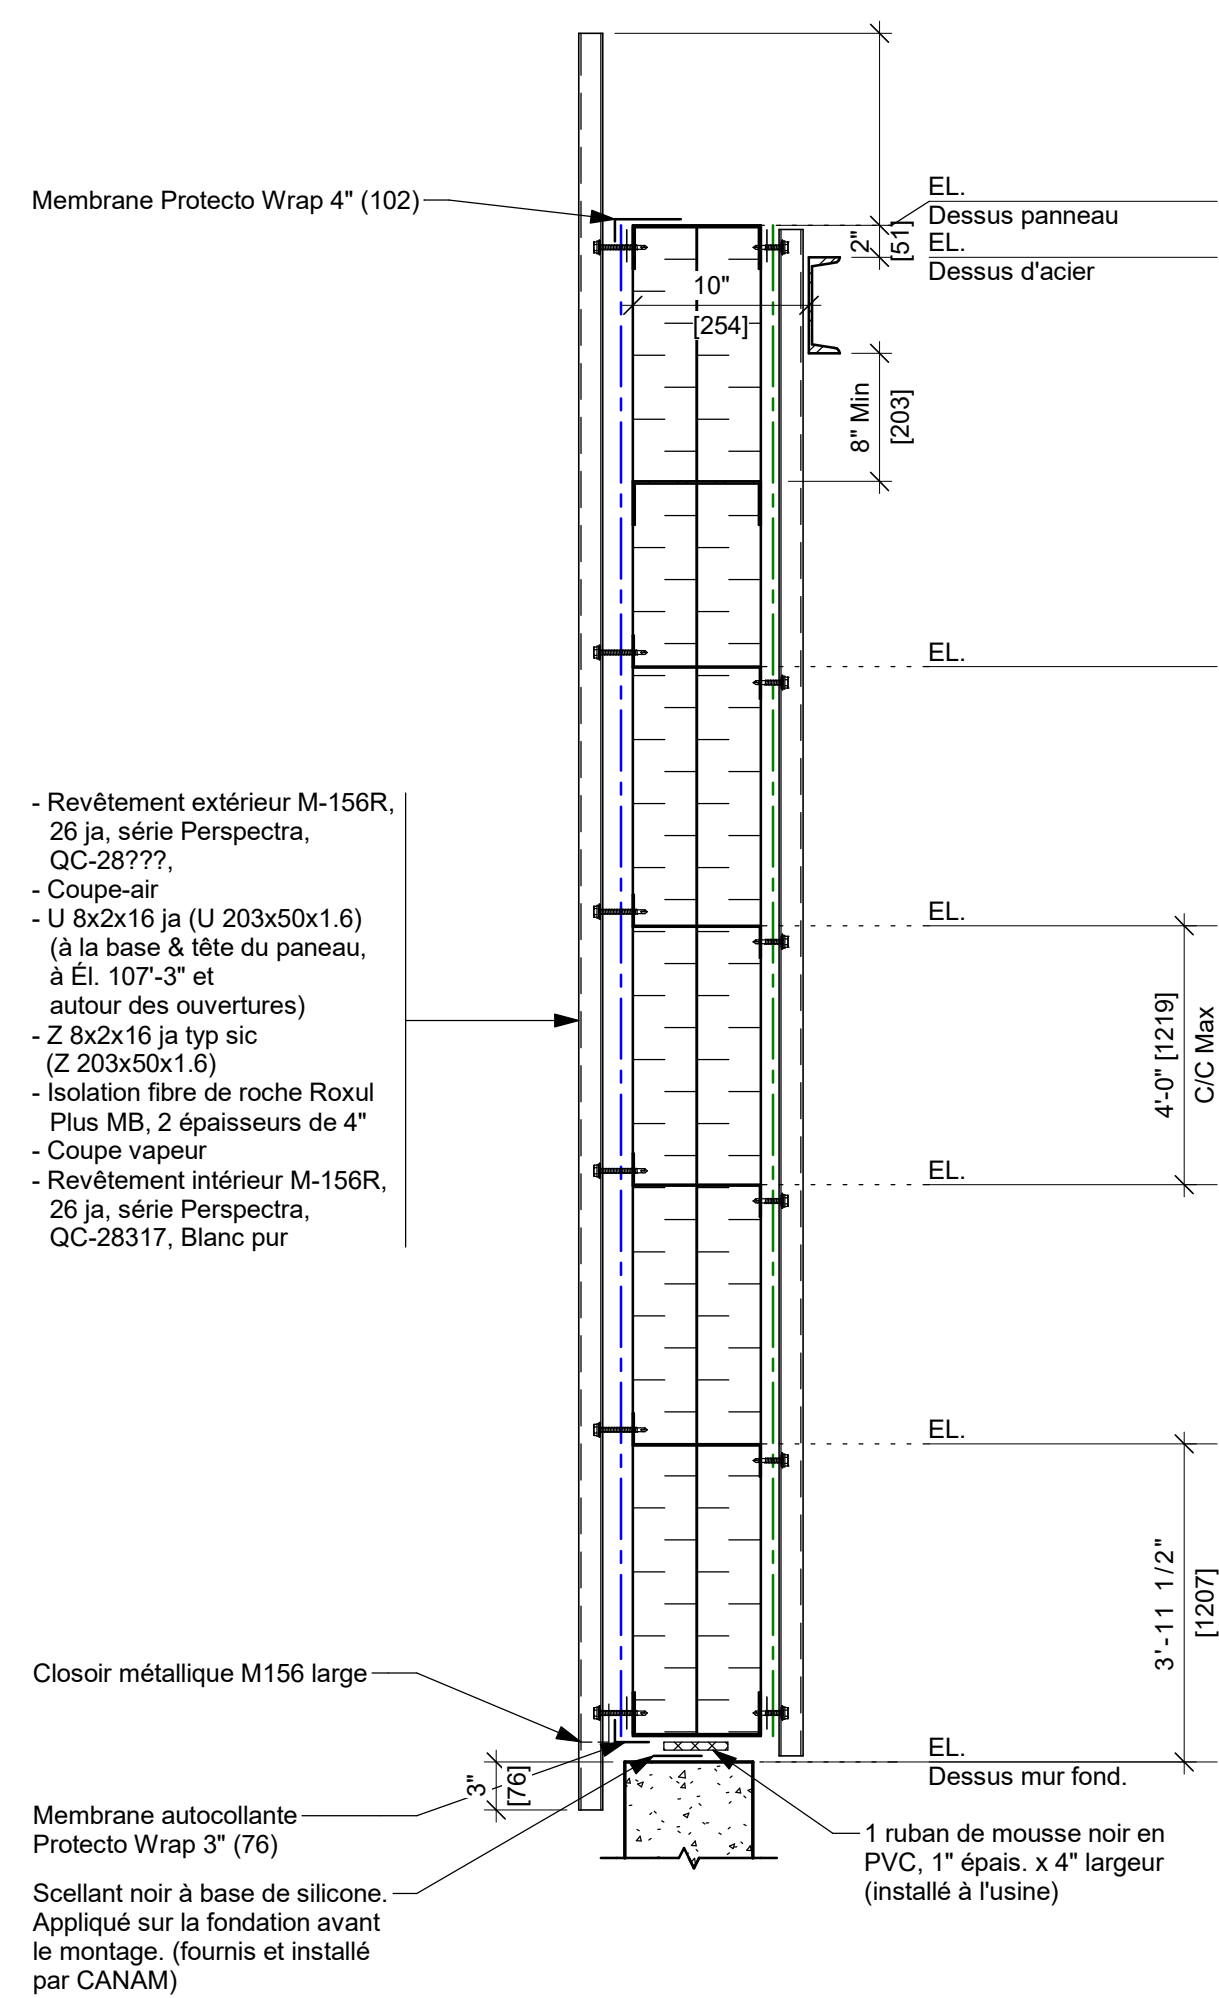

COUPE DE MUR EN OPTION
1" = 1'-0"

PRÉLIMINAIRE

NE DOIT PAS SERVIR À LA CONSTRUCTION

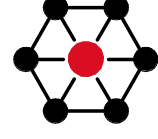REVISION	DATE	DESCRIPTION	DESS	VER
GERANT DE PROJET				
		-		
		-		
		-		
		-		
DESSIN				
DESSINÉ PAR	CONÇU PAR	INGÉNIEUR DU PROJET	ÉCHELLE:	
SL			Comme indiqué	
VERIFIÉ PAR	INGÉNIEURS CONSEILS / ARCHITECTES		DATE (mm/aaaa)	
			12/06/2026	
CLIENT: MOREAU INDUSTRIES				
 CANAM 11505, 1^{re} Avenue, bureau 500, Saint-Georges Beauce Québec, Canada, G5Y 7G5 Téléphone : (418) 228-8031 Sans frais : (877) 459-8049 www.canamf.com				
SCAUX PROFESSIONNEL				
PROJET				
BÂTIMENT VENTILATEUR VAL-D'OR, QUÉBEC				
TITRE				
CROQUIS PRÉLIMINAIRE - ÉLÉVATION, COUPE DE MUR ET CÉDULES				
NUMERO CONTRAT	NUMERO DESSIN	DIVISION	REVISION	
P2026-120	EsMx502			
				