





NORD POUR
L'ÉRECTION

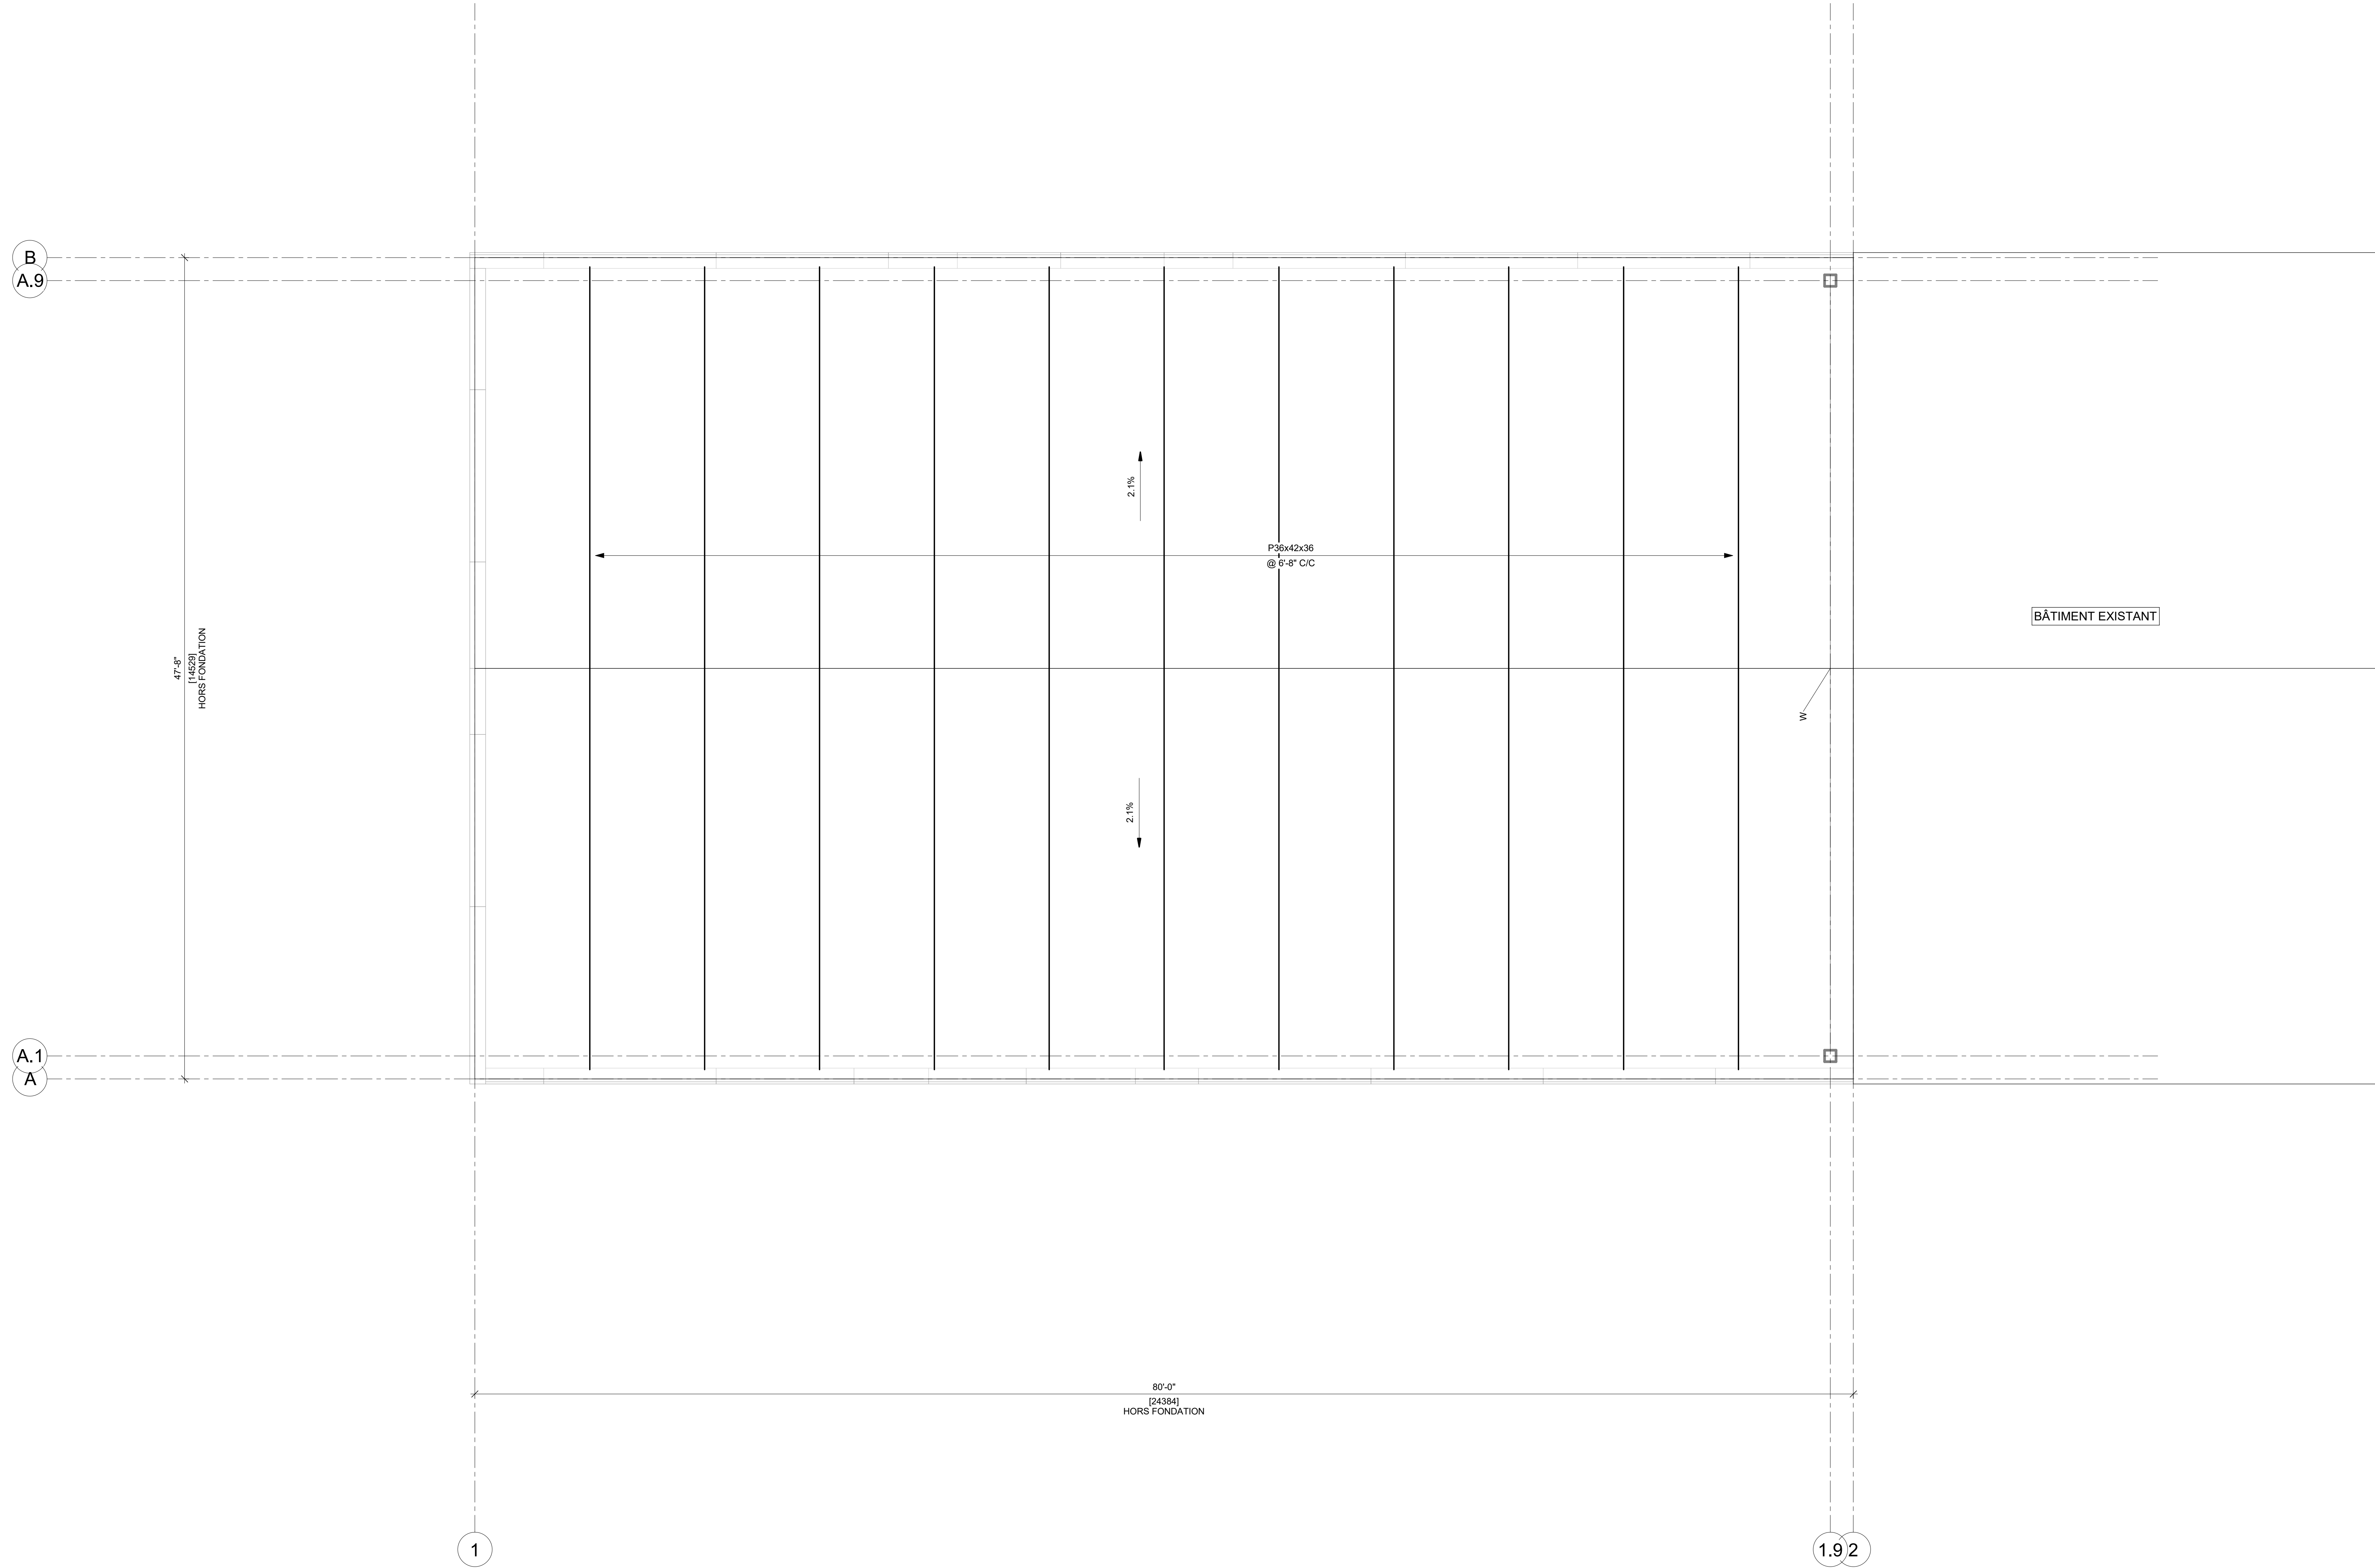

PLAN DE TOIT
1/4" = 1'-0"

DIAGRAMME DE SOULÈVEMENT BRUT (NON PONDERÉ)

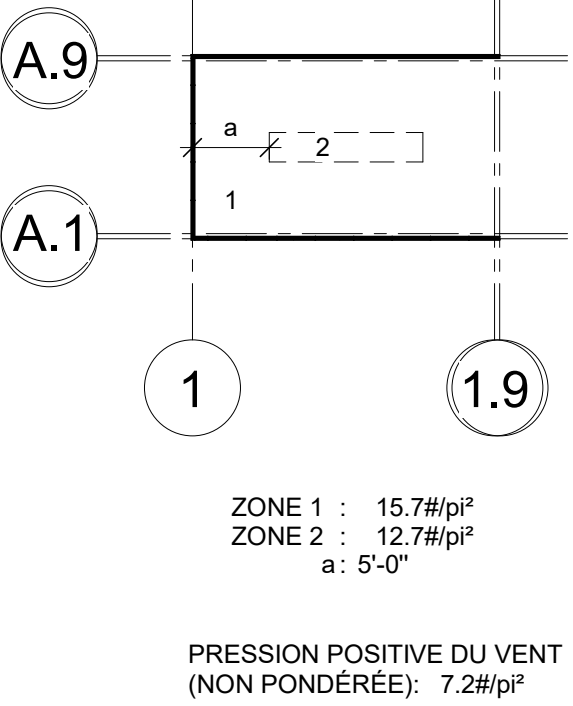

NOTE POUR LE CONTRACTEUR/ÉRECTEUR:
IL EST STRICTEMENT DÉFENDU DE MODIFIER, COPIER, REPRODUIRE OU DE DISTRIBUER CES DESSINS OU QUELQUES REPRÉSENTATIONS DE CES DESSINS, PAR TOUTES SOURCES DE MÉDIA INCLUANT ÉLECTRONIQUEMENT, SANS L'APPROBATION ÉCRITE DE GROUPE CANAM INC.

TOIT

DESSUS DE LA DALLE : 99'-6"
DESSUS DE LA FONDATION : 100'-0"
HAUTEUR LIBRE : 16'-0"
DESSUS D'ACIER HAUT : 120'-0"
DESSUS D'ACIER BAS : 119'-4"

CHARGES

Charge morte au toit (incluant charge collatérale) : 18.0 lb/ft²
Charge collatérale : 5.0 lb/ft² (incluant éclairage et/ou mécanique et gicleurs plus petits que 4" de diamètre)
Charge de neige au sol : $S_s = 71.0$ lb/ft²
 $S_s = 6.3$ lb/ft²
Coefficient de surcharge de neige : $C_s = 0.9$
 $C_w = 1.0$
Charge vive au toit : 0.0 lb/ft²
 $I_s = 1.0$
Charge de neige au toit : 63.1 lb/ft²
 $I_s = 1.0$
Charge de vent q 1/50 : 6.7 lb/ft²
Catégorie de risque : normal

Séisme (Sol de classe D assumé)

I_e : 1.0
 $S_s(0.2)$: 0.313
 $S_s(0.5)$: 0.319
 $S_s(1.0)$: 0.198
 $S_s(2.0)$: 0.0978
 $S_s(5.0)$: 0.0272
 $S_s(10.0)$: 0.0087
 PGA : 0.174
 PGV : 0.212

• Code Applicable : Code National du Bâtiment du Canada
Code du bâtiment du Québec, dernières éditions adoptées
Code de Pratique Standard ICCA.

• NOTE :
1. Si toutefois la catégorie d'emplacement devient E ou F selon le rapport géotechnique, le concept structural préliminaire (localisation et géométrie des contreventements, etc.) devra être validé et coordonné par l'ingénieur de Canam.

PRÉLIMINAIRE

NE DOIT PAS SERVIR À LA
CONSTRUCTION

REVISION	DATE	DESCRIPTION	DESS	VER
GERANT DE PROJET		-	-	-
DESSIN		-	-	-
DESSINÉ PAR	CONÇU PAR	INGÉNIEUR DU PROJET	ÉCHELLE:	
SL			Comme indiqué	
VÉRIFIÉ PAR	INGÉNIEURS CONSEILS / ARCHITECTES	DATE (jj/mm/aaaa)		
		12/06/2026		

CLIENT: MOREAU INDUSTRIES



SCAUX PROFESSIONNEL

PROJET

BÂTIMENT VENTILATEUR
VAL-D'OR, QUÉBEC

TITRE

CROQUIS PRÉLIMINAIRE - PLAN DE
TOIT

Initiales

NUMÉRO CONTRAT	NUMÉRO DESSIN	DIVISION	REVISION
P2026-120	EsMx401		