




Autodesk Docs://260890 - CTC 638 Humboldt/260890 CTC 638_CNM_2026.rvt

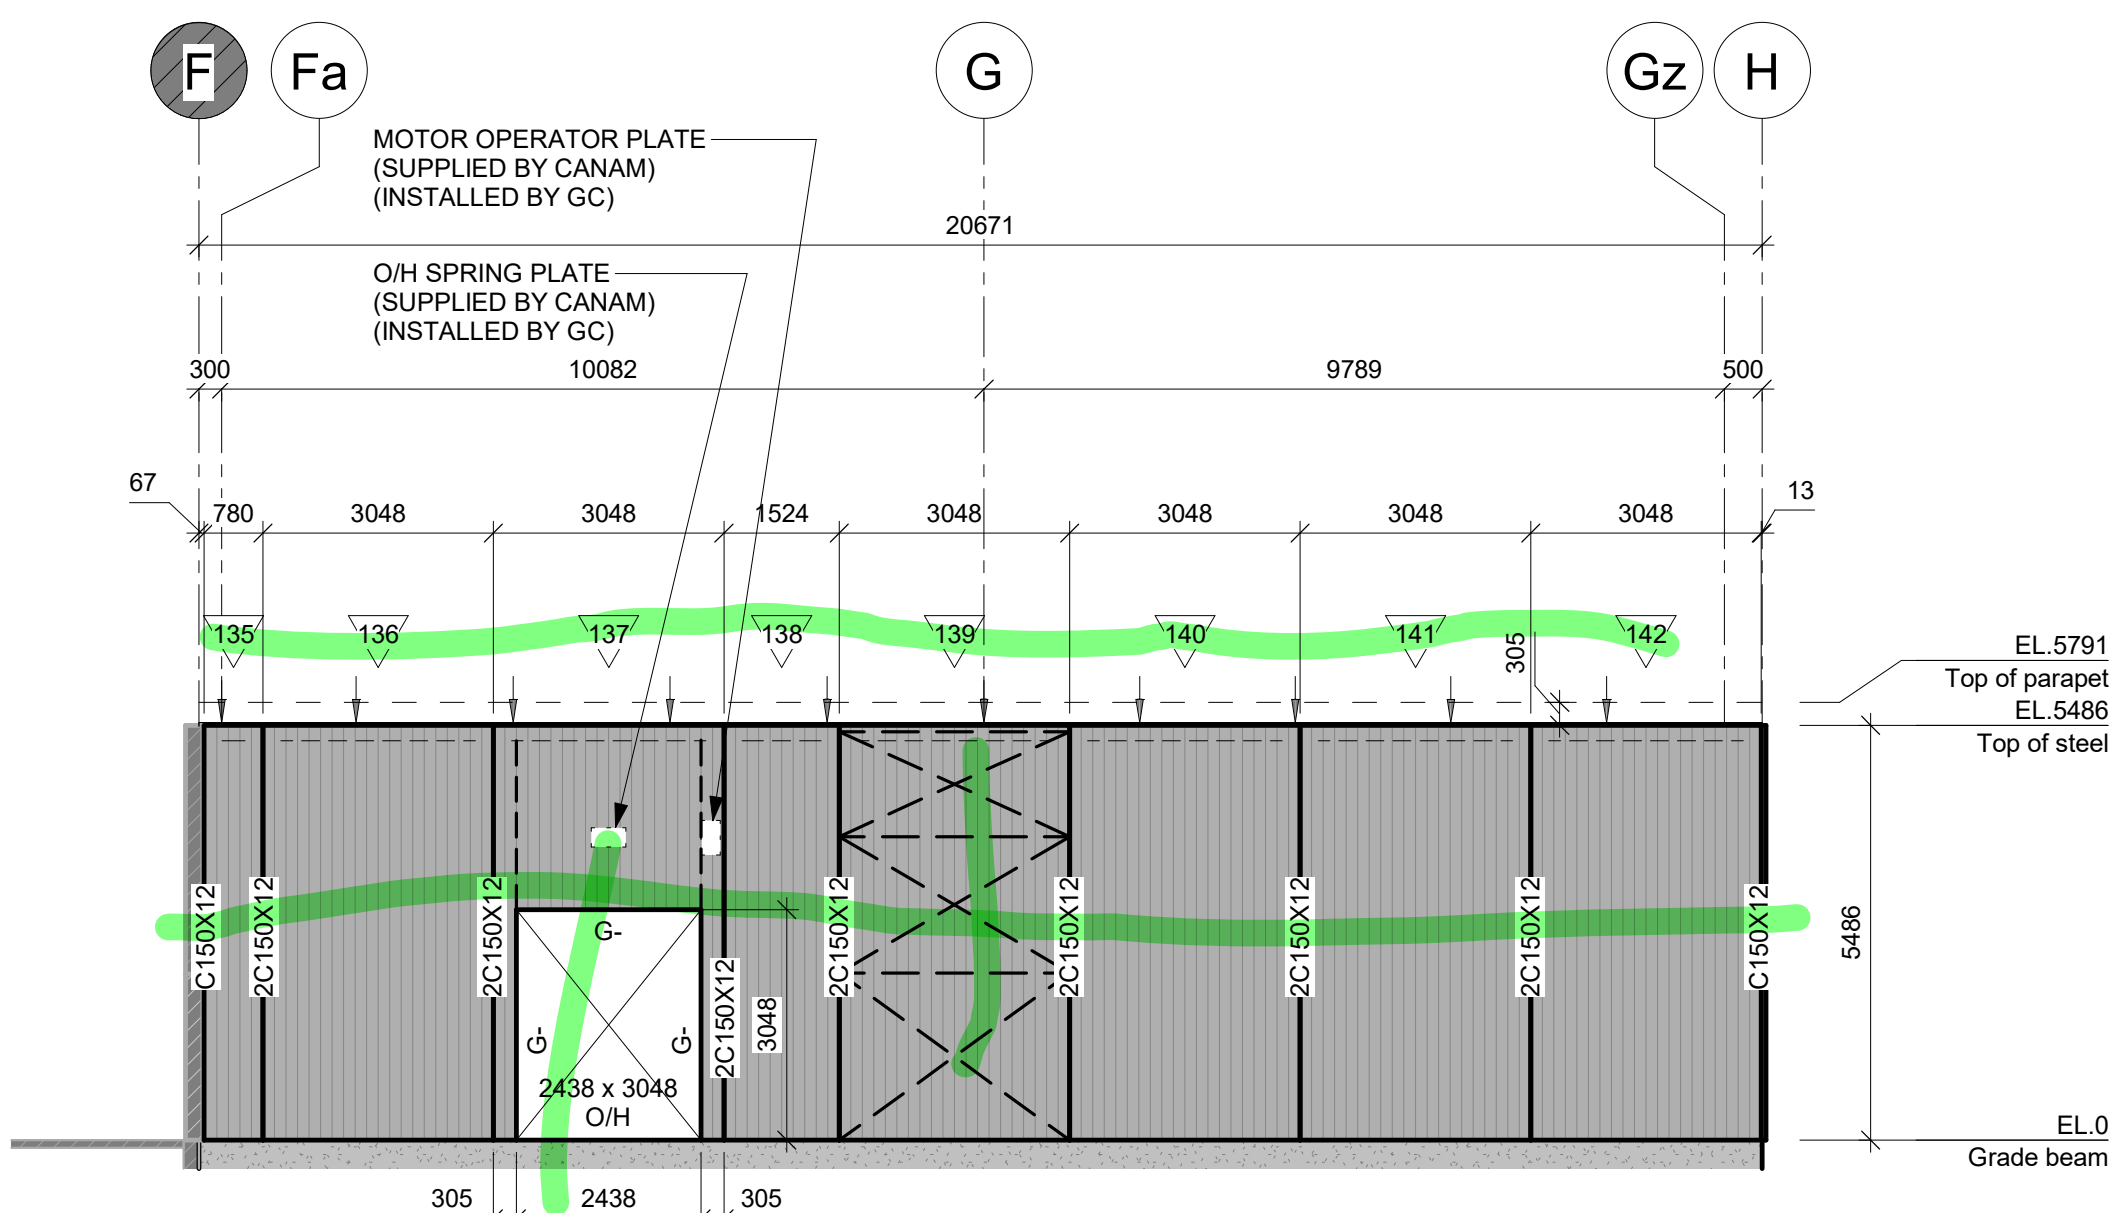


ELEVATION LINE 3c
1:100
LOAD BEARING PANELS
BRACING ROD 1"ø TYP UNO

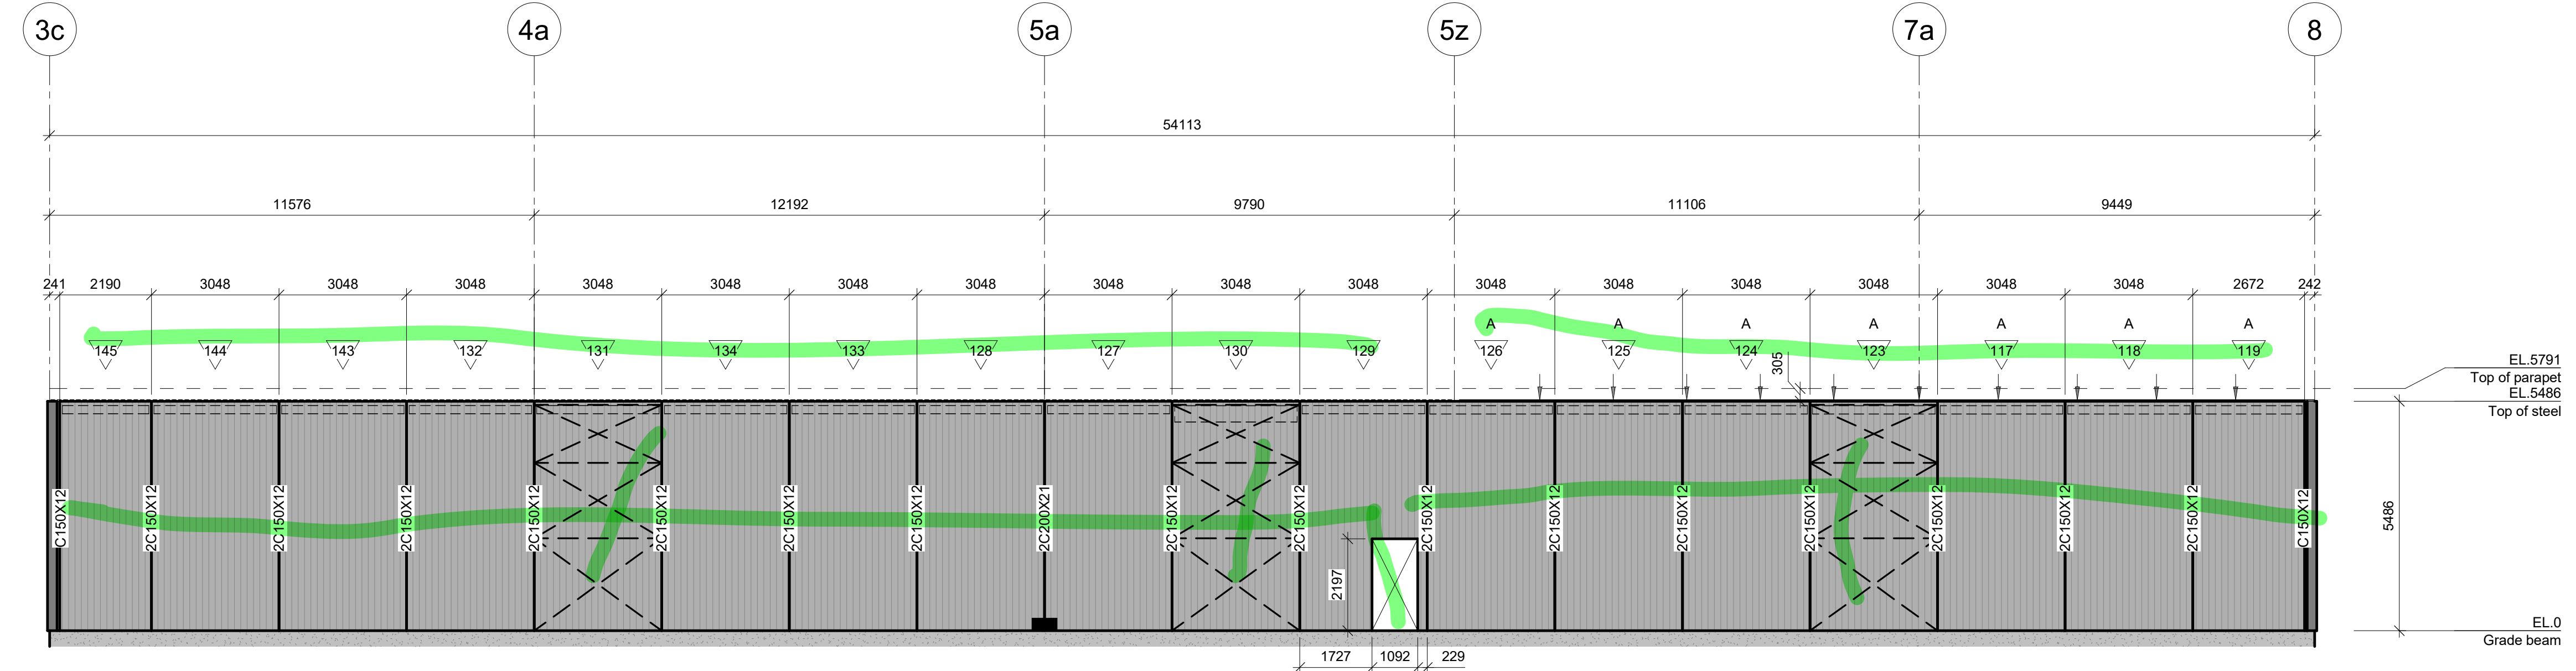


ELEVATION LINE H
1:100
NON LOAD BEARING PANELS
BRACING ROD 1"ø TYP UNO

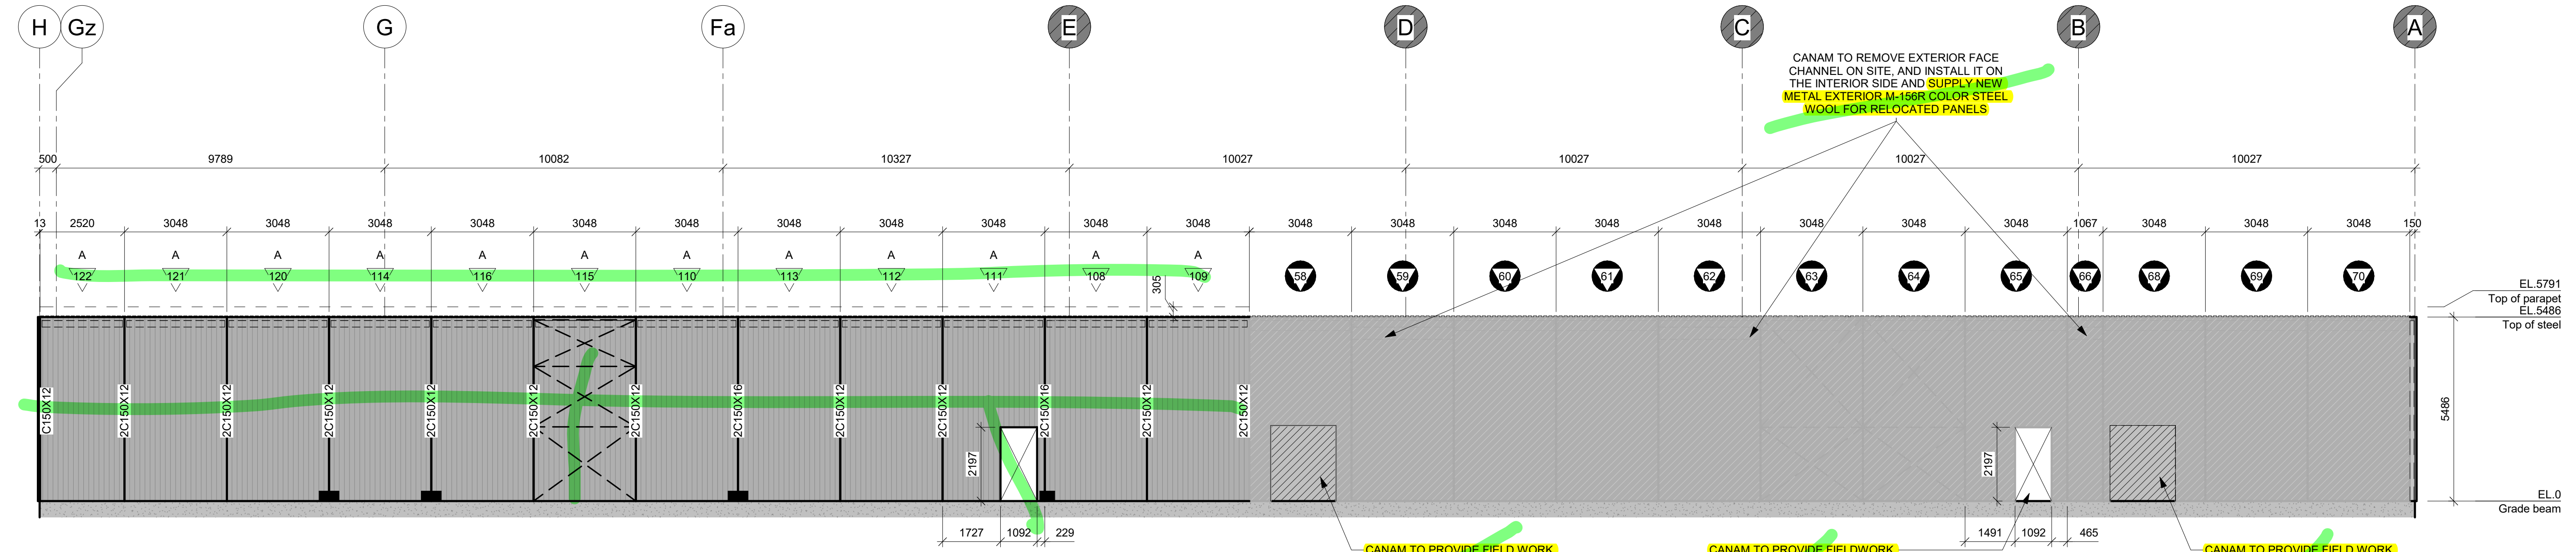


ELEVATION LINE 8
1:100
NON LOAD BEARING PANELS
BRACING ROD 1"ø TYP UNO

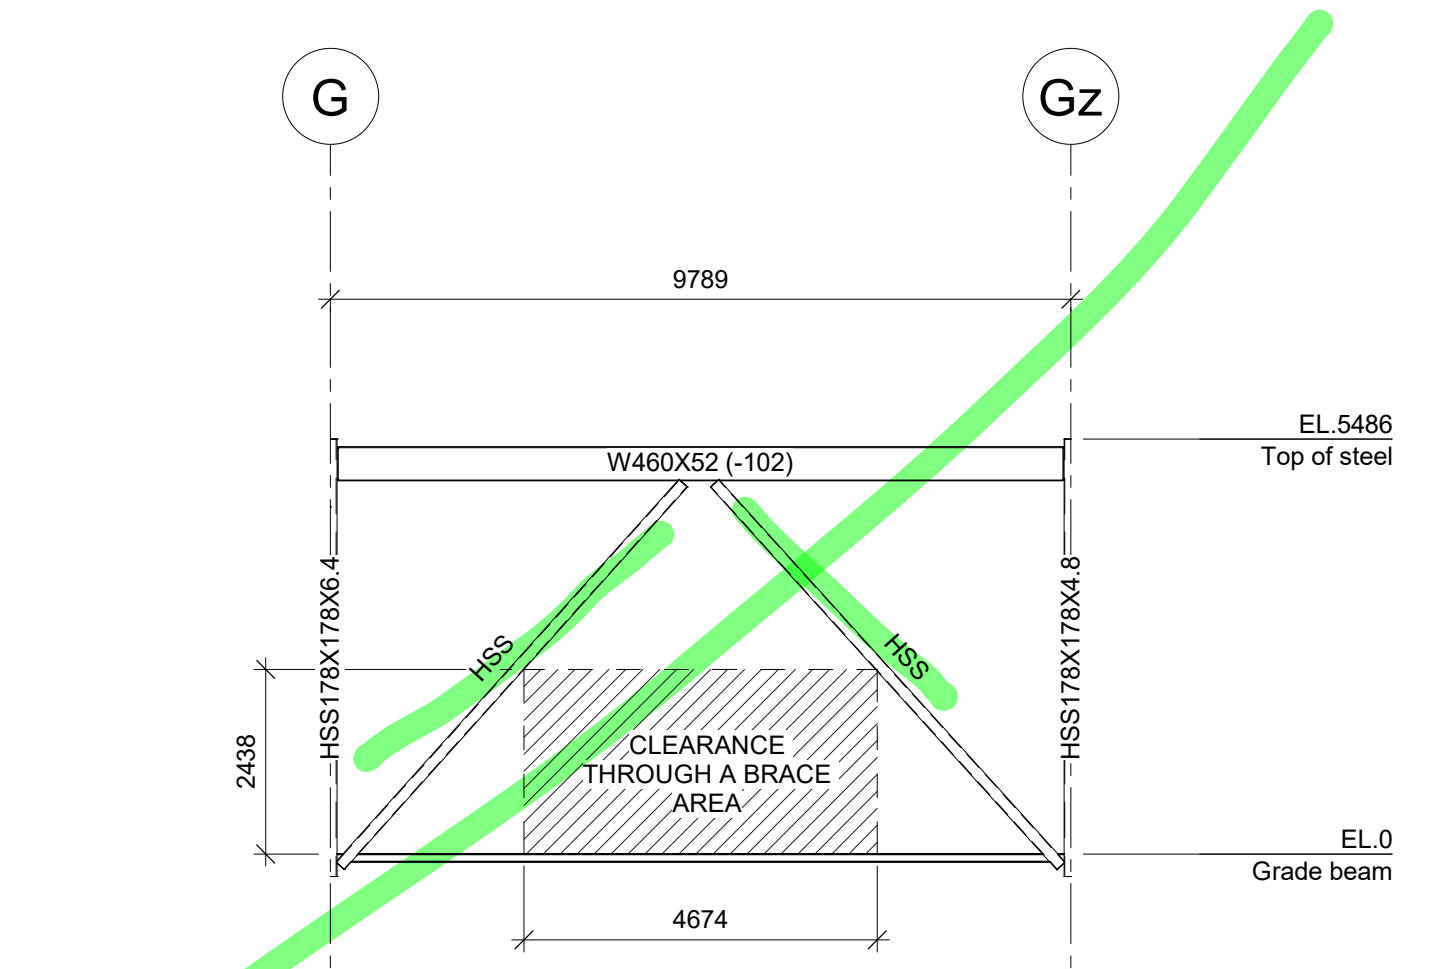

BRACING ELEVATION LINE 5z
1:100

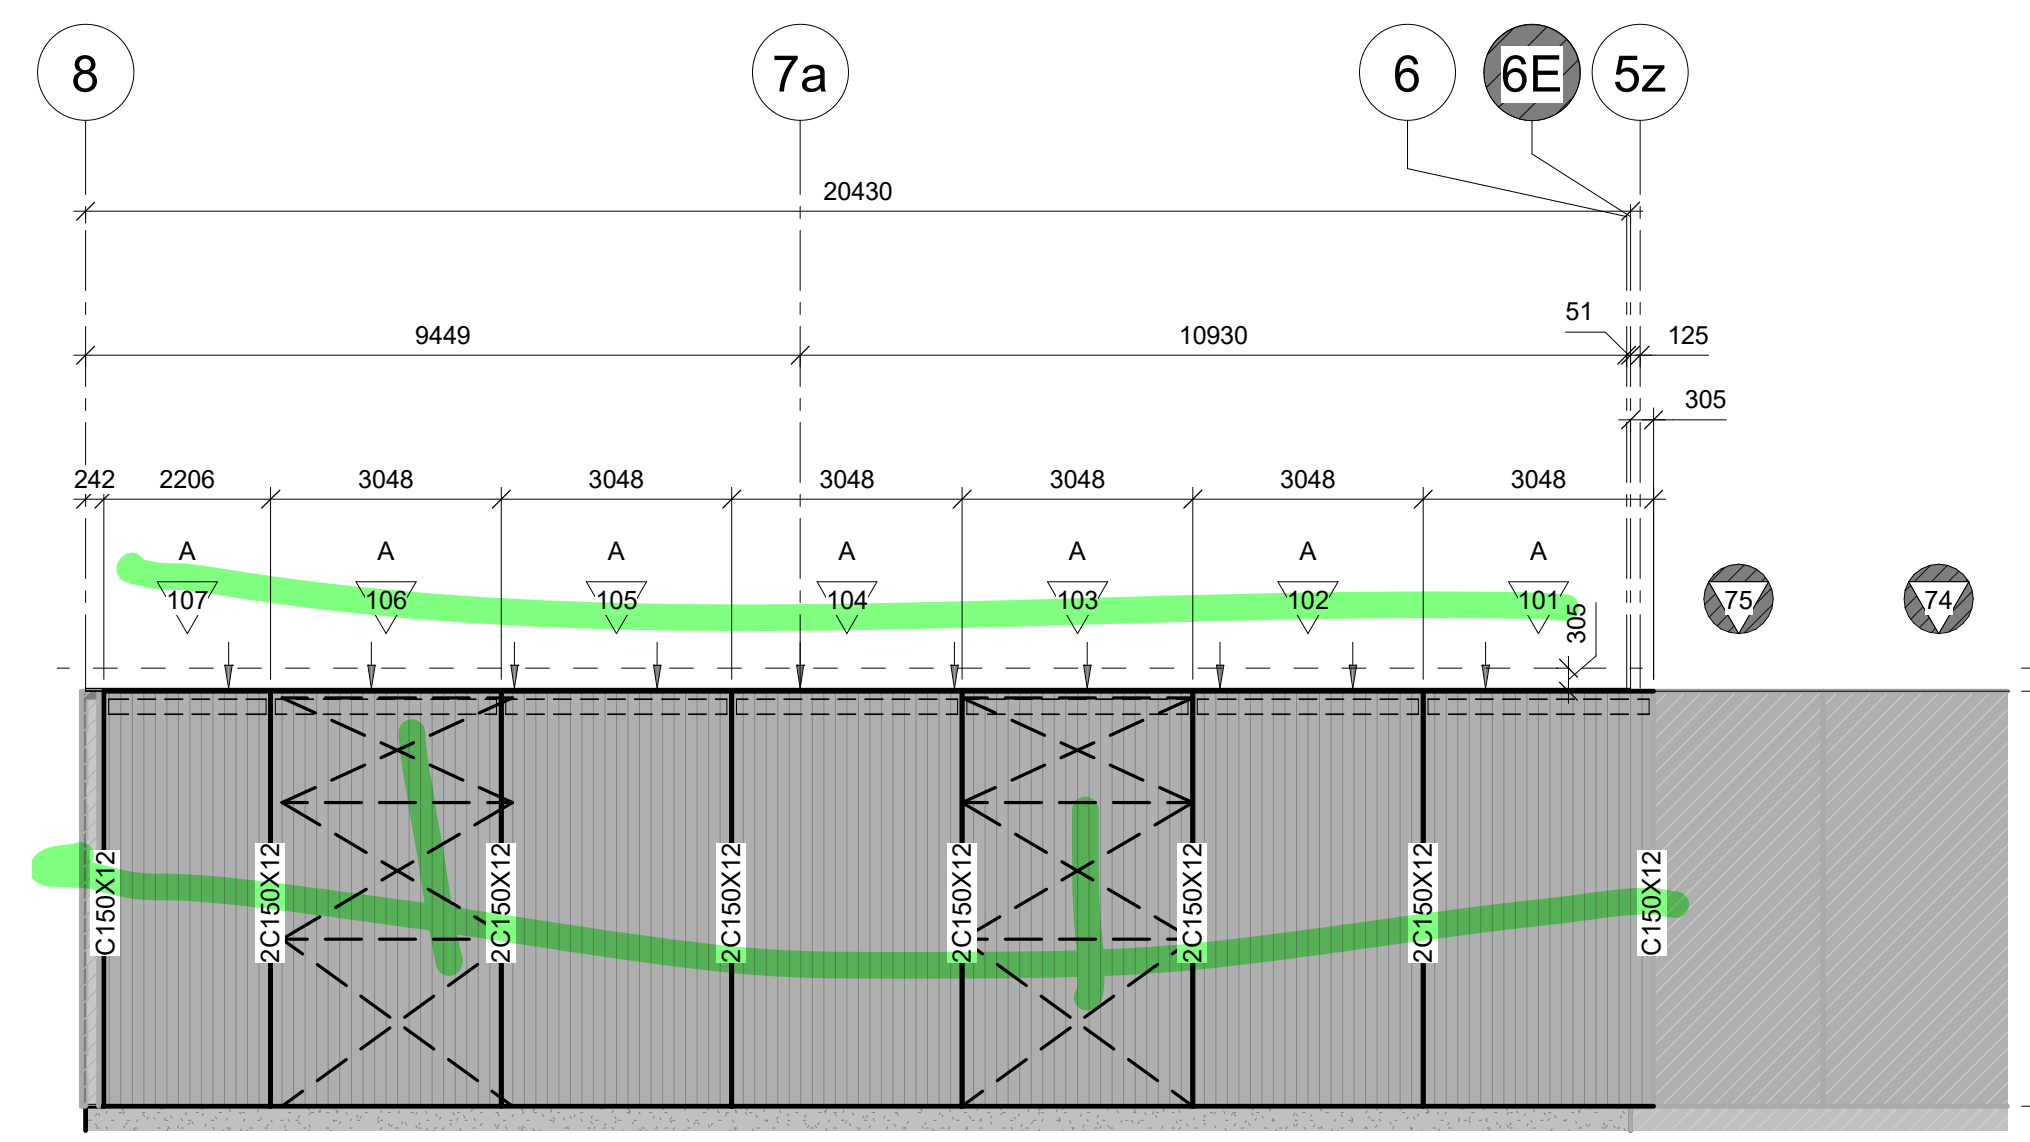

ELEVATION LINE A (SOUTH)
1:100
NON LOAD BEARING PANELS
BRACING ROD 1"ø TYP UNO

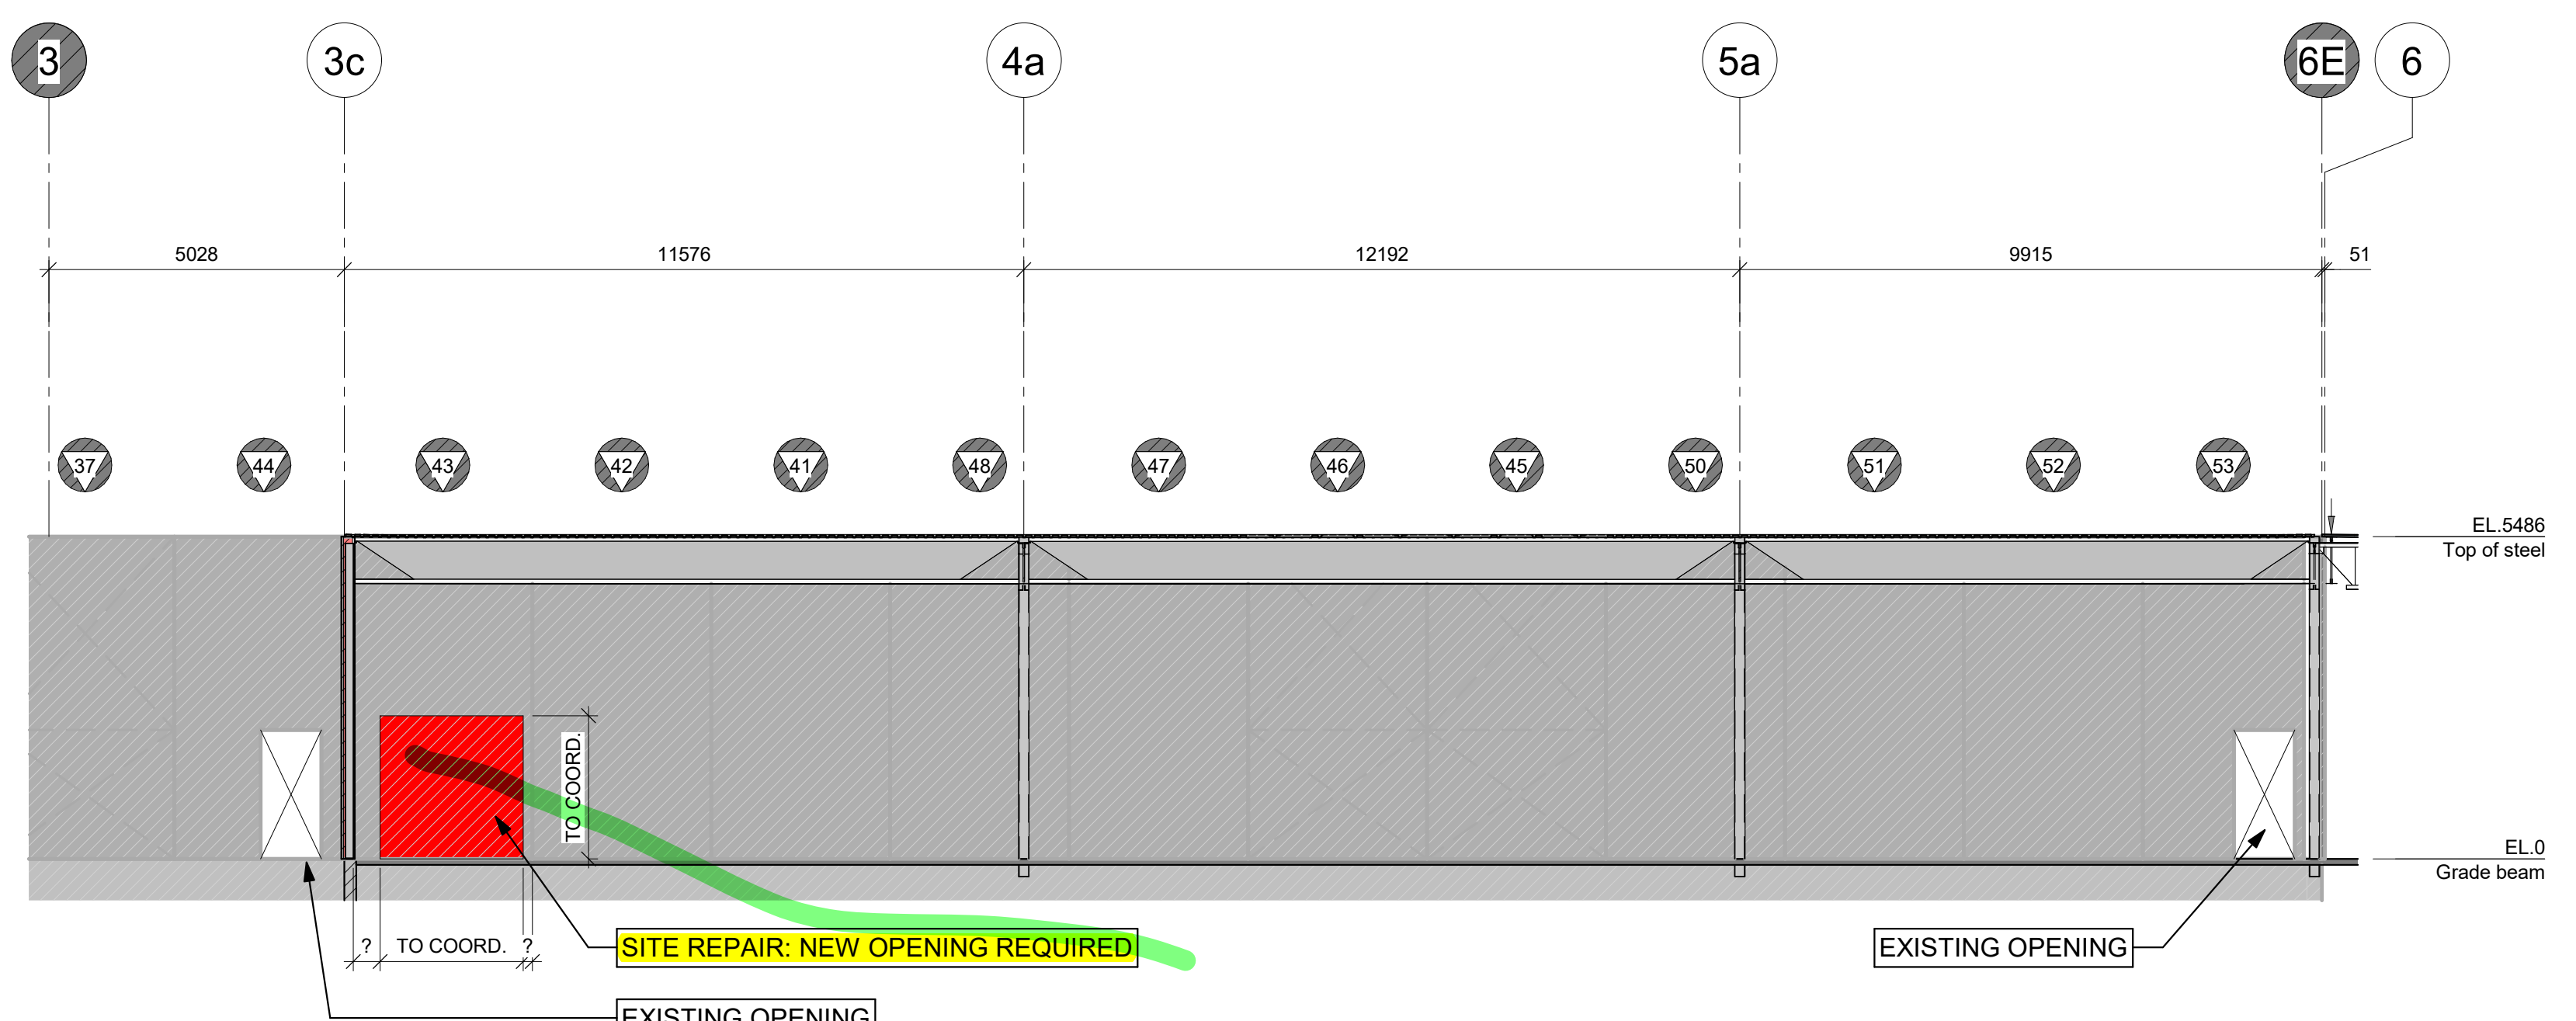

ELEVATION LINE F - EXISTING PANELS
1:100

REFER TO SHEET MX1000 FOR ALL DEMOLITION SCOPE AND RELATED REQUIREMENTS.

LEGEND ELEVATIONS		
Joint location on load bearing panels.	Boiling panel joints.	Boiling of panel joints with girt @ 12.5mm c/c (for rigid insulation 51mm full height).
OH ope Over head door opening.	El. girts	El. girts
X Panel section type		
XX-B?? Panel number - No bundle		
Extra DX-1		
GC General contractor		

FOR PERMIT

C	JUNE12008	For Permit	A.D.	J.L.
B	MAY12008	6% Review Submission	A.D.	M.C.
A	MAY12008	In Progress	A.D.	
REVISION	DATE	DESCRIPTION	REVIS	VER

PROJECT MANAGER
-
-
-
-

DRAFTING			
DRAWN	DESIGNED	PROJECT ENGINEER	SCALE
Stefan Gras	Imola Aranyosi	Martin Couture	AS INDICATED
CHECKED	CONSULTING ENGINEERS - ARCHITECTS	DATE (yyyy/mm/dd)	
Arthur Dugay	GRAVITY ENGINEERING & NEOTERIC	2028/04/14	

CUSTOMER: CANADIAN TIRE CORPORATION LTD.

CANAM
11505, 1re Avenue, bureau 500, Saint-Georges Beauce
Quebec, Canada, G5V 7A3
Phone : (418) 228-8031
Toll free : (877) 499-6049
www.canam.com

PROFESSIONAL SEAL
M. COUTURE
1001-10006
2026/04/14
PROFESSIONAL ENGINEER
MARTIN COUTURE
2026/04/14
SASKATCHEWAN

PROJECT
CTC 638
HUMBOLDT, SASKATCHEWAN

DRAWING TITLE
ELEVATIONS

CONTRACT NUMBER	DRAWING NUMBER	DIVISION	REVISION
P0000-000 260890	MX501		