



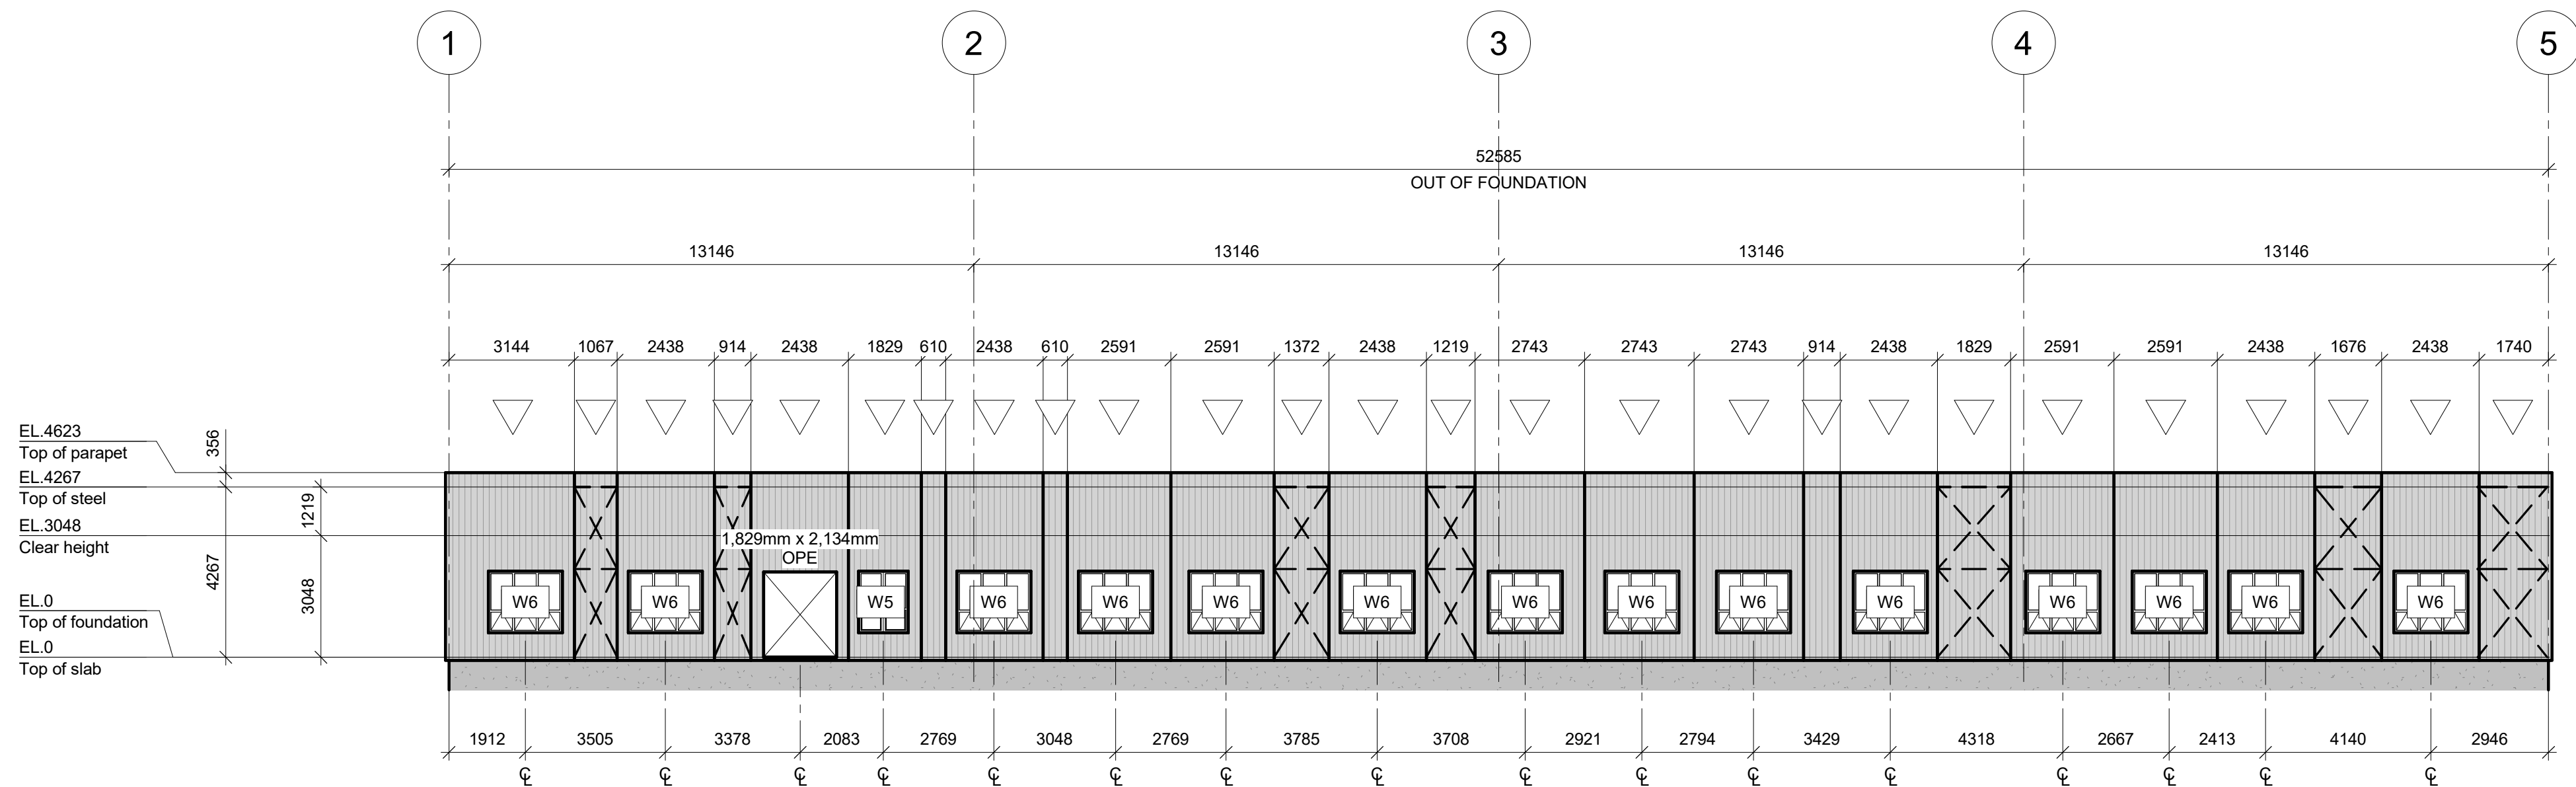



ELEVATION LINE A (SOUTH)
1 : 125

O/H & OPENING SCHEDULE			
Total	Type	Tag	Remarks
3	1,829mm x 2,134mm	OPE	
1	914mm x 2,134mm	OPE	
Total général: 4			


WINDOW SCHEDULE						
Identity	Qty.	Installation	Description	Sizes (Ext. of frame) (width & height)	Frame color	Remarks
W1	1		Awning single aluminium window with thermal break and sealed glass + Low-E argon clear	711mm x 813mm	Aluminum Frame (no color)	
W2	1		Awning single aluminium window with thermal break and sealed glass + Low-E argon clear	1,219mm x 813mm	Aluminum Frame (no color)	
W3	1		Awning double aluminium window with thermal break and sealed glass + Low-E argon clear (2 w x 1 h)	1,829mm x 813mm	Aluminum Frame (no color)	
W4	1		Fixed and single awning aluminium window with thermal break and sealed glass + Low-E argon clear (1 wide x 2 high)	610mm x 1,524mm	Aluminum Frame (no color)	
W5	3		Fixed and awning aluminium window with thermal break and sealed glass + Low-E argon clear (2 wide x 2 high)	1,219mm x 1,524mm	Aluminum Frame (no color)	
W6	26		Awning aluminium window with thermal break and sealed glass + Low-E argon clear (3 wide eq x 2 high)	1,829mm x 1,524mm	Aluminum Frame (no color)	
W7	4		Awning aluminium window with thermal break and sealed glass + Low-E argon clear (3 wide eq x 2 high)	2,438mm x 1,524mm	Aluminum Frame (no color)	

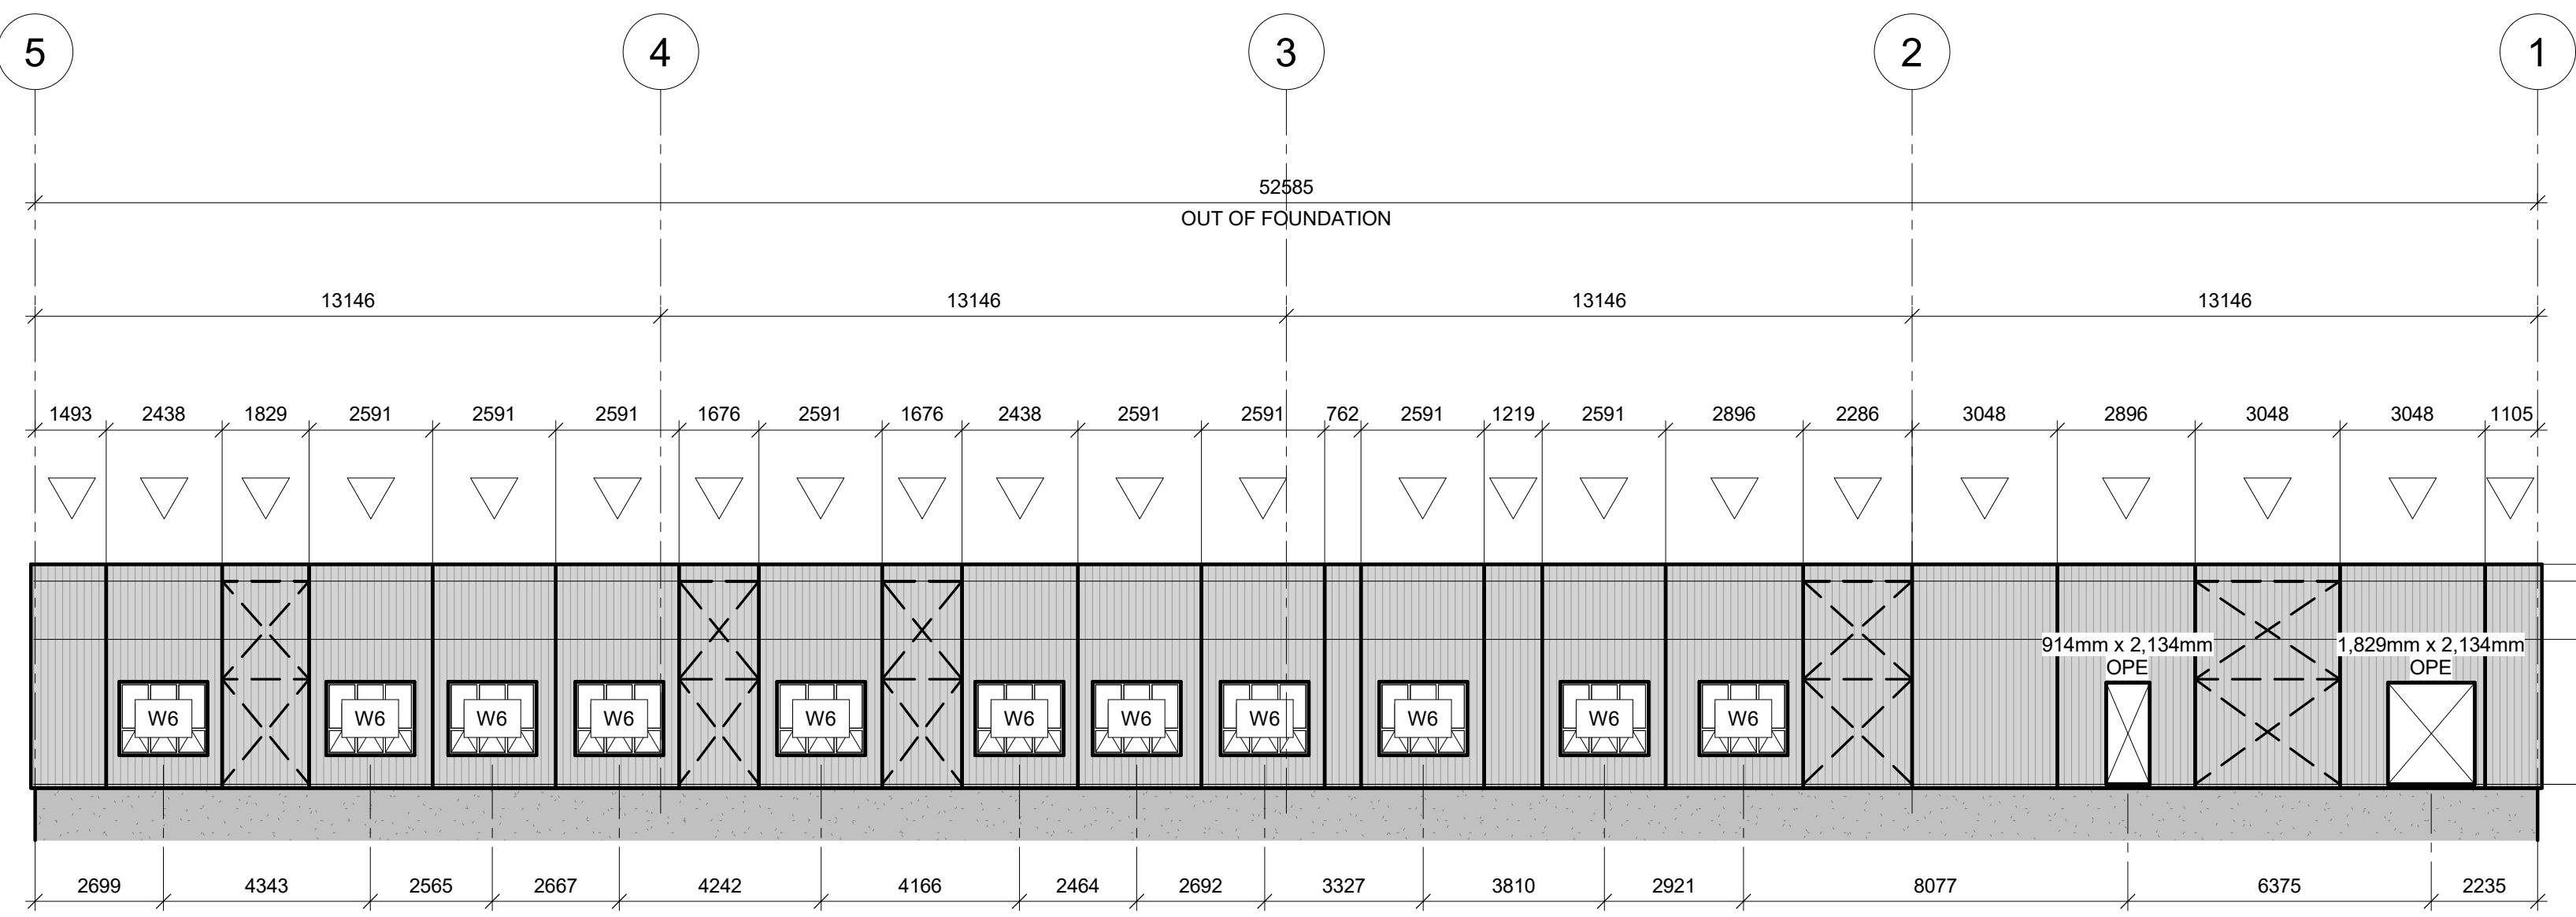

ELEVATION LINE C (NORTH)
1 : 125

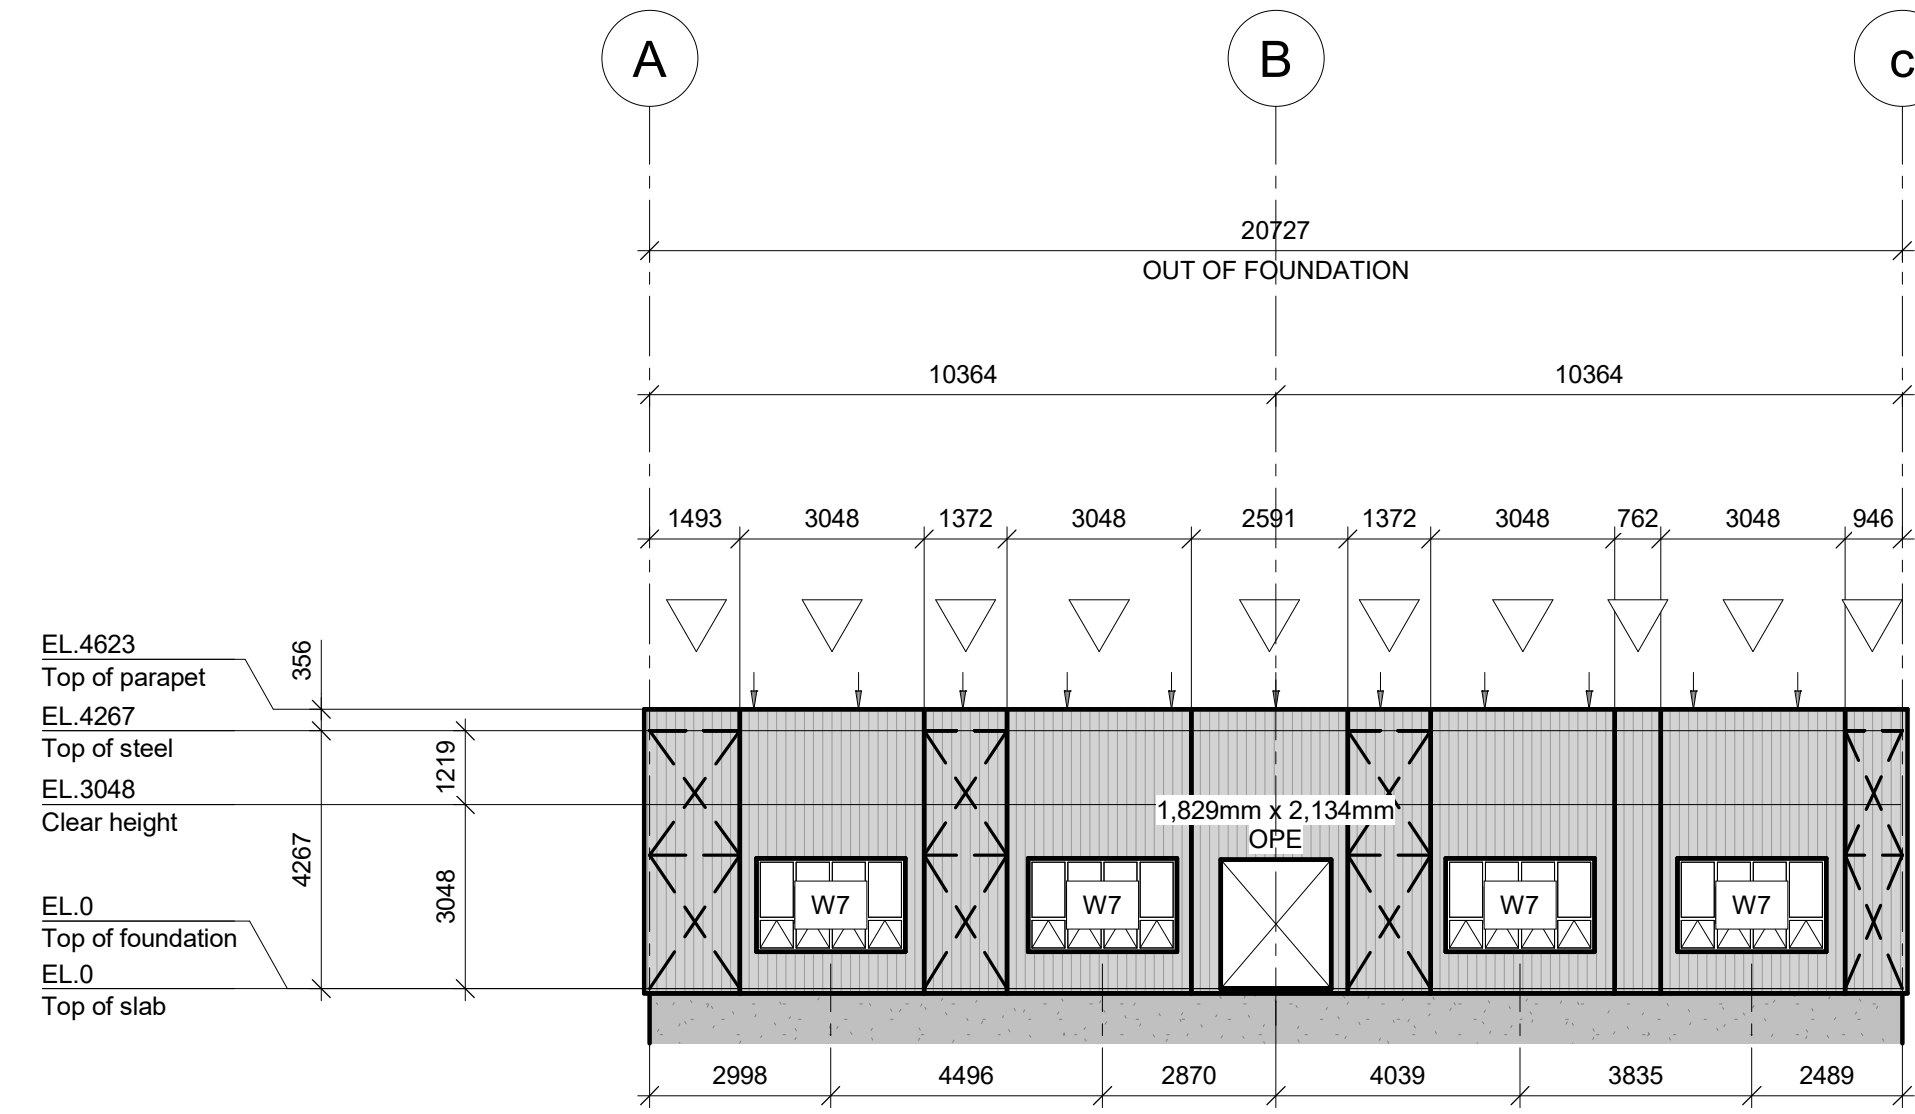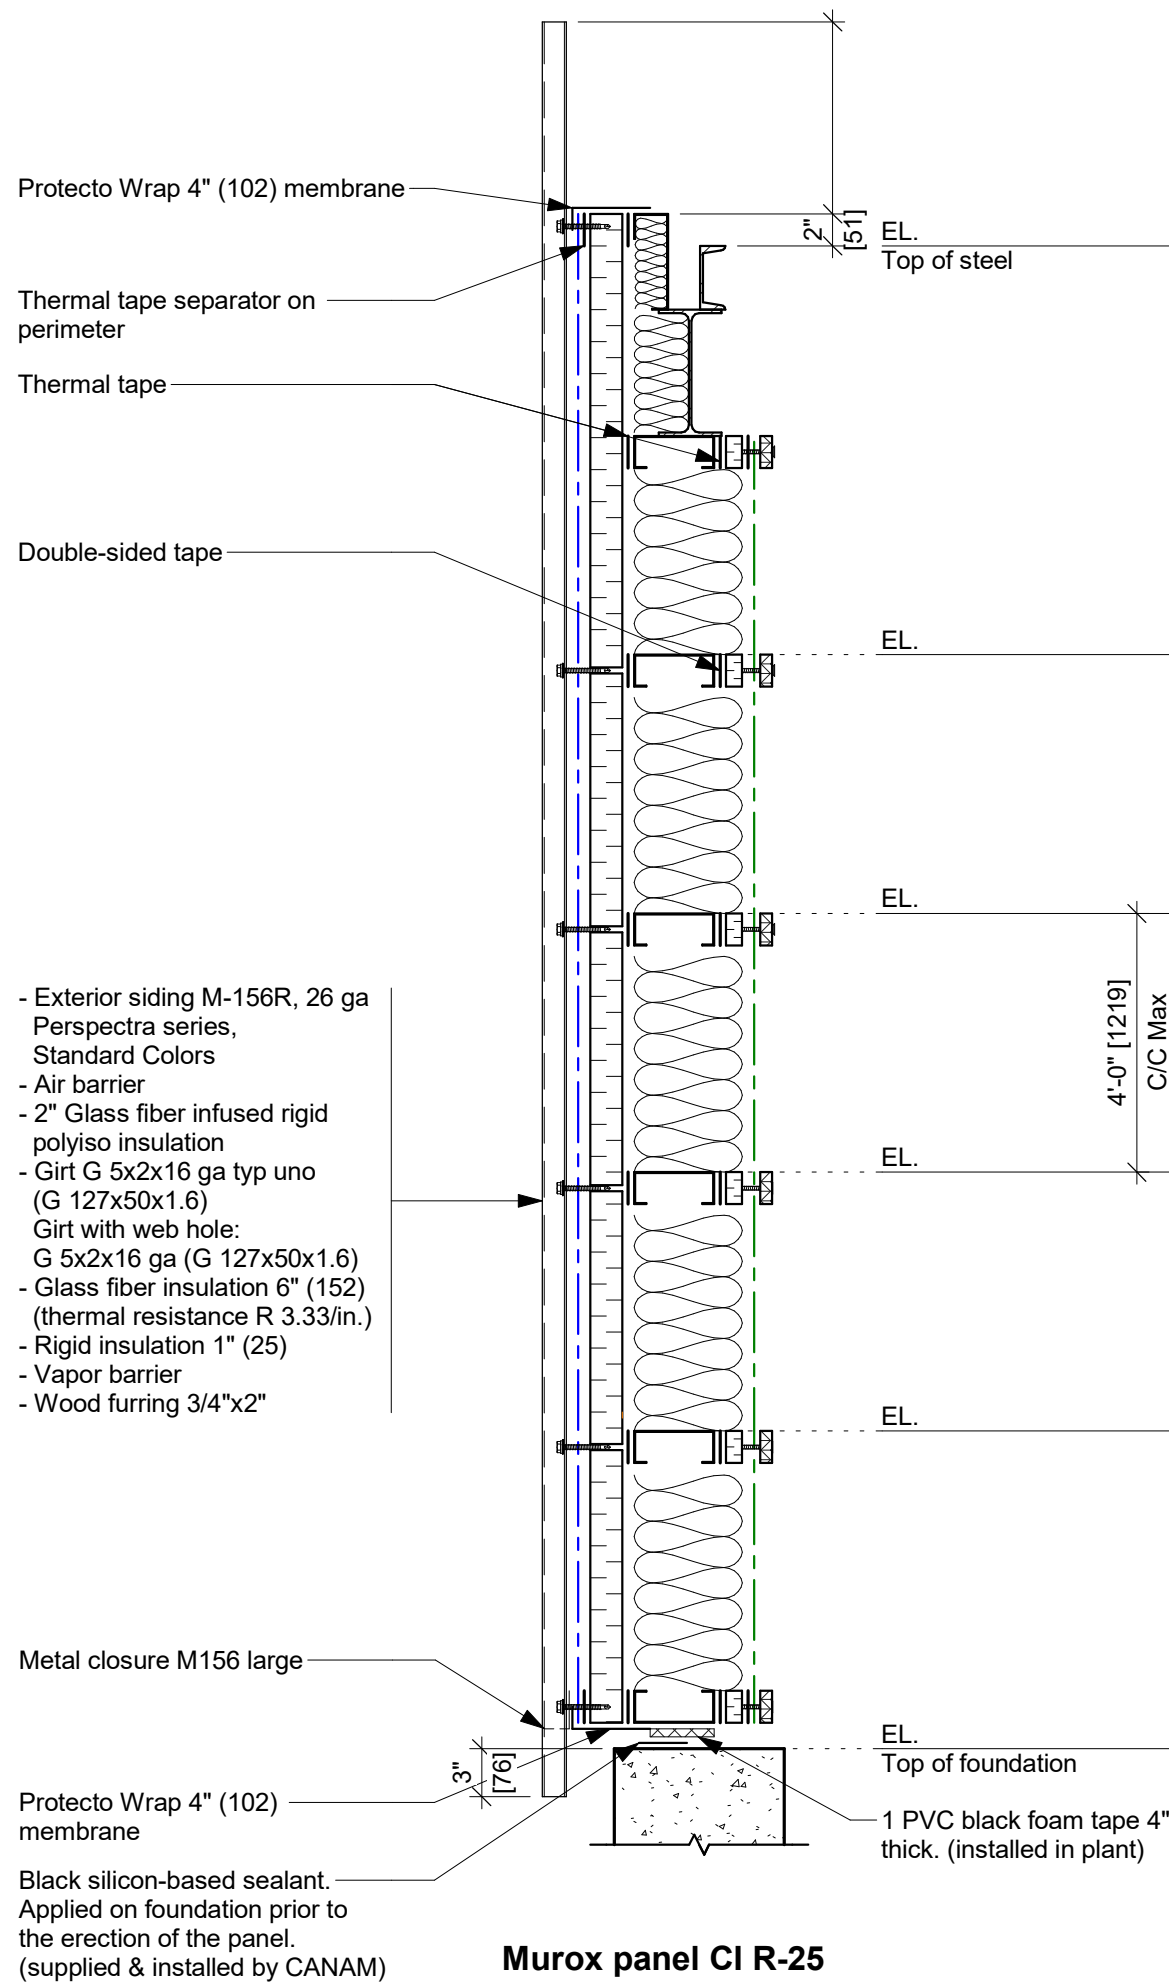

ELEVATION LINE 5 (EAST)
1 : 125

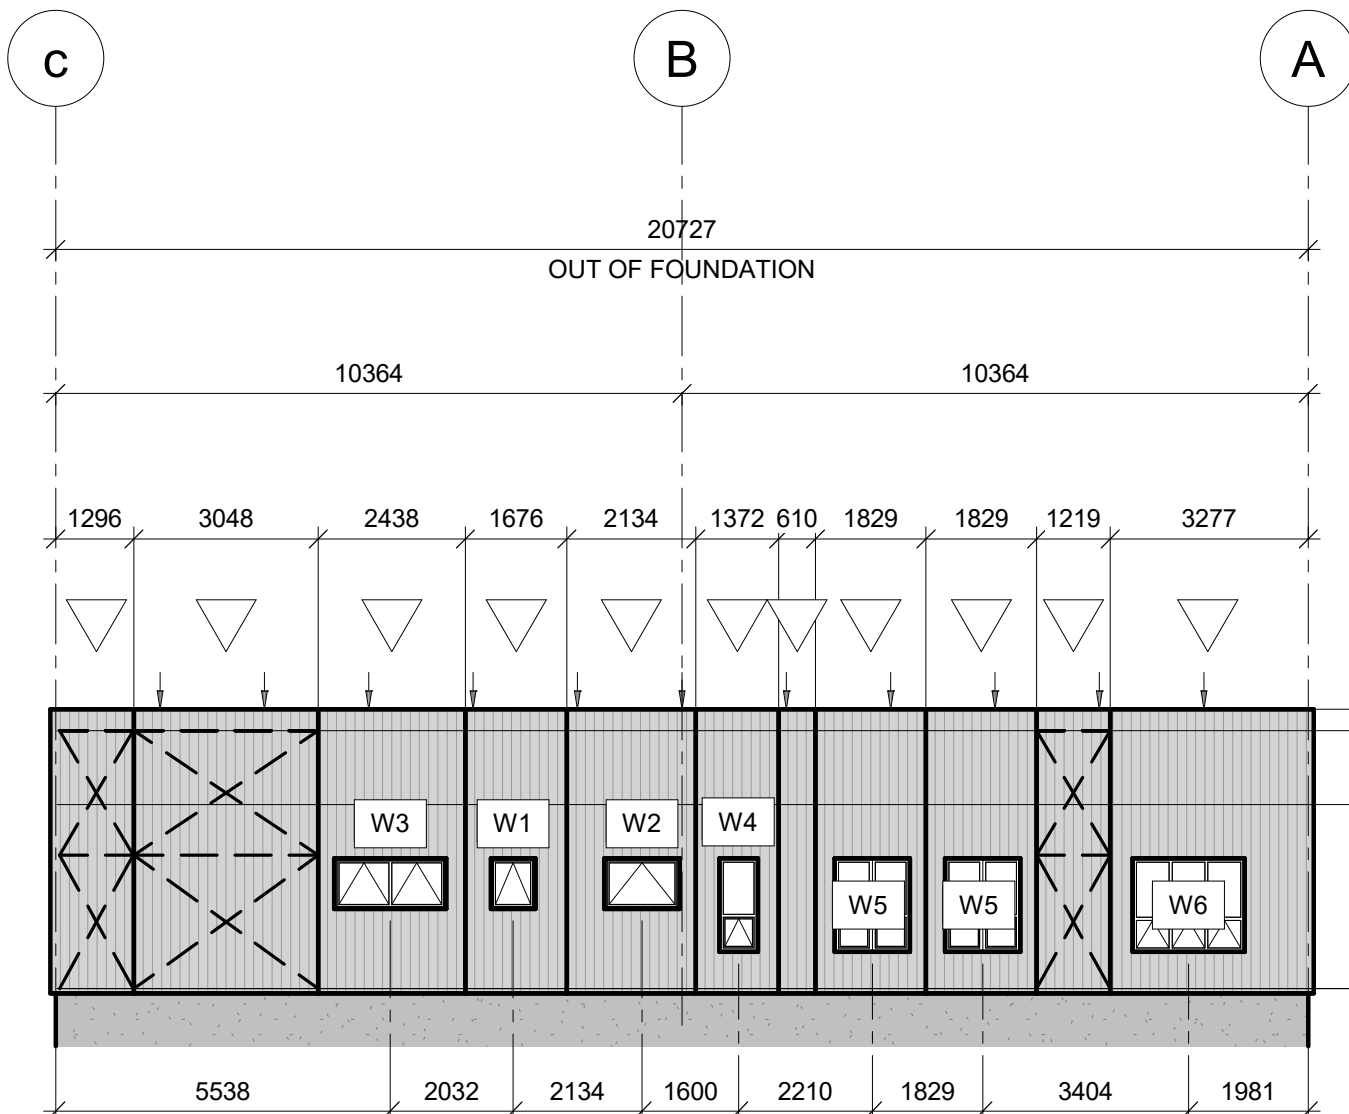

ELEVATION LINE 1 (WEST)
1 : 125

CONTRACTOR/ERECTOR NOTE:
IT IS PROHIBITED TO MODIFY, COPY, REPRODUCE OR OTHERWISE DISTRIBUTE THIS DRAWING OR ANY REPRESENTATION OF THIS DRAWING, OR ANY MEDIA, INCLUDING ELECTRONIC, WITHOUT THE PRIOR WRITTEN APPROVAL OF CANAM GROUP INC.

PRELIMINARY

NOT TO BE USED FOR CONSTRUCTION

REVISION	DATE	DESCRIPTION	DESS	VER.
PROJECT MANAGER				
		-		
		-		
		-		
		-		
DRAFTING:				
DRAWN	DESIGNED	PROJECT ENGINEER	SCALE:	
J.P.			Comme indiqué	
CHECKED	CONSULTING ENGINEERS / ARCHITECTS		DATE (yyyy/mm/iss) :	
			2026/07/28	

CUSTOMER: Strong Bros.



PROFESSIONAL SEAL

PROJECT

DCC Site Office
Kingston, Ontario

DRAWING TITLE

PRELIMINARY SKETCH - ELEVATION,
WALL SECTION AND SCHEDULES

CONTRACT NUMBER	DRAWING NUMBER	DIVISION	REVISION
P2026-142	EsMx501		