


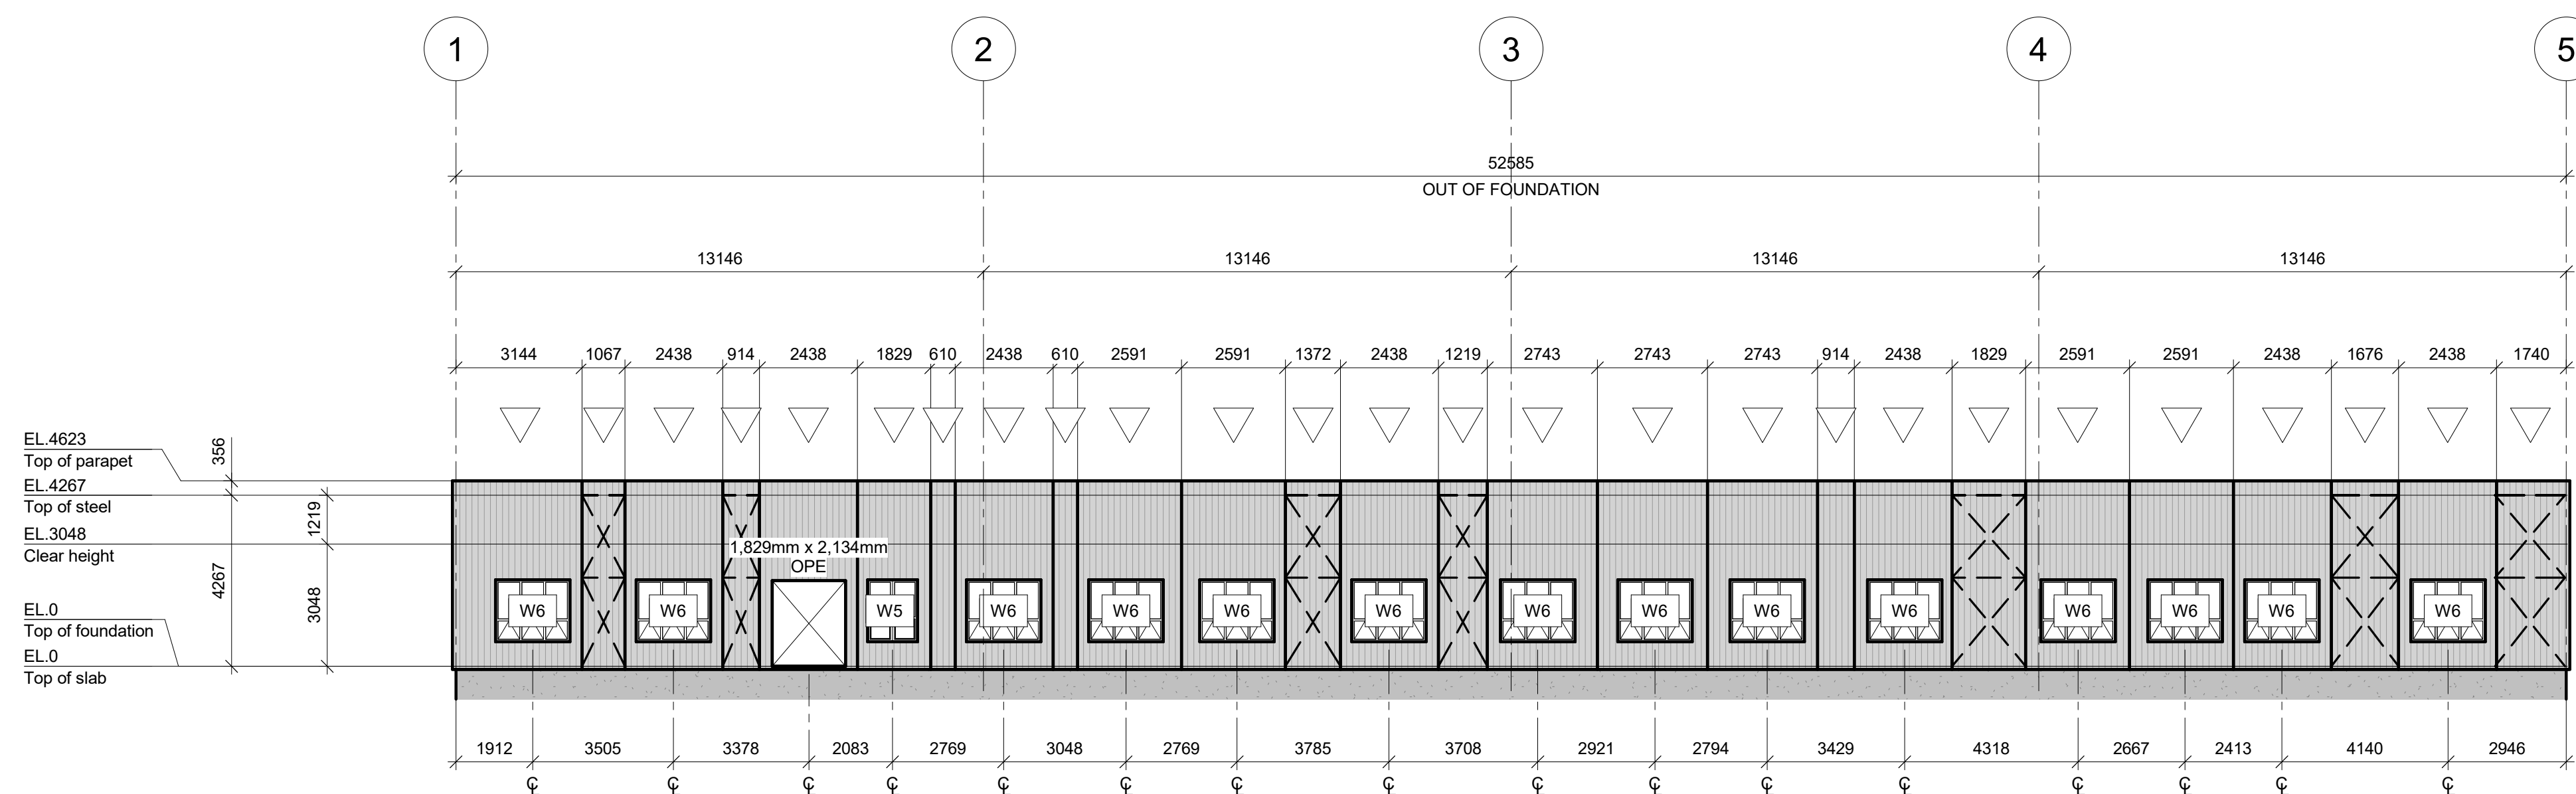


ELEVATION LINE A (SOUTH)  
1 : 125

| O/H & OPENING SCHEDULE |                   |     |         |
|------------------------|-------------------|-----|---------|
| Total                  | Type              | Tag | Remarks |
| 3                      | 1,829mm x 2,134mm | OPE |         |
| 1                      | 914mm x 2,134mm   | OPE |         |
| Total général: 4       |                   |     |         |


| WINDOW SCHEDULE |      |              |   |                                           |                               |         |
|-----------------|------|--------------|---|-------------------------------------------|-------------------------------|---------|
| Identity        | Qty. | Installation | Description   | Sizes (Ext. of frame)<br>(width & height) | Frame color                   | Remarks |
| W1              | 1    |              | Awning single aluminium window with thermal break and sealed glass + Low-E argon clear                             | 711mm x 813mm                             | Aluminium Frame<br>(no color) |         |
| W2              | 1    |              | Awning single aluminium window with thermal break and sealed glass + Low-E argon clear                             | 1,219mm x 813mm                           | Aluminium Frame<br>(no color) |         |
| W3              | 1    |              | Awning double aluminium window with thermal break and sealed glass + Low-E argon clear (2 w x 1 h)                 | 1,829mm x 813mm                           | Aluminium Frame<br>(no color) |         |
| W4              | 1    |              | Fixed and single awning aluminium window with thermal break and sealed glass + Low-E argon clear (1 wide x 2 high) | 610mm x 1,524mm                           | Aluminium Frame<br>(no color) |         |
| W5              | 3    |              | Fixed and awning aluminium window with thermal break and sealed glass + Low-E argon clear (2 wide x 2 high)        | 1,219mm x 1,524mm                         | Aluminium Frame<br>(no color) |         |
| W6              | 26   |              | Awning aluminium window with thermal break and sealed glass + Low-E argon clear (3 wide eq x 2 high)               | 1,829mm x 1,524mm                         | Aluminium Frame<br>(no color) |         |
| W7              | 4    |              | Awning aluminium window with thermal break and sealed glass + Low-E argon clear (3 wide eq x 2 high)               | 2,438mm x 1,524mm                         | Aluminium Frame<br>(no color) |         |

# PRELIMINARY


NOT TO BE USED FOR CONSTRUCTION

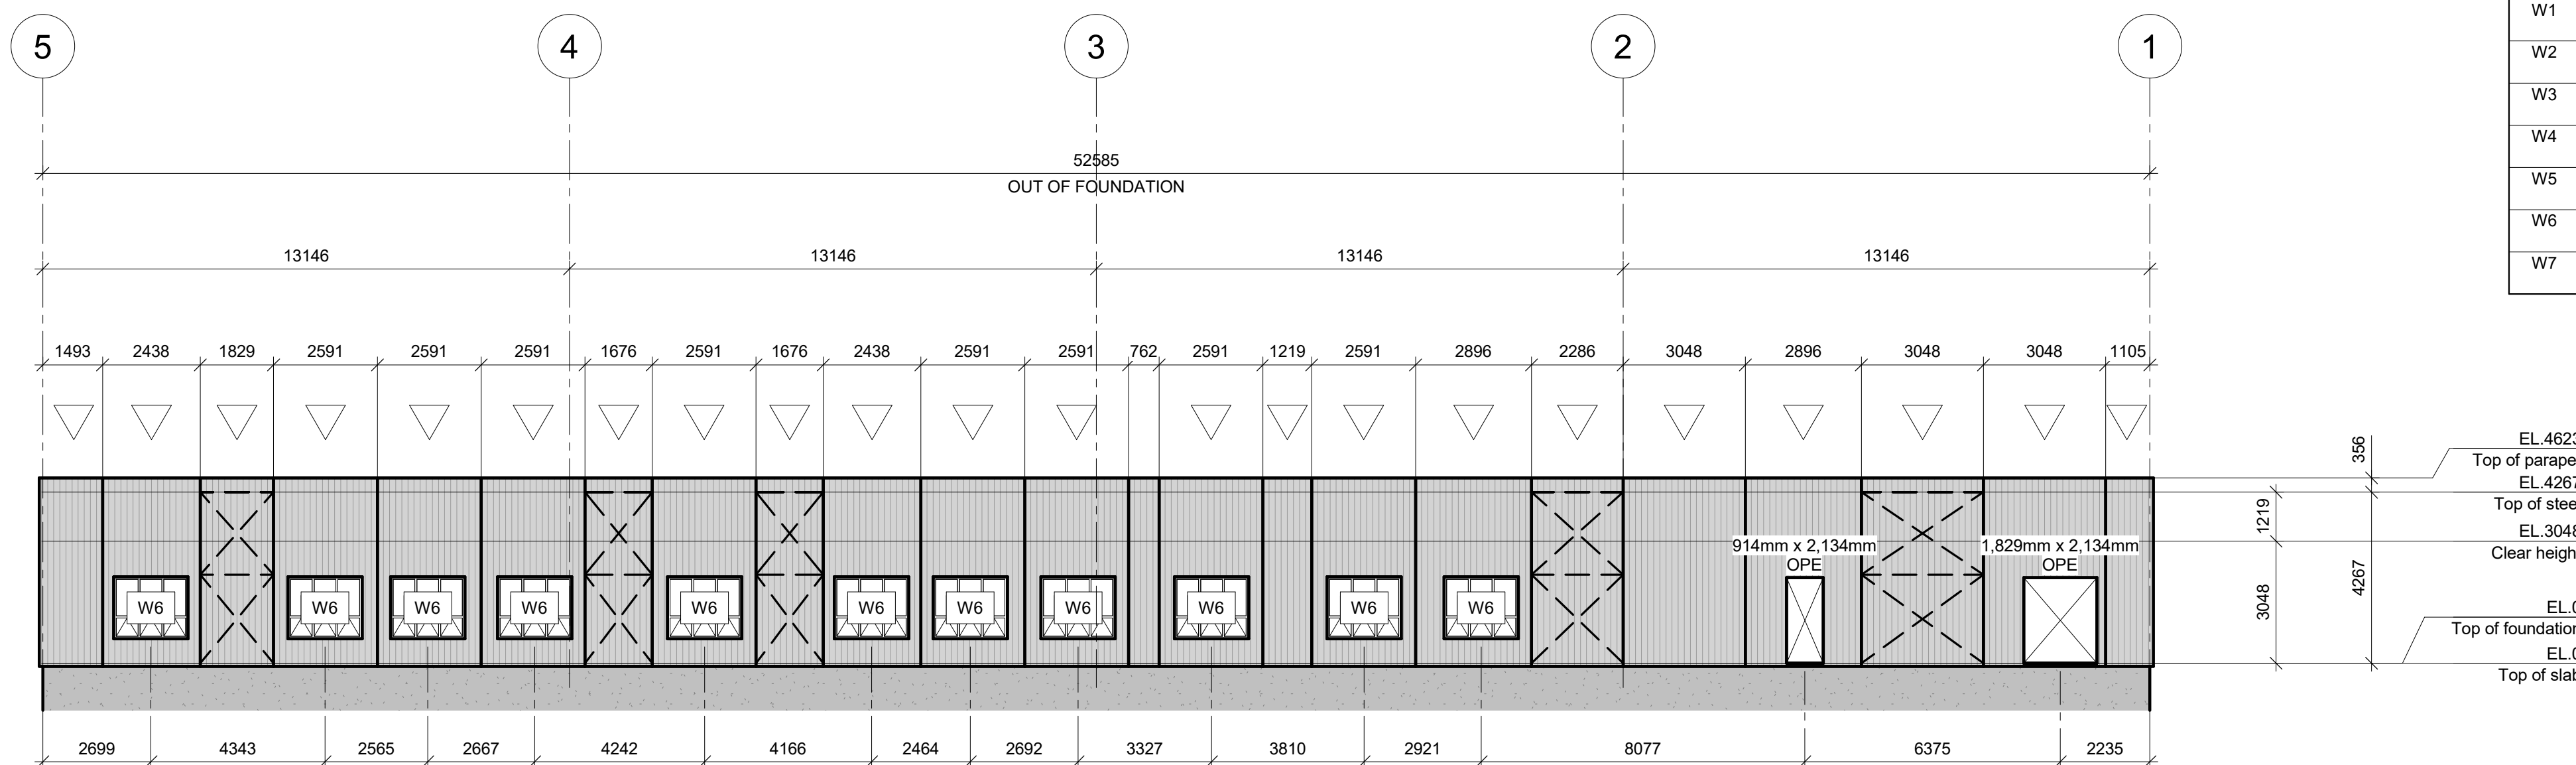


ELEVATION LINE C (NORTH)  
1 : 125

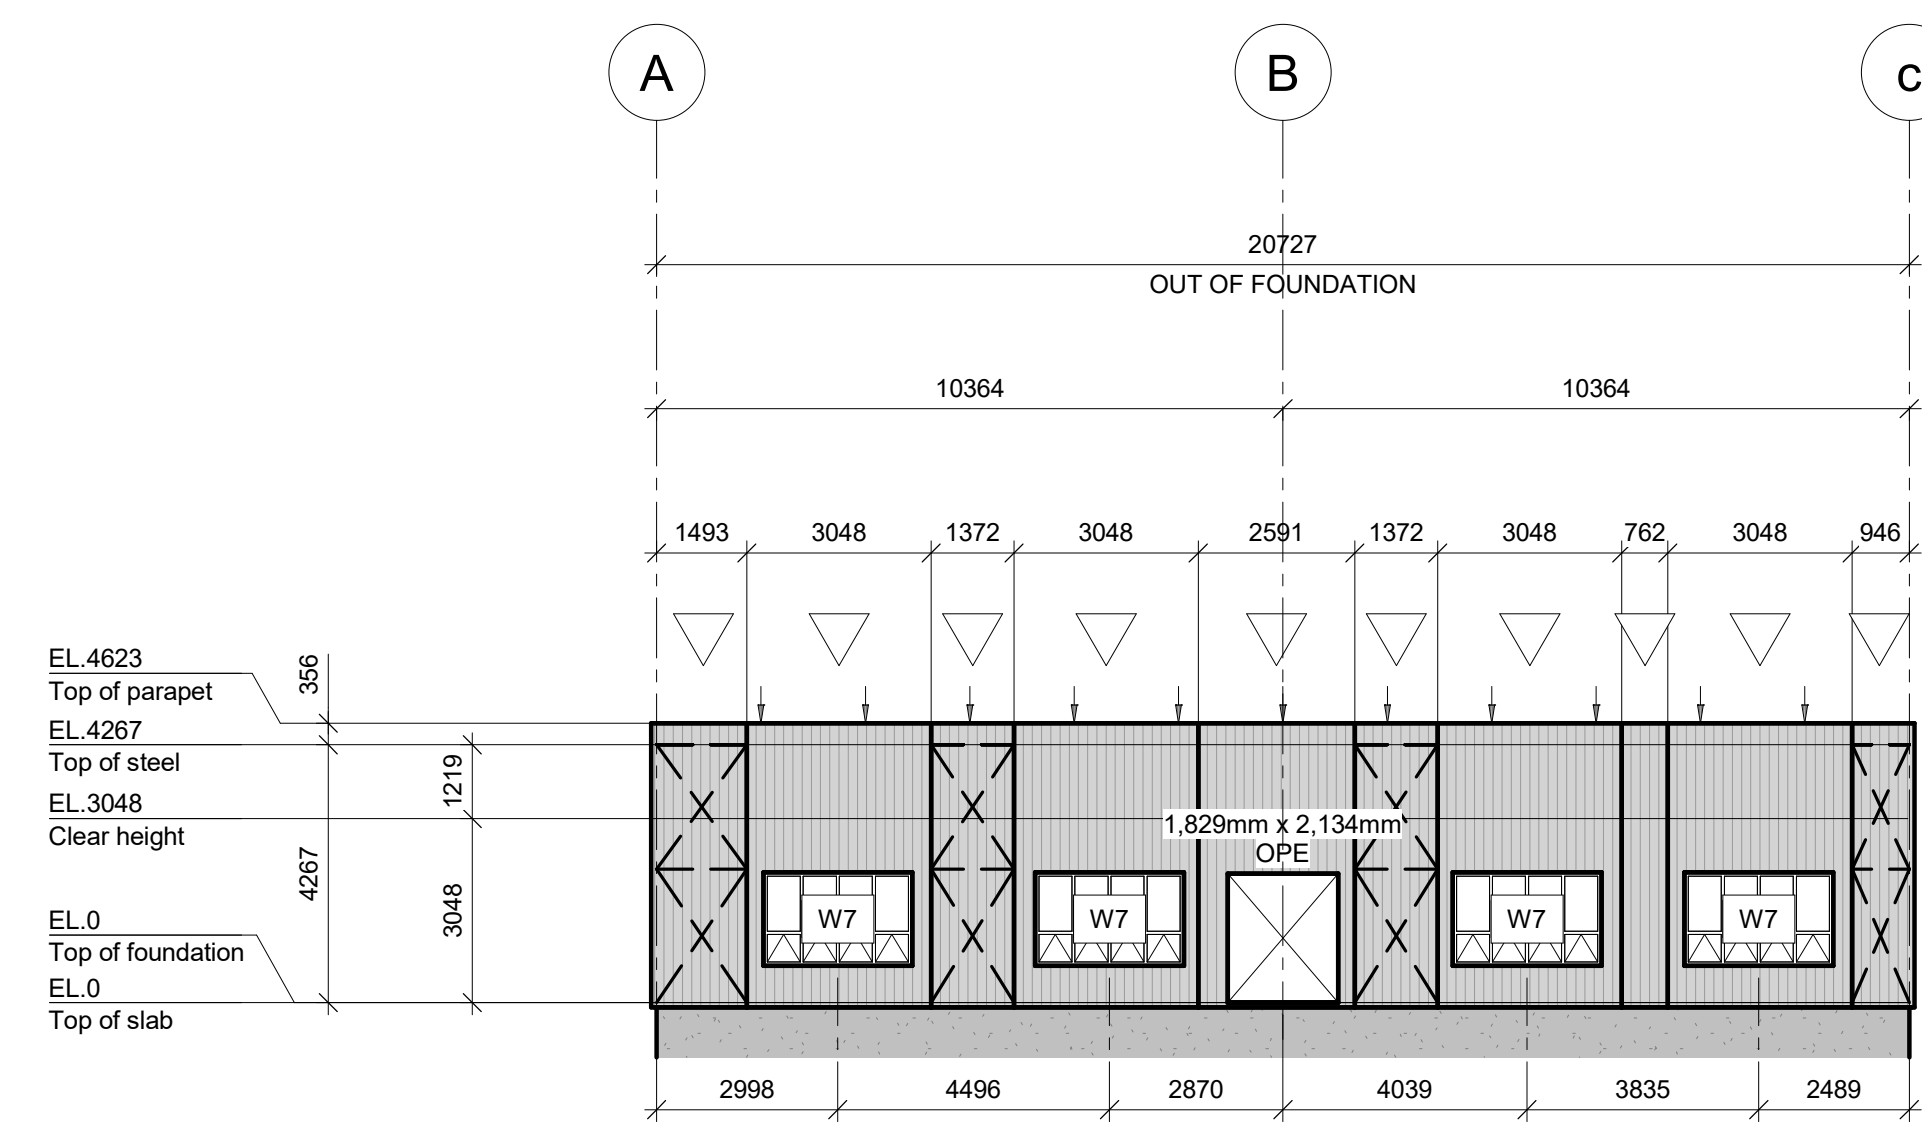

ELEVATION LINE 5 (EAST)  
1 : 125

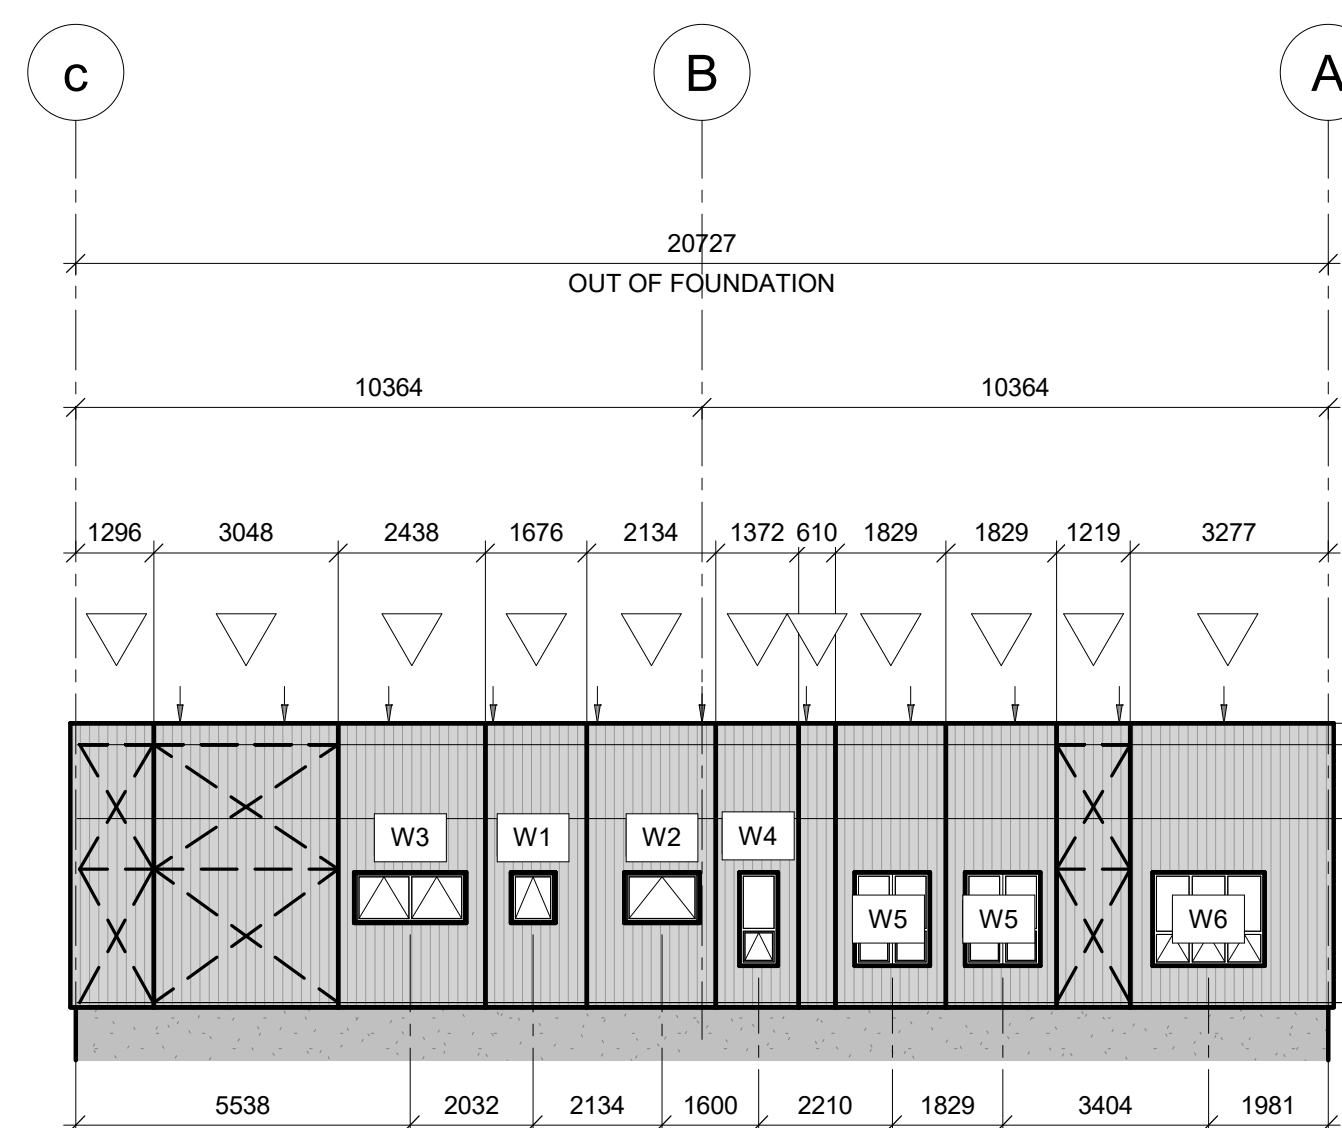

ELEVATION LINE 1 (WEST)

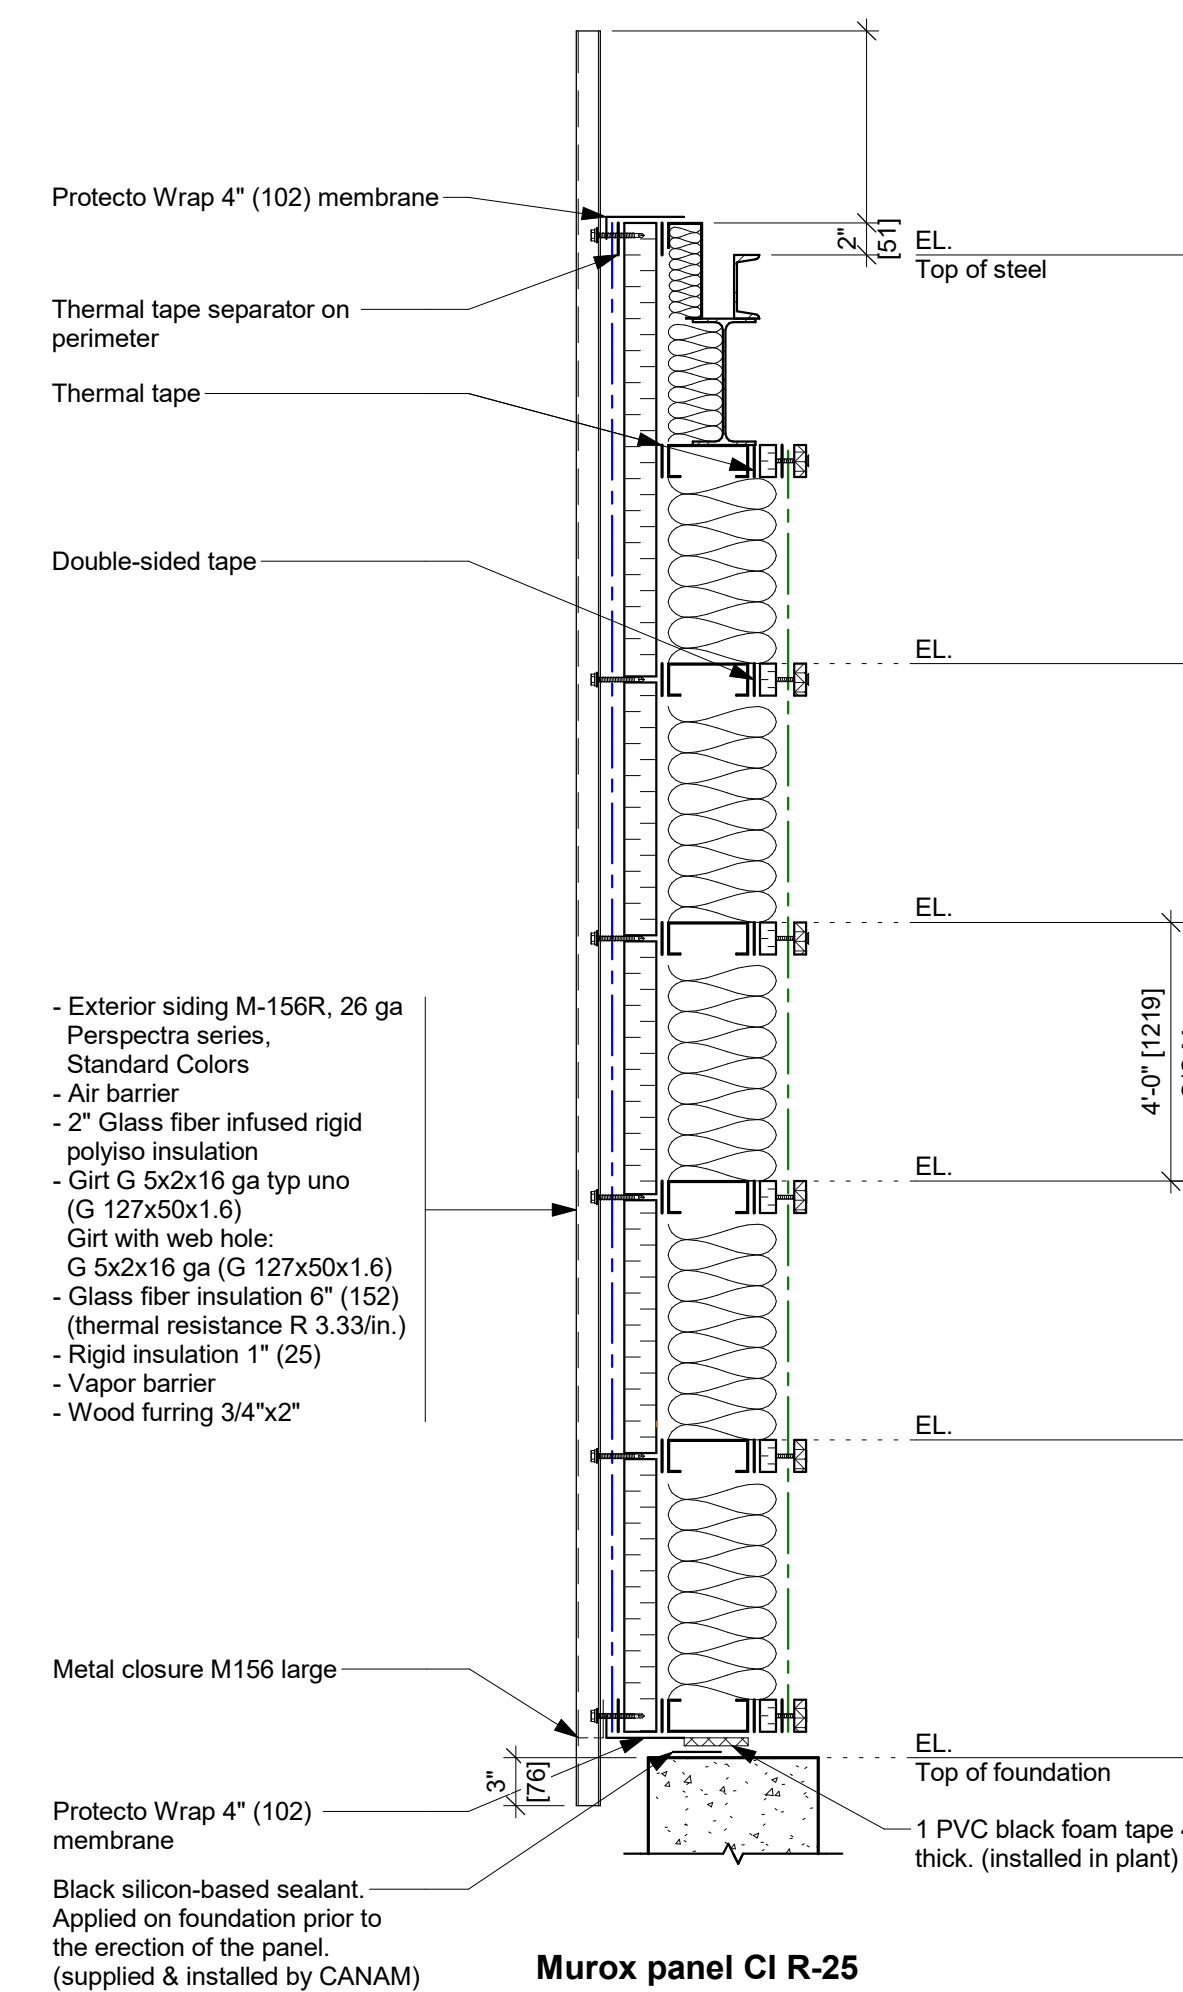

CONTRACTOR/ERECTOR NOTE:

IT IS PROHIBITED TO MODIFY, COPY, REPRODUCE OR OTHERWISE  
DISTRIBUTE THIS DRAWING OR ANY REPRESENTATION OF THIS  
DRAWING, OR ANY MEDIA, INCLUDING ELECTRONIC, WITHOUT THE  
PRIOR WRITTEN APPROVAL OF CANAM GROUP INC.

| REVISION        | DATE | DESCRIPTION | DESS | VER |
|-----------------|------|-------------|------|-----|
| PROJECT MANAGER |      |             |      |     |
|                 |      | -           |      |     |
|                 |      | -           |      |     |
DRAFTING:

|                   |                                   |                  |                                       |
|-------------------|-----------------------------------|------------------|---------------------------------------|
| DRAWN<br><br>J.P. | DESIGNED                          | PROJECT ENGINEER | SCALE:<br><br>Comme indiqu            |
| CHECKED           | CONSULTING ENGINEERS / ARCHITECTS |                  | DATE (yyyy/mm/dd) :<br><br>2026/07/28 |

CUSTOMER: Strong Bros.



11505, 1re Avenue, bureau 500, Saint-Georges Beauce  
Quebec, Canada, G5Y 7X3  
Phone : (418) 228-8031  
Toll free : (877) 499-6049  
[www.canam.com](http://www.canam.com)

PROFESSIONAL SEAL

PROJECT

DCC Site Office  
Kingston, Ontario

|  |               |
|--|---------------|
|  | DRAWING TITLE |
|--|---------------|

### PRELIMINARY SKETCH - ELEVATION, WALL SECTION AND SCHEDULES

|                              |                           |          |                                                                                                   |
|------------------------------|---------------------------|----------|---------------------------------------------------------------------------------------------------|
| CONTRACT NUMBER<br>P2026-142 | DRAWING NUMBER<br>EsMx501 | DIVISION | REVISION<br> |
|------------------------------|---------------------------|----------|---------------------------------------------------------------------------------------------------|