




METRIC

ALL DIMENSIONS SHOWN ARE
IN METRES AND/OR MILLIMETRES
UNLESS OTHERWISE NOTED.

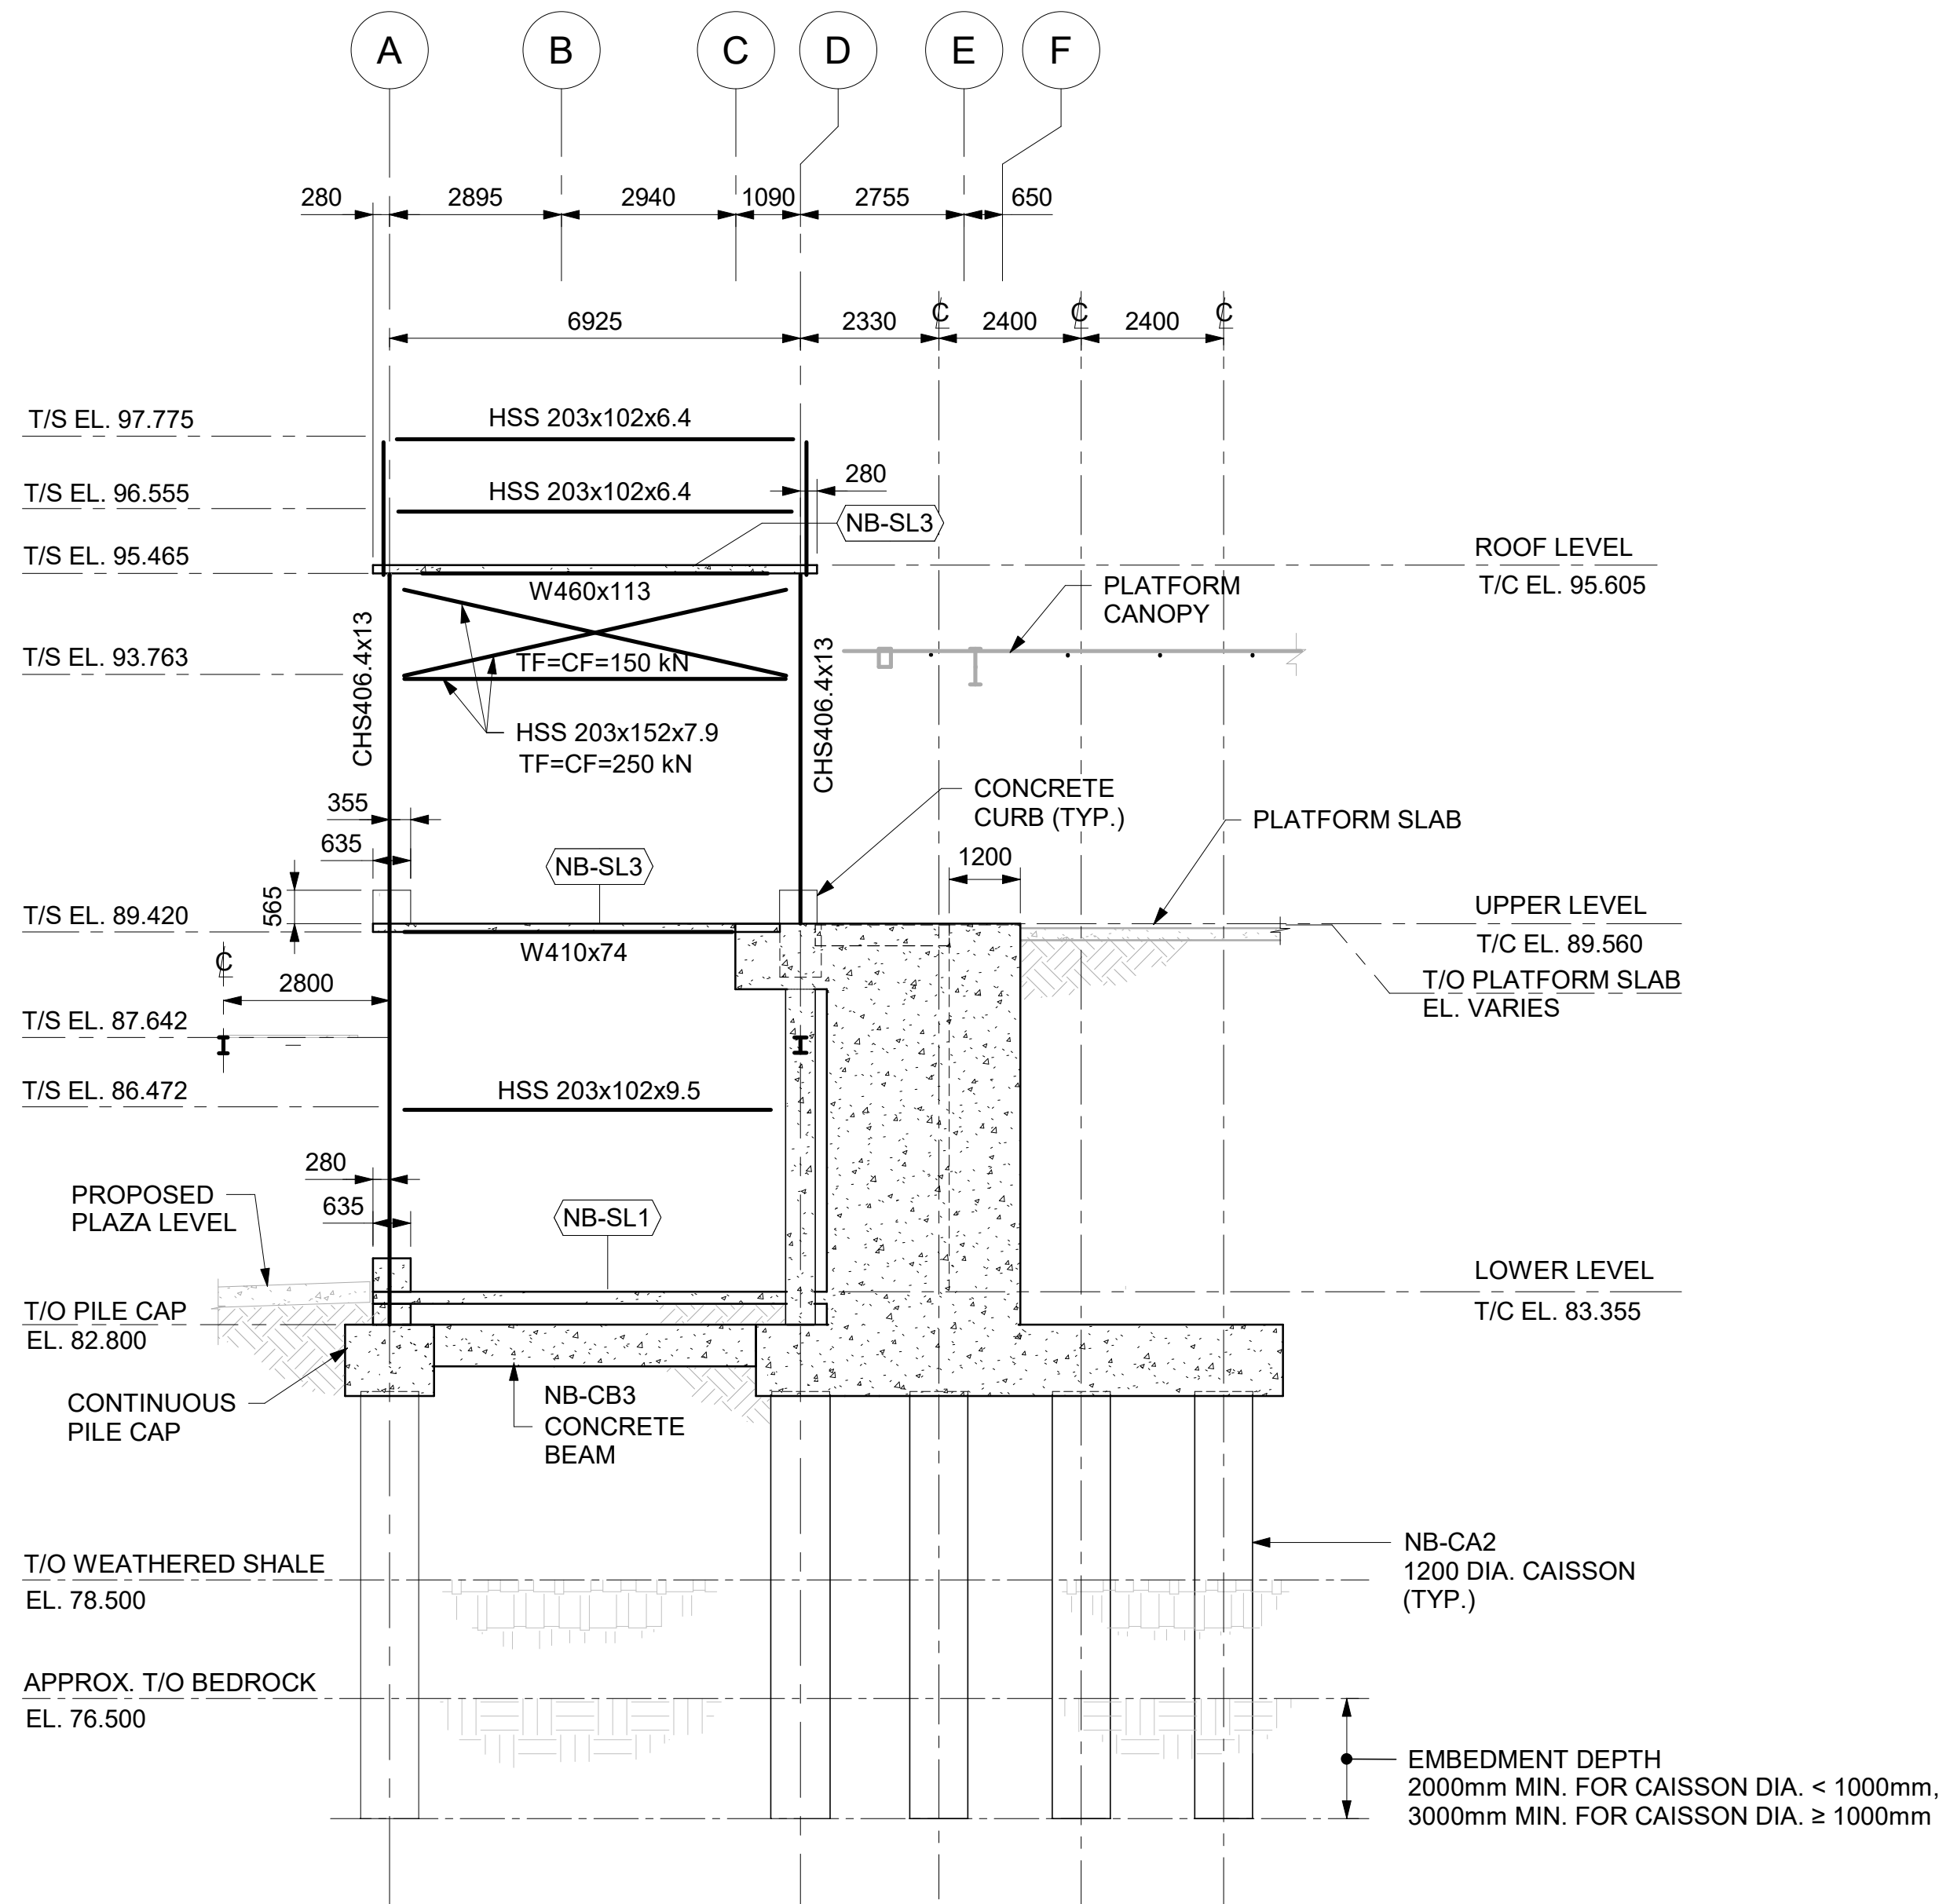


SECTION

LOOKING EAST

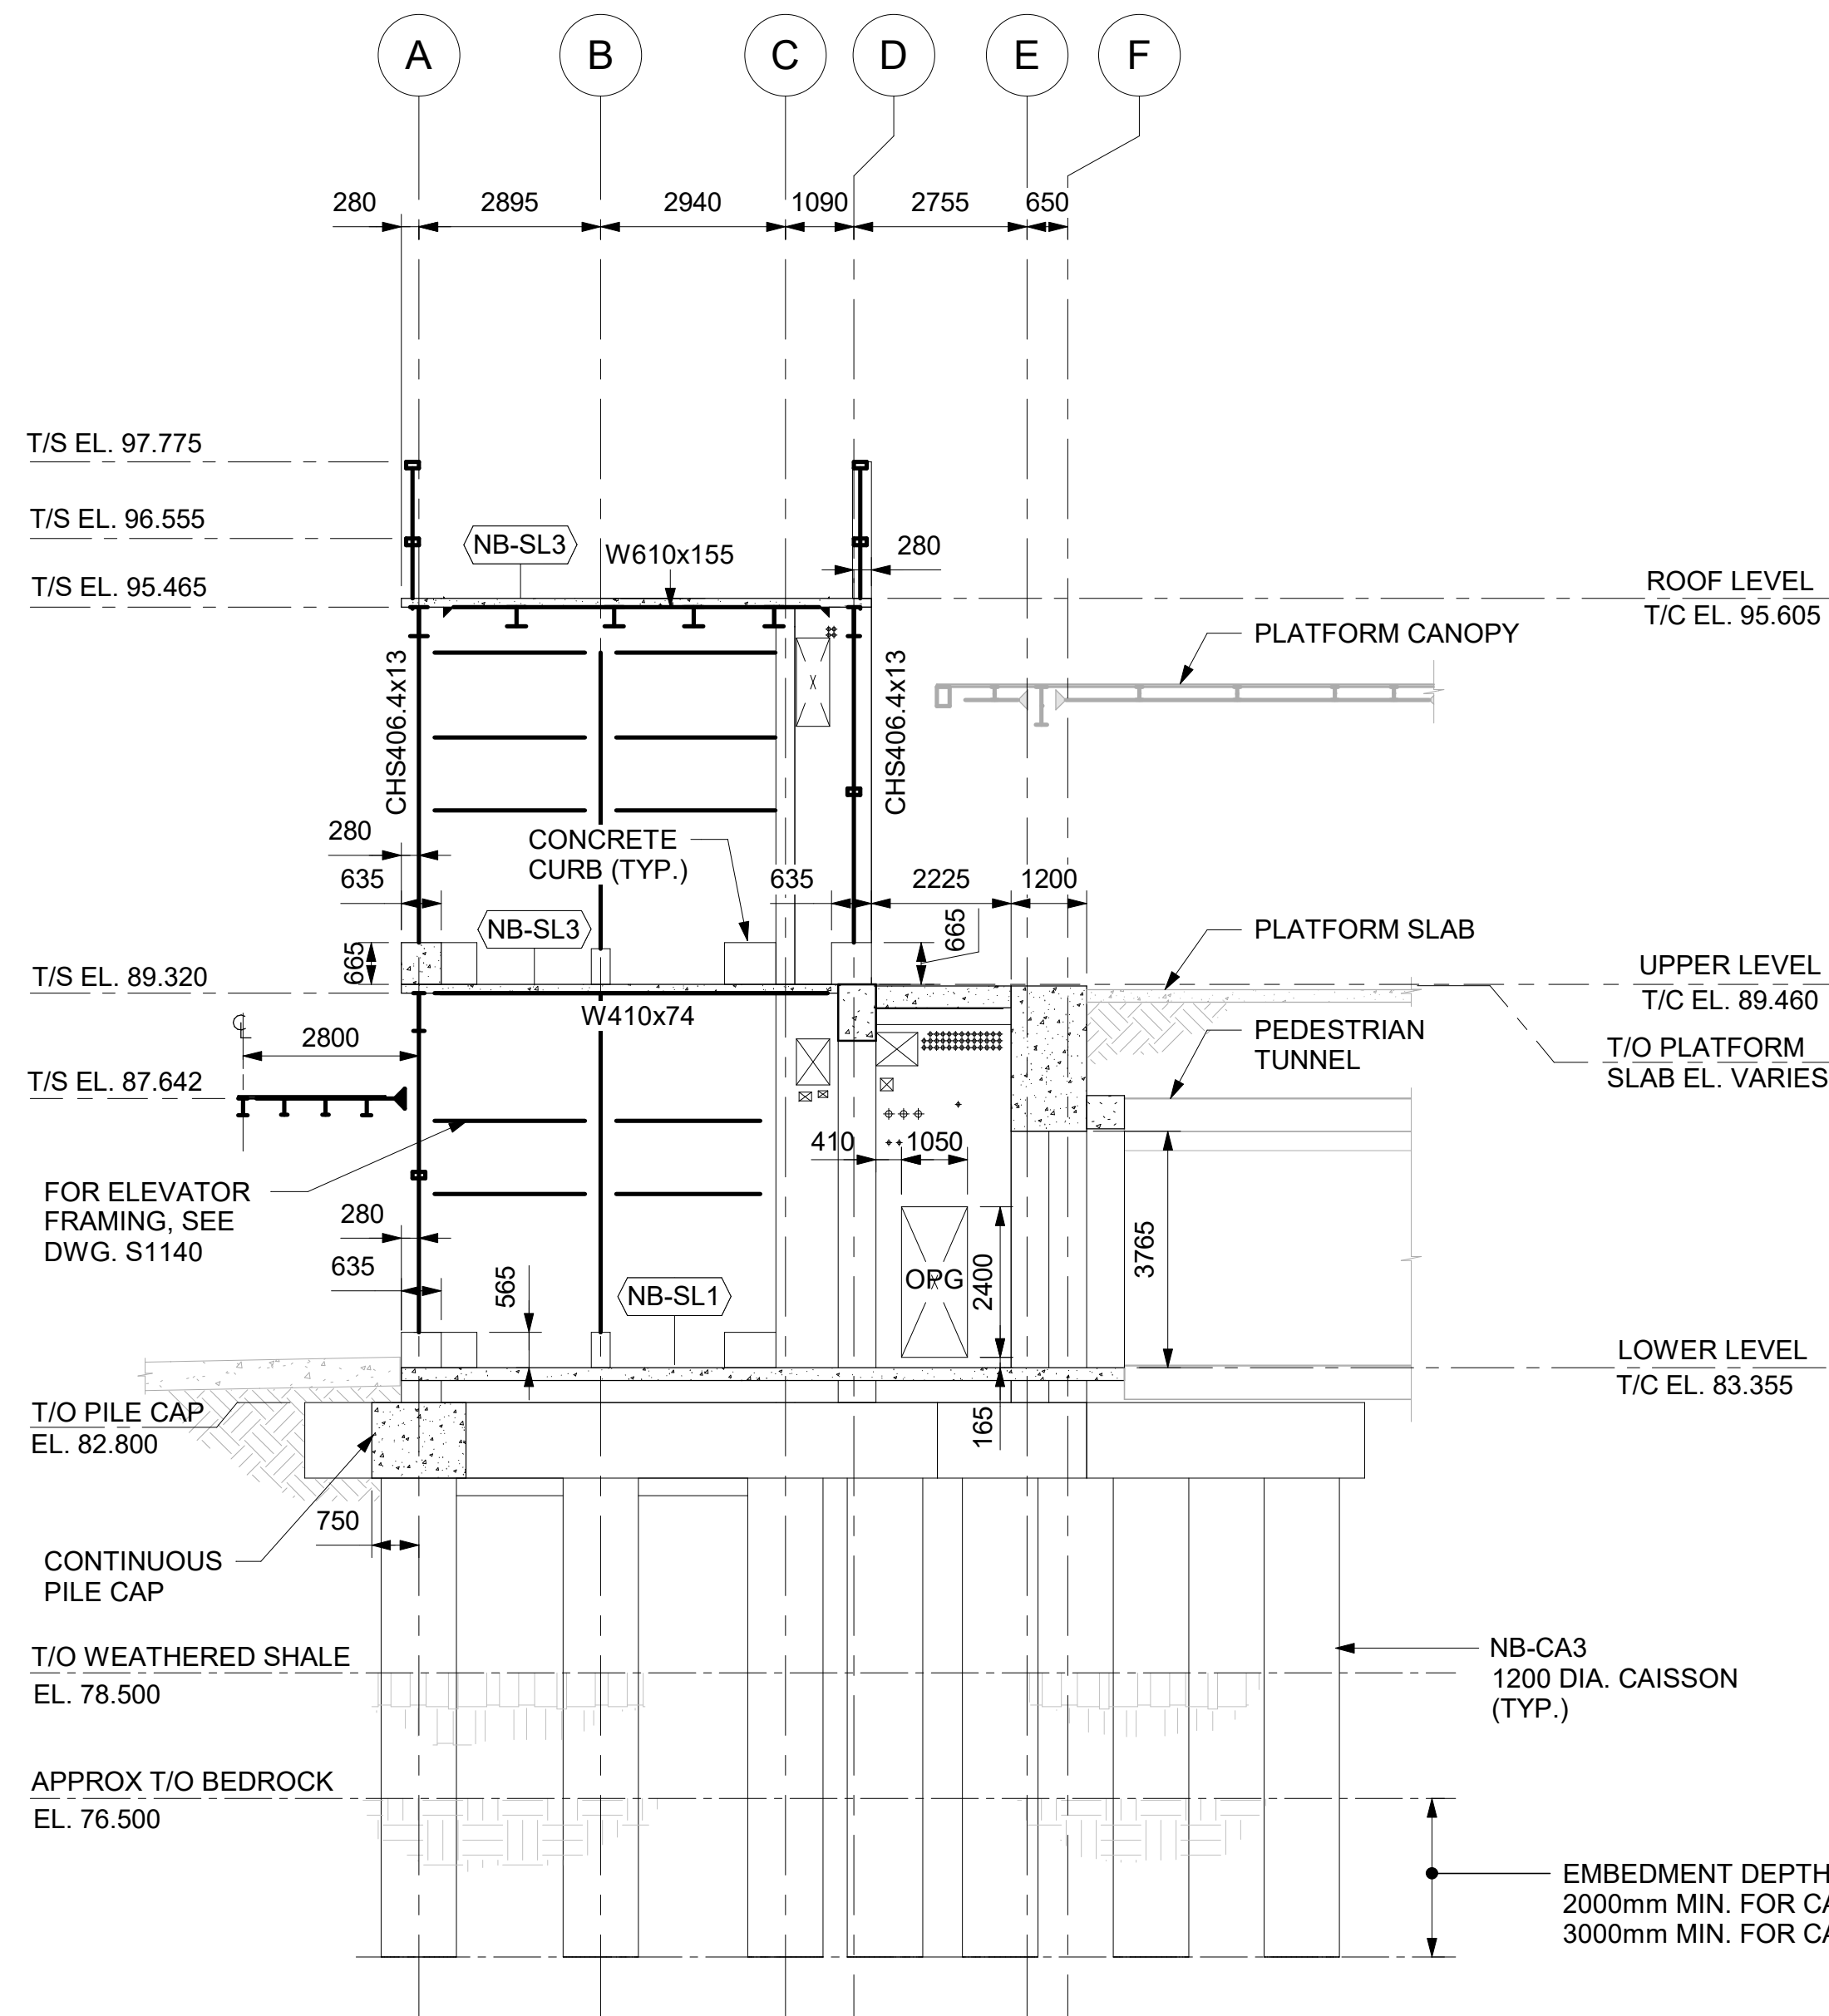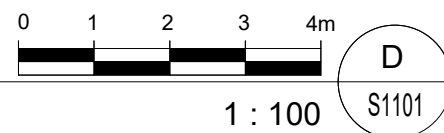

SECTION

LOOKING EAST

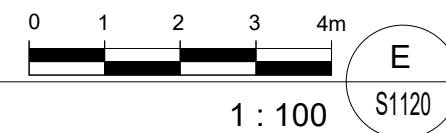

SLAB SCHEDULE

MARK	DESCRIPTION
NB-SL1	CIP SLAB 200mm
NB-SL2	CIP SLAB 350mm
NB-SL3	COMPOSITE DECK SLAB 140mm
NB-SL5	38mm METAL DECK
NB-SL6	CIP SLAB 400mm

NOTES:

- FOR GENERAL NOTES REFER TO DRAWING S0043.
- ALL OPENINGS, SLEEVES, CHASES ARE NOT NECESSARILY SHOWN ON THE STRUCTURAL DRAWINGS
- FOR OPENING SIZES AND LOCATIONS REFER TO ARCHITECTURAL, MECHANICAL, ELECTRICAL, VENTILATION, AND SYSTEMS DRAWINGS AND SPECIFICATIONS FOR OPENINGS AND SLEEVING REQUIREMENTS.

METROLINX PROJECT NO. 195701

PARK LAWN GO STATION
STRUCTURAL
NORTH STATION BUILDING
CROSS SECTION

CONTRACT NO.
195701

DWG. NO.
S1120

REV.
D

SHEET

THIS DRAWING WAS PREPARED FOR THE EXCLUSIVE USE OF LAKESHORE DEVELOPMENT INC. ("OWNERS") AND IS ISSUED PURSUANT TO THE RELEVANT AGREEMENT BETWEEN OWNERS AND HATCH LTD. ("HATCH") UNLESS OTHERWISE AGREED IN WRITING WITH OWNERS OR SPECIFIED ON THIS DRAWING.
(A) HATCH DOES NOT ACCEPT AND DISCLAIMS ANY AND ALL LIABILITY OR RESPONSIBILITY ARISING FROM ANY USE OF OR RELIANCE ON THIS DRAWING BY ANY THIRD PARTY OR ANY MODIFICATION OR MISUSE OF THIS DRAWING BY OWNERS, AND
(B) THIS DRAWING IS CONFIDENTIAL AND ALL INTELLECTUAL PROPERTY RIGHTS EMBODIED OR REFERENCED IN THIS DRAWING REMAIN THE PROPERTY OF HATCH.

12/2/2024 8:54:48 AM
BIM 360://H361249 - Park Lawn Go Station/H361249 - ISTA-SBR-MOD-0001.rvt

SHEET SIZE: ANSI D (34" x 22" 558.8mm x 863.6mm)

REFERENCE DRAWINGS

REVISIONS


DRAWN BY:
I.BALTAZAR
2022/02/08

DESIGNED BY:
A.DEHGHANI
2024/01/10

CHECKED BY:
A.FRANIC
2024/11/28

APPROVED BY:
A.PATON
2024/11/29

SCALE: 1:100 FULL SIZE ONLY

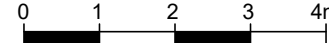

FIRST CAPITAL
Lakeshore Development Inc.

ISSUED FOR
BUILDING PERMIT

METROLINX
HATCH

CONTRACT NO.
195701

DWG. NO.
S1120

REV.
D

SHEET