
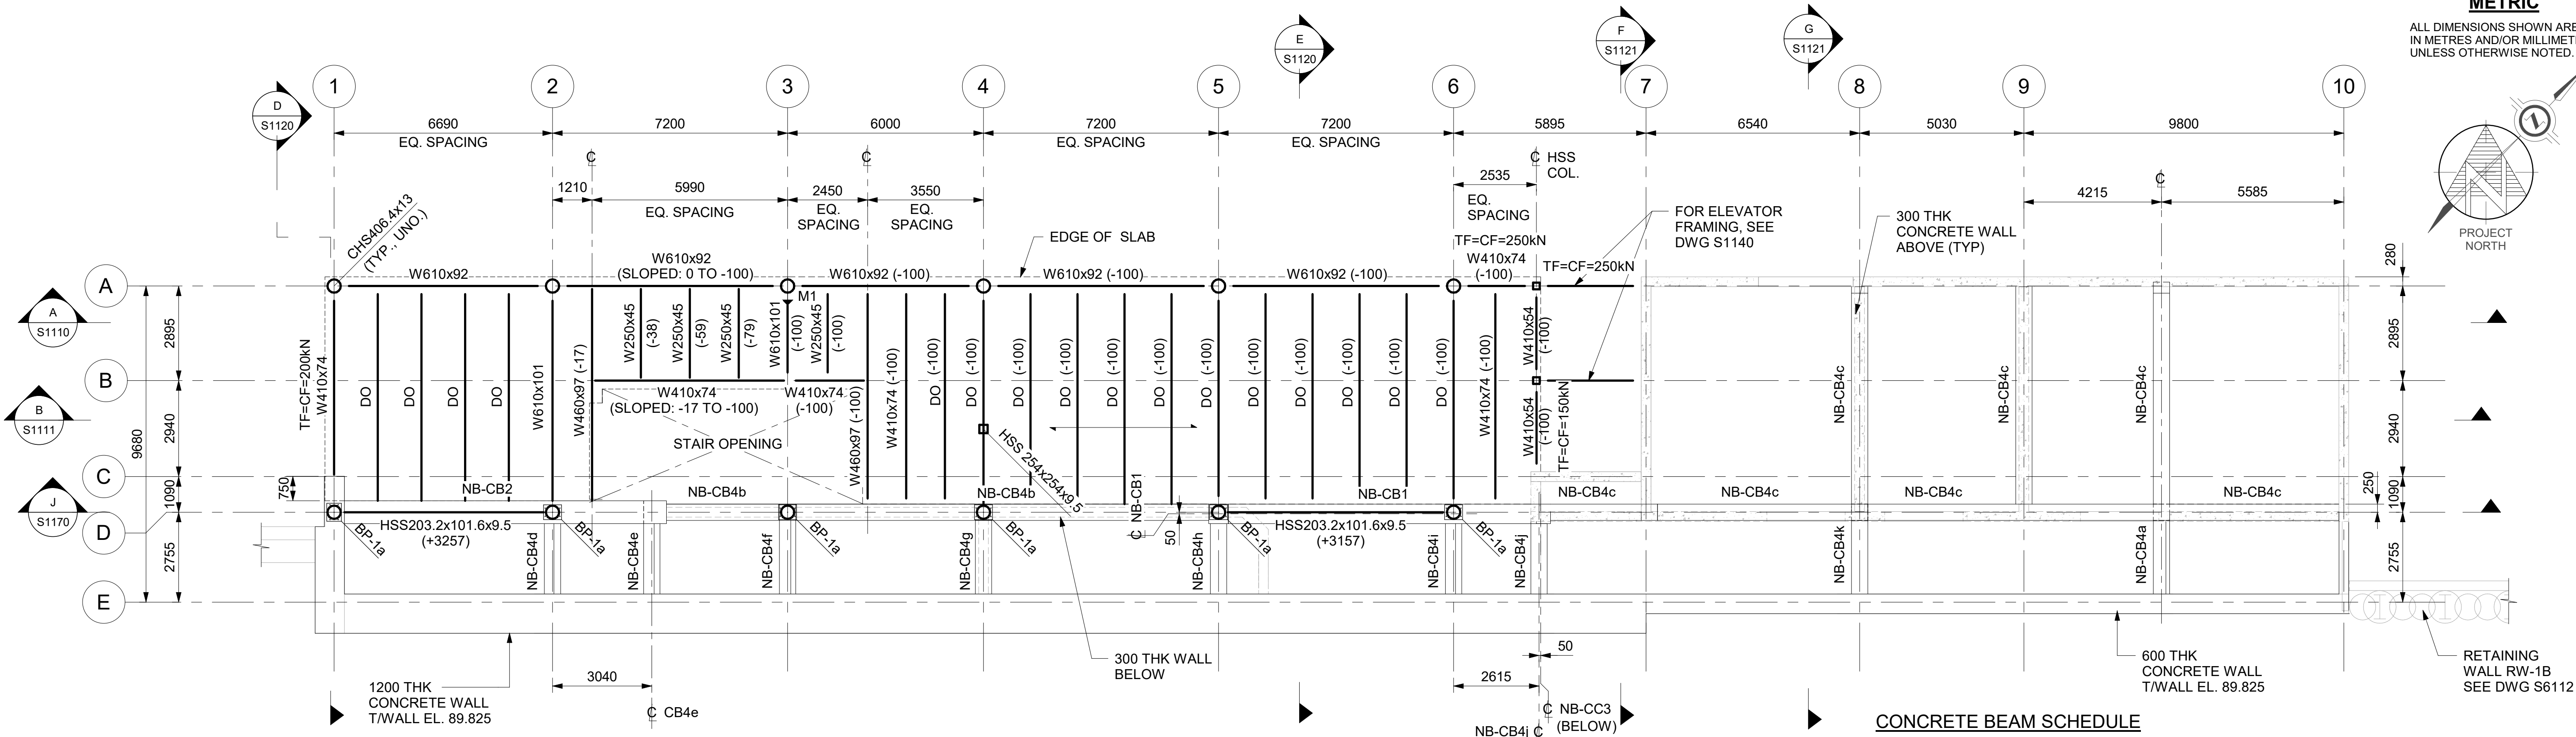


METRIC

ALL DIMENSIONS SHOWN ARE IN METRES AND/OR MILLIMETRES UNLESS OTHERWISE NOTED.

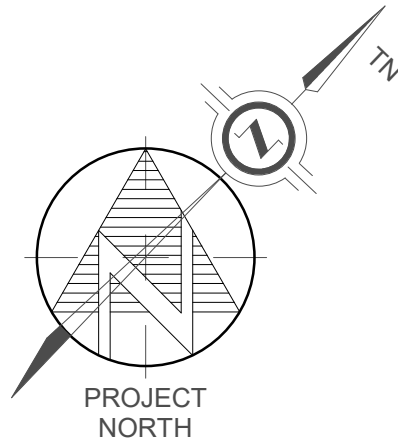

PLAN

FLOOR FRAMING PLAN AT T/S EL. 89.420 (H.P.)
UPPER LEVEL



CONCRETE BEAM SCHEDULE


MARK	SIZE (w x h)	TOP EL. (m)
NB-CB1	600x900	89.460
NB-CB2	700x900	89.560
NB-CB4a	500x600	89.340
NB-CB4b	500x600	89.460
NB-CB4c	500x600	89.570
NB-CB4d	500x600	89.517
NB-CB4e	500x600	89.506
NB-CB4f	500x600	89.491
NB-CB4g	500x600	89.460
NB-CB4h	500x600	89.444
NB-CB4i	500x600	89.418
NB-CB4j	500x600	89.409
NB-CB4k	500x600	89.375

NOTES:

- FOR GENERAL NOTES REFER TO DRAWING S0043.
- FOR TYPICAL EDGE BEAM DETAILS AROUND OPENINGS REFER TO DRAWING S0058. TO SEE OPENINGS ON THE ROOF SEE S1101A.
- DESIGN ALL BEAM TO COLUMN CONNECTION FOR CF = TF = 100 kN UNLESS OTHERWISE NOTED.
- FOR MOMENT CONNECTIONS SEE THE TABLE. THE AMOUNT OF MOMENT CONNECTIONS WHICH ARE NOT INDICTED ARE 75 kN-M.

M1	300 kN-M
M2	200 kN-M

KEY PLAN

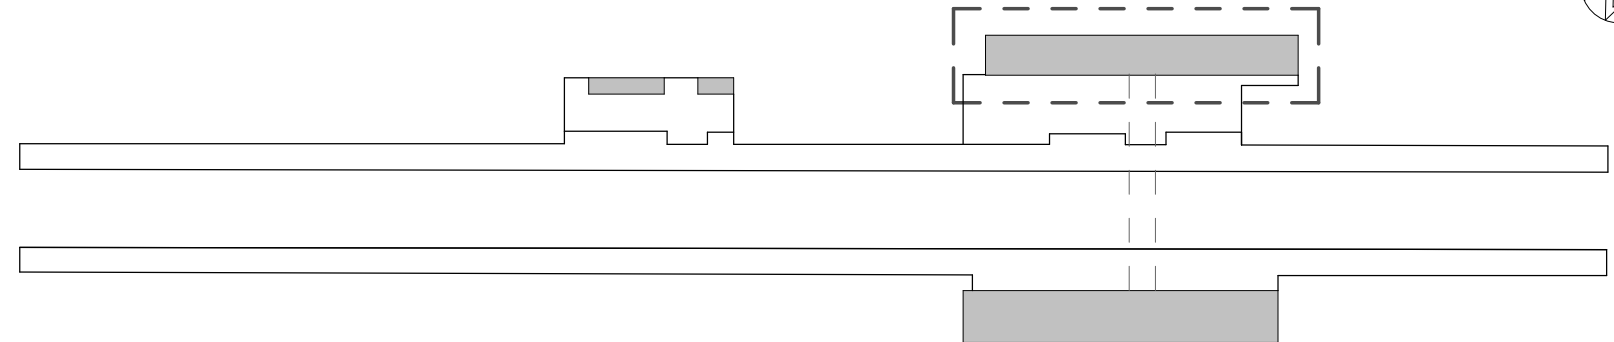


METROLINX PROJECT NO. 195701




PARK LAWN GO STATION
STRUCTURAL
NORTH STATION BUILDING
PLAN AT T/S EL. 89.935 - UPPER LEVEL

CONTRACT NO. 195701	DWG. NO. S1102	REV. D	SHEET
------------------------	-------------------	-----------	-------

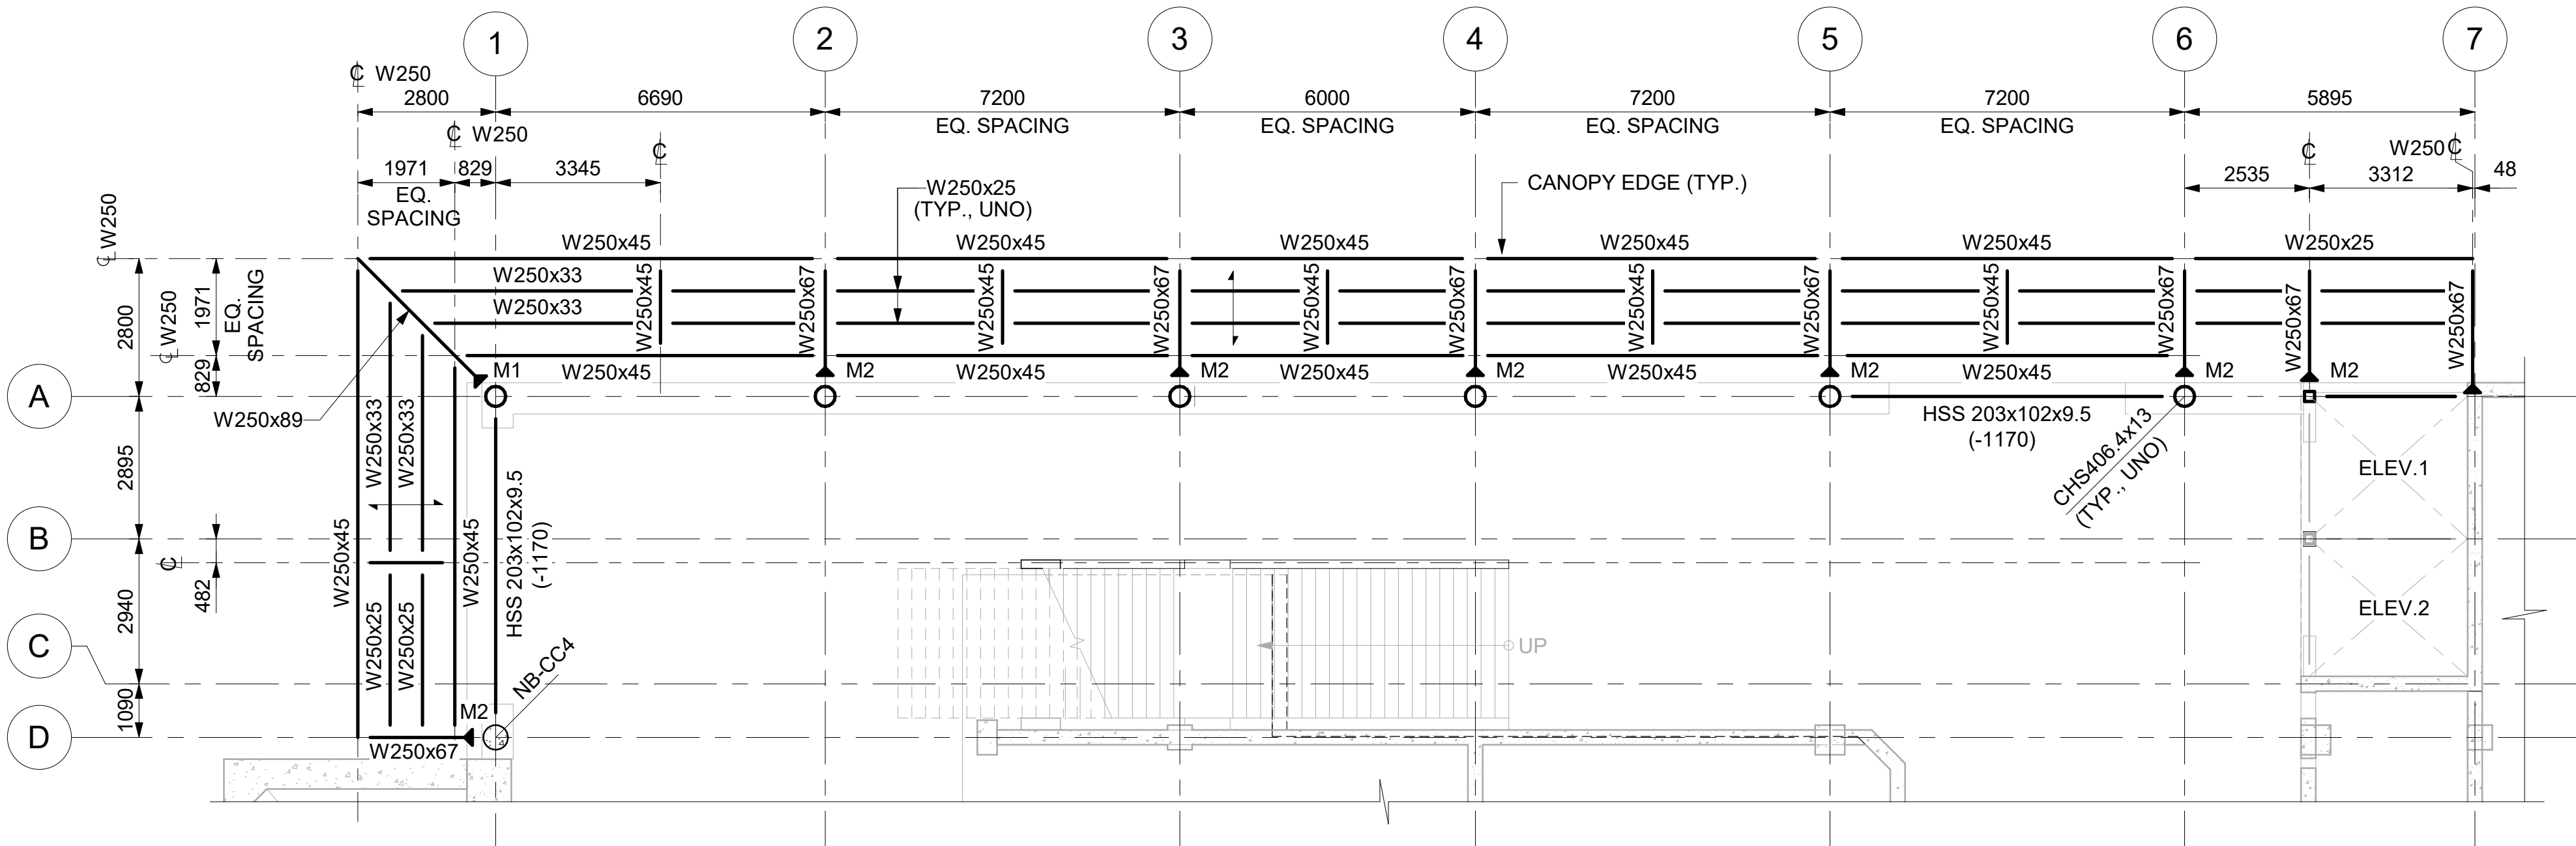

PARTIAL PLAN

NORTH ENTRANCE CANOPY FRAMING PLAN
AT T/S EL. 87.642

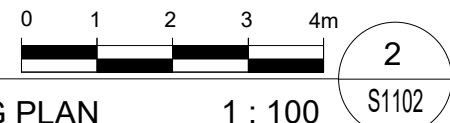

REFERENCE DRAWINGS

REVISIONS

DRAWN BY:
I.BALTAZAR
2022/02/07

DESIGNED BY:
A.DEHGHANI
2024/01/10

CHECKED BY:
A.FRANIC
2024/11/28

APPROVED BY:
A.PATON
2024/11/29

SCALE: 1:100 FULL SIZE ONLY



FIRST CAPITAL
Lakeshore Development Inc.

ISSUED FOR
BUILDING PERMIT

12/2/2024 8:54:35 AM
BIM 360://H361249 - Park Lawn Go Station/H361249-1STA-SBR-MOD-0001.rvt

SHEET SIZE: ANSI D (34" x 22" 558.8mm x 863.6mm)

THIS DRAWING WAS PREPARED FOR THE EXCLUSIVE USE OF LAKESHORE DEVELOPMENT INC. (OWNERS') AND IS ISSUED PURSUANT TO THE RELEVANT AGREEMENT BETWEEN OWNERS AND HATCH LTD. ("HATCH") UNLESS OTHERWISE AGREED IN WRITING WITH OWNERS OR SPECIFIED ON THIS DRAWING. (A) HATCH DOES NOT ACCEPT AND DISCLAIMS ANY AND ALL LIABILITY OR RESPONSIBILITY ARISING FROM ANY USE OF OR RELIANCE ON THIS DRAWING BY ANY THIRD PARTY OR ANY MODIFICATION OR MISUSE OF THIS DRAWING BY OWNERS, AND (B) THIS DRAWING IS CONFIDENTIAL AND ALL INTELLECTUAL PROPERTY RIGHTS EMBODIED OR REFERENCED IN THIS DRAWING REMAIN THE PROPERTY OF HATCH.