


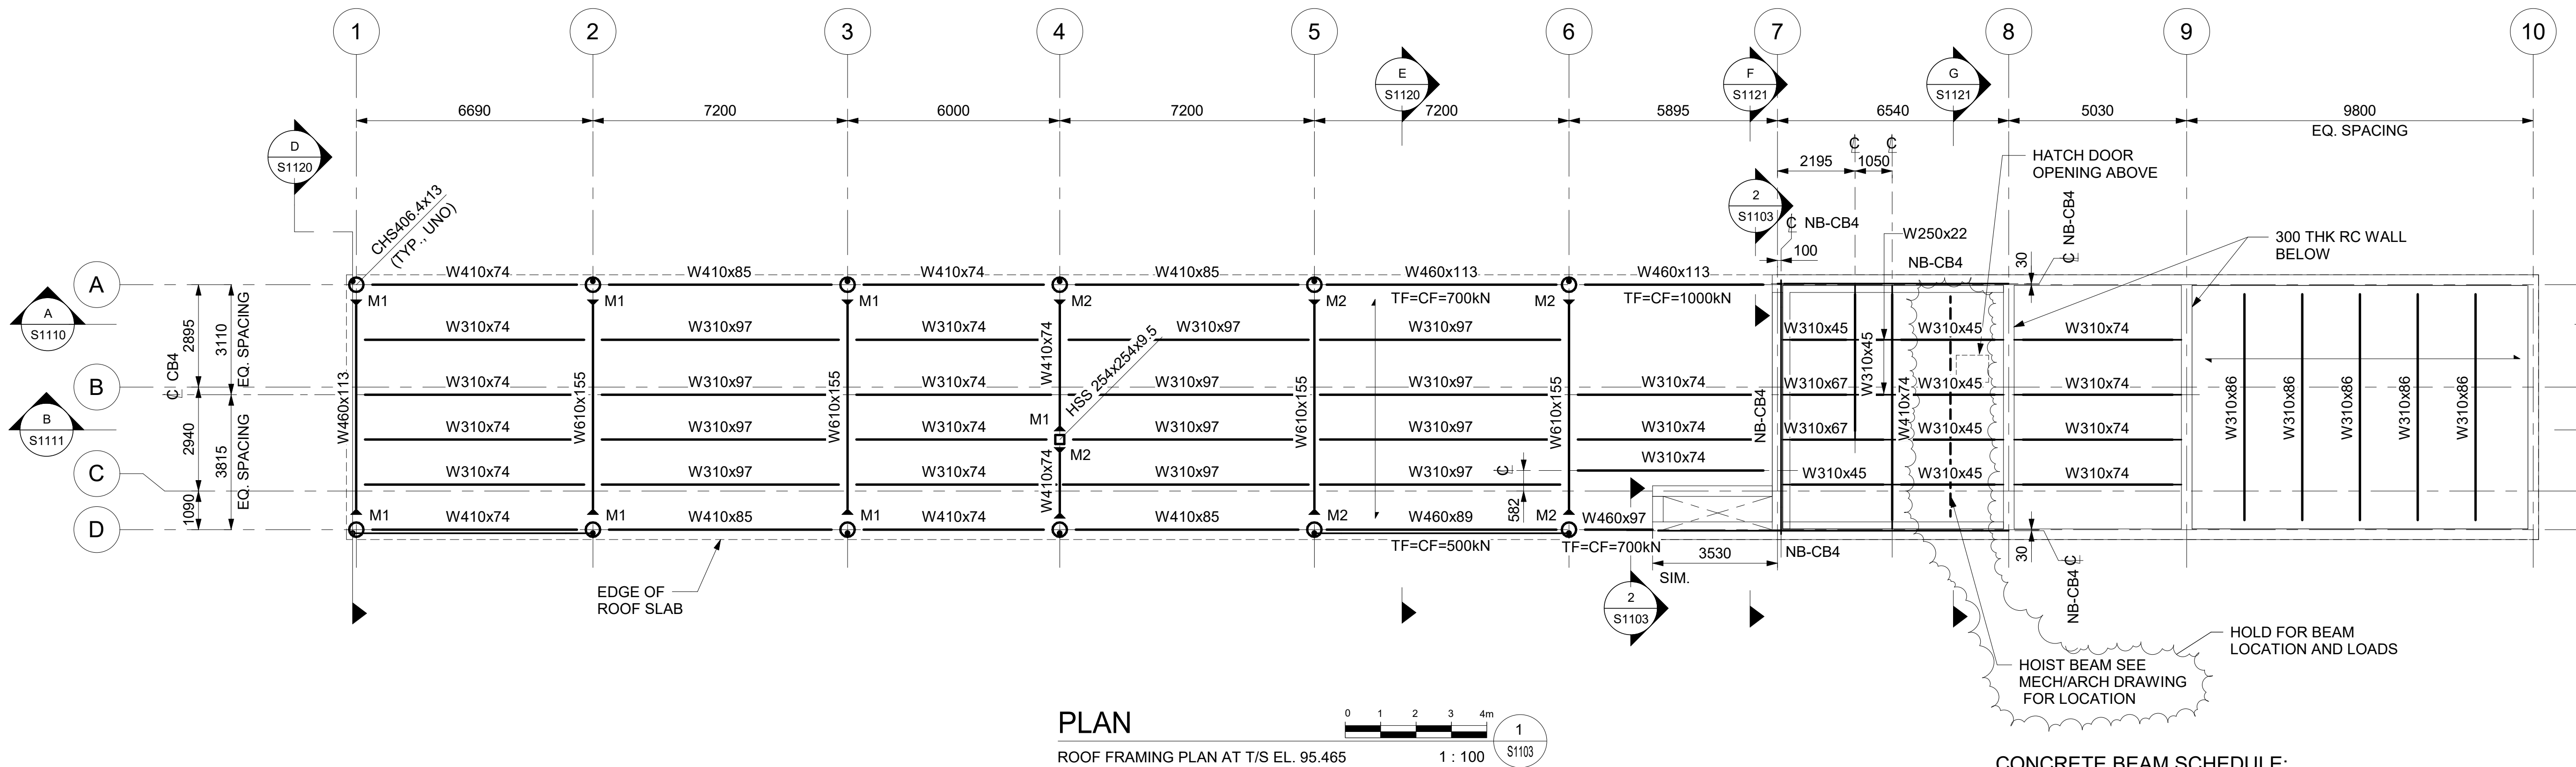

CONCRETE BEAM SCHEDULE:


MARK	SIZE (w x h)	TOP EL. (m)
NB-CB4	500x600	95.605

NOTES:

- FOR GENERAL NOTES REFER TO DRAWING S0043.
- FOR TYPICAL EDGE BEAM DETAILS AROUND OPENINGS REFER TO DRAWING S0058. TO SEE OPENINGS ON THE ROOF SEE S1101B.
- DESIGN ALL BEAM TO COLUMN CONNECTION FOR CF = TF = 300 kN UNLESS OTHERWISE NOTED.
- FOR MOMENT CONNECTIONS SEE THE TABLE. THE AMOUNT OF MOMENT CONNECTIONS WHICH ARE NOT INDICTED ARE 75 kN-M.

M1	300 kN-M
M2	250 kN-M

KEY PLAN

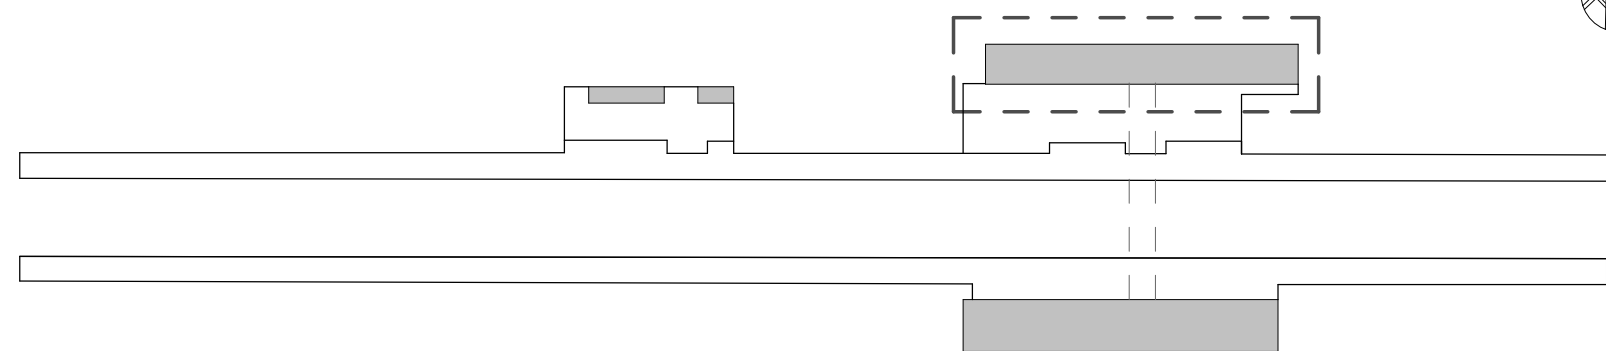

METROLINX PROJECT NO. 195701



PARK LAWN GO STATION
STRUCTURAL
NORTH STATION BUILDING
ROOF FRAMING PLAN AT T/S EL 95.815

CONTRACT NO. 195701	DWG. NO. S1103	REV. D	SHEET
------------------------	-------------------	-----------	-------

REFERENCE DRAWINGS

REVISIONS

DRAWN BY:
I.BALTAZAR
2022/02/08

DESIGNED BY:
A.DEHGHANI
2024/01/10

CHECKED BY:
A.FRANIC
2024/11/28

APPROVED BY:
A.PATON
2024/11/29

SCALE: 1:100 FULL SIZE ONLY



FIRST
CAPITAL
Lakeshore Development Inc.

ISSUED FOR
BUILDING PERMIT

12/2/2024 8:54:39 AM
BIM 360://H361249 - Park Lawn Go Station/H361249 - ISTA-SBR-MOD-0001.rvt

SHEET SIZE: ANSI D (34" x 22" 558.8mm x 863.6mm)

THIS DRAWING WAS PREPARED FOR THE EXCLUSIVE USE OF LAKESHORE DEVELOPMENT INC. ("OWNERS") AND IS ISSUED PURSUANT TO THE RELEVANT AGREEMENT BETWEEN OWNERS AND HATCH LTD. ("HATCH") UNLESS OTHERWISE AGREED IN WRITING WITH OWNERS OR SPECIFIED ON THIS DRAWING. (A) HATCH DOES NOT ACCEPT AND DISCLAIMS ANY AND ALL LIABILITY OR RESPONSIBILITY ARISING FROM ANY USE OF OR RELIANCE ON THIS DRAWING BY ANY THIRD PARTY OR ANY MODIFICATION OR MISUSE OF THIS DRAWING BY OWNERS. AND (B) THIS DRAWING IS CONFIDENTIAL AND ALL INTELLECTUAL PROPERTY RIGHTS EMBODIED OR REFERENCED IN THIS DRAWING REMAIN THE PROPERTY OF HATCH.