



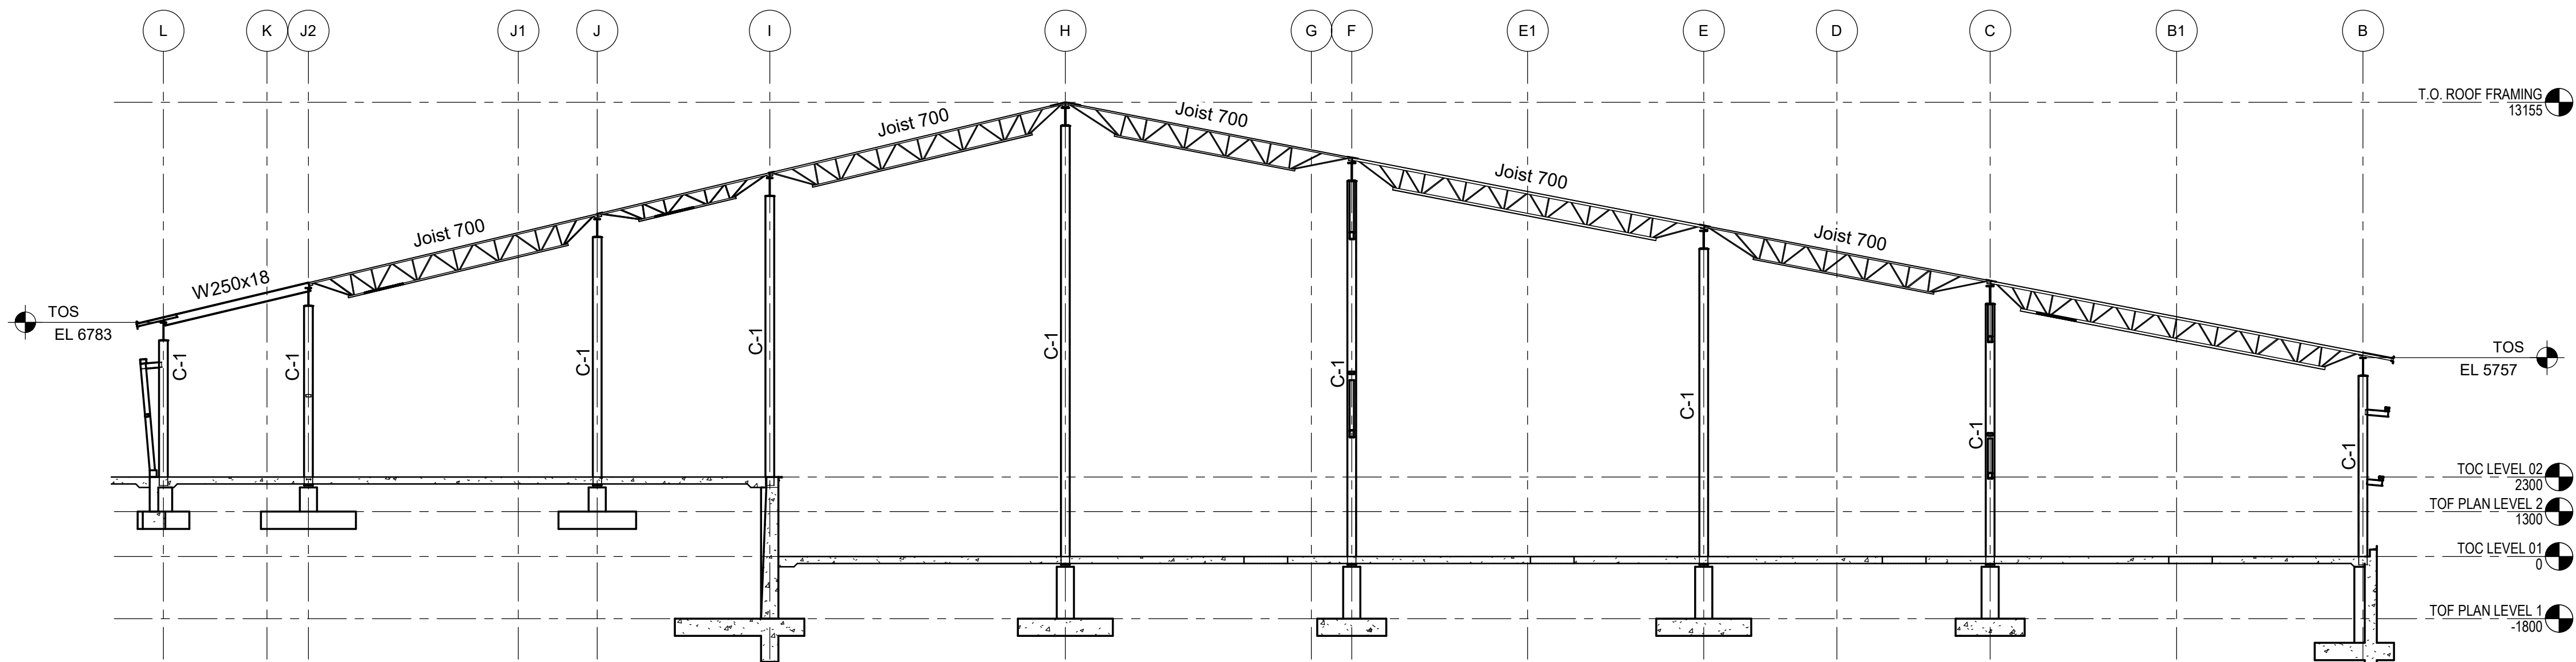

1 BUILDING SECTION (NEAR GL 4)
S-101 1: 125

NOTE: THIS SECTION IS TYPICAL FOR S-102, S-103, S-104

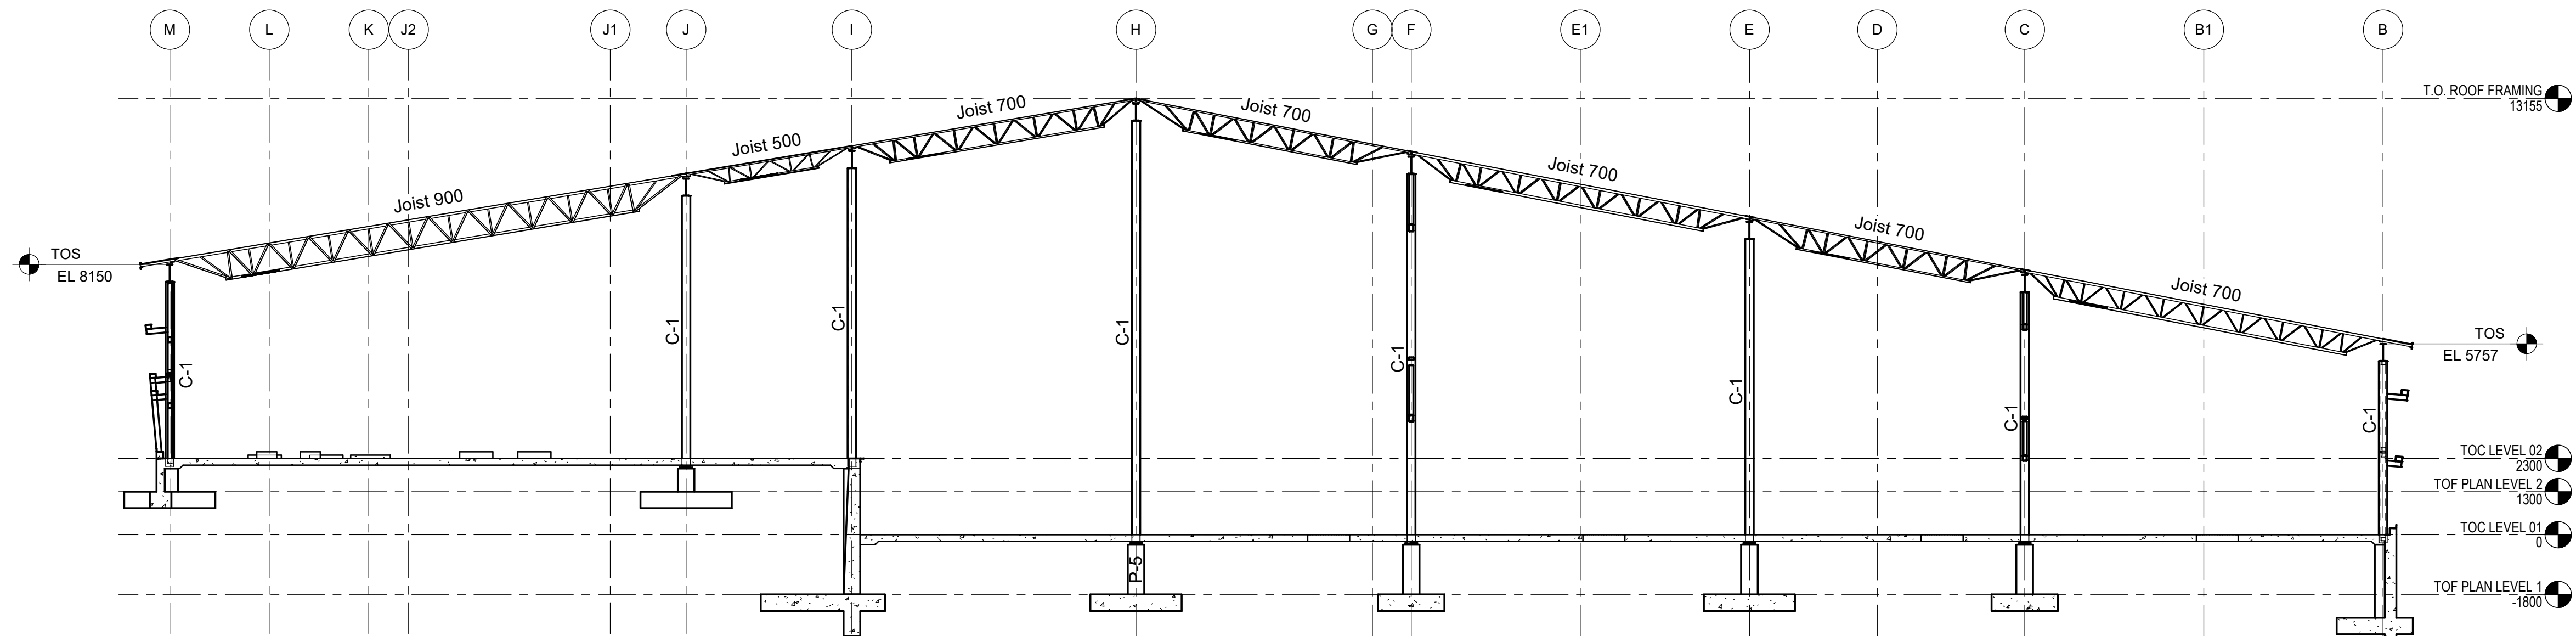

2 BUILDING SECTION (NEAR GL 8)
S-101 1: 125


NOTE: THIS SECTION IS TYPICAL FOR S-102, S-103, S-104

NOTES

- FOR NOTES SEE DWG S-201.

2023/02/10	1	ISSUED FOR TENDER	BC	MRM/AD
DATE	REV.	DESCRIPTION	DRAWN BY	CHECKED BY

CONSULTANT

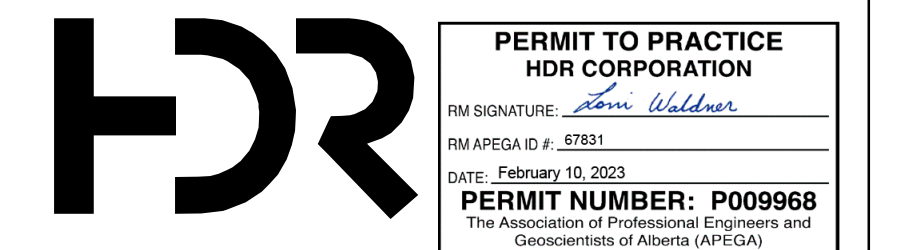

PROJECT

**CAROLINE - NEW RAVEN CREEK BROOD
TROUT STATION, CONSTRUCTION**

TITLE

BUILDING SECTIONS

SEAL	DRAWN BY BC	CHECKED BY MRM/AD	SCALE 1 : 125
DATE 2023/02/10	SITE ID S0654	BUILDING ID	
PLAN NO. 020791E	PHASE DD	DISCIPLINE S	
PROJECT ID. P-004974.01	SHEET NO. S-301		

DOCUMENT CODE