


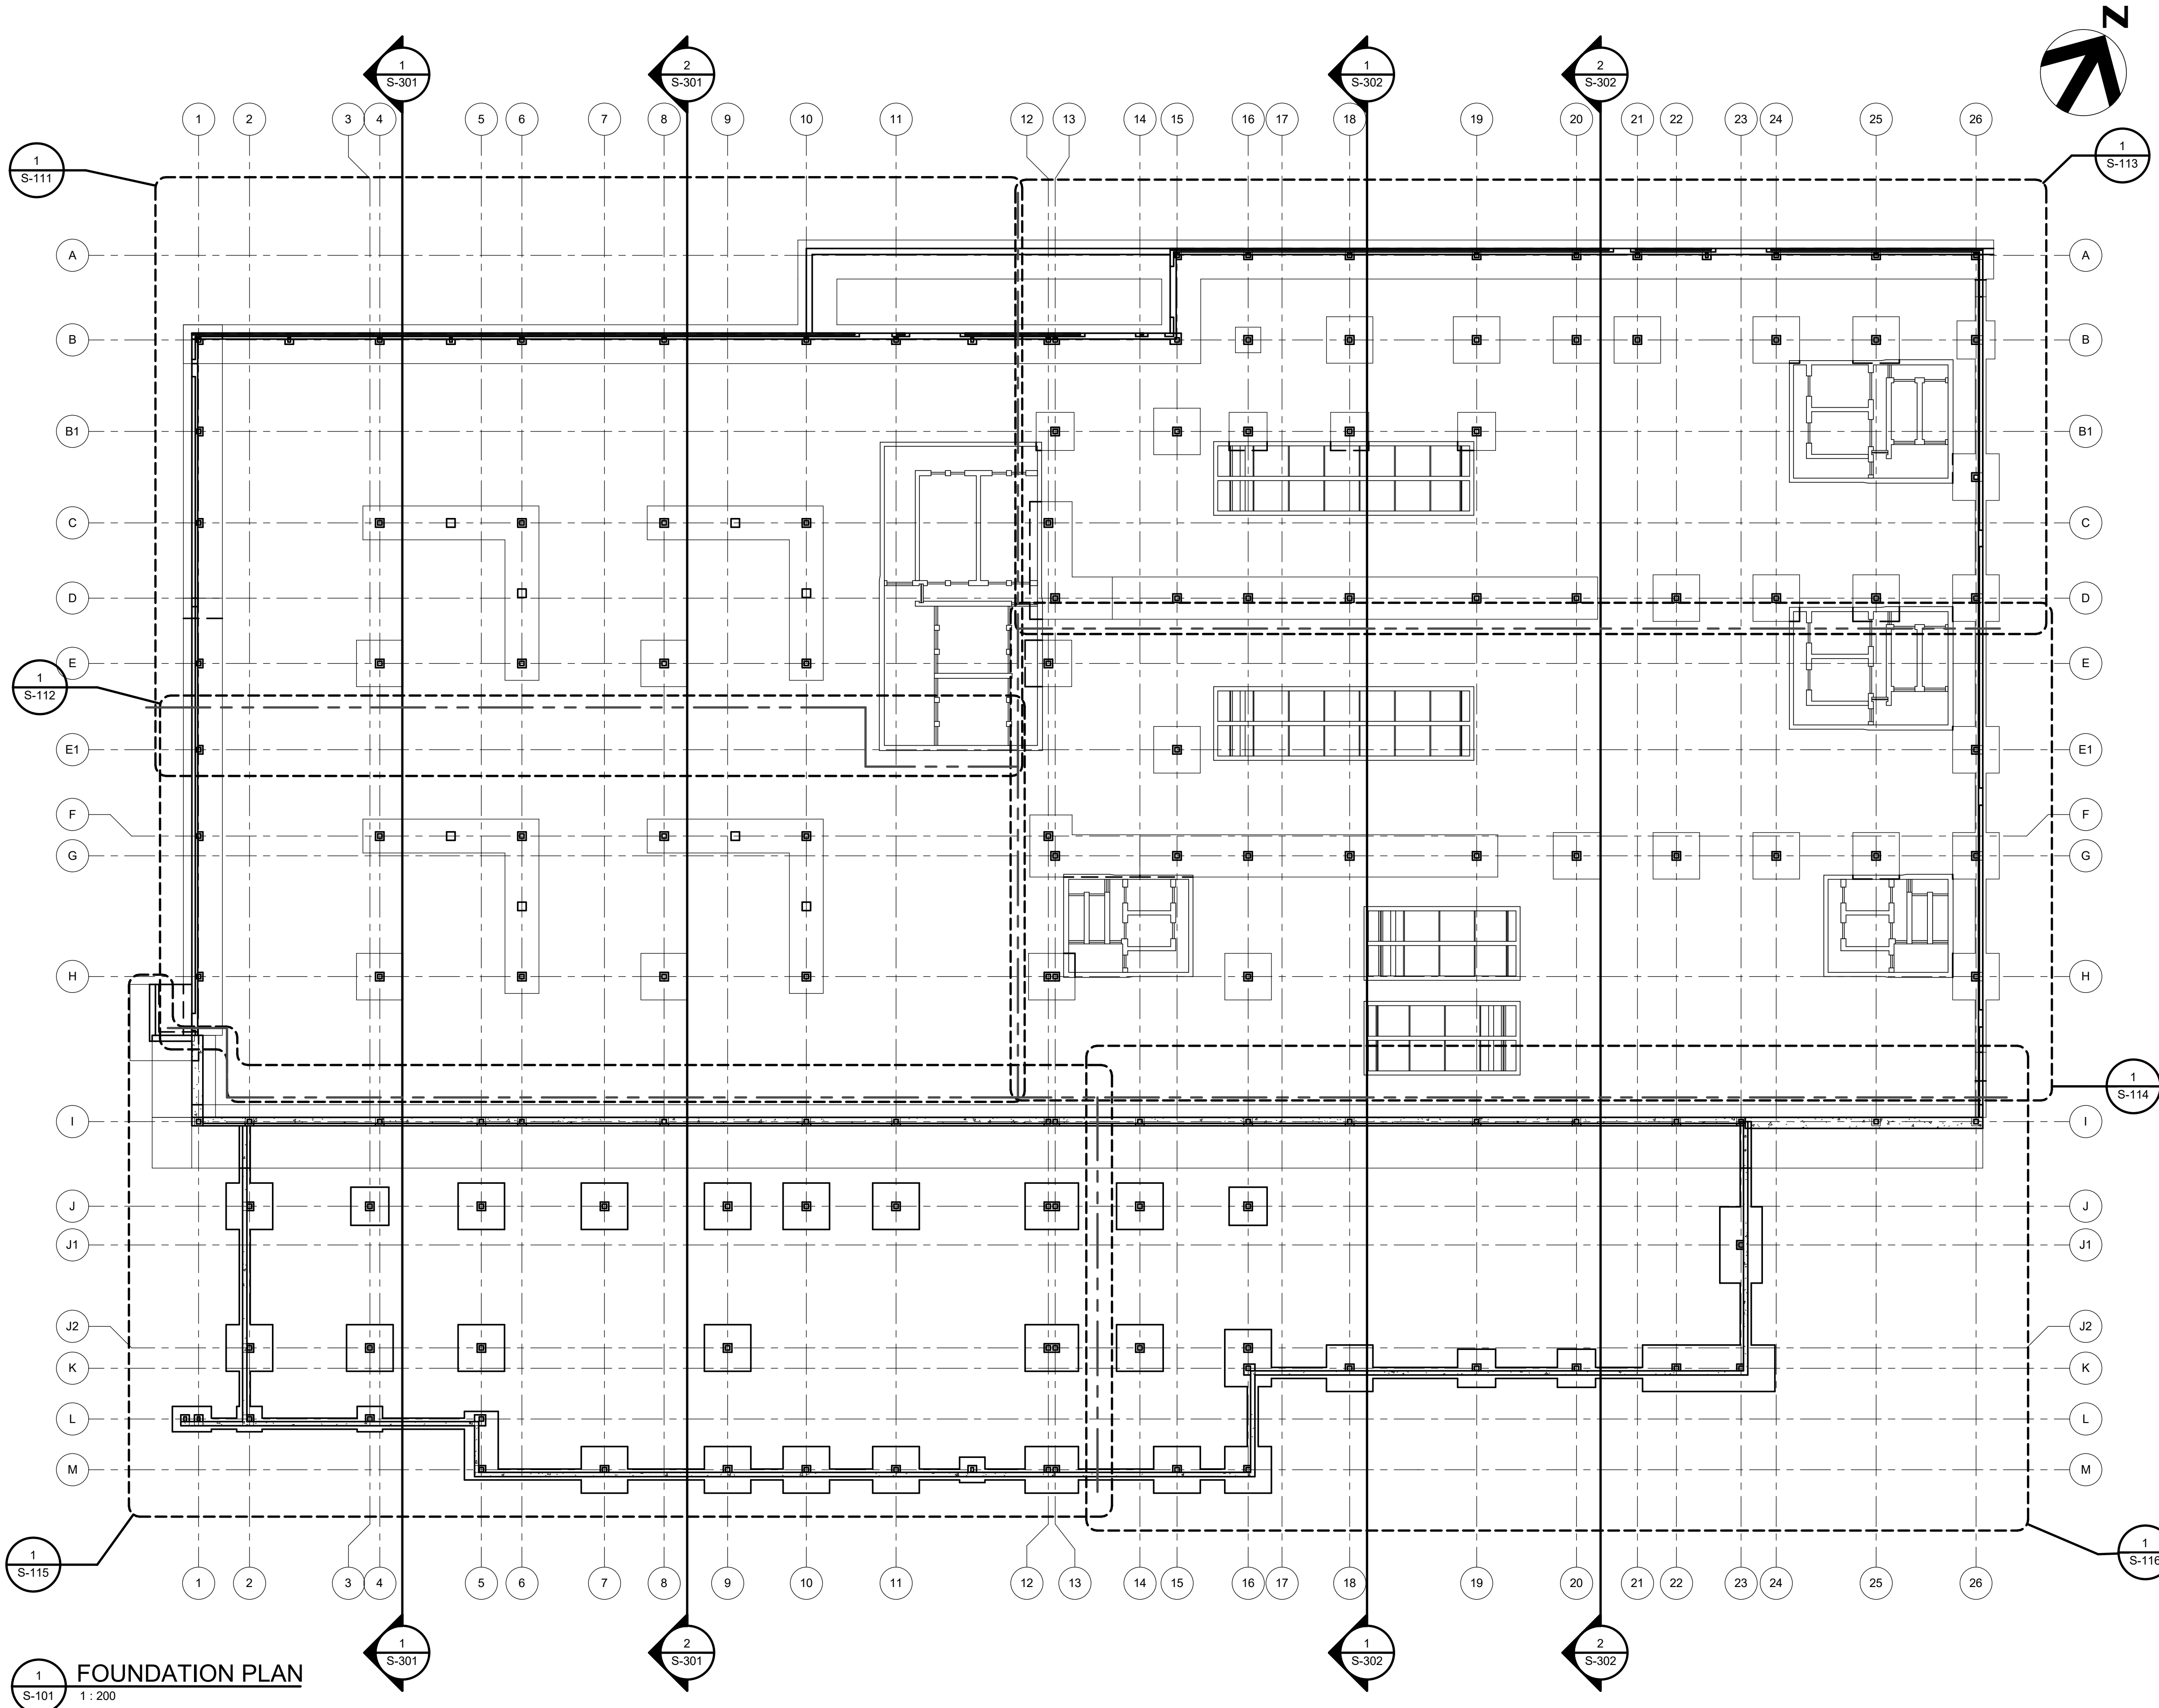

1 FOUNDATION PLAN
S-101 1 : 200

KEY PLAN

NOTES

2023/02/10	1	ISSUED FOR TENDER	BC	MRM/AD
DATE	REV.	DESCRIPTION	DRAWN BY	CHECKED BY

CONSULTANT

PERMIT TO PRACTICE
HDR CORPORATION
RM SIGNATURE: *[Signature]*
RM APEGA ID #: 27831
DATE: February 10, 2023
PERMIT NUMBER: P009968
The Association of Professional Engineers and Geoscientists of Alberta (APEGA)

PROJECT

CAROLINE - NEW RAVEN CREEK BROOD
TROUT STATION, CONSTRUCTION

TITLE

FOUNDATION - KEY PLAN

SEAL

DRAWN BY BC	CHECKED BY MRM/AD	SCALE 1 : 200
DATE 2023/02/10	SITE ID S0654	BUILDING ID
PLAN NO. 020791E	PHASE DD	DISCIPLINE S
PROJECT ID. P-004974.01		SHEET NO. S-101

DOCUMENT CODE