




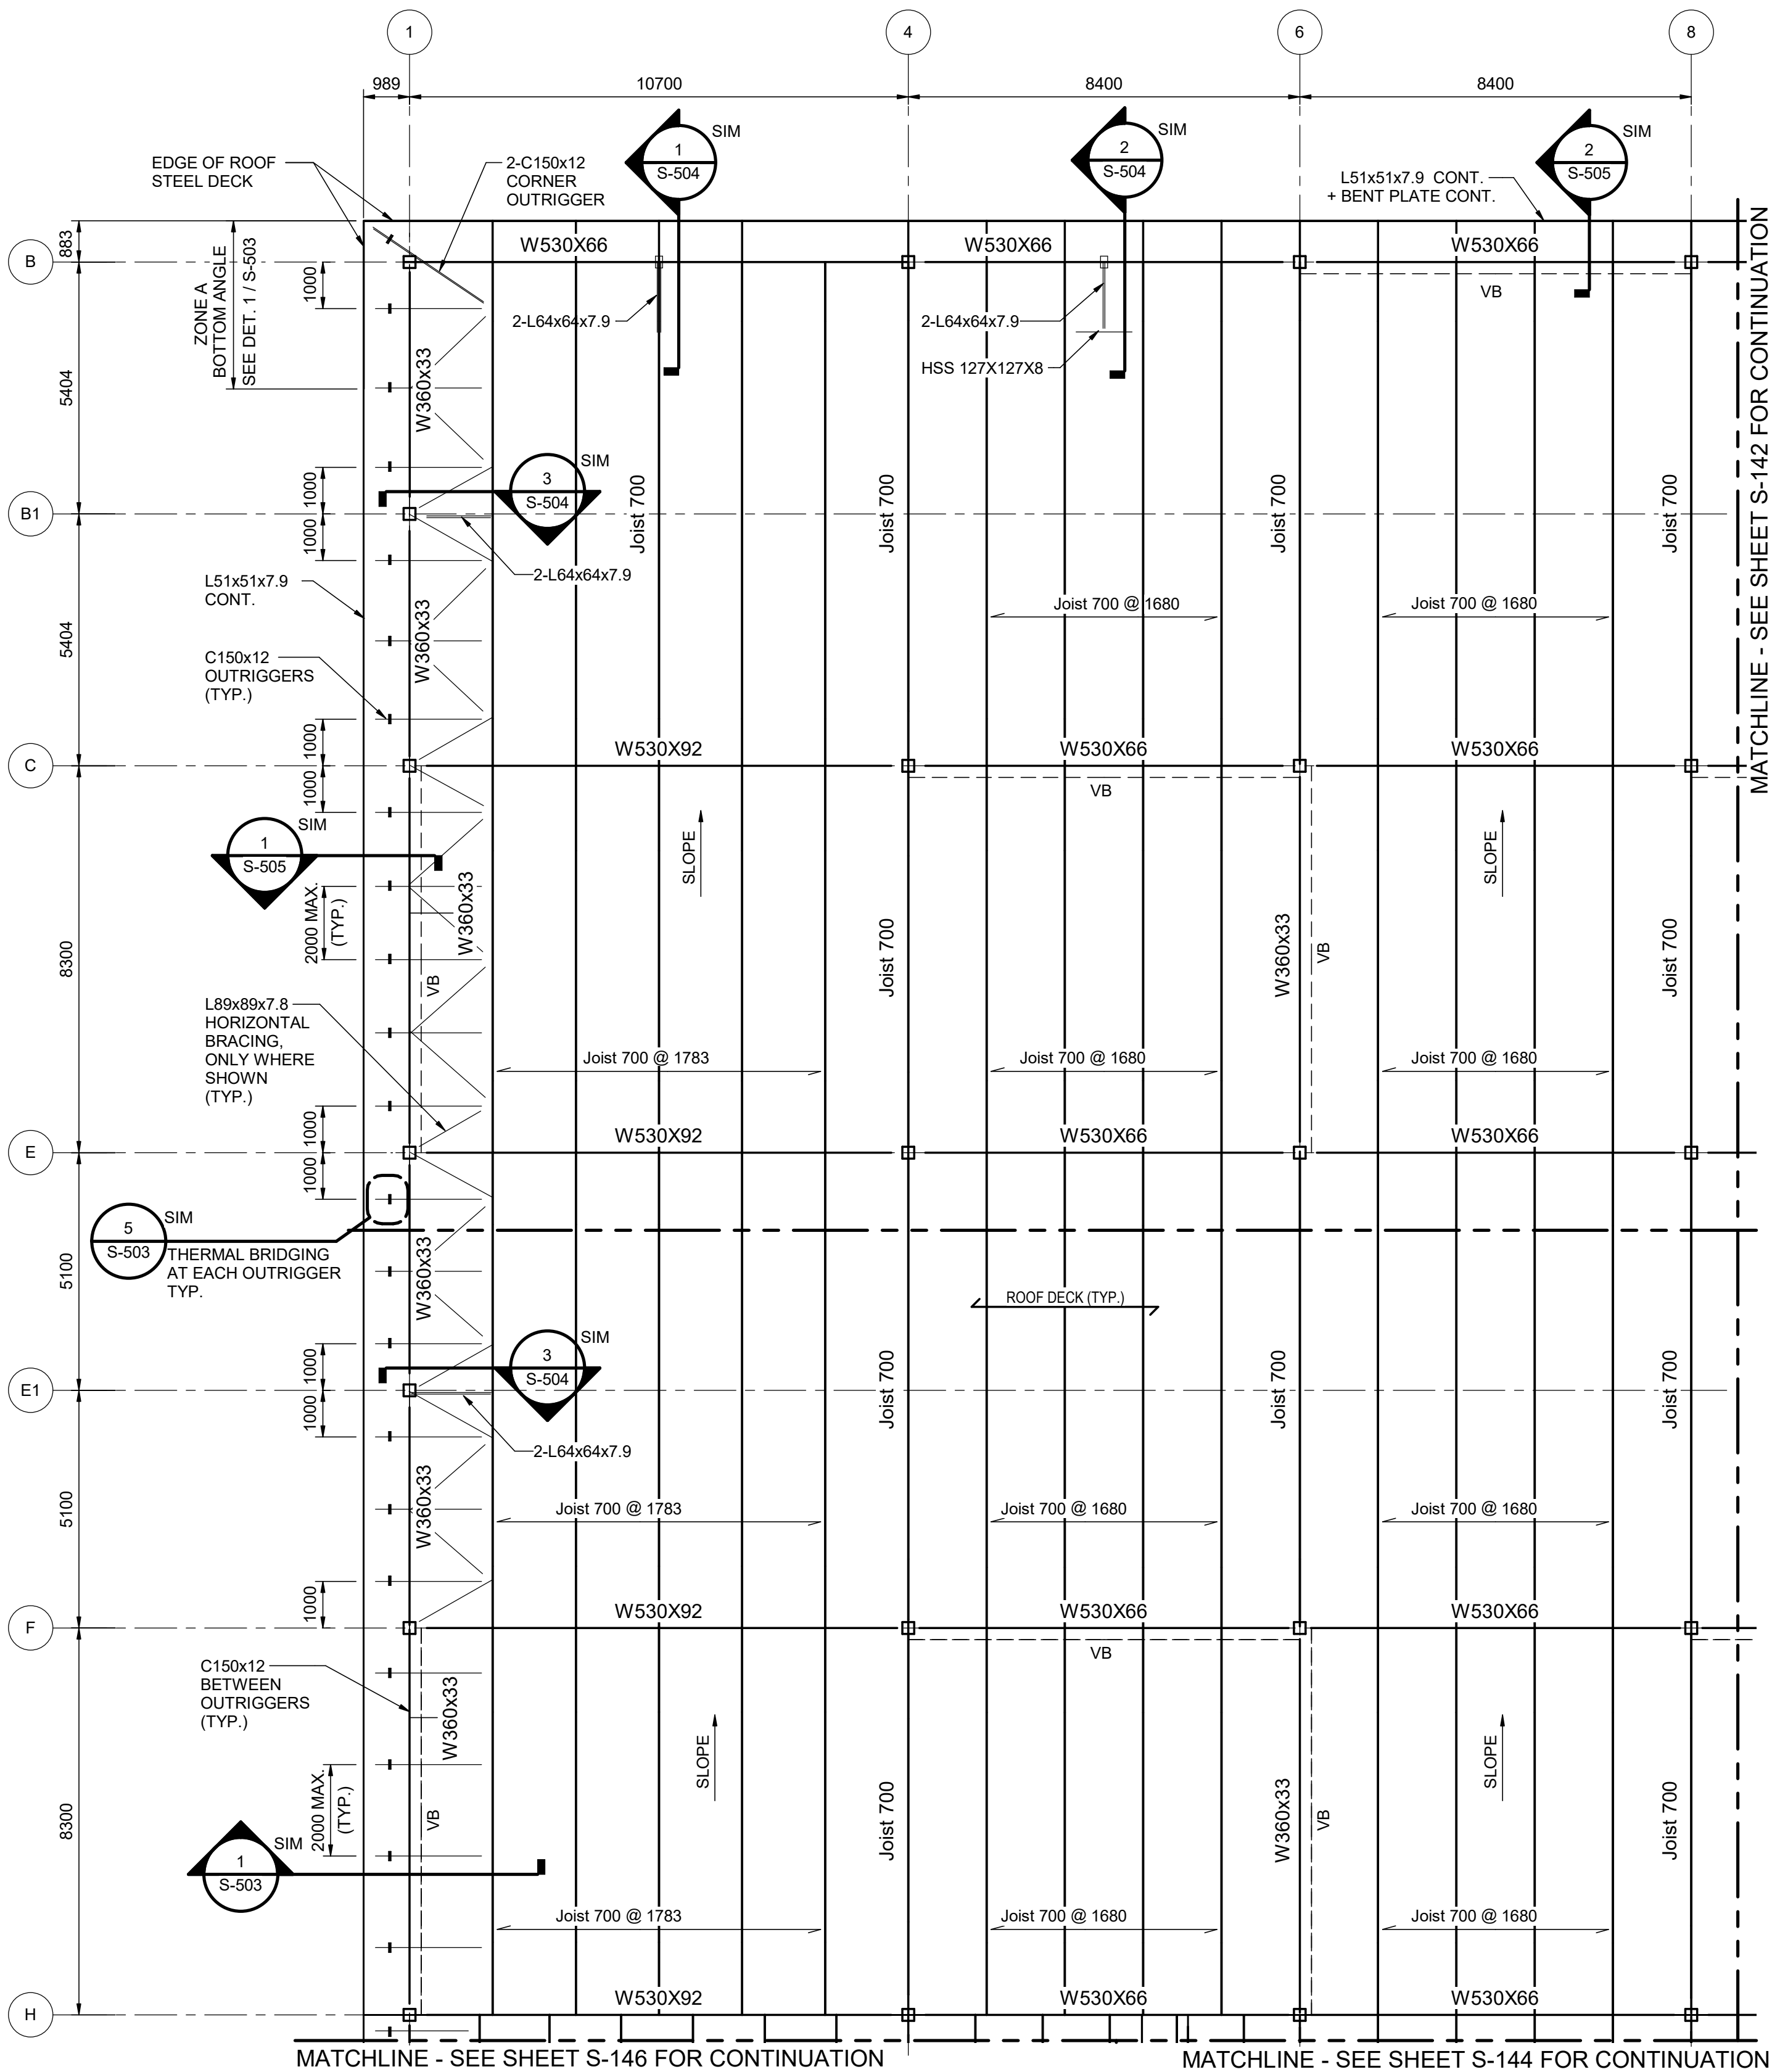

1
S-104
ROOF FRAMING PLAN - AREA A
1 : 100

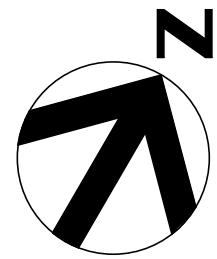

KEY PLAN

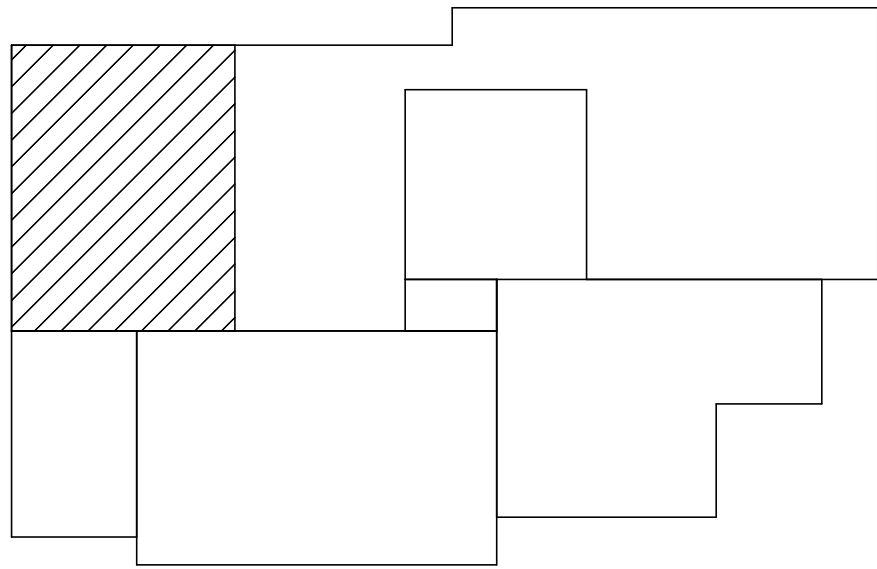


NOTES

- FOR GENERAL NOTES SEE DWGS S-001 TO S003.
- FOR STEEL, OWSJ TYPICAL DETAILS SEE DWGS S-013 TO S-016.
- ALL ROOF STEEL DECKS ARE CANAM P-3615, GAGE 20, 0.91mm THK., ASTM A 653M SS GRADE 230 (UON).
- FOR ROOF ELEVATIONS REFER TO THE SECTIONS AND ELEVATIONS DWGS S-201 TO S-313.

2023/02/10	1	ISSUED FOR TENDER	BC	MRM/AD
DATE	REV.	DESCRIPTION	DRAWN BY	CHECKED BY

CONSULTANT

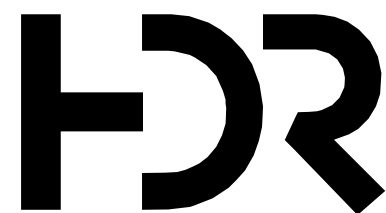

PERMIT TO PRACTICE
HDR CORPORATION
RM SIGNATURE: *[Signature]*
RM APEGA ID #: 27831
DATE: February 10, 2023
PERMIT NUMBER: P009968
The Association of Professional Engineers and Geoscientists of Alberta (APEGA)



PROJECT

CAROLINE - NEW RAVEN CREEK BROOD
TROUT STATION, CONSTRUCTION

TITLE

ROOF FRAMING PLAN - AREA A

SEAL	DRAWN BY BC	CHECKED BY MRM/AD	SCALE 1 : 100
	DATE 2023/02/10	SITE ID S0654	BUILDING ID
	PLAN NO. 020791E	PHASE DD	DISCIPLINE S
	PROJECT ID. P-004974.01		SHEET NO. S-141

DOCUMENT CODE