

AUGERED FOOTINGS SCHEDULE

TYPE	F1A	F1	F2A	F2	F3
SIZE	Ø3000	Ø3000	Ø2500	Ø2500	Ø1000
TOP OF FOOTING ELEVATION	187.425	187.425	187.425	187.425	187.425
REINFORCING STEEL	25M @ 400 C/C VERTICAL 15M @ 400 C/C HORIZONTAL	25M @ 400 C/C VERTICAL 15M @ 400 C/C HORIZONTAL	25M @ 400 C/C VERTICAL 15M @ 400 C/C HORIZONTAL	25M @ 400 C/C VERTICAL 15M @ 400 C/C HORIZONTAL	25M @ 400 C/C VERTICAL 15M @ 400 C/C HORIZONTAL
BOTTOM FOUNDING ELEVATION	184.1	185.0	184.1	185.0	185.0


NOTES:
1. AT RAIN WATER LEADER LOCATIONS, TOP OF PIER TO BE LOWERED 600 MM.
(FOR LOCATIONS SEE MECHANICAL DRAWINGS, ±10 PIER AT REPAIR BAY, 1 PIER AT BUS GARAGE AREA)

FOOTING SCHEDULE

TYPE	F4	F4A	F5	F6	F7	F8	F9	F10	F11	F12	F13	F14	F14A
SIZE	820x1145	700x950	1000x1000	1000x2000	1500x1500	4000x2000	3500x2000	9500x2000	5500x2000	2000x2000	5000x2000	820x1145	820x1145
DEPTH	250	200	400	400	600	600	600	700	700	600	700	250	250
REINFORCING STEEL	15M @ 200 E.W. BOTTOM	15M @ 200 E.W. BOTTOM	20M @ 200 E.W. BOTTOM	20M @ 200 E.W. BOTTOM	20M @ 200 E.W. BOTTOM	20M @ 250 E.W. BOTTOM 20M @ 200 E.W. TOP	20M @ 250 E.W. BOTTOM 20M @ 200 E.W. TOP	20M @ 250 E.W. BOTTOM 20M @ 200 E.W. TOP	20M @ 250 E.W. BOTTOM 20M @ 200 E.W. TOP	20M @ 200 E.W. BOTTOM	20M @ 250 E.W. BOTTOM 20M @ 200 E.W. TOP	15M @ 200 E.W. BOTTOM	15M @ 200 E.W. BOTTOM
BOTTOM FOUNDING ELEVATION	187.175	187.175	186.300	186.300	186.300	186.300	186.300	186.300	186.300	186.300	186.300	187.35	186.300

PIER SCHEDULE

TYPE	P1	P2	P3	P4	P5	P6	P7	P8	P9
PIER SIZE	600x600	800x825	700x700	800x875	875x875	825x600	825x825	500x825	500x750
TOP OF PIER ELEVATION	187.815	188.09	188.09	188.09	188.09	187.815	187.815	188.09	188.09
ANCHOR RODS	4-25M	4-25M	4-25M	4-25M	4-25M	4-25M	4-25M	4-25M	4-25M
VERTICALS / DOWELS TIES	12-25M 3-10M @ 200	12-25M 3-10M @ 200	12-25M 3-10M @ 200	12-25M 3-10M @ 200	12-25M 3-10M @ 200	12-25M 3-10M @ 200	12-25M 3-10M @ 200	12-25M 3-10M @ 200	12-25M 3-10M @ 200
PIER SHAPE									

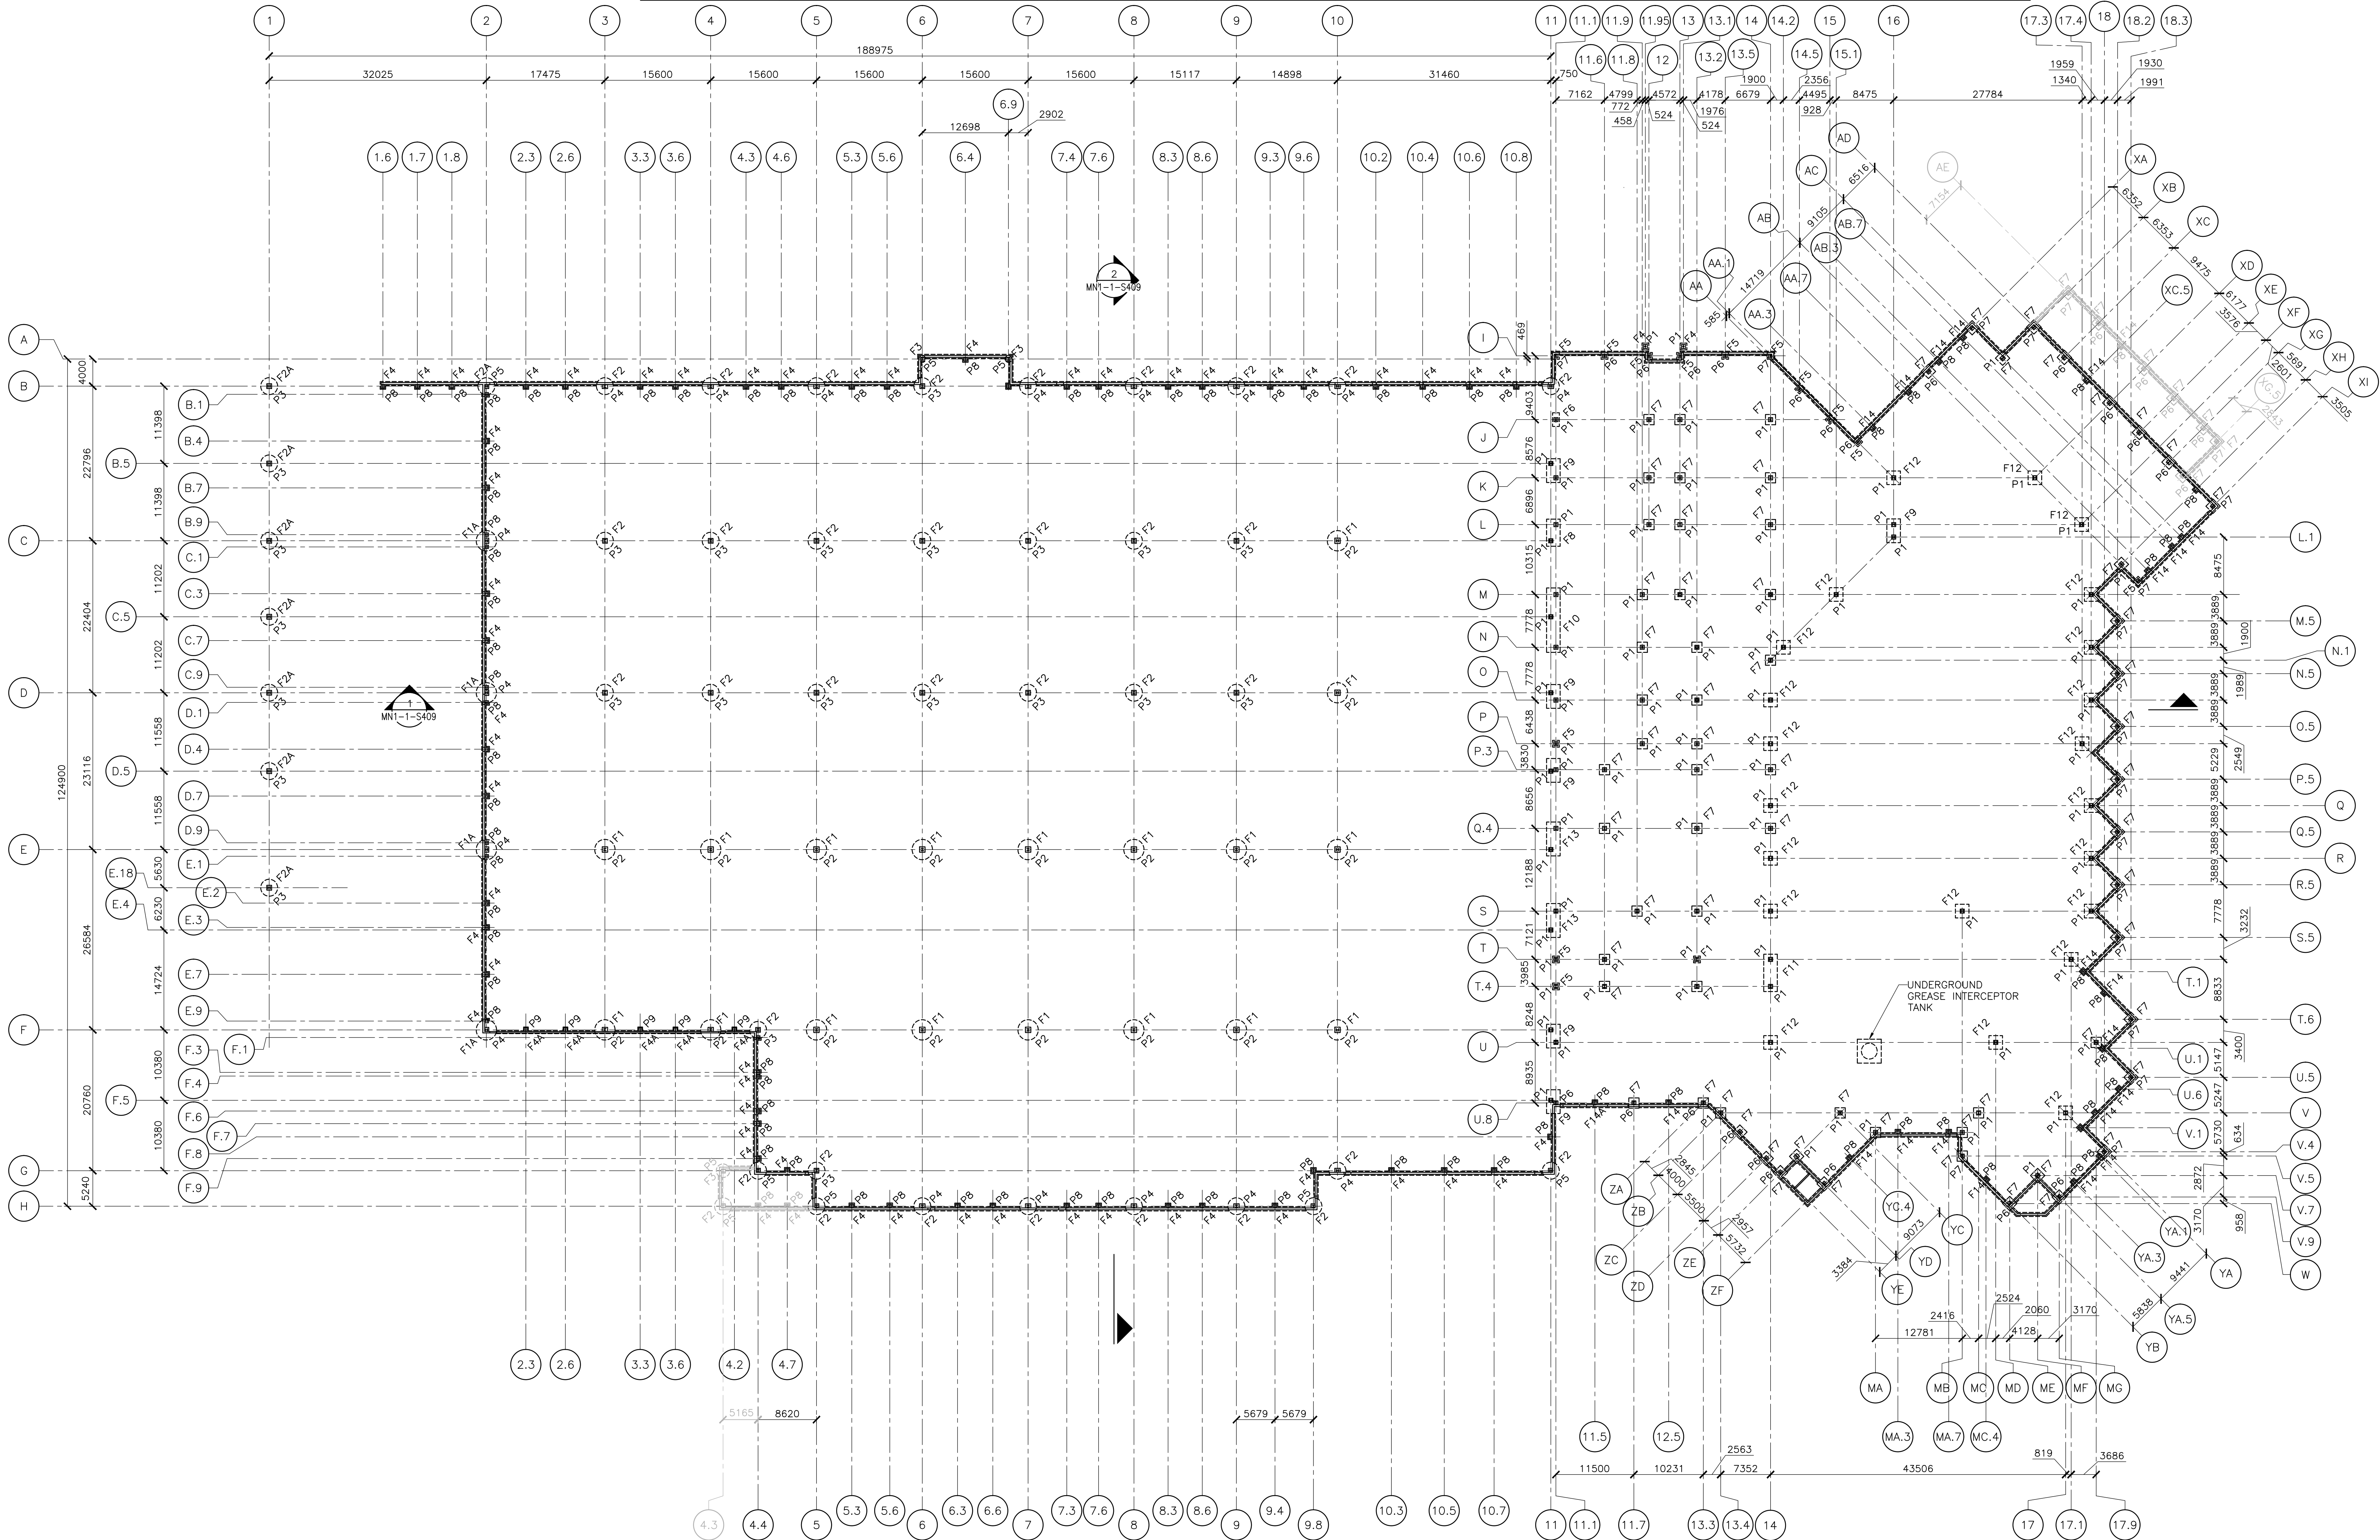

FOUNDATION PLAN - OVERALL
SCALE 1 : 400

NOTES:
1. FOR GENERAL NOTES REFER TO DWG. MN1-1-S001.

DATE
(mm dd yyyy)
SEP 13 2016

ISSUED FOR
TECHNICAL SUBMISSION

REV
0

KEY PLAN

IBI GROUP
100-175 Galaxy Boulevard
Toronto ON M9W 0C3 Canada
Tel 416 679 1530 Fax 416 675 4620
ibigroup.com

This drawing has been prepared solely for the use of TTC McNICOLL Bus Garage RFP Response and there are no representations of any kind made by IBI Group to any party with whom IBI Group has not entered into a contract.

North Arrow

Detail Symbol

Project Manager
E. CZERNIAK

Architect/Engineer
K. HSU

Project Leader
A. KTECHA

Drawn
A. SHIRAZI

Date
APR 2016

Checked
K. ANGER

Client
TORONTO TRANSIT COMMISSION

Project
McNICOLL BUS GARAGE
- DESIGN BUILD

Drawing Title
FOUNDATION PLAN-OVERALL

Check Scale (may be photo-reduced)
0 1 inch 10mm

Project No.
24RX15.0199

Drawing No.
MN1-1-S100