

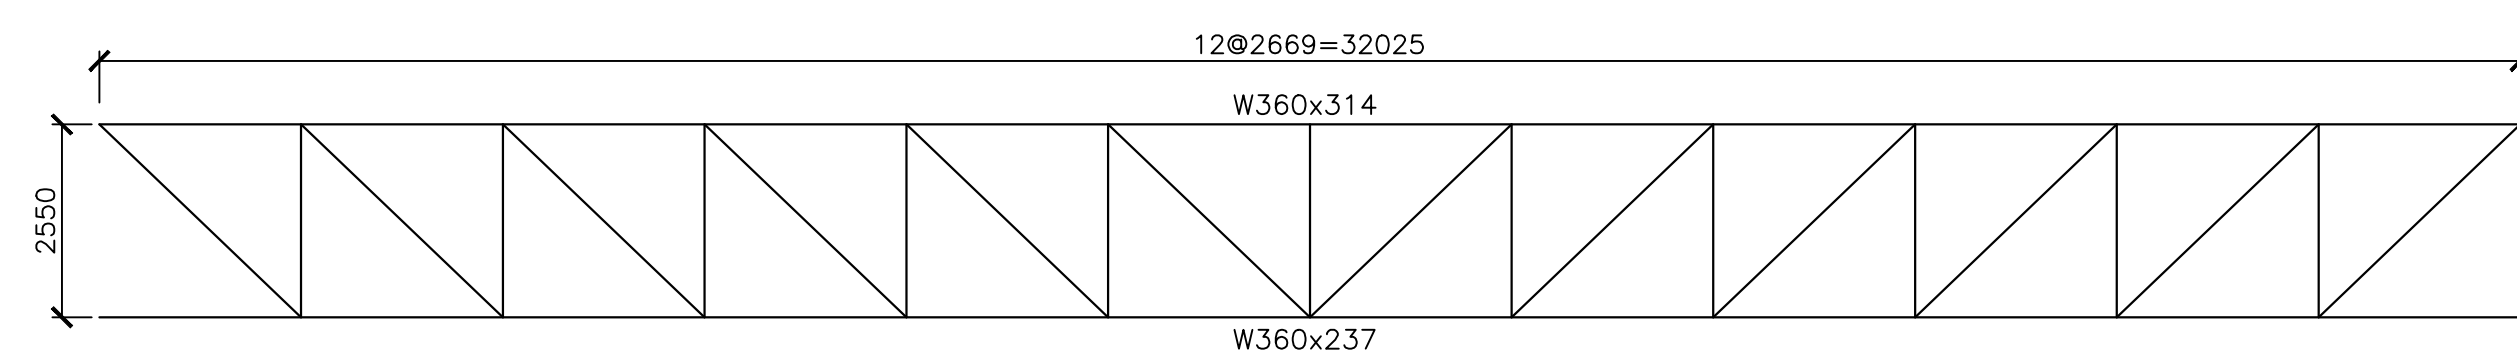
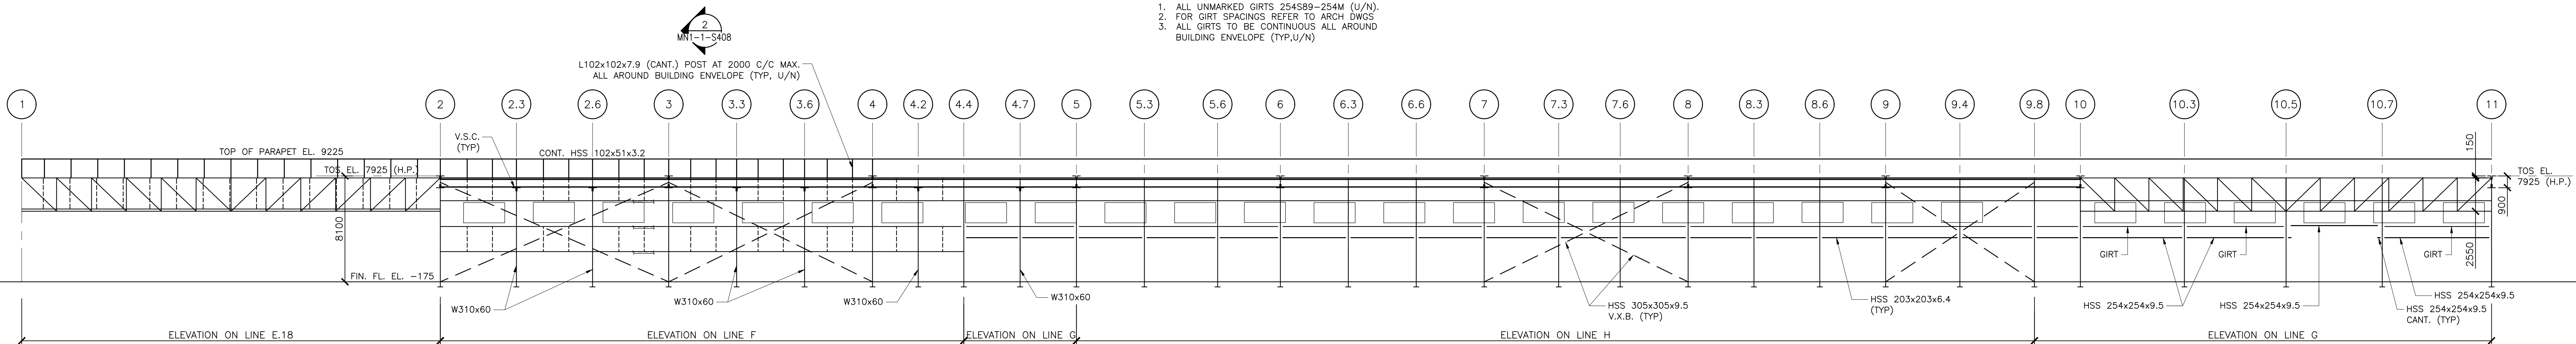
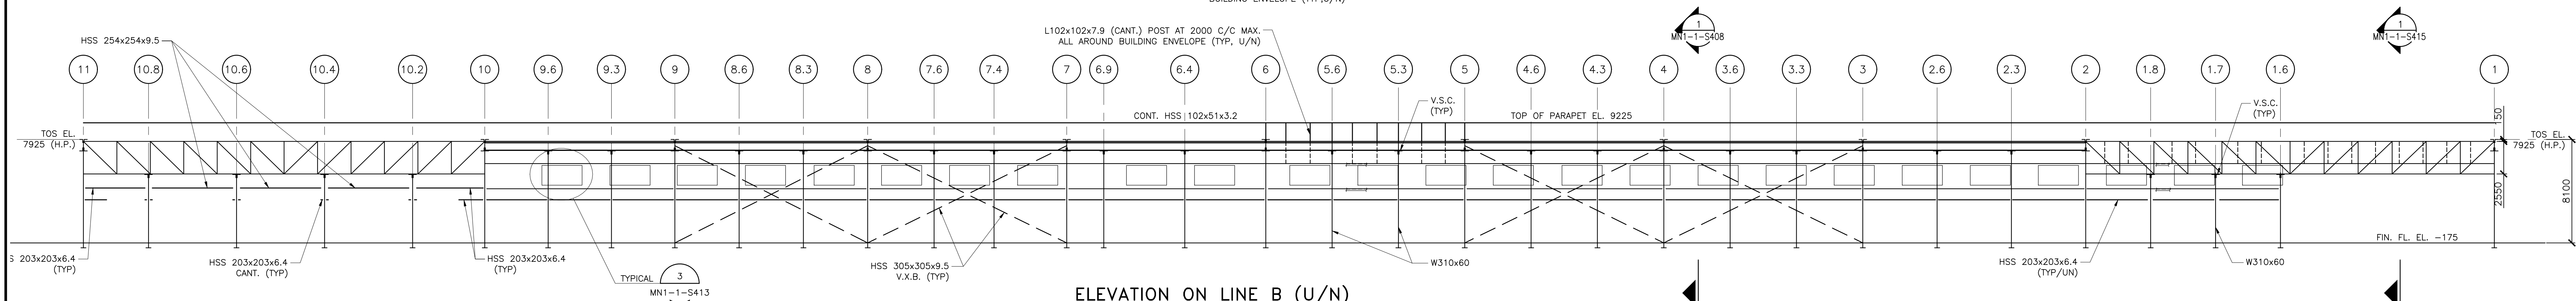
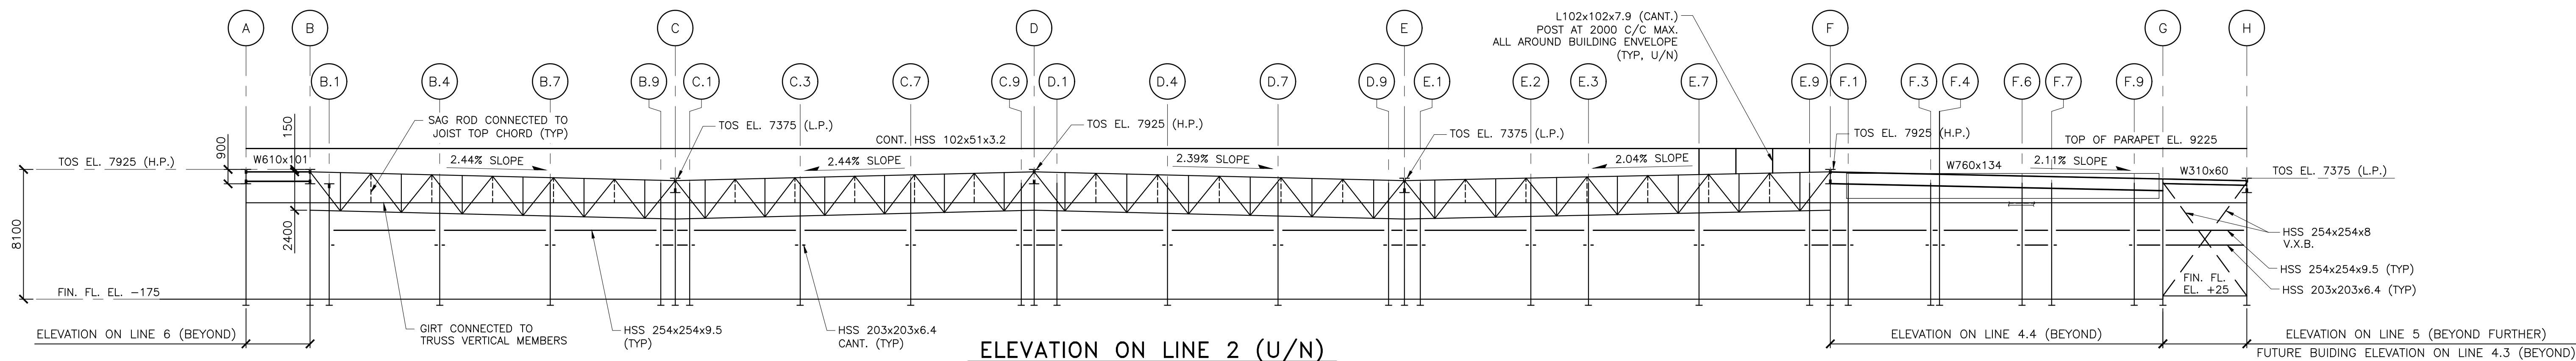
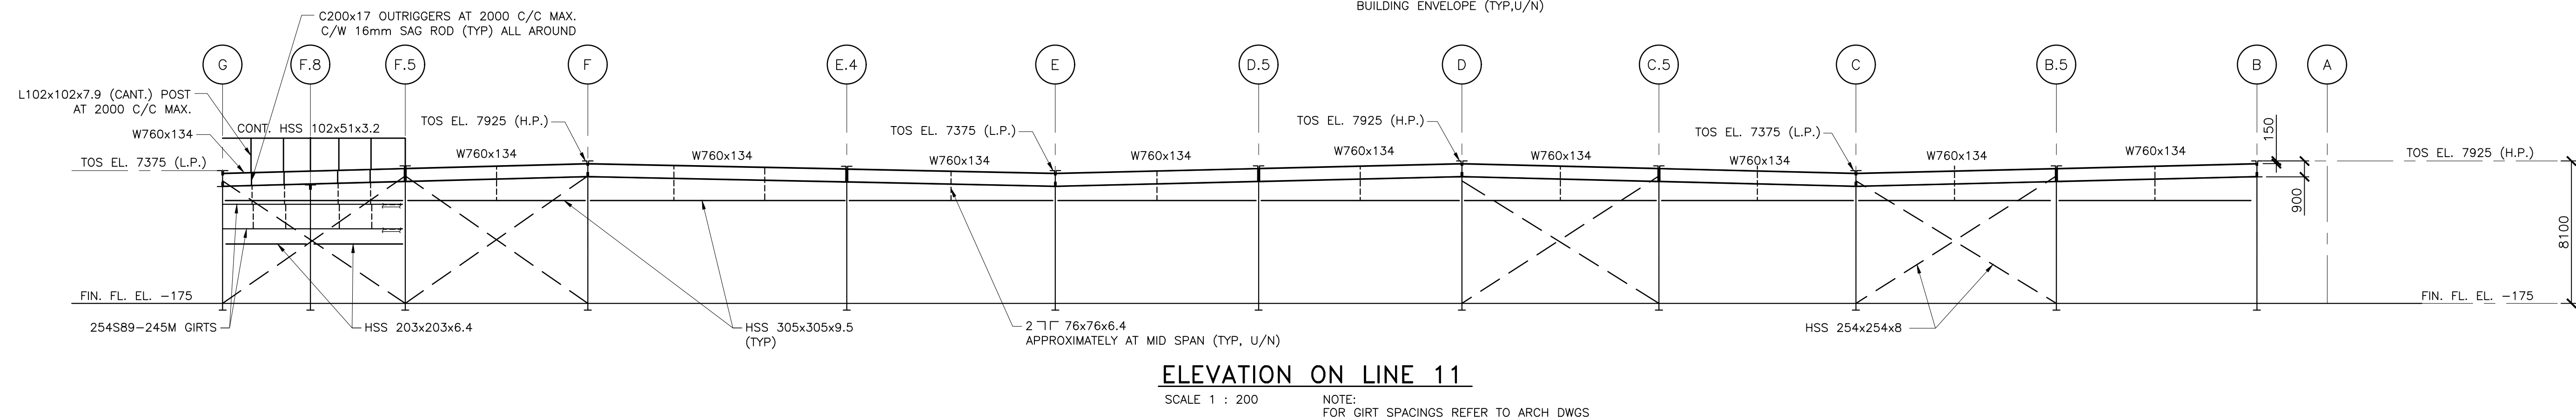


User Name: Adeleh Shirazi Plot Date: Thursday, September 08, 2016 1:18:53 PM Path and File Name: j:\24rx15.0199_etc_mcnicoll-bus\5.9 drawing\99struc\layout\mn1-1-s401.dwg

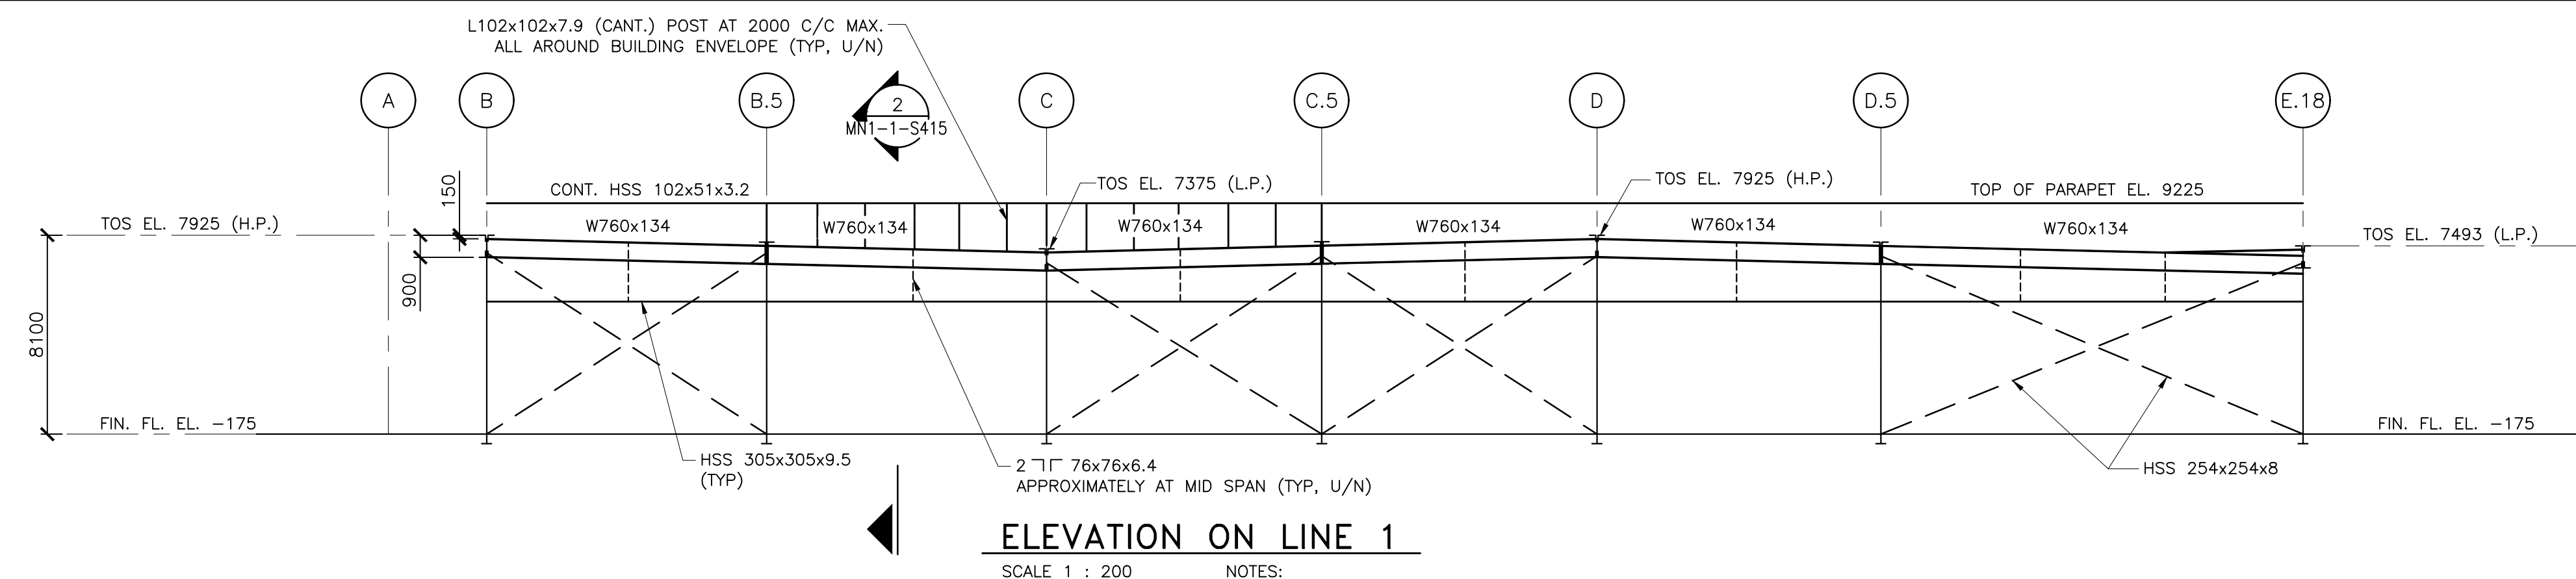


TRUSS TI
VERTICAL MEMBERS : W200x46 UNO
DIAGONAL MEMBERS : 2L152x203x13 UNO

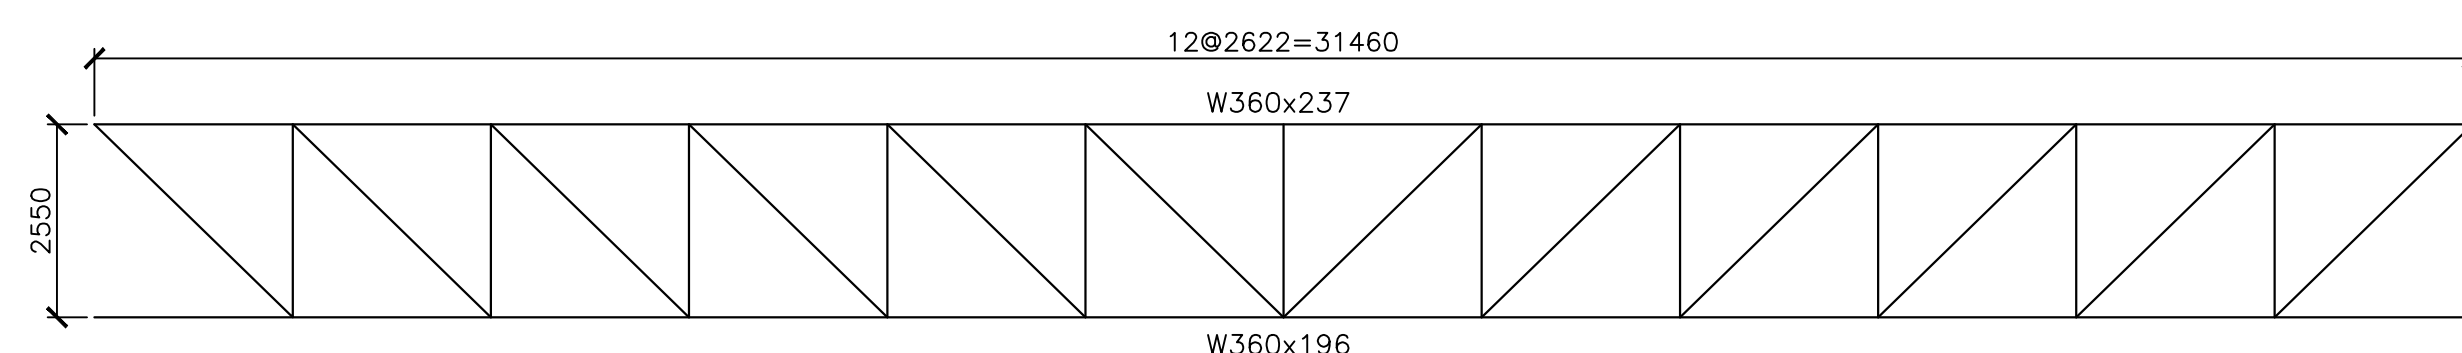

TRUSS T2
VERTICAL MEMBERS : W200x46 UNO
DIAGONAL MEMBERS : 2L152x152x11 UNO

DATE (mm dd yyyy)	ISSUED FOR	REV
SEP 13 2016	TECHNICAL SUBMISSION	0

KEY PLAN

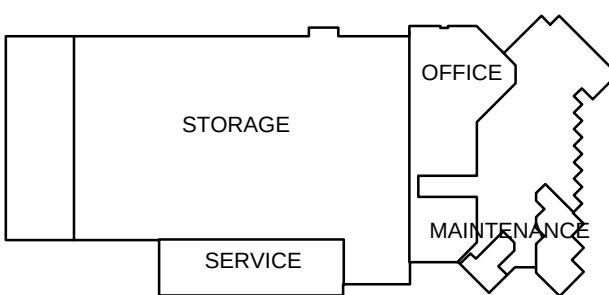


IBI GROUP
100-175 Galaxy Boulevard
Toronto ON M9W 0C3 Canada
Tel 416 679 1550 Fax 416 675 4620
ibigroup.com

This drawing has been prepared solely for the use of TTC McNICOLL Bus Garage RFP Response and there are no representations of any kind made by IBI Group to any party with whom IBI Group has not entered into a contract.

North Arrow

Detail Symbol

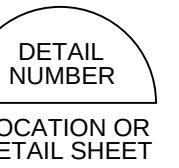

Project Manager E. CZERNIAK	Architect/Engineer K. HSU
Project Leader A. KTECHA	Drawn A. SHIRAZI
Date APR 2016	Checked K. ANGER

Client
TORONTO TRANSIT COMMISSION



Project
McNICOLL BUS GARAGE
- DESIGN BUILD

Drawing Title

ELEVATIONS

Check Scale (may be photo-reduced)
0 1 inch 0 10mm

Project No.
24RX15.0199

Drawing No.
MN1-1-S401