



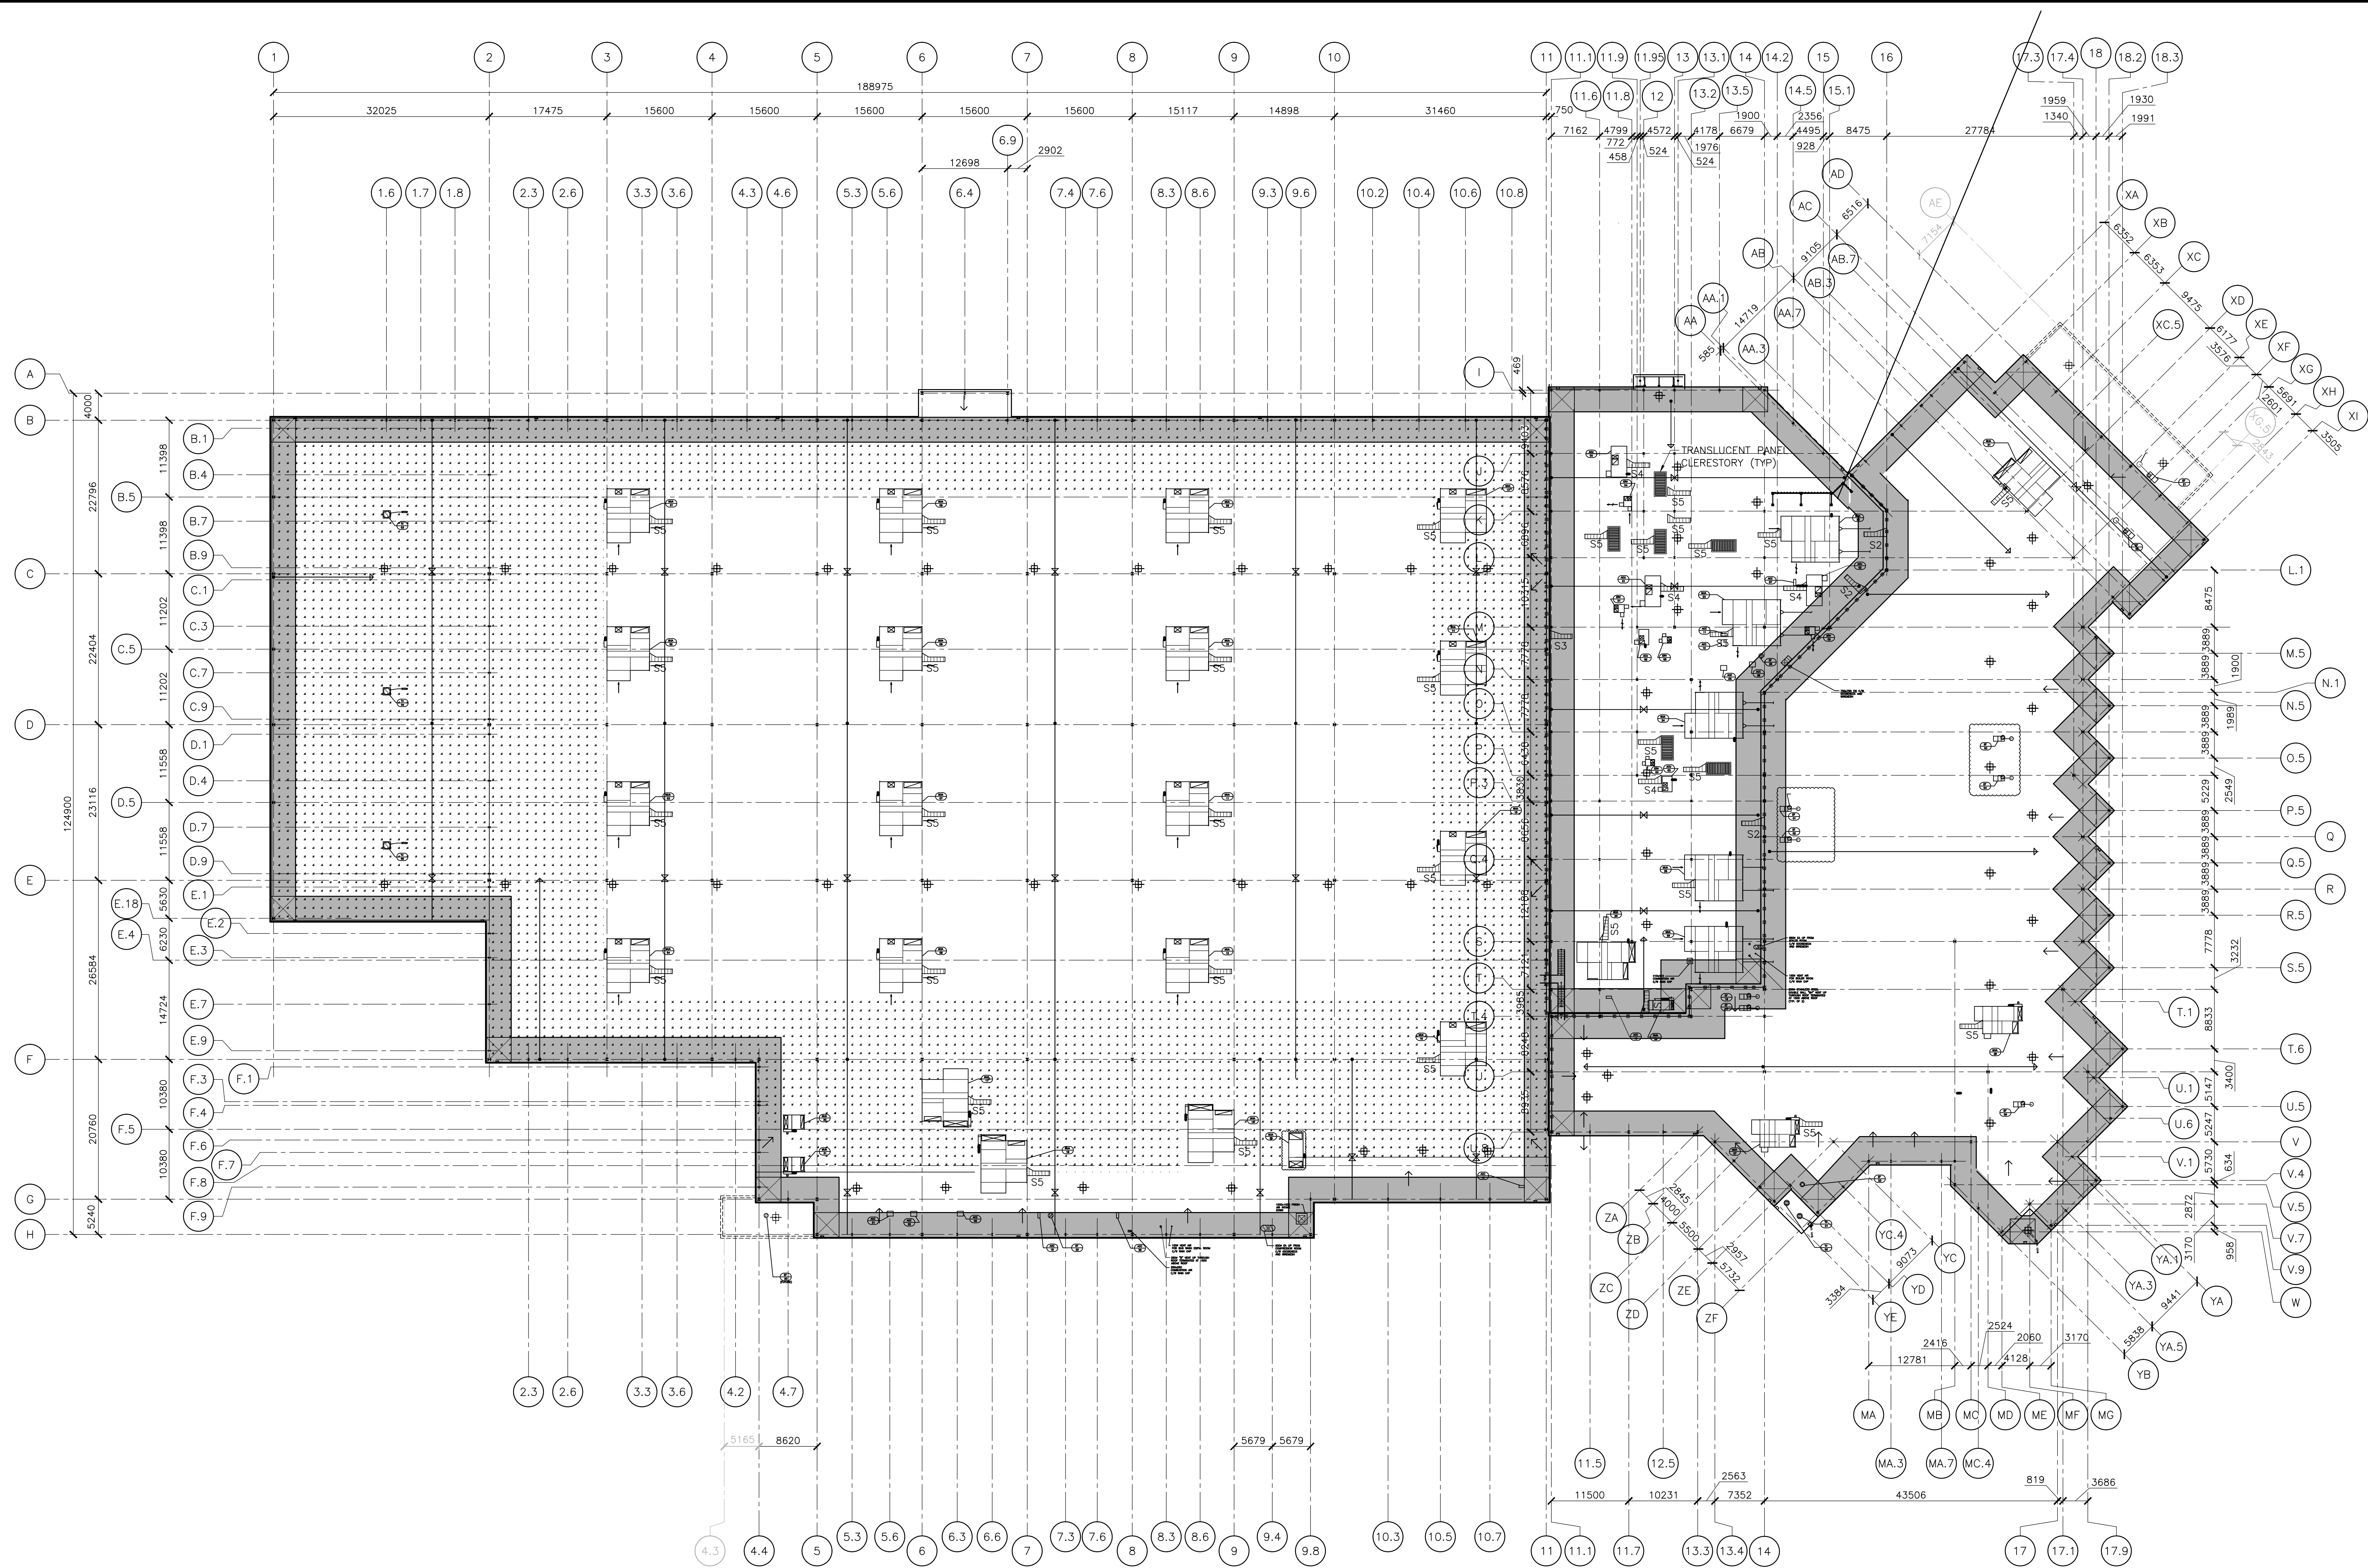

OVERALL ROOF PLAN – SNOW PILE-UP & GROSS WIND UPLIFT LOAD DIAGRAMS
SCALE 1 : 400

DATE (mm dd yyyy)	ISSUED FOR	REV
SEP 13 2016	TECHNICAL SUBMISSION	0


KEY PLAN

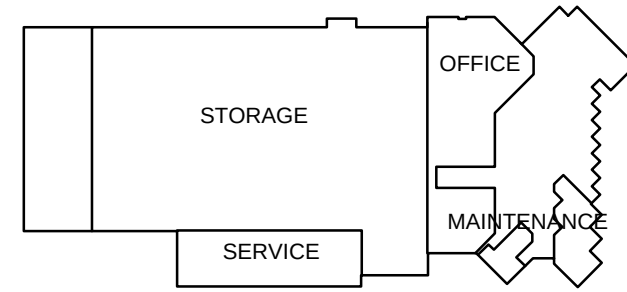


IBI GROUP
100-175 Galaxy Boulevard
Toronto ON M9W 0C9 Canada
Tel 416 679 1530 Fax 416 675 4620
ibigroup.com

This drawing has been prepared solely for the use of TTC McNICOLL Bus Garage RFP Response and there are no representations of any kind made by IBI Group to any party with whom IBI Group has not entered into a contract.

North Arrow

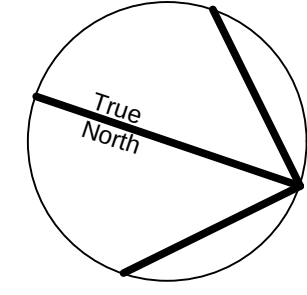

Detail Symbol

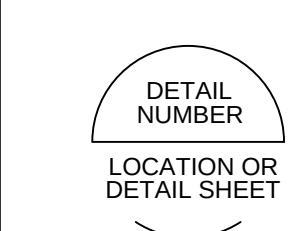

Project Manager E. CZERNIAK	Architect/Engineer K. HSU
Project Leader K. HSU	Drawn M. BOGOSLAVOV
Date MAY 2016	Checked K. ANGER
Client TORONTO TRANSIT COMMISSION	



Project
**McNICOLL BUS GARAGE
– DESIGN BUILD**

Drawing Title
**OVERALL ROOF PLAN SNOW
PILE-UP & GROSS WIND
UPLIFT LOAD DIAGRAMS**

Check Scale (may be photo-reduced)
0 1 inch 10mm

Project No.
24RX15.0199 MN1-1-S002

Drawing No.