


S-201.DWG

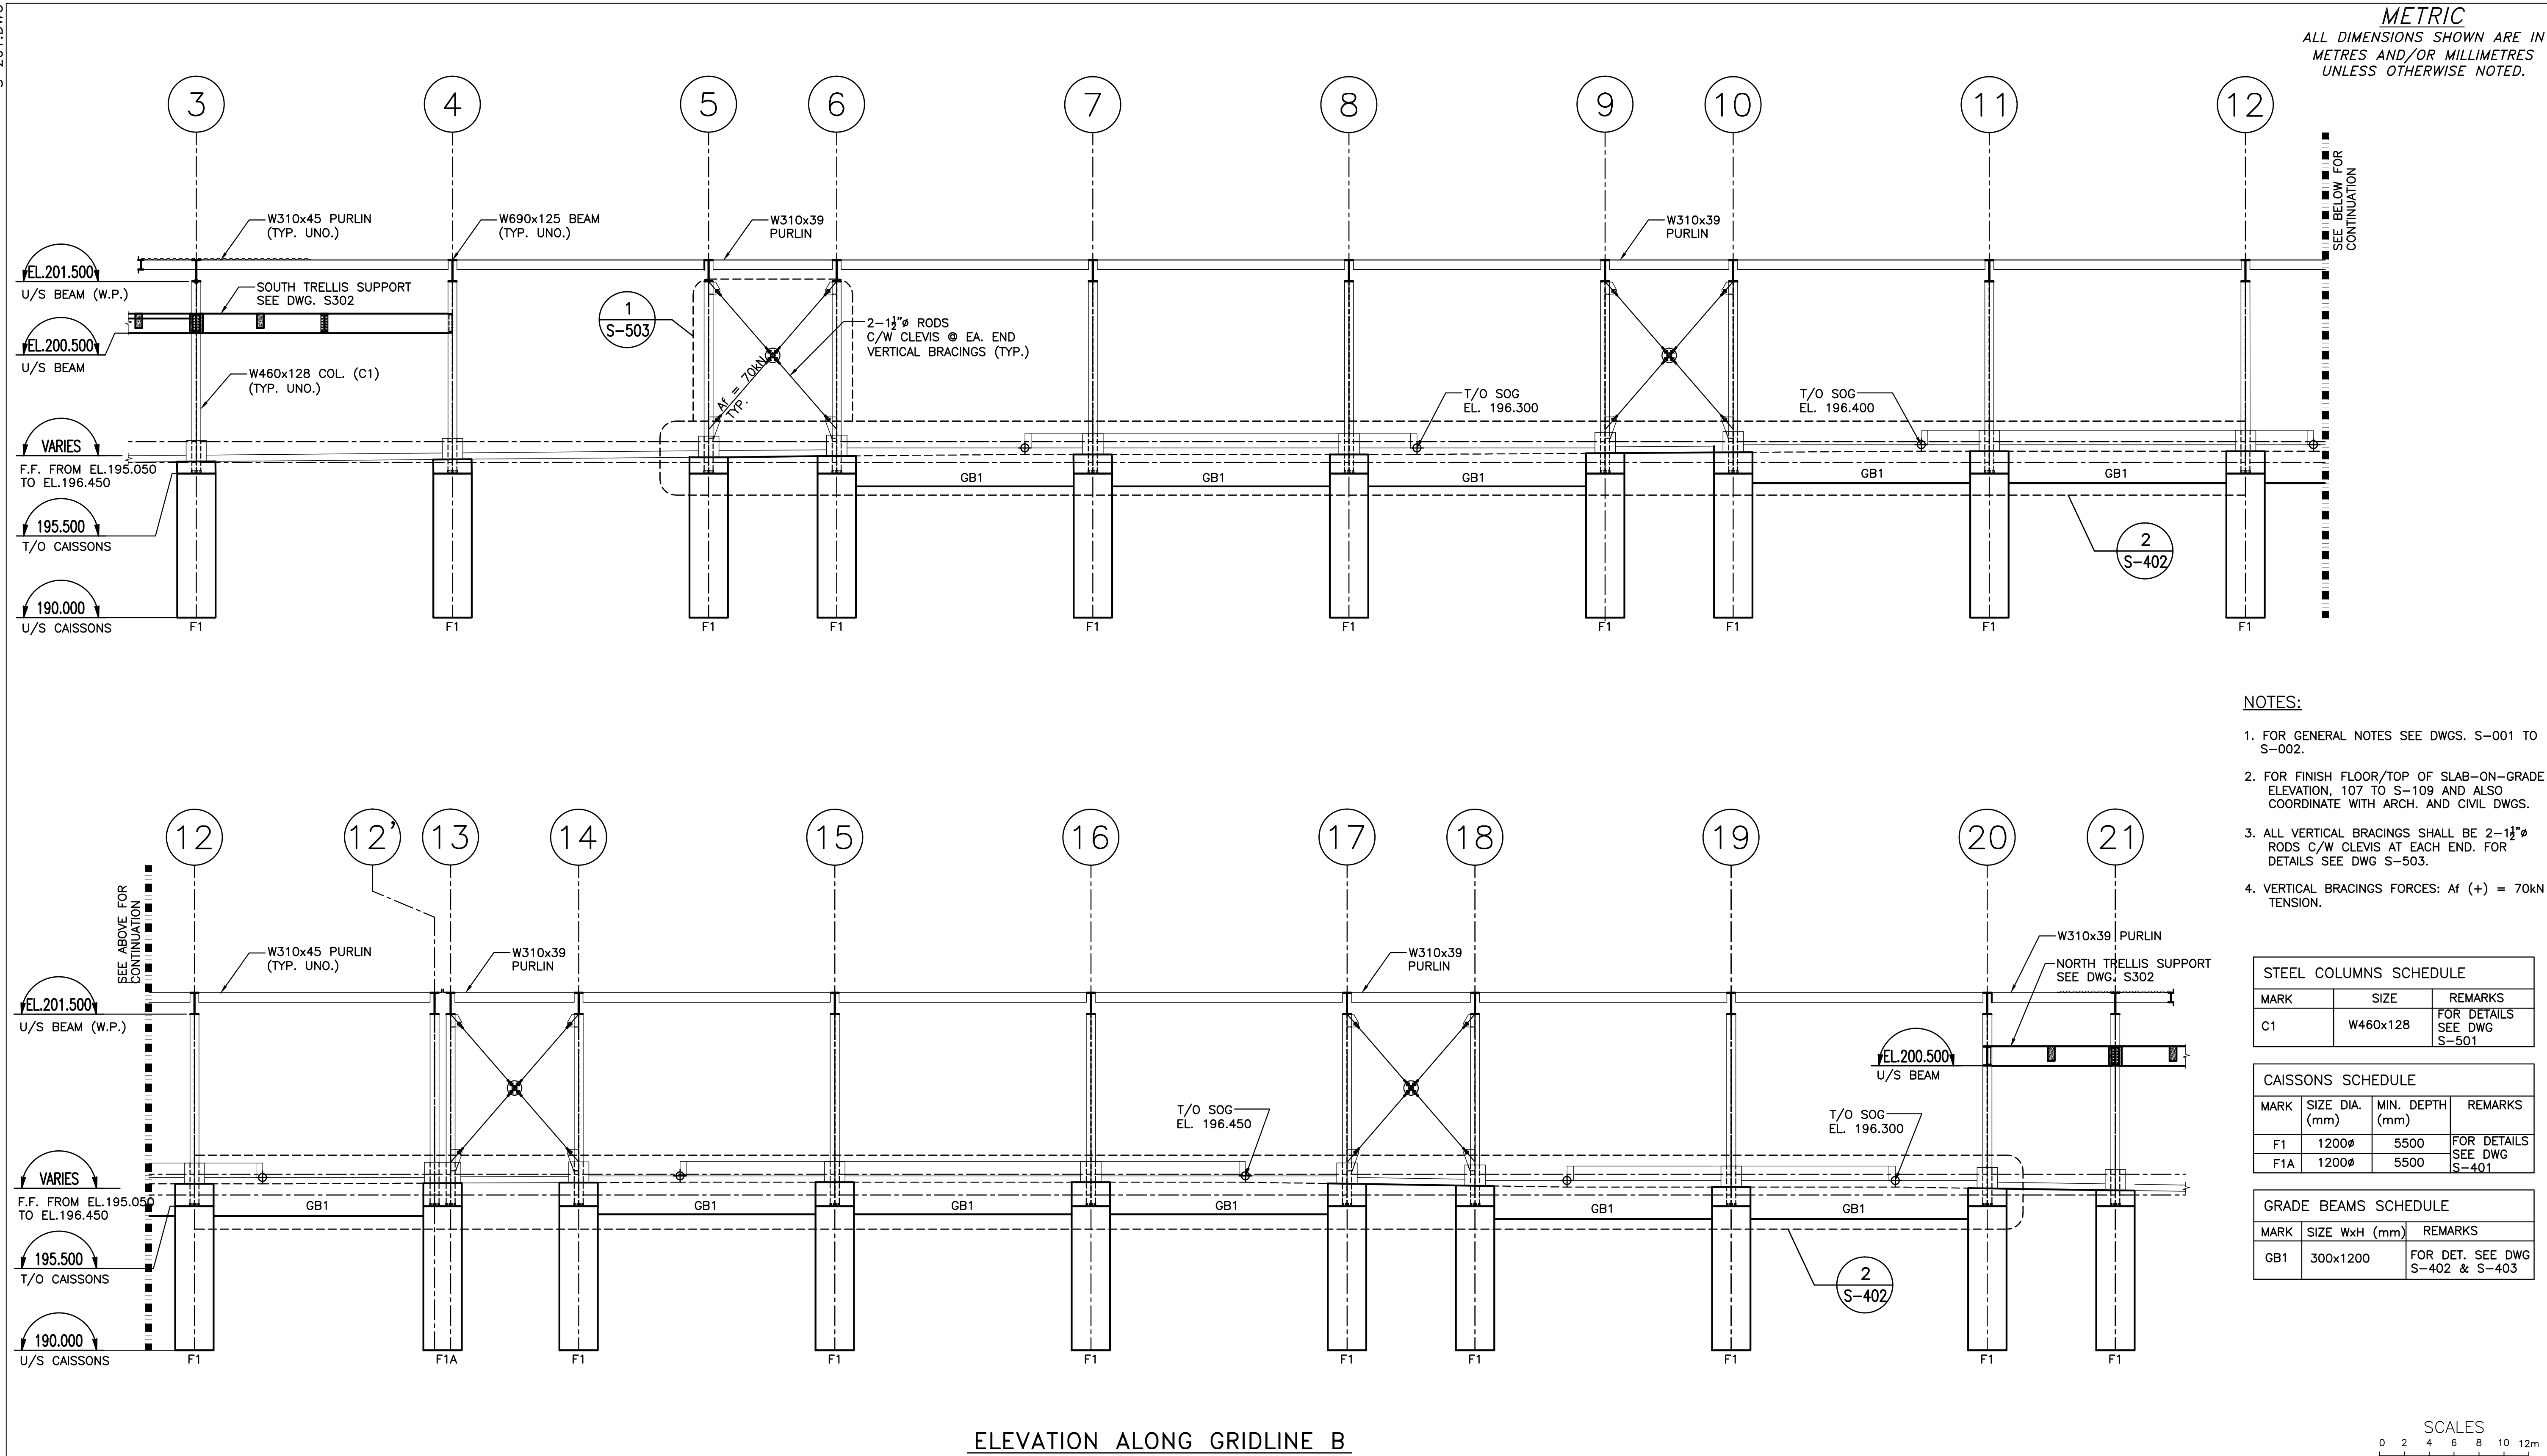


FILENAME: C:\working\pht\1825556\S-201.dwg
PLOTDATE: Feb 27, 2018 - 2:46pm
PLOTTER: B7: bchikov

No.	DATE	REVISIONS	BY
A	12/29/2017	ISSUED FOR TENDER	OP/SK
B	03/05/2018	ISSUED FOR BUILDING PERMIT	OP/SK



Transportation
Services

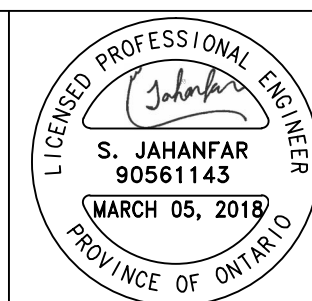

DESIGN
OP

DRAWN
RV

CHECKED
SJ

CORNELL BUS TERMINAL
ELEVATIONS (1/2)

DWG. NO.
S-201

CONT. NO.
PT-17-061-RT

SHEET NO.
171