



S-110.DWG

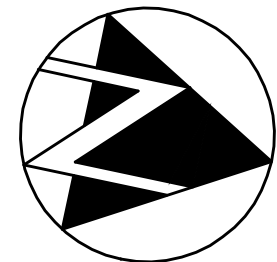

METRIC
ALL DIMENSIONS SHOWN ARE IN
METRES AND/OR MILLIMETRES
UNLESS OTHERWISE NOTED.

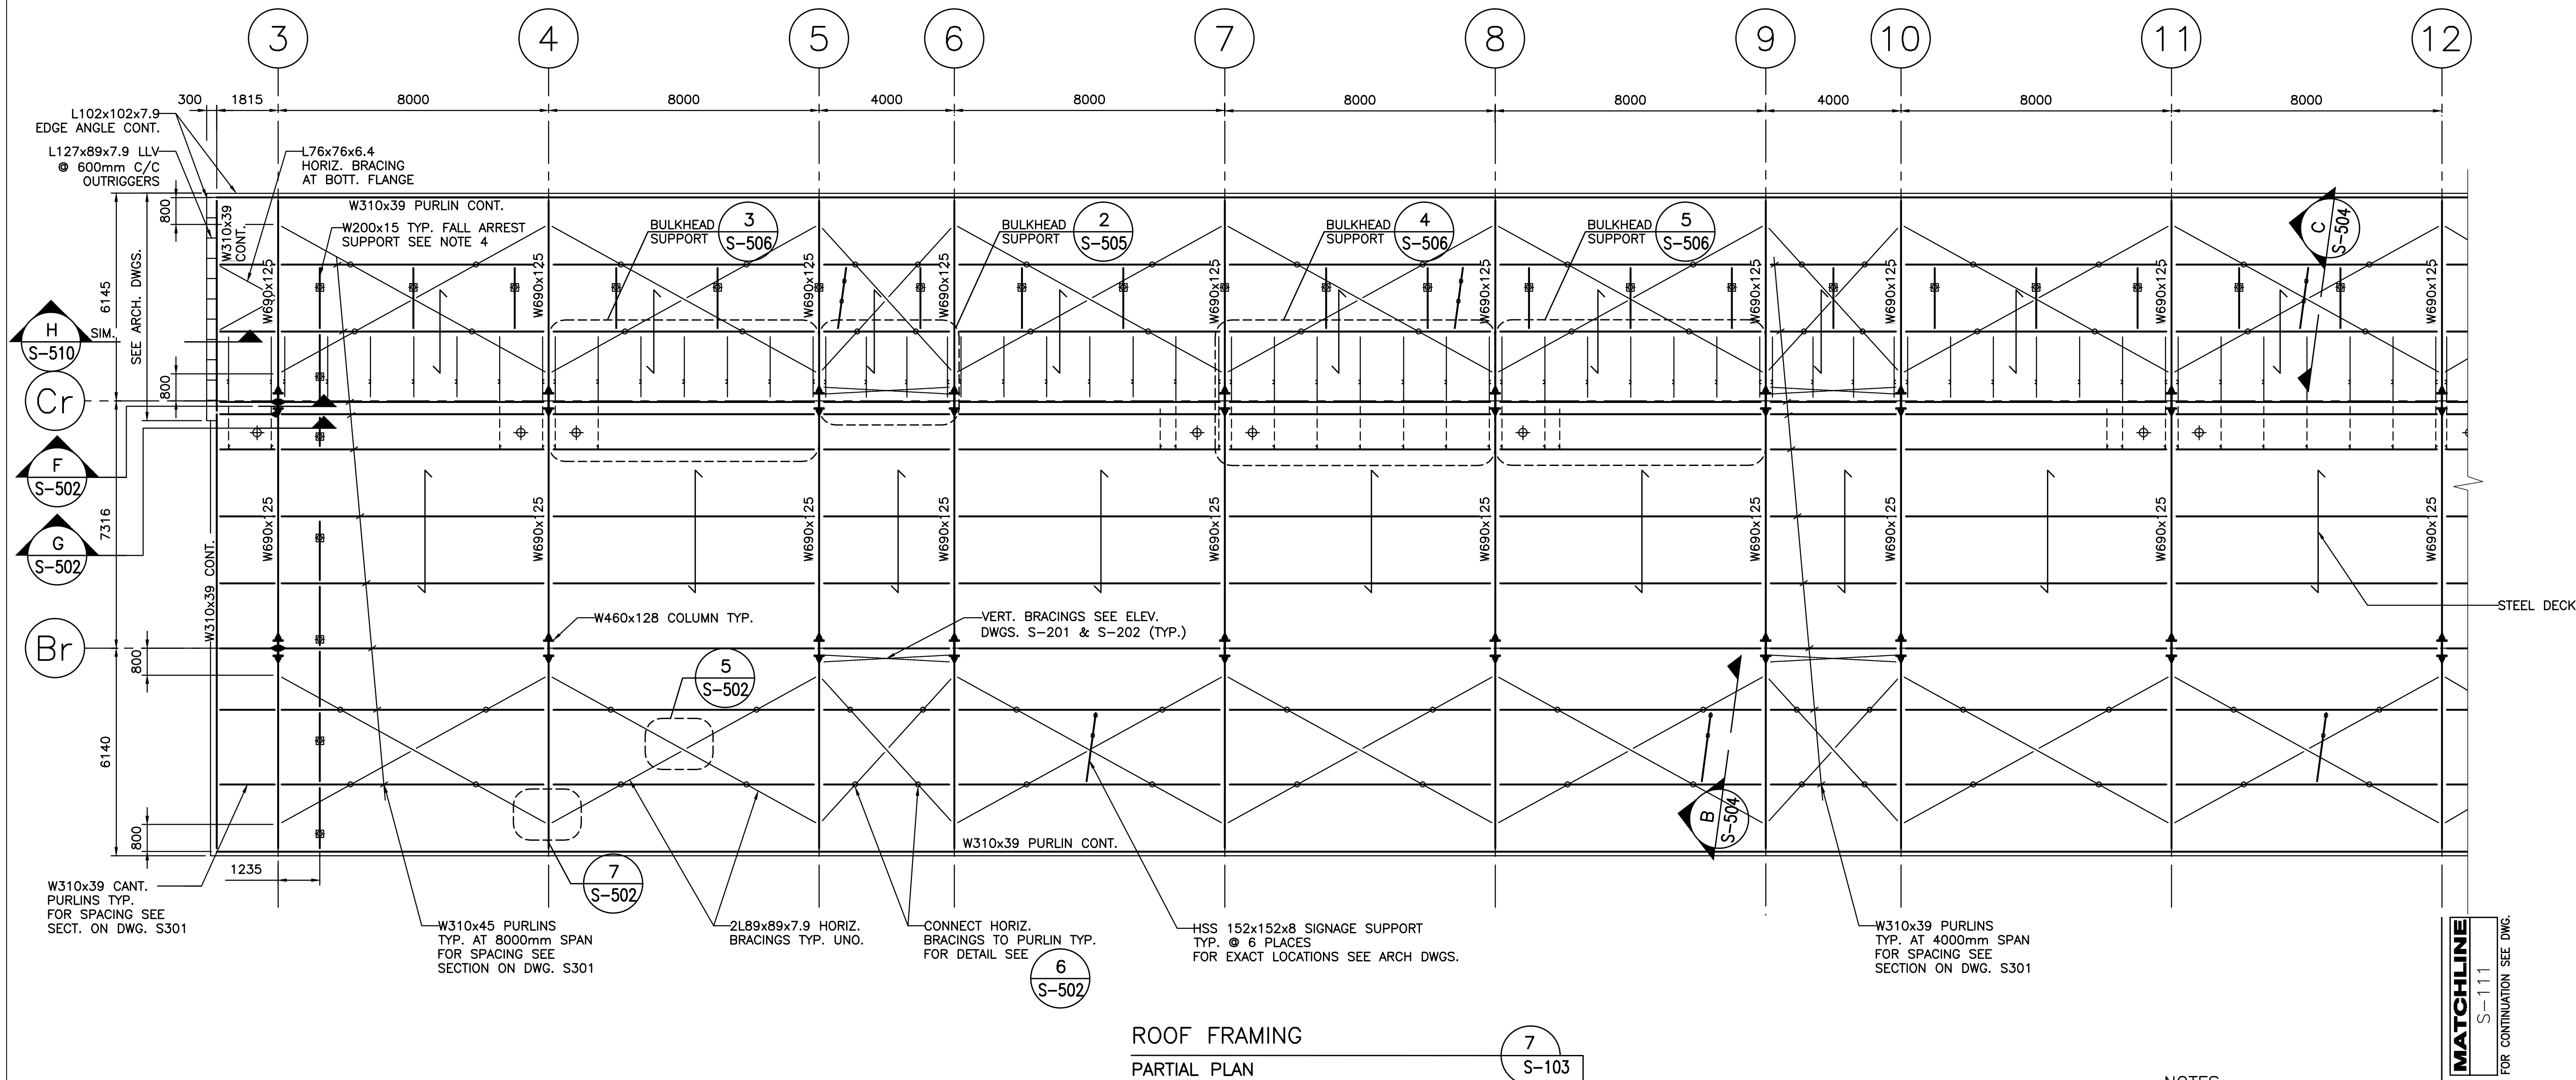

ROOF FRAMING
PARTIAL PLAN


7
S-103

NOTES:

- FOR GENERAL NOTES SEE DWGS. S-001 TO S-002.
- FOR TYPICAL DETAILS SEE DWG. S-003 TO S-006.
- FOR ROOF NOTES, LOADS AND SNOW ACCUMULATION DIAGRAM SEE DWG. S-103.
- FOR FALL ARREST LOCATION SEE ARCH. DWGS. FOR ANCHORAGE DETAIL SEE DWG. S-006.
- FOR ROOF DRAIN LOCATION SEE ARCH. DWGS.
- SEE SECTIONS ON DWG. S-301 FOR M_c LOADS.

LEGEND:

- STEEL DECK P-3606 38mm DEEP 1.22 (18GA) CANAM OR SIMILAR
- MOMENT CONNECTION
- FALL ARREST
- ROOF DRAIN

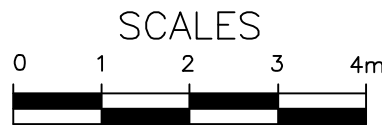

MATCHLINE
S-111
FOR CONTINUATION SEE DWG.




100 York Blvd., Suite 300
Richmond Hill, ON, L4B 1J8
Ph. (289) 695-4600
Fax. (289) 695-4601

FILENAME: C:\working\pht\1825556\S-110.dwg
PLOTDATE: Feb 27, 2018 - 2:45pm
PLOTTER: B7: bchikov

No.	DATE	REVISIONS	BY
A	12/29/2017	ISSUED FOR TENDER	OP
B	03/05/2018	ISSUED FOR BUILDING PERMIT	OP



**Transportation
Services**

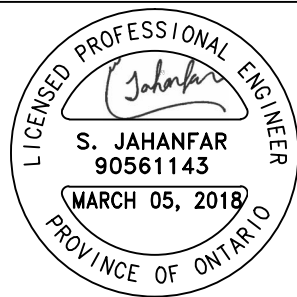

DESIGN
OP

DRAWN
RV

CHECKED
SJ

CORNELL BUS TERMINAL

ROOF FRAMING
PARTIAL PLAN (1/2)

DWG. NO.
S-110

CONT. NO.
PT-17-061-RT

SHEET NO.
161