



CADD FILE NAME: pw:\pwhdrcacan01:HDR CA Canada 01\Documents\548057\10003181\10313648\6.0 CAD BIM\6.2 WIP\6.2.2 Contract Drawings\e Struct\Sheet\HDR 3k pln rf 01.dgn\HDR 3k pln rf 01.dgn
engborc3.dgn (BORDER) FEBRUARY 2, 2020
BLDG. REF. No.
FILENAME: HDR_3k_pln_rf_01.dgn
SHEET No.
DRAWING No. K001

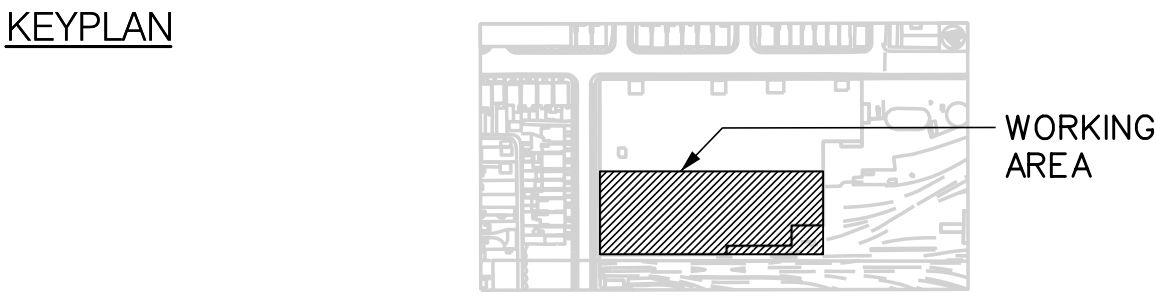

REVISIONS	REVISIONS
△	△
△	△
△	△

ISSUED FOR INFORMATION ONLY
NOT FOR CONSTRUCTION

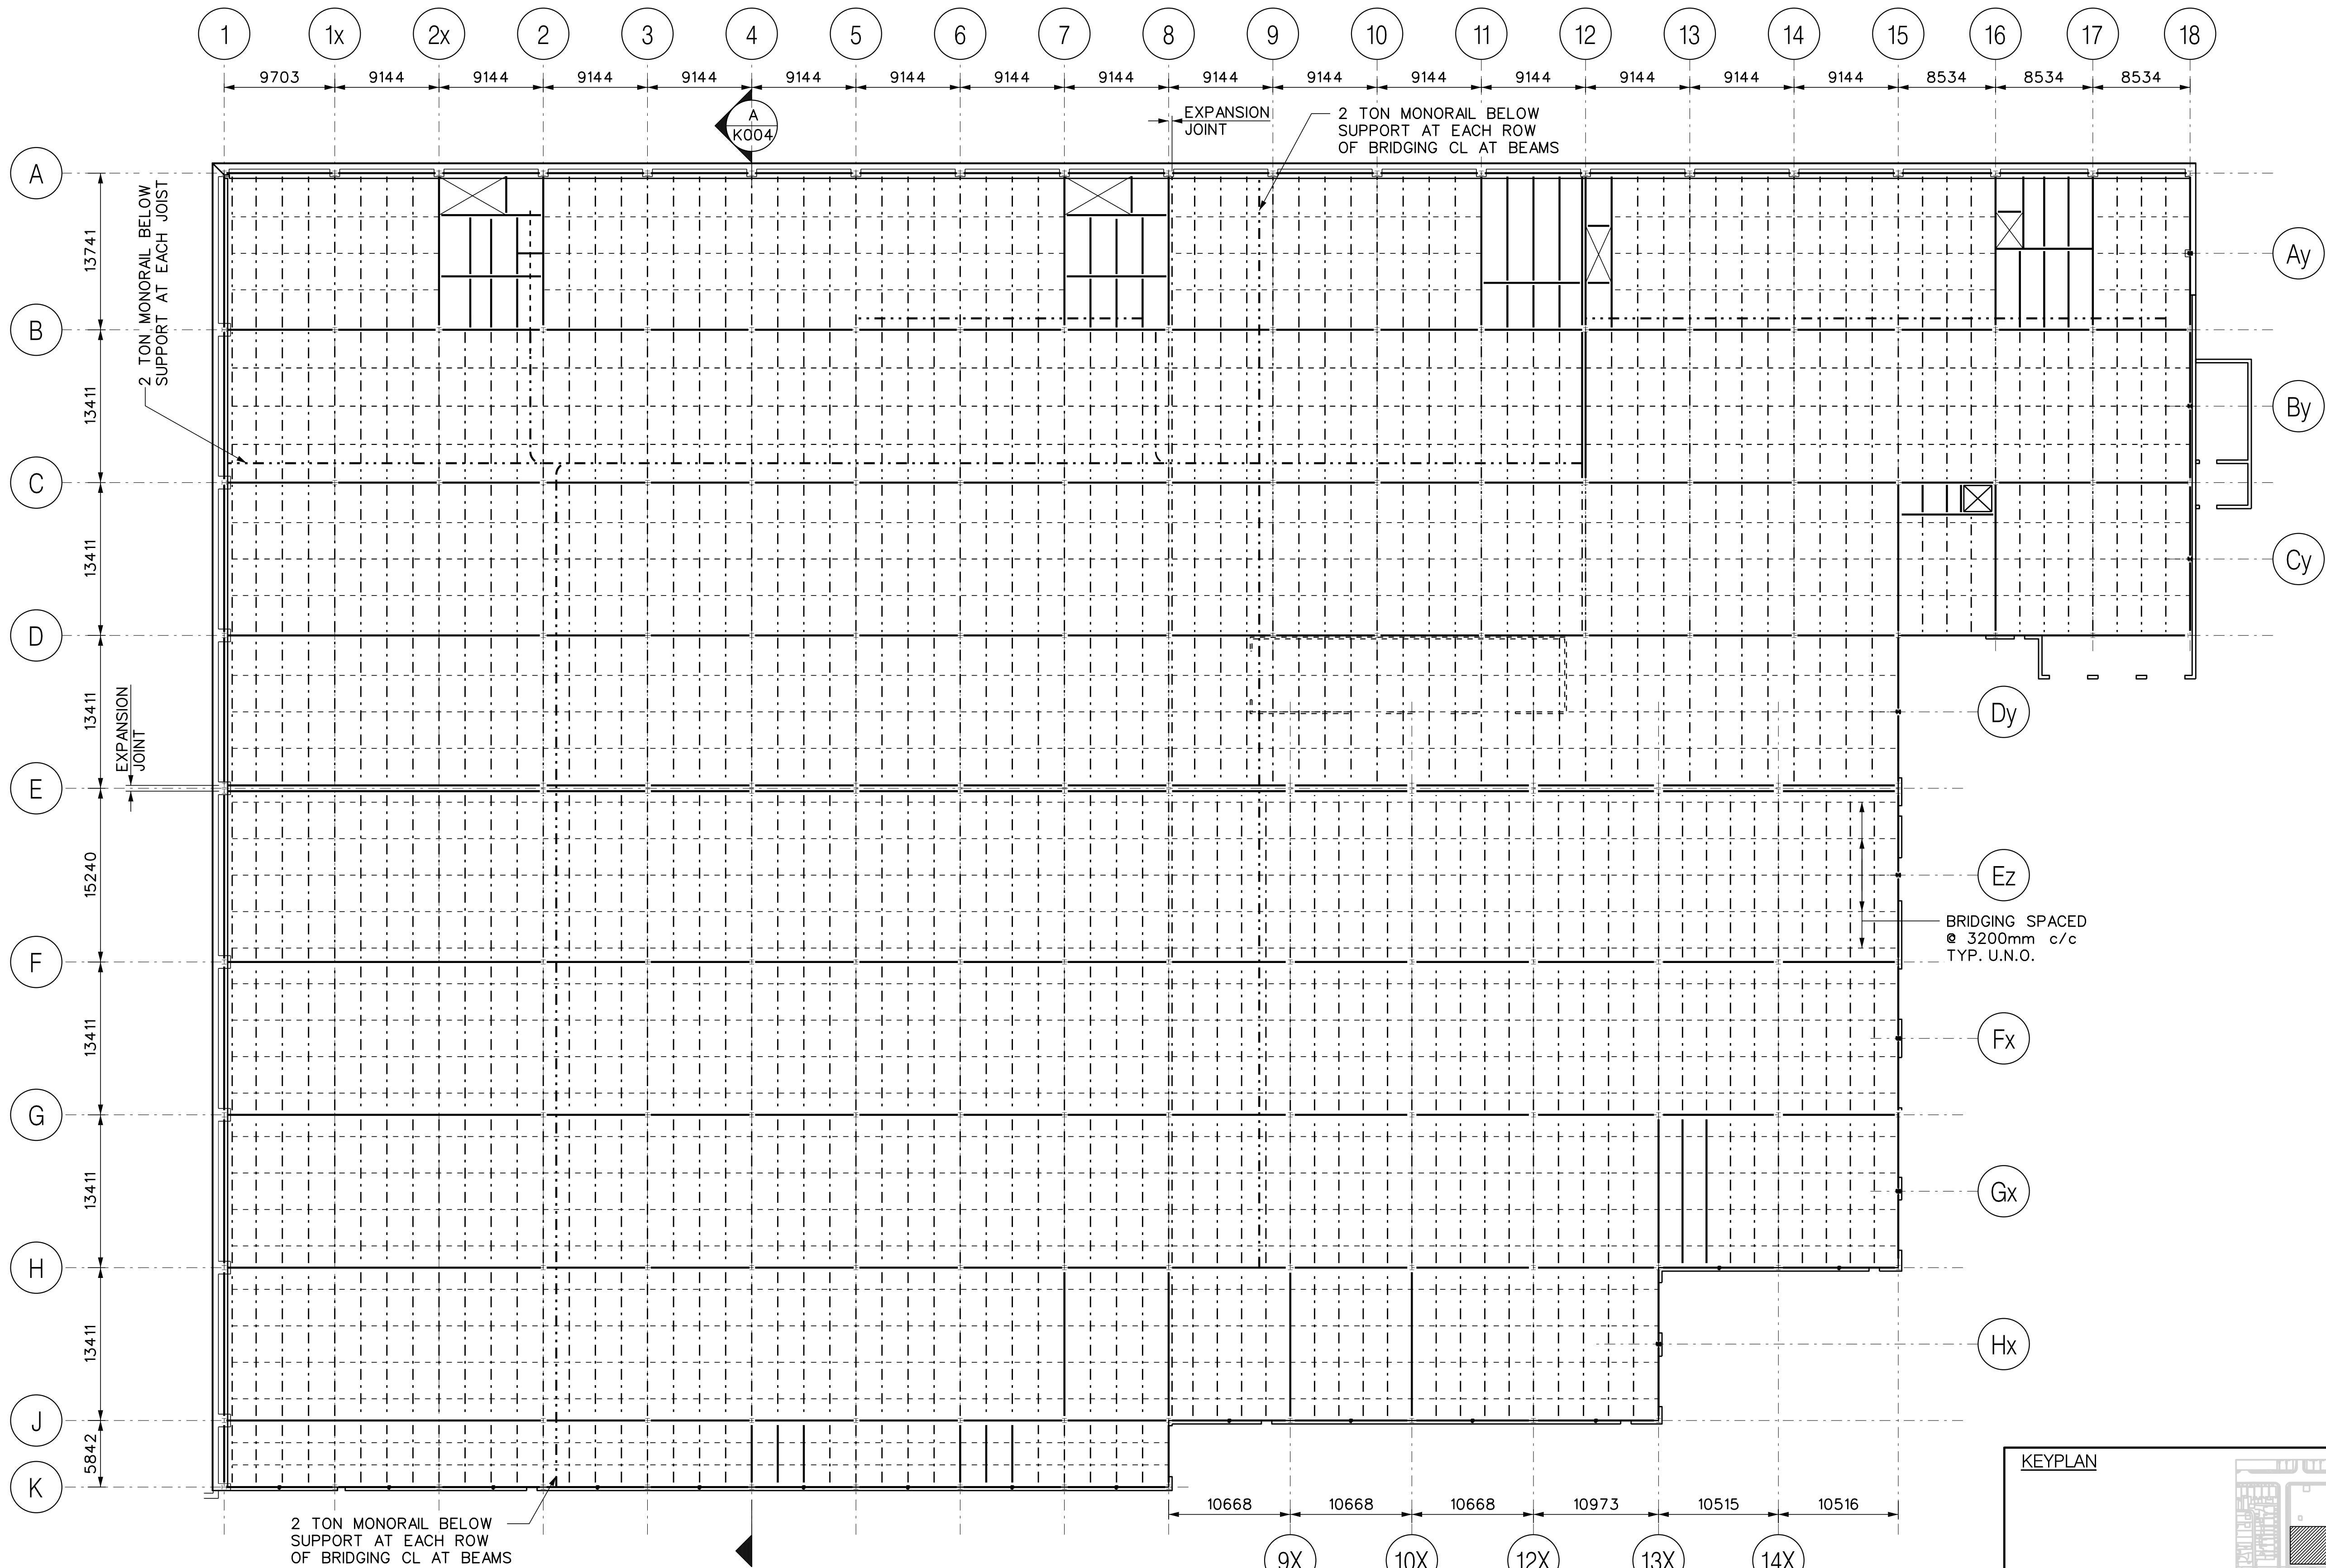

DRAWN	R. VALIENTE	YYYY/MM/DD
CHECKED	M. REZAEI MEHR	09/16/2021
CORRECT		
SCALE	0 2 4 6 8 10 12m	

GREENWOOD OVERHAUL AND SHOP			Contract:	
HIGH LEVEL PLATFORM			TORONTO TRANSIT COMMISSION ENGINEERING DEPARTMENT	
EXISTING ROOF FRAMING PLAN			Dwg. No.	Rev. No.
			K001	
			Sheet No.	