

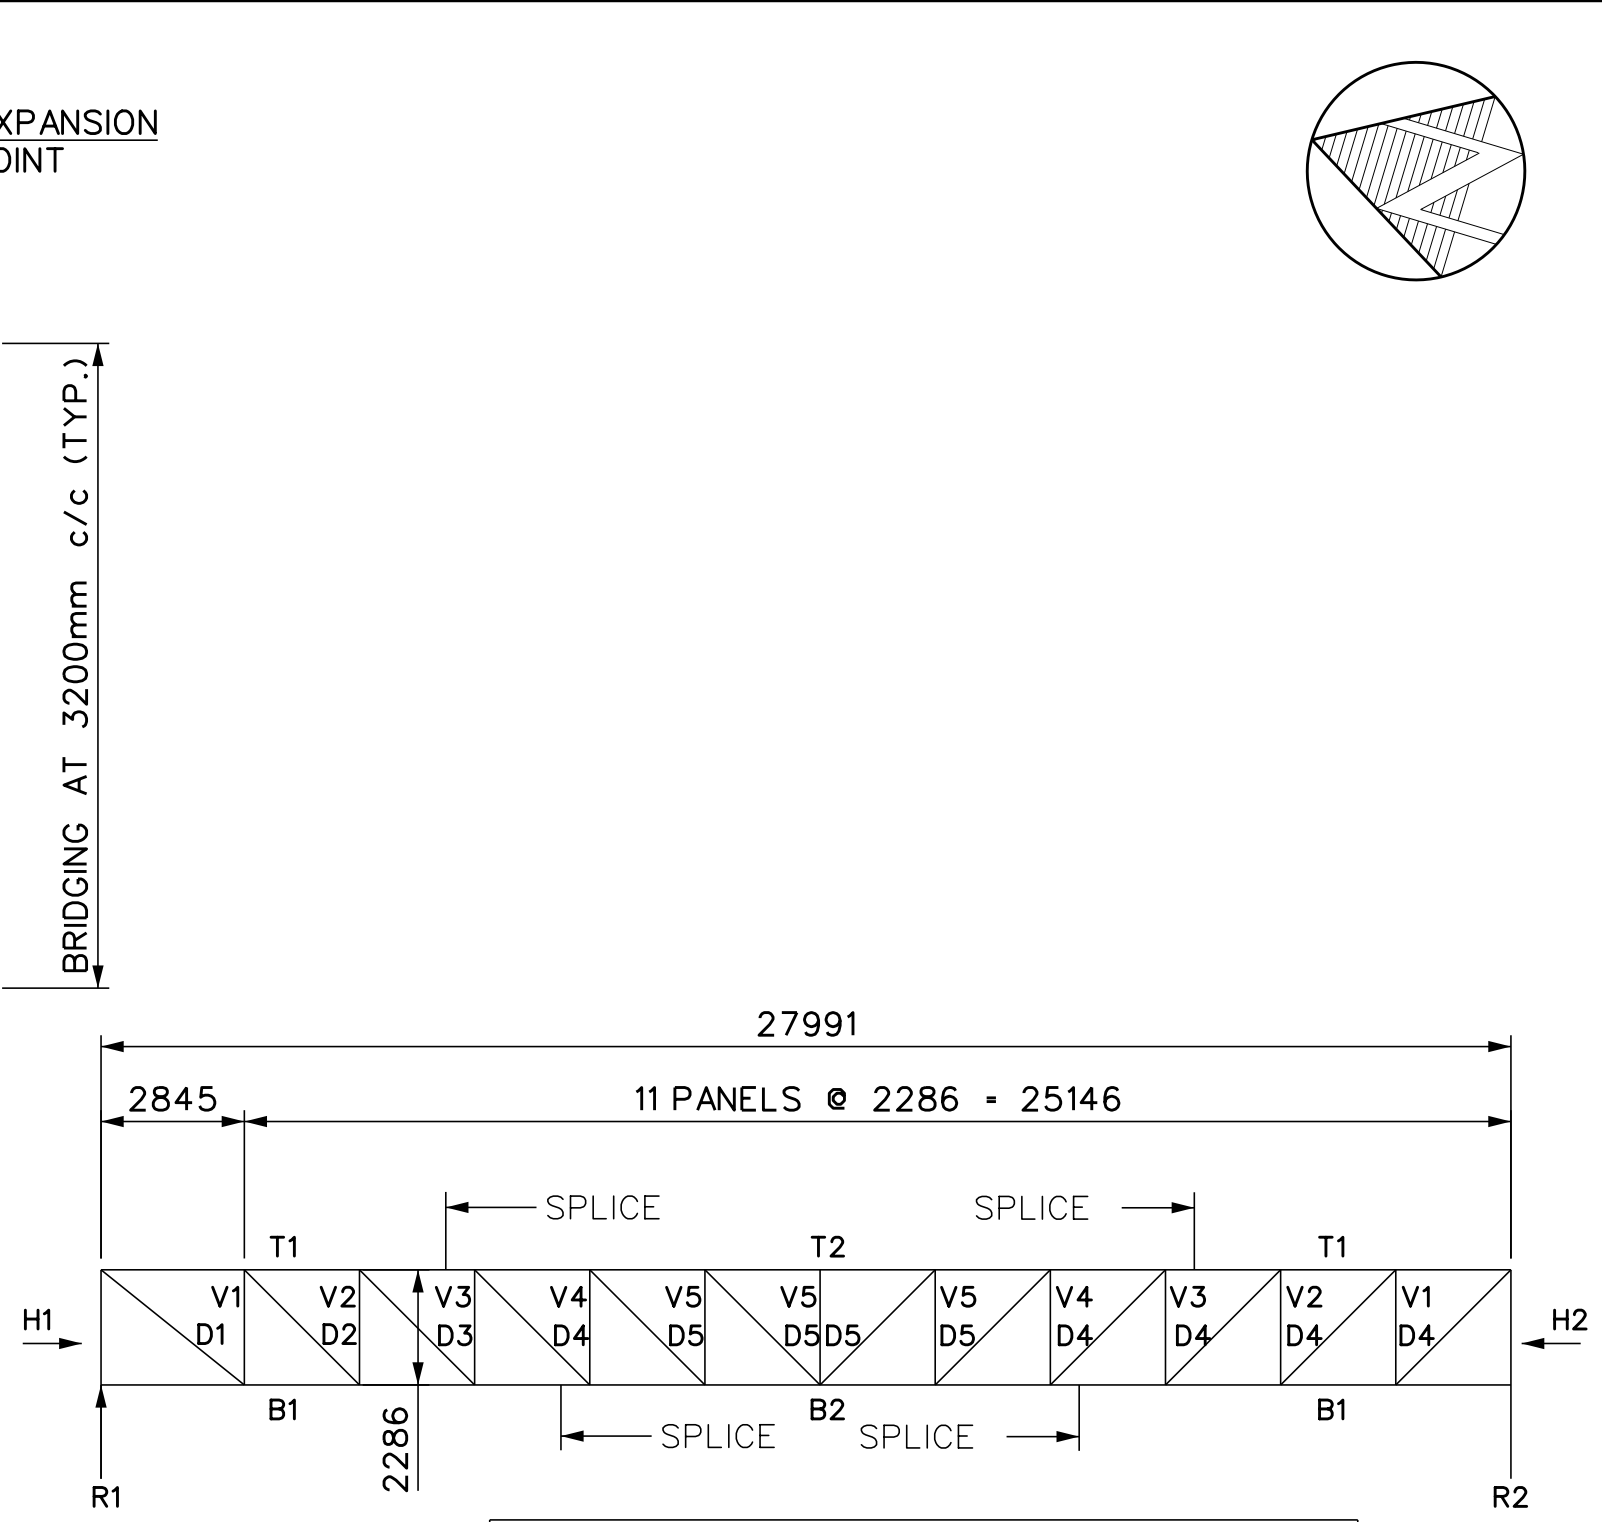



CADD FILE NAME: pw:\pwhdrcan\01\HDR CA Canada 01\Documents\548057\10003181\10313648\6.0 CAD BIM\6.2 WIP\6.2.2 Contract Drawings\e Struct\Sheet\HDR 3k.pln rf 02.dgn\HDR 3k.pln rf 02.dgn
engborc3.dgn (BORDER) FEBRUARY 2, 2020
BLDG. REF. No.
FILENAME: HDR_3k.pln_rf_02.dgn
SHEET No.

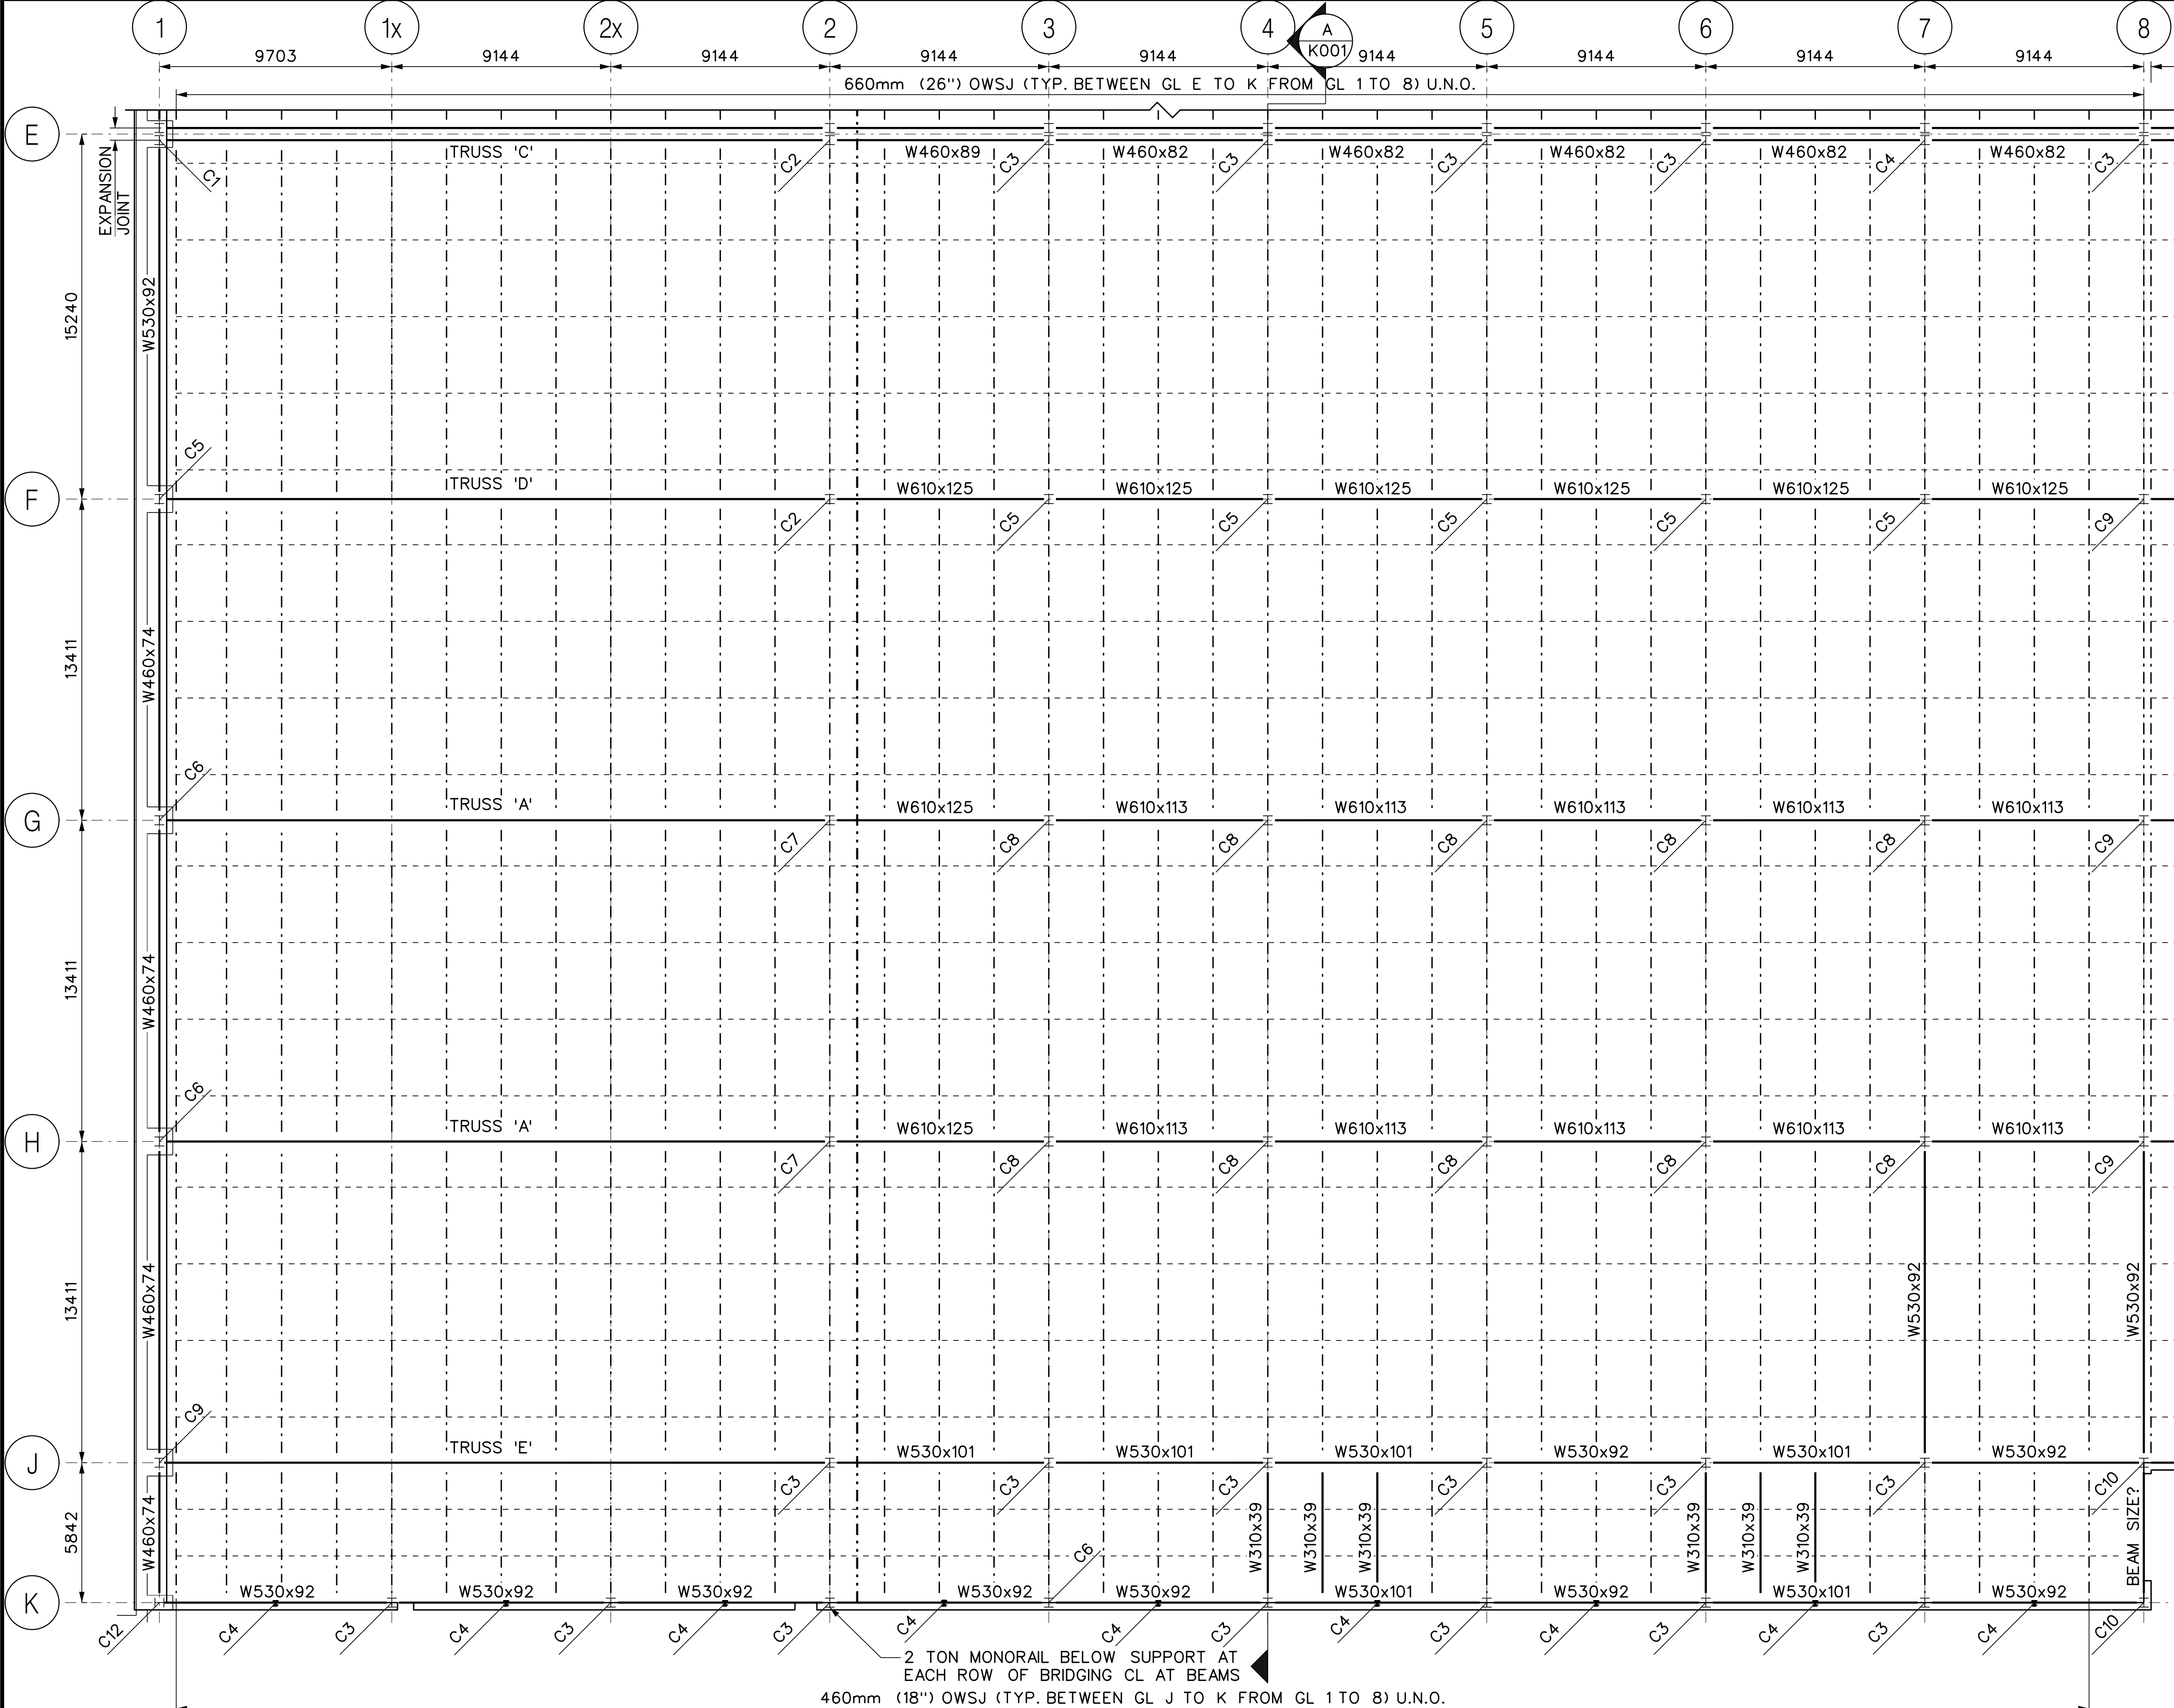

TRUSS SCHEDULE			
TRUSS A		TRUSS D	
MEMBER	SIZE	MEMBER	SIZE
T1	2L203x203x16	T1	2L203x203x16
T2	2L203x203x22	T2	2L203x203x22
B1	2L203x203x14	B1	2L203x203x16
B2	2L203x203x19	B2	2L203x203x22
D1	2L178x102x14	D1	2L178x102x16
D2	2L152x102x11	D2	2L152x102x12.7
D3	2L152x89x9.5	D3	2L152x89x9.5
D4	2L89x76x9.5	D4	2L102x76x9.5
D5	2L89x76x6.4	D5	2L89x76x6.4
V1	2L127x89x12.7	V1	2L127x89x12.7
V2	2L127x89x9.5	V2	2L127x89x11
V3	2L102x76x9.5	V3	2L102x89x9.5
V4	2L89x76x7.9	V4	2L102x76x7.9
V5	2L89x76x6.4	V5	2L89x76x6.4

COLUMN SCHEDULE	
MARK	SIZE
C1	W360x509
C2	W360x592
C3	W360x196
C4	W200x46
C5	W360x262
C6	W360x382
C7	W360x551
C8	W360x237
C9	W360x287
C10	W360x216
C11	W360x314
C12	W360x122

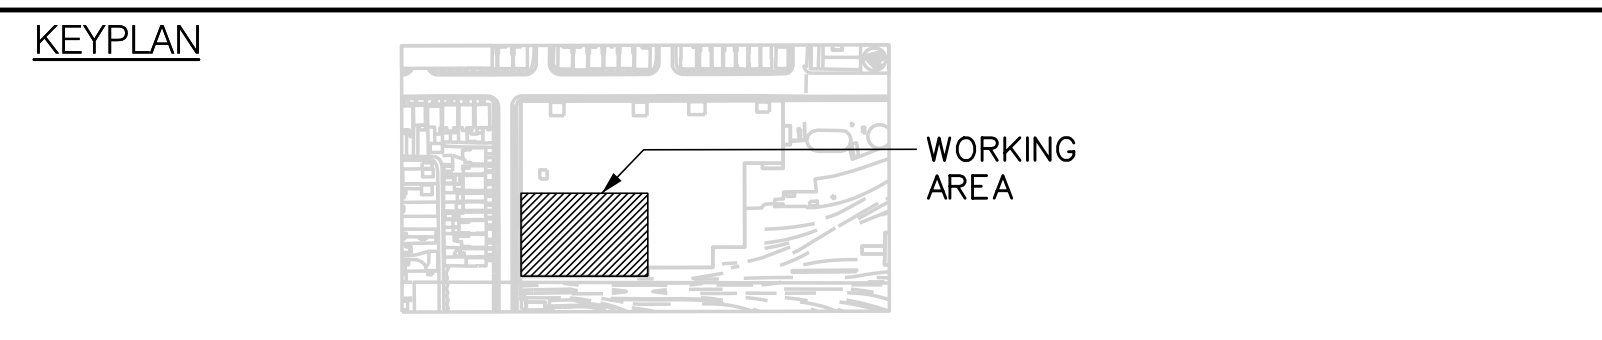

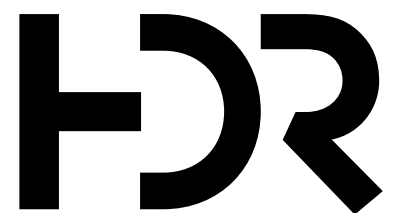REVISIONS		REVISIONS		ISSUED FOR INFORMATION ONLY NOT FOR CONSTRUCTION		 Gannett Fleming A JOINT VENTURE		DRAWN <u>R. VALIENTE</u> YYYY/MM/DD 09/16/2021 CHECKED <u>M. REZAEI MEHR</u> CORRECT SCALE		GREENWOOD OVERHAUL AND SHOP HIGH LEVEL PLATFORM EXISTING ROOF FRAMING PARTIAL PLAN SHEET 1 OF 2		Contract:  TORONTO TRANSIT COMMISSION ENGINEERING DEPARTMENT Dwg. No. <u>K002</u> Rev. No. <u>1</u> Sheet No. <u>1</u>	
-----------	--	-----------	--	---	--	---	--	--	--	--	--	---	--