CADD FILE NAME: pw:\\pwhdrcacan01:HDR_CA_Canada_01\Documents\548057\10003181\10313648\6.0_CAD_BIM\6.2_WIP\6.2.2_Contract Drawings\e_Struct\Sheet\HDR_3k_sec_01.dgn\HDR_3k_sec_01.dgn


engbord3.dgn (BORDER) FEBRUARY 2, 2020


BLDG. REF. No.

FILENAME: HDR_3k_sec_01.dgn

SHEET No.

DRAWING No.

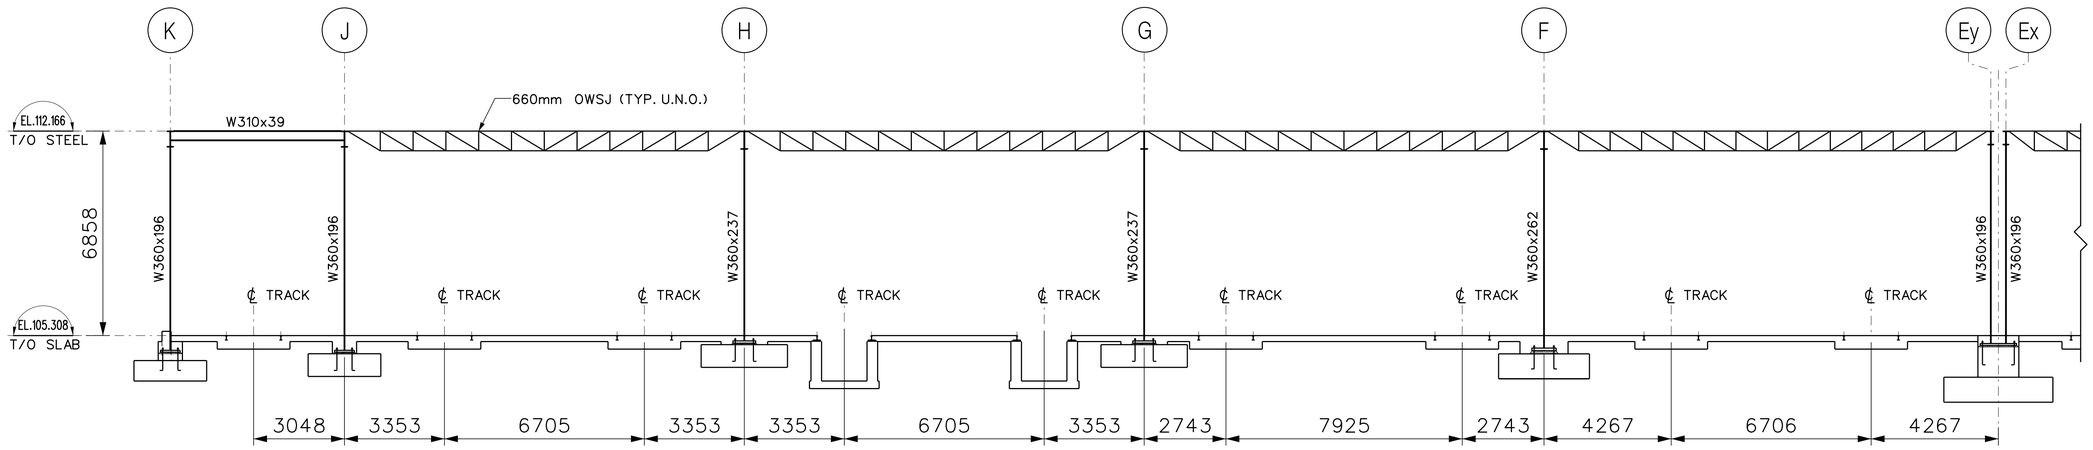

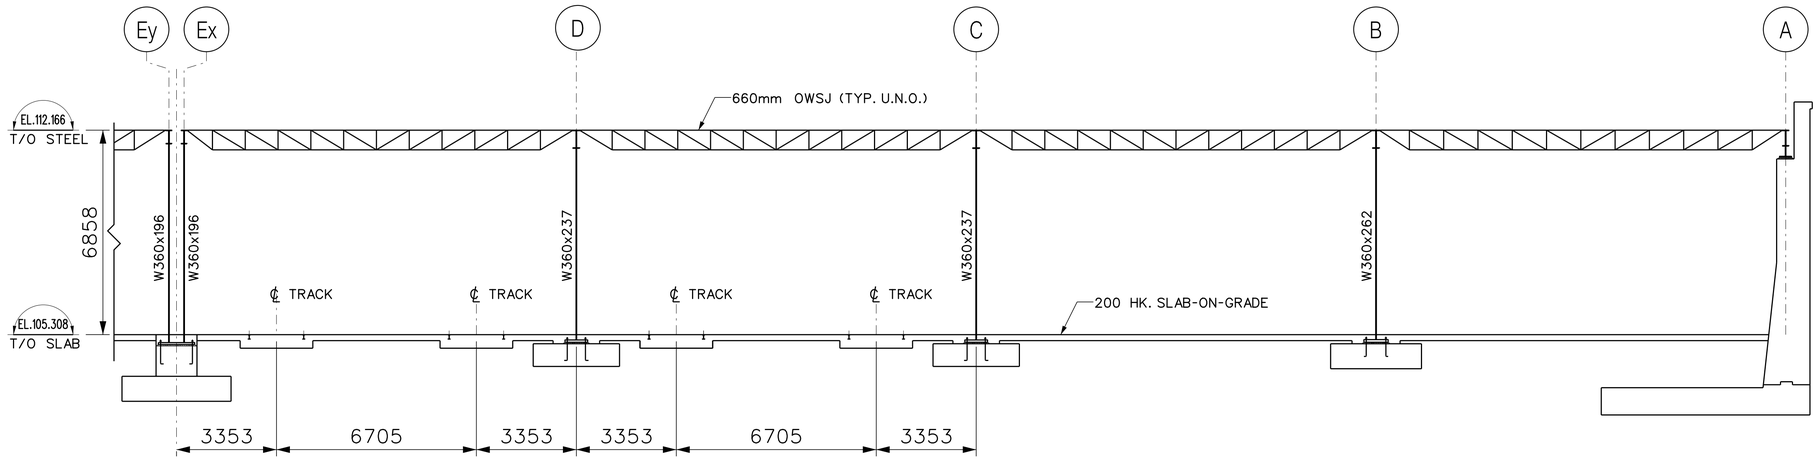

SECTION
AT GRIDLINE 4

A
K001, K002

KEYPLAN

REVISIONS	REVISIONS

ISSUED FOR INFORMATION ONLY
NOT FOR CONSTRUCTION

HDR Gannett Fleming
A JOINT VENTURE

DRAWN R. VALIENTE YYYY/MM/DD 10/13/2021
CHECKED M. REZAEIMEHR
CORRECT
SCALE

GREENWOOD OVERHAUL AND SHOP

HIGH LEVEL PLATFORM

BUILDING SECTION

Contract:

TORONTO TRANSIT COMMISSION
ENGINEERING DEPARTMENT

Dwg. No.	Rev. No.	Sheet No.
K004		

Plot Date: 20-OCT-2021