


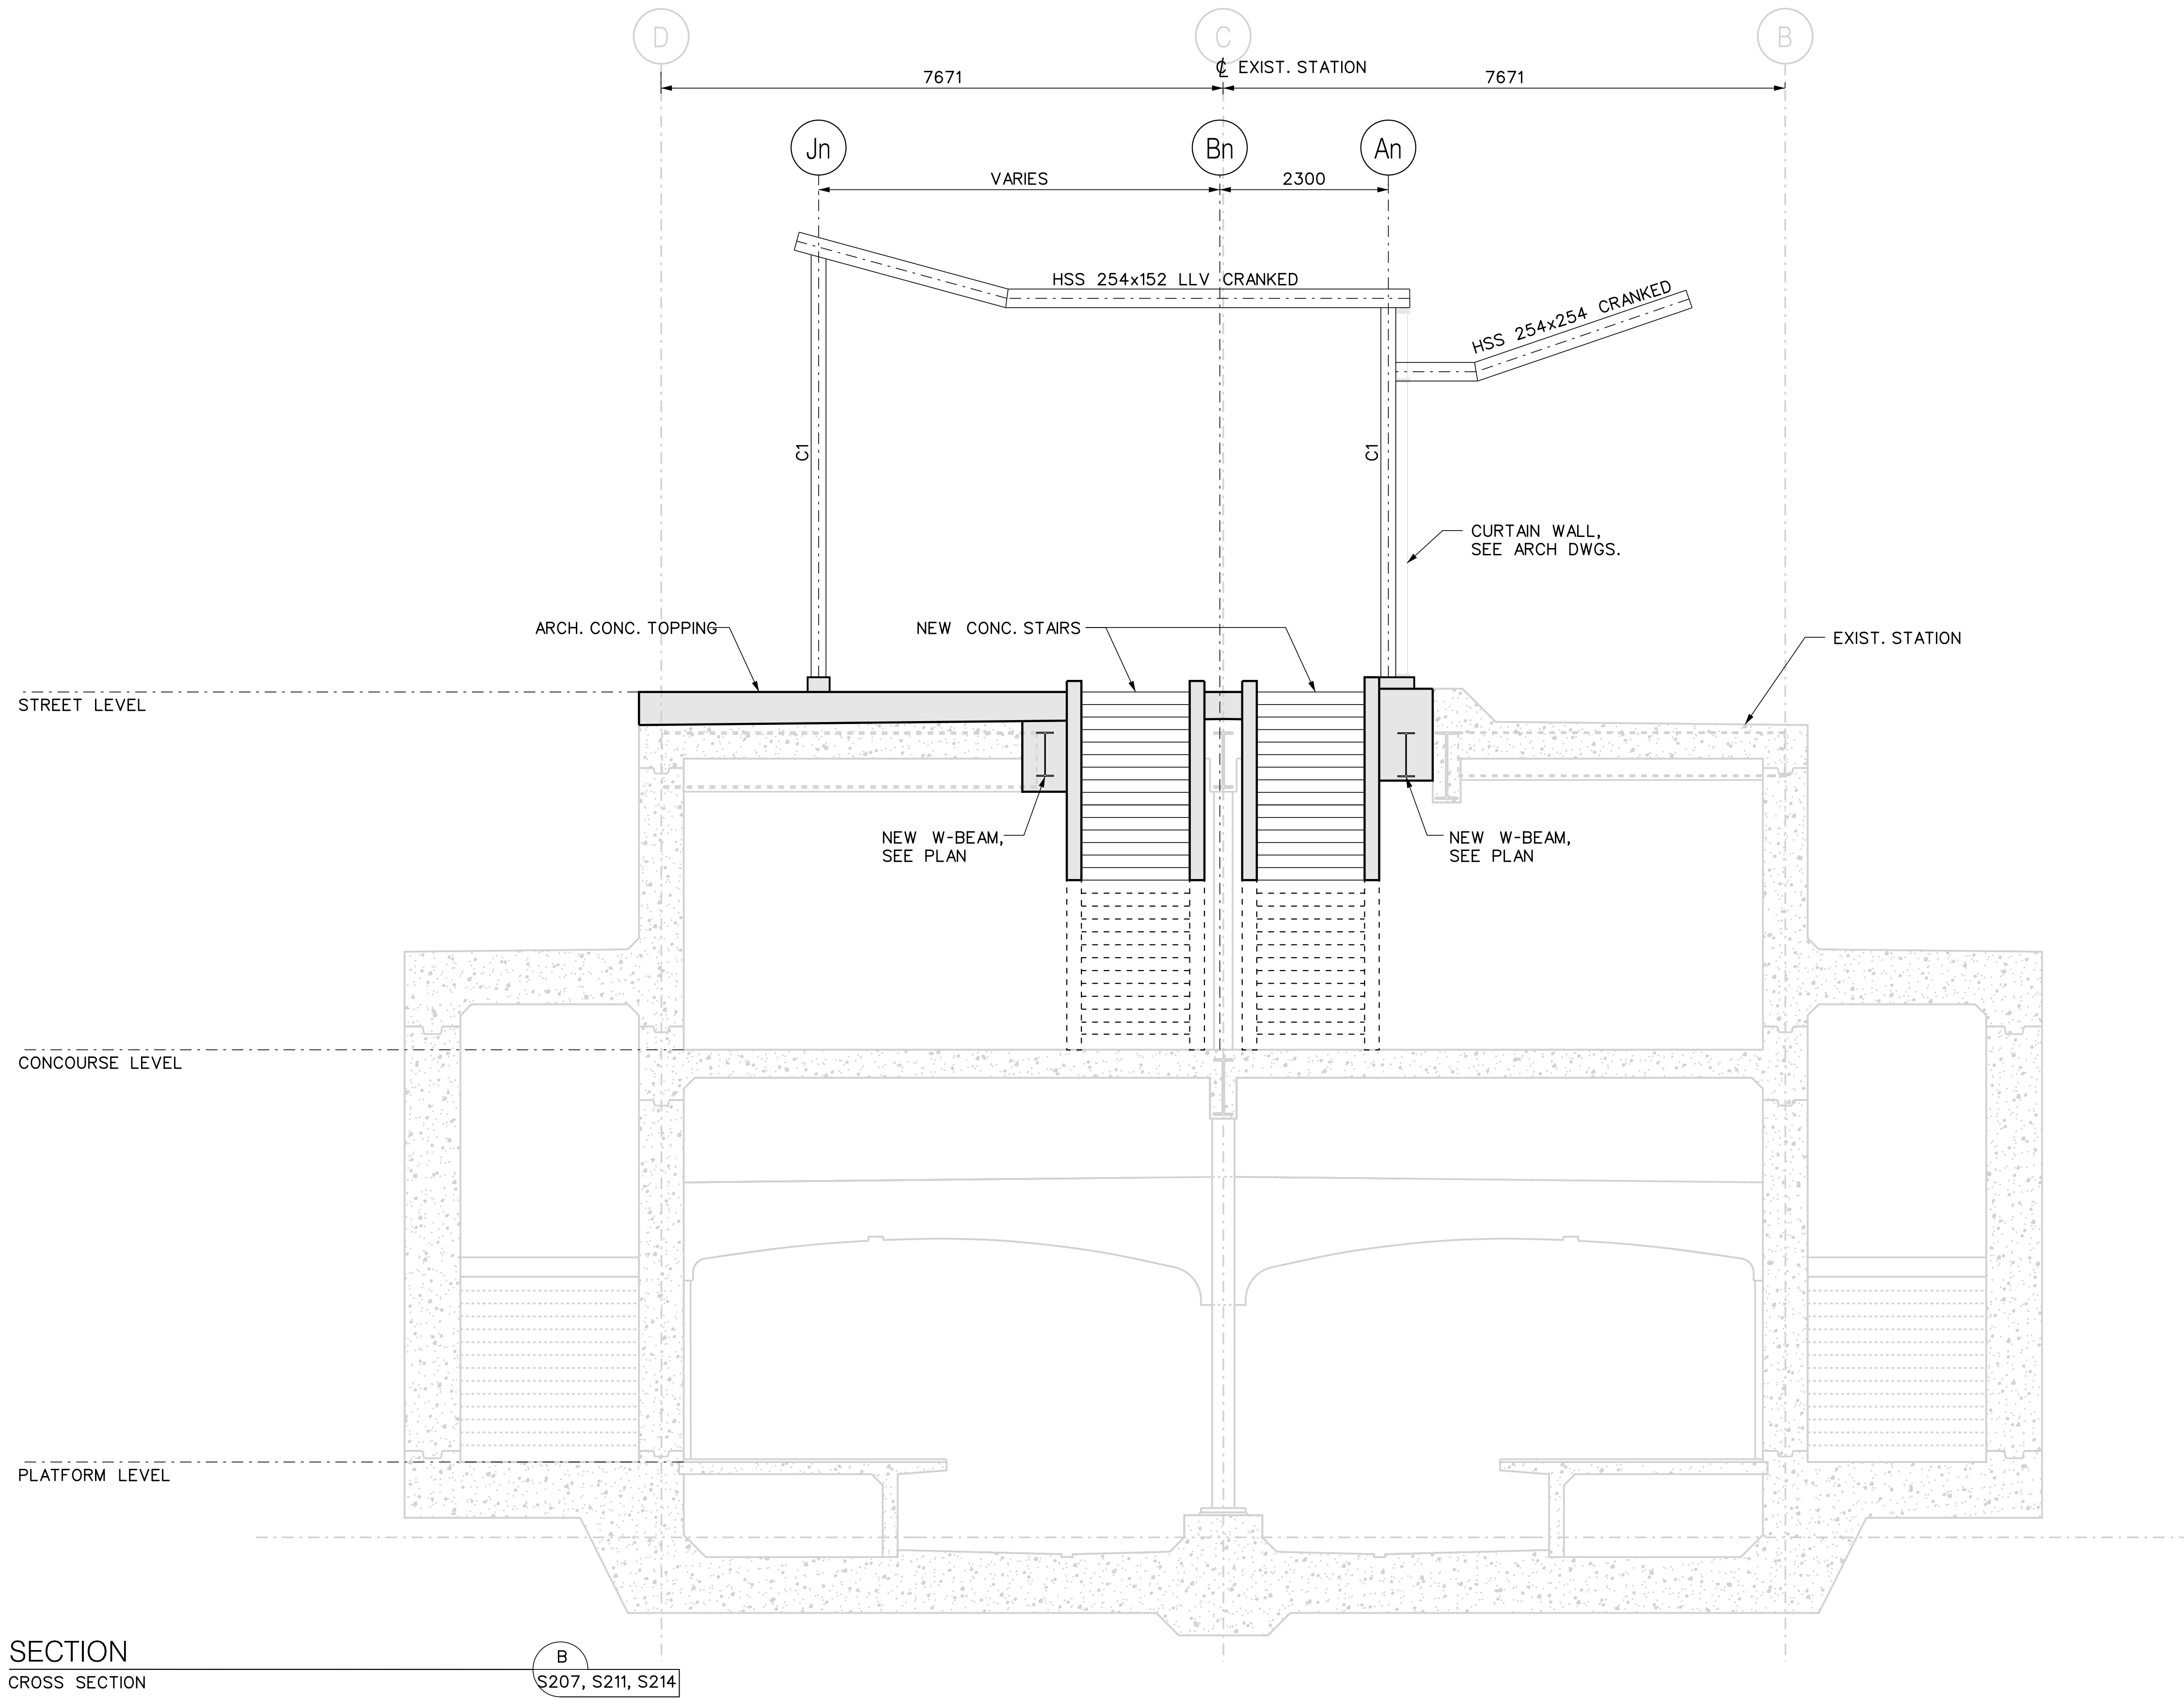

- NOTES:
1. ALL BEAMS CONNECTING TO THE COLUMNS OR PASSING ON TOP OF THE COLUMNS HAVE RIGID CONNECTION TO THE COLUMNS/BEAMS.
 2. FOR COLUMN SCHEDULE REFER TO PLANS.

- LEGEND:
- NEW CONCRETE
 - EXISTING CONCRETE

SECTION
CROSS SECTION

B
S207, S211, S214

REVISIONS	REVISIONS
△	△
△	△
△	△

10% REVIEW
DRAWING
NOT FOR CONSTRUCTION



DRAWN	B. CHIRKOV	YYYY/MM/DD
CHECKED	J. BRATA BOSE	2022-12-16
CORRECT	A. DEHGHANI	2022-12-16
SCALE		

LINE 2 – CAPACITY ENHANCEMENT		Contract: G85-399B	
STAGE GATE 2 – JANE STATION			
SECTION A		Dwg. No. G85-399B-S301	Rev. No. Sheet No.