


engbdr03.dgn (BORDER) FEBRUARY 2, 2020

BLDG. REF. No.

FILENAME: HDR_3s_elev_01.dgn

SHEET No.

DRAWING No. G85-399B-S321

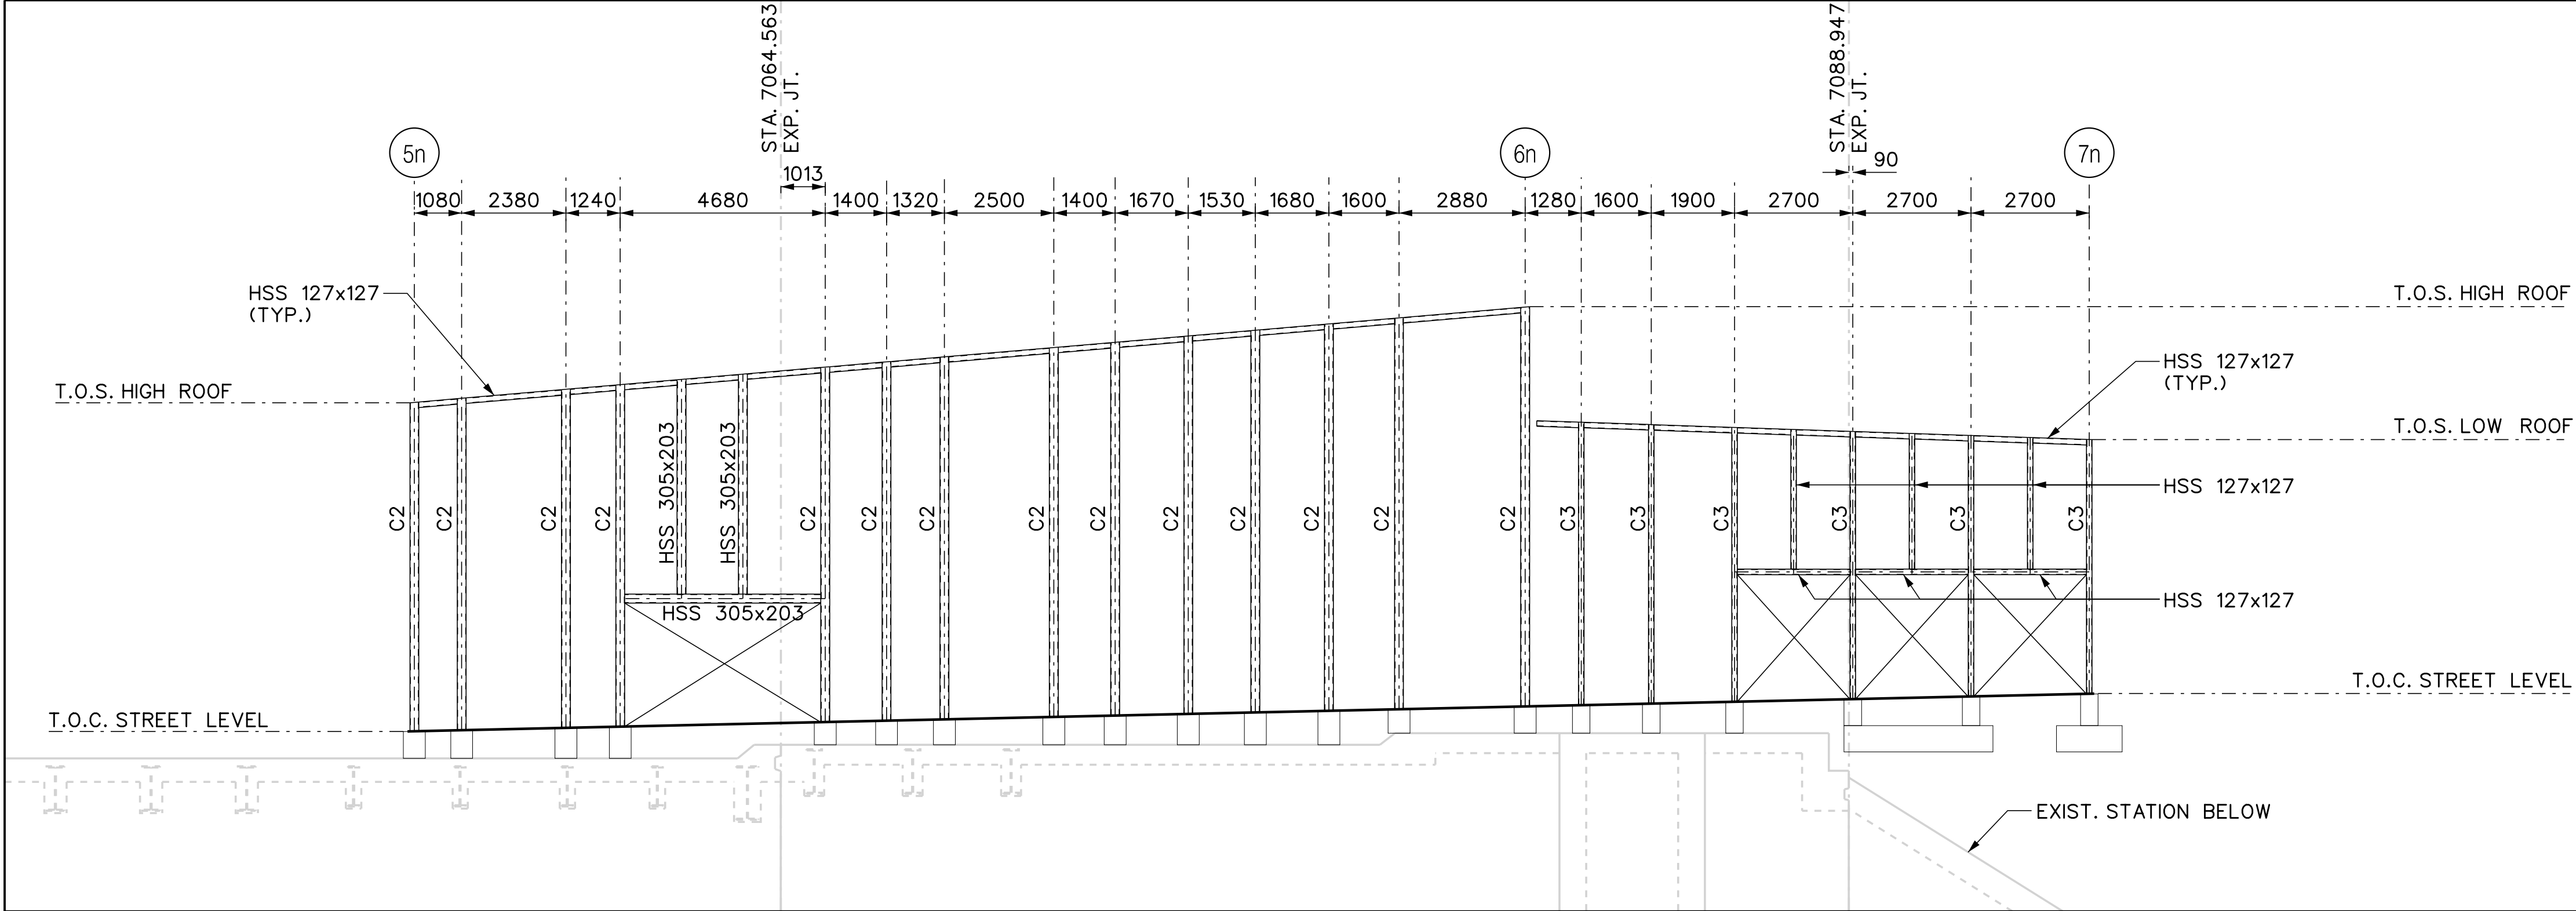


NOTE:
FOR COLUMN SCHEDULE REFER TO PLANS.

ELEVATION

STRUCTURAL ELEVATION AT G.L. En

A
G85-399B-S321

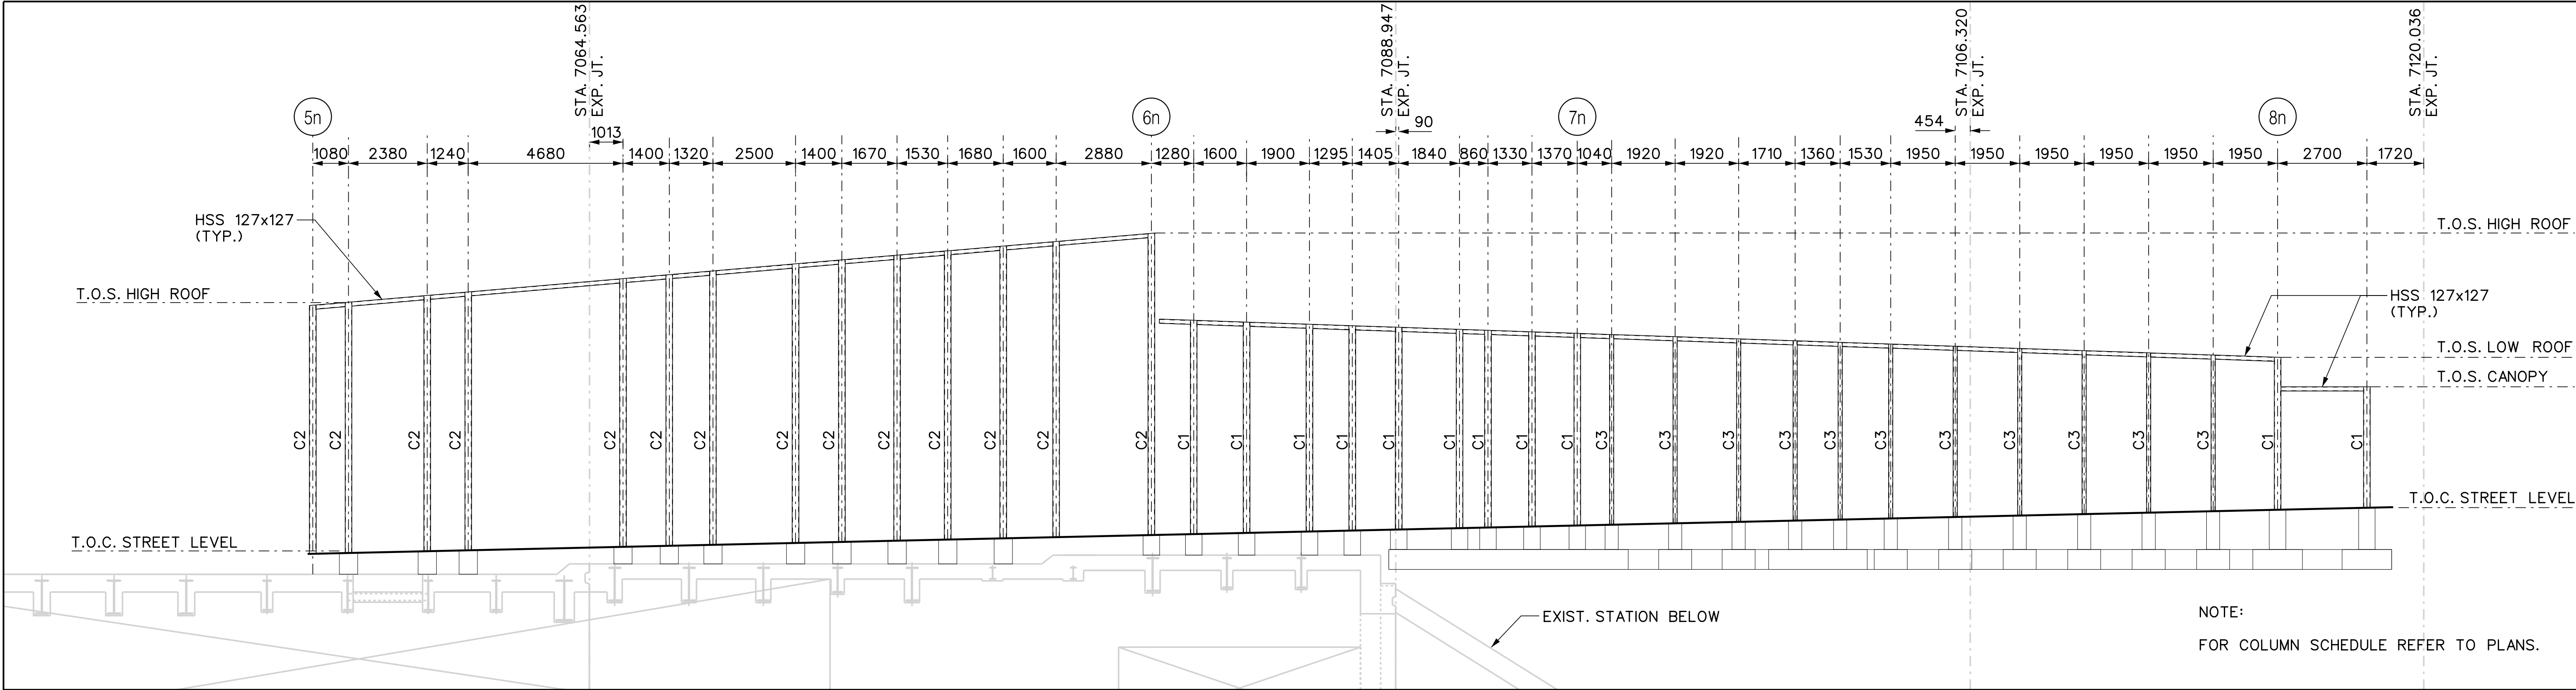

NOTE:
FOR COLUMN SCHEDULE REFER TO PLANS.

ELEVATION

STRUCTURAL ELEVATION AT G.L. Dn

B
G85-399B-S321

REVISIONS	REVISIONS
△	△
△	△
△	△

10% REVIEW
DRAWING
NOT FOR CONSTRUCTION



DRAWN	B.CHIRKOV	YYYY/MM/DD
CHECKED	J.BRATA BOSE	2022-12-16
CORRECT	A.DEHGHANI	2022-12-16
SCALE		

LINE 2 – CAPACITY ENHANCEMENT		Contract: G85-399B
STAGE GATE 2 – JANE STATION		
STRUCTURAL ELEVATIONS SHEET 1 OF 3		TORONTO TRANSIT COMMISSION ENGINEERING DEPARTMENT
Dwg. No. G85-399B-S321	Rev. No.	Sheet No.