



engh003.dgn (BORDER) FEBRUARY 2, 2020
BLDG. REF. No.
HDR_3s_pln_rf_02.dgn
FILENAME:
SHEET No. 00
DRAWING No. G85-399B-S211

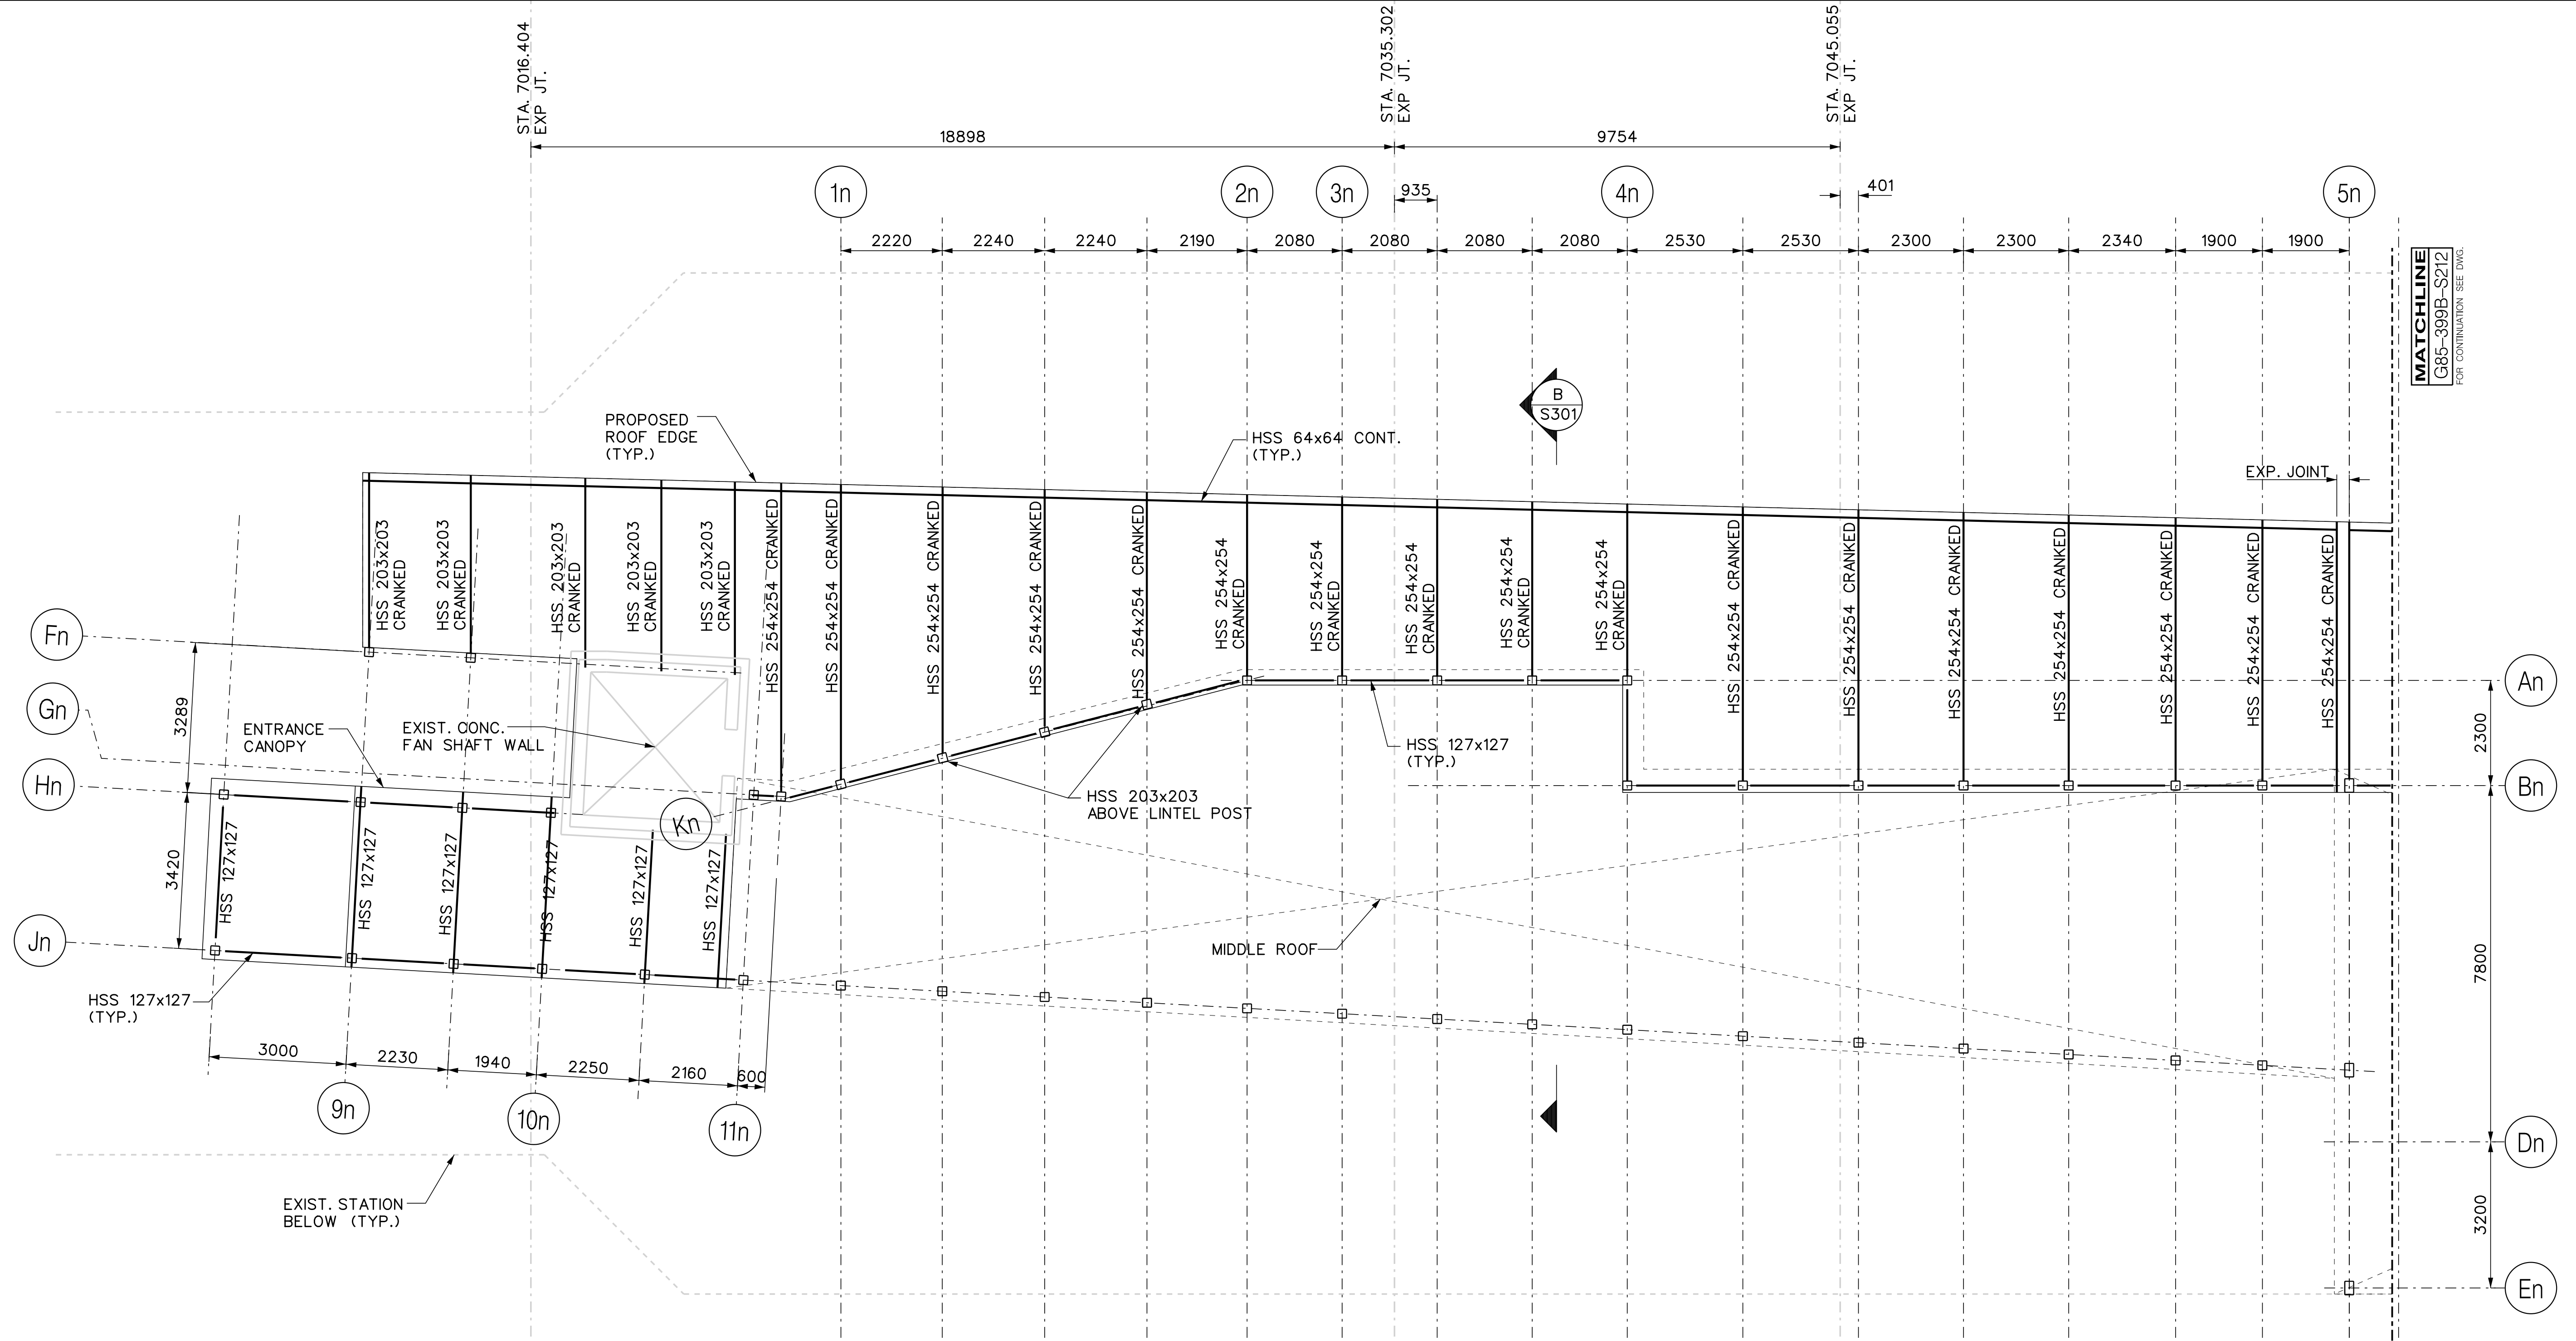

- NOTES:
- ALL BEAMS CONNECTING TO THE COLUMNS OR PASSING ON TOP OF THE COLUMNS HAVE RIGID CONNECTION TO THE COLUMNS/BEAMS.

PARTIAL PLAN
HEADHOUSE LOW ROOF PLAN
1
G85-399B-S022

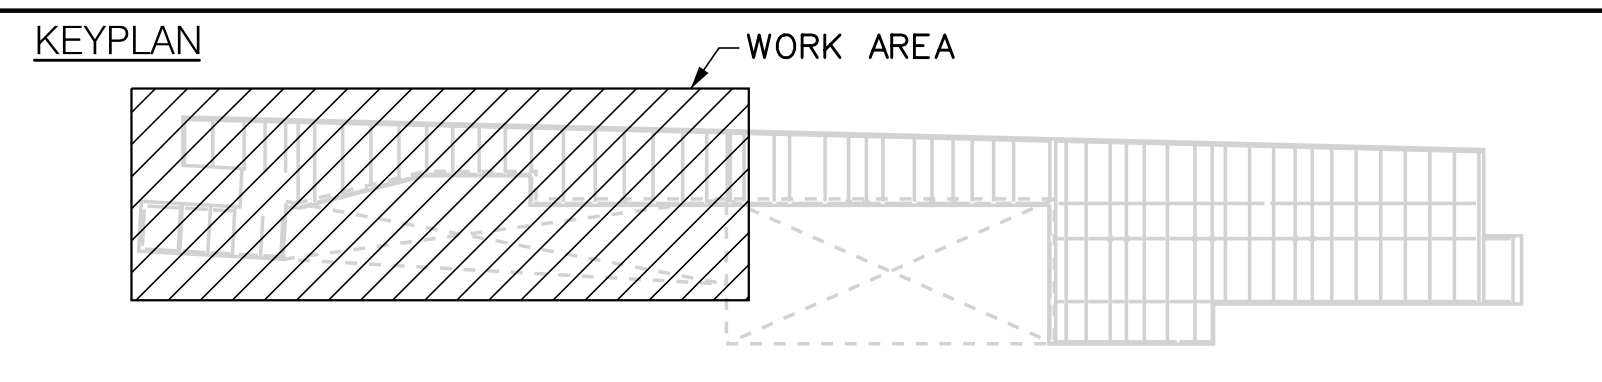

REVISIONS		REVISIONS		10% REVIEW DRAWING NOT FOR CONSTRUCTION		GANNETT FLEMING A JOINT VENTURE		HDR		DRAWN: B. CHIRKOV 2022-12-16 CHECKED: J. BRATA BOSE 2022-12-16 CORRECT: A. DEHGHANI 2022-12-16 SCALE: 0 1 2 3m		LINE 2 – CAPACITY ENHANCEMENT		Contract: G85-399B	
												STAGE GATE 2 – JANE STATION		TORONTO TRANSIT COMMISSION ENGINEERING DEPARTMENT	
												HEADHOUSE LOW ROOF PARTIAL PLAN PART 1		Dwg. No. G85-399B-S211 Rev. No. Sheet No.	