



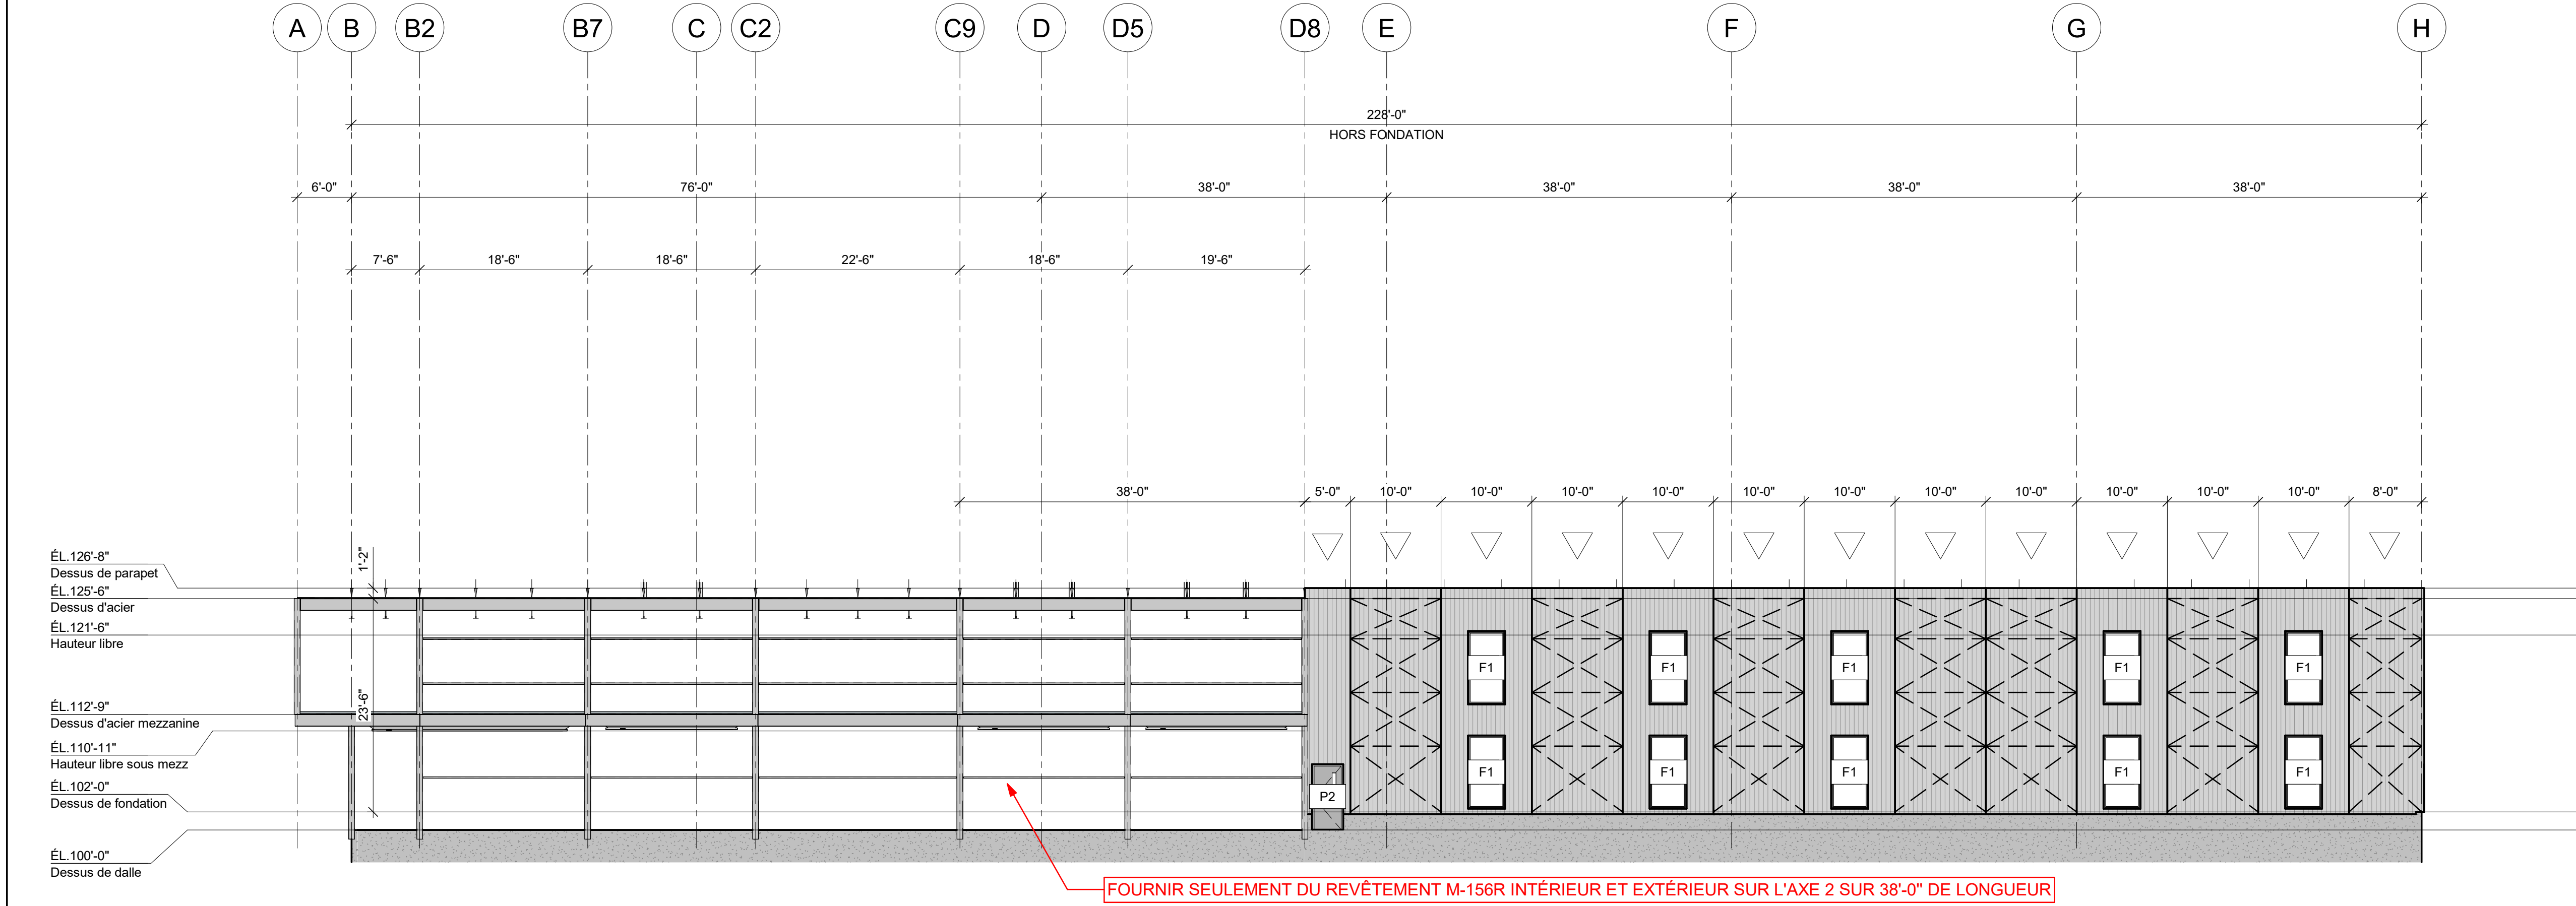


ÉLÉVATION AXE 1 & 2 (SUD)
3/32" = 1'-0"

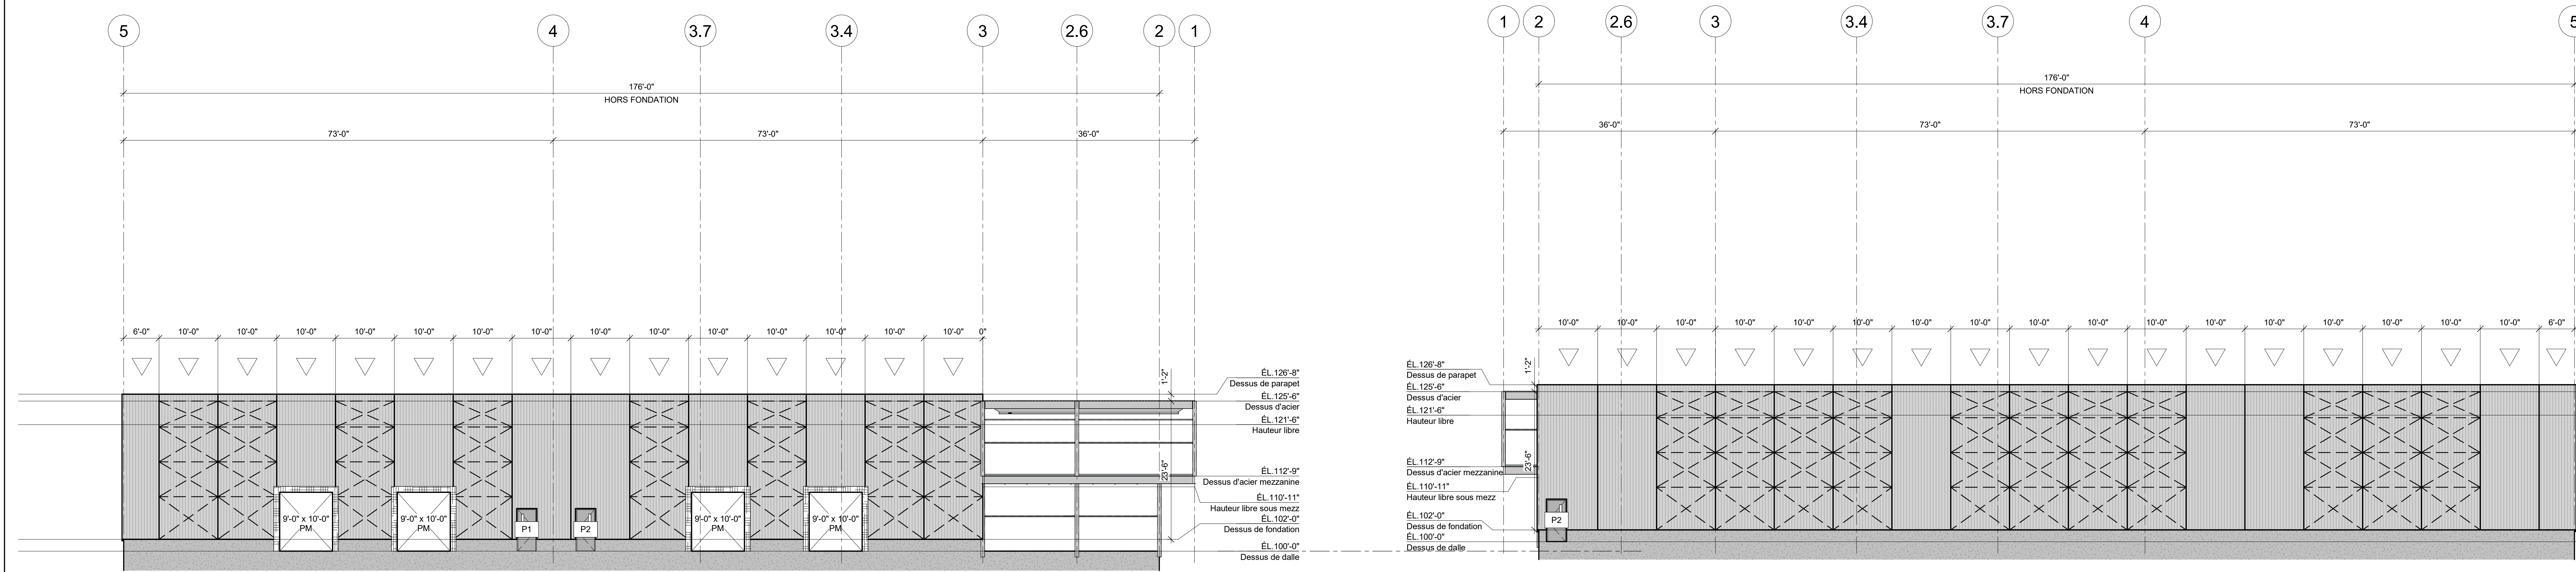


ÉLÉVATION AXE A & B (OUEST)
3/32" = 1'-0"

ÉLÉVATION AXE D8 & H (EST)
3/32" = 1'-0"

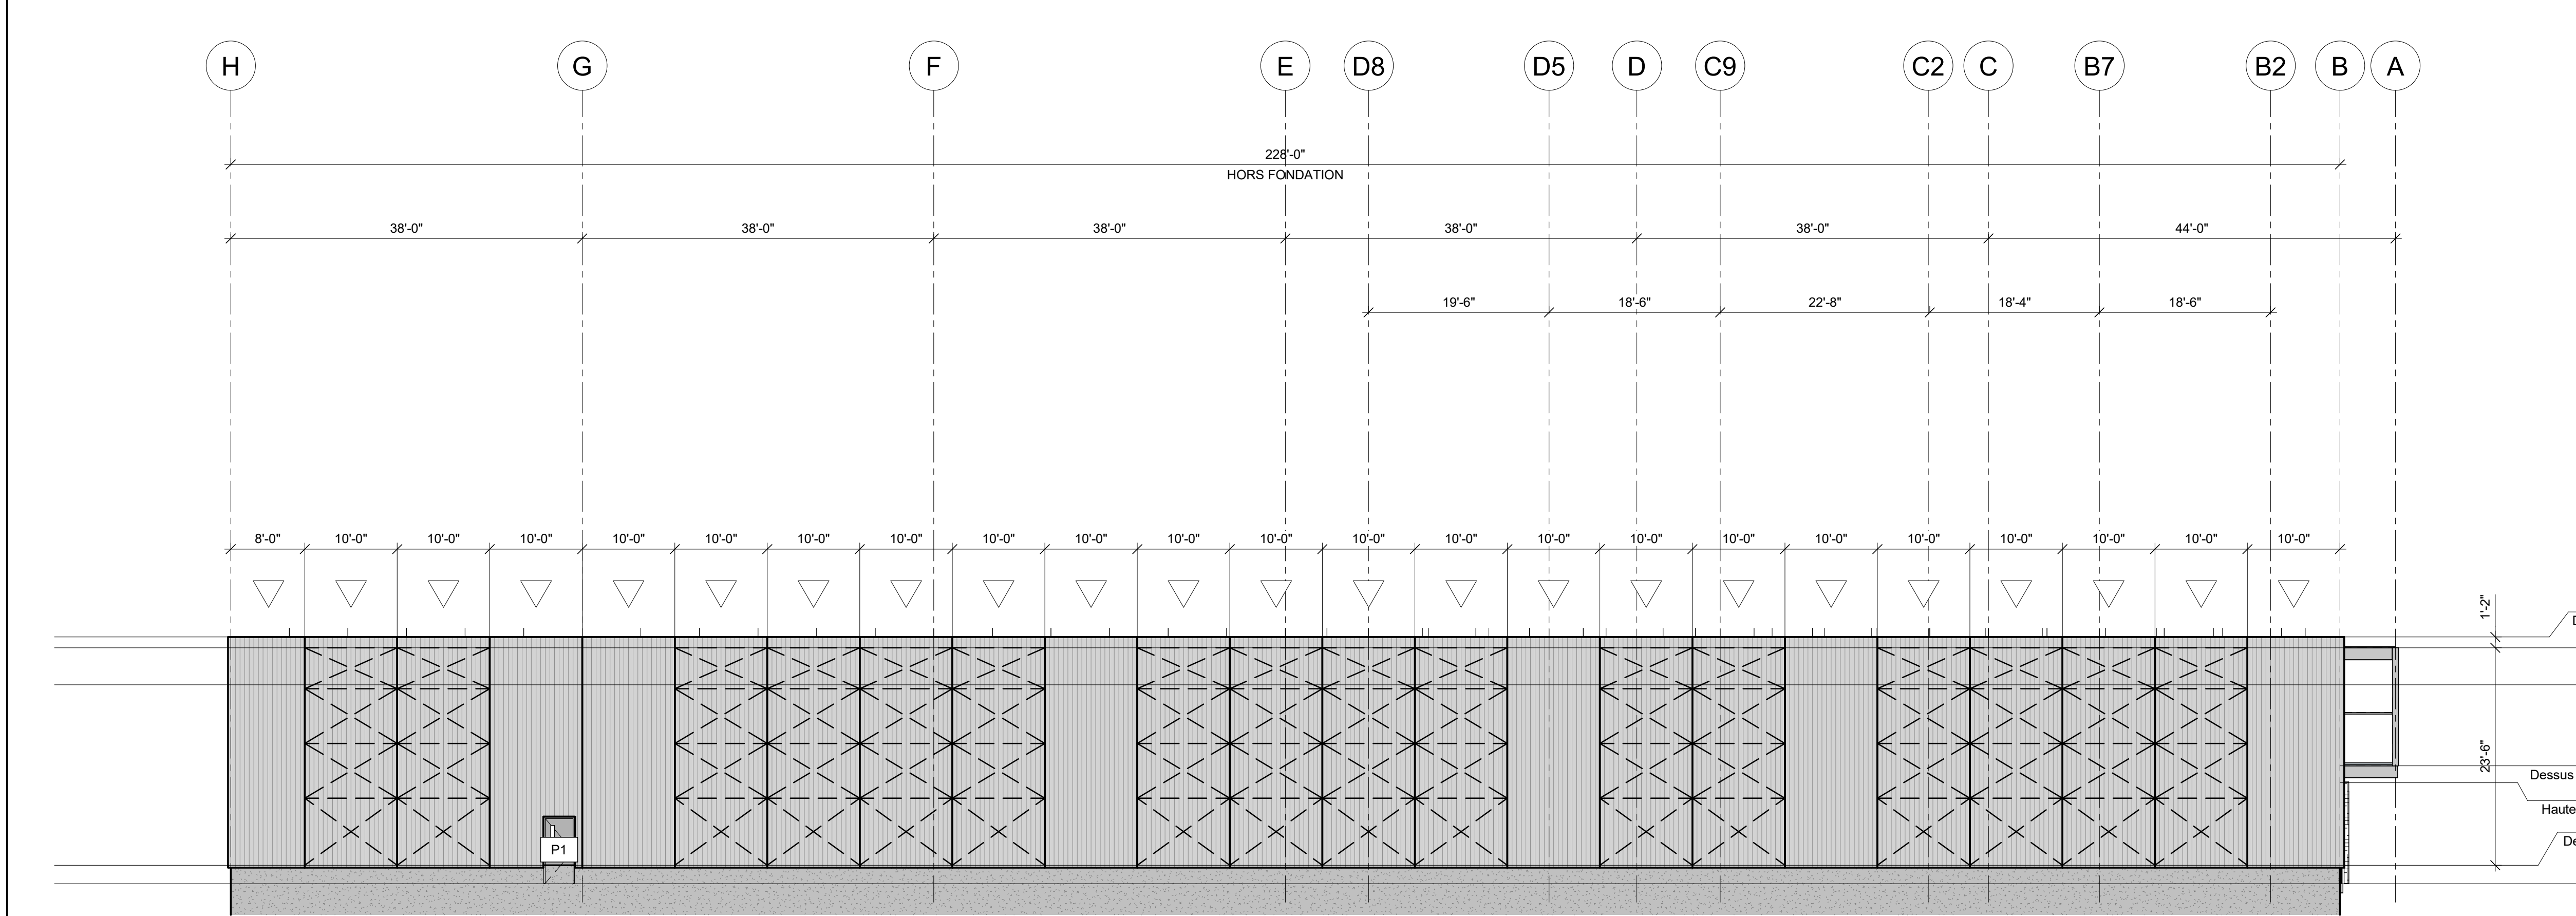

ÉLÉVATION AXE 3 & 5 (NORD)
3/32" = 1'-0"

- Quincaillerie standard du fournisseur:
- Chamères : Stanley FBB179 4.5" x 4"
 - Barre panique : Von Duprin 22 x 689 avec poignée extérieure 230L
 - Cylindre permanent : Schlage 20001C 626
 - Ferme-porte : LCN 1261 689
 - Coupe-froid de tête et des montants : Unique 1650
 - Coupe-froid du bas : Unique DS4
 - Seuil : Voir la remarque dans la "Cédule de porte"

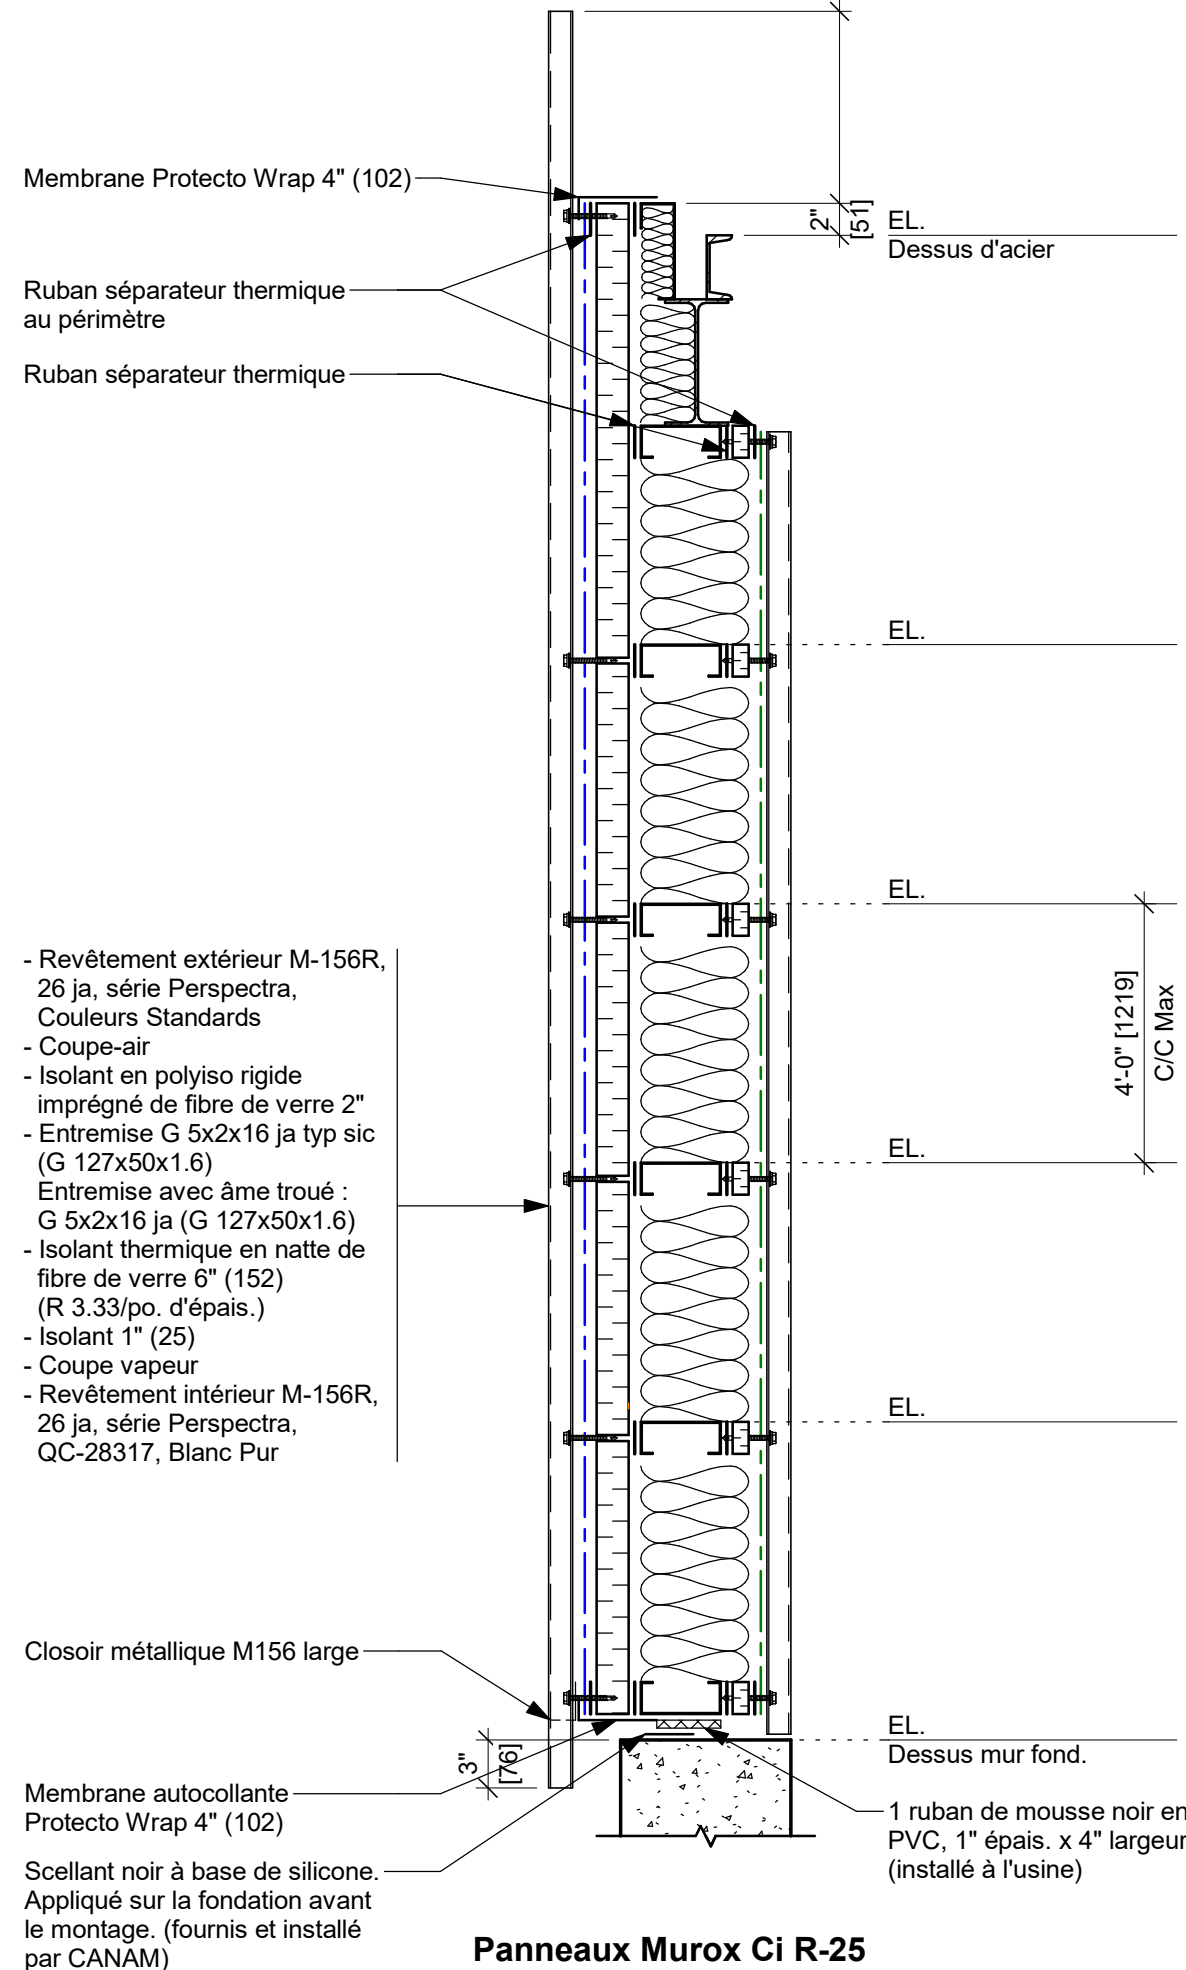

COUPE DE MUR - TYPE
1" = 1'-0"

CÉDULE DES FENÊTRES					
Identifiant	Qté	Installation	Description	Dimensions ext. cadre largeur X hauteur	Remarques
F1	10		Fenêtre en aluminium fixe avec bris thermique et verre scellé + Low-E argon clair	4'-0" x 8'-0"	Cadre d'Aluminium (Blanc ext. et int.)

CÉDULE DES OUVERTURES			
Total	Type	Tag	Commentaires

CÉDULE DES PORTES													
Identifiant	Qté	Installation	Porte 16 ja.		Vitrage		Cadre d'acier 16 ja., avec bris thermique	(3) Pentures @ tige fixe	Poignée seulement	Barre panique sans poignée ext. 22EO	Quincaillerie avec poignée ext. 230L	Verrou en surface (Porte inactive)	Seuil machiné
			Isolation (R12)	Dimensions (R12)	Sens ouv.	Largeur							
P1	2			3'-0" x 7'-0"		5'	1'-8"						
P2	3			3'-0" x 7'-0"		5'	1'-8"						

CÉDULE DES P.M. ET DES OUVERTURES			
Total	Type	Tag	Commentaires
4	9'-0" x 10'-0"	PM	
Total général: 4			