



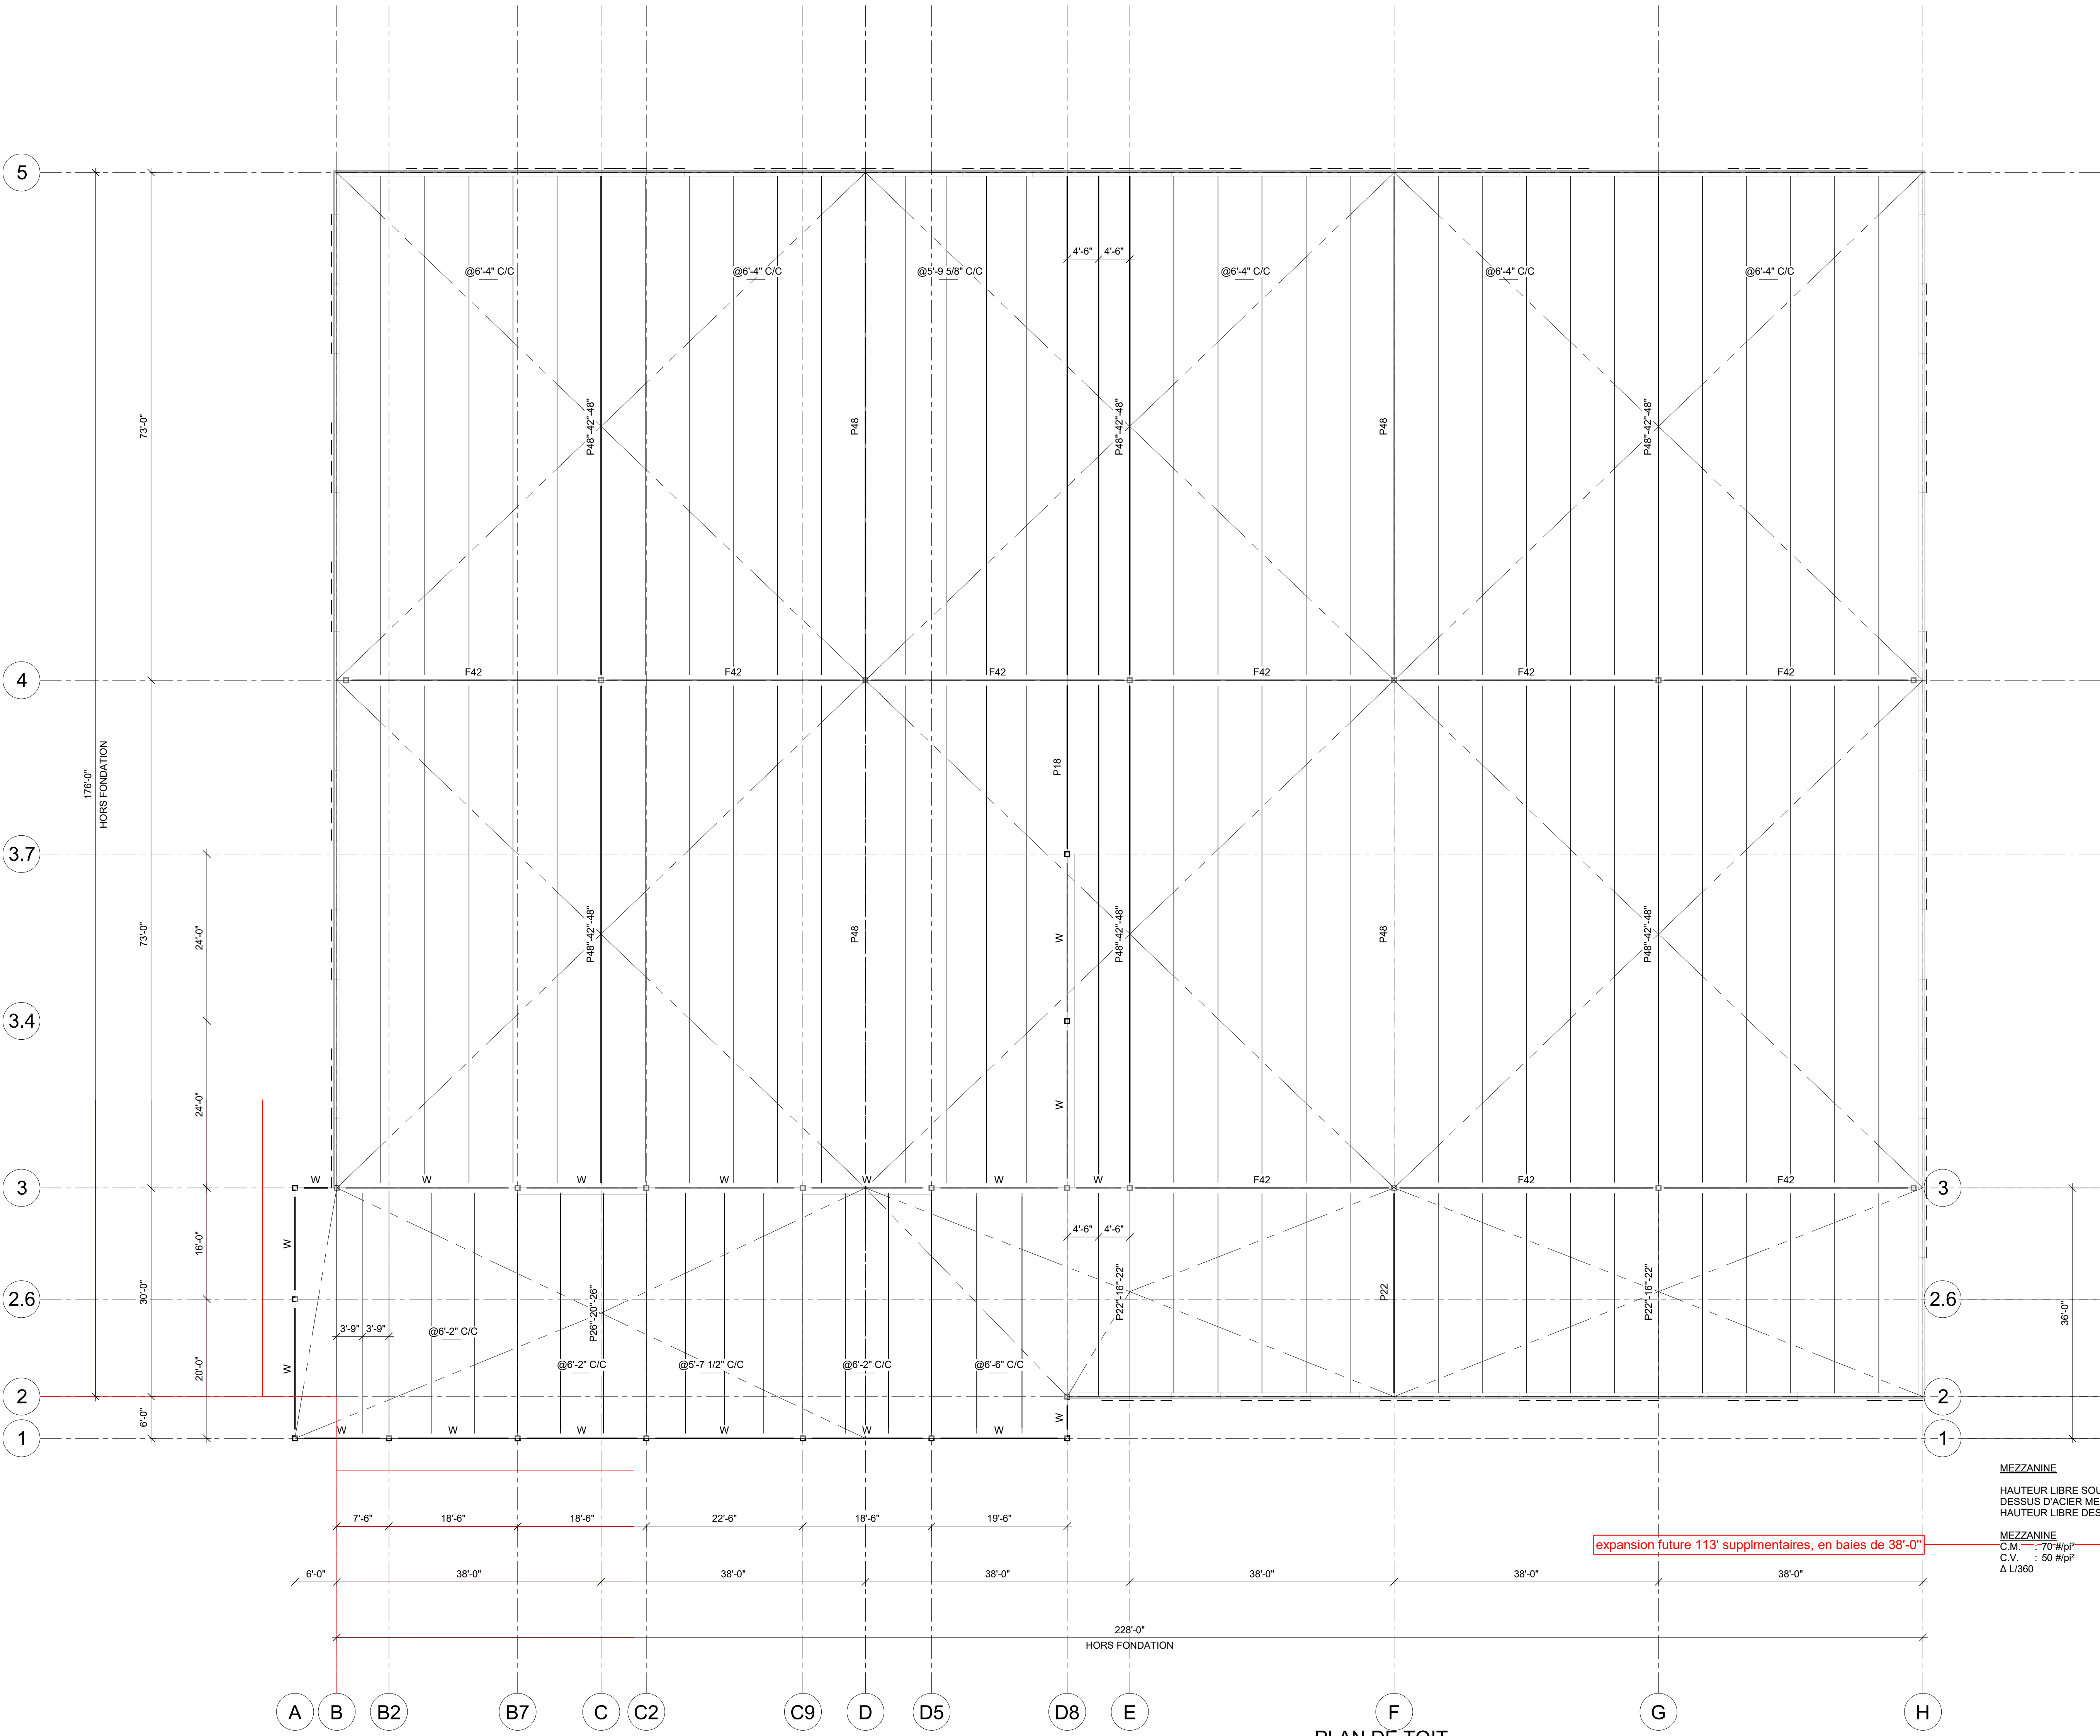


PLAN DE TOIT
3/32" = 1'-0"

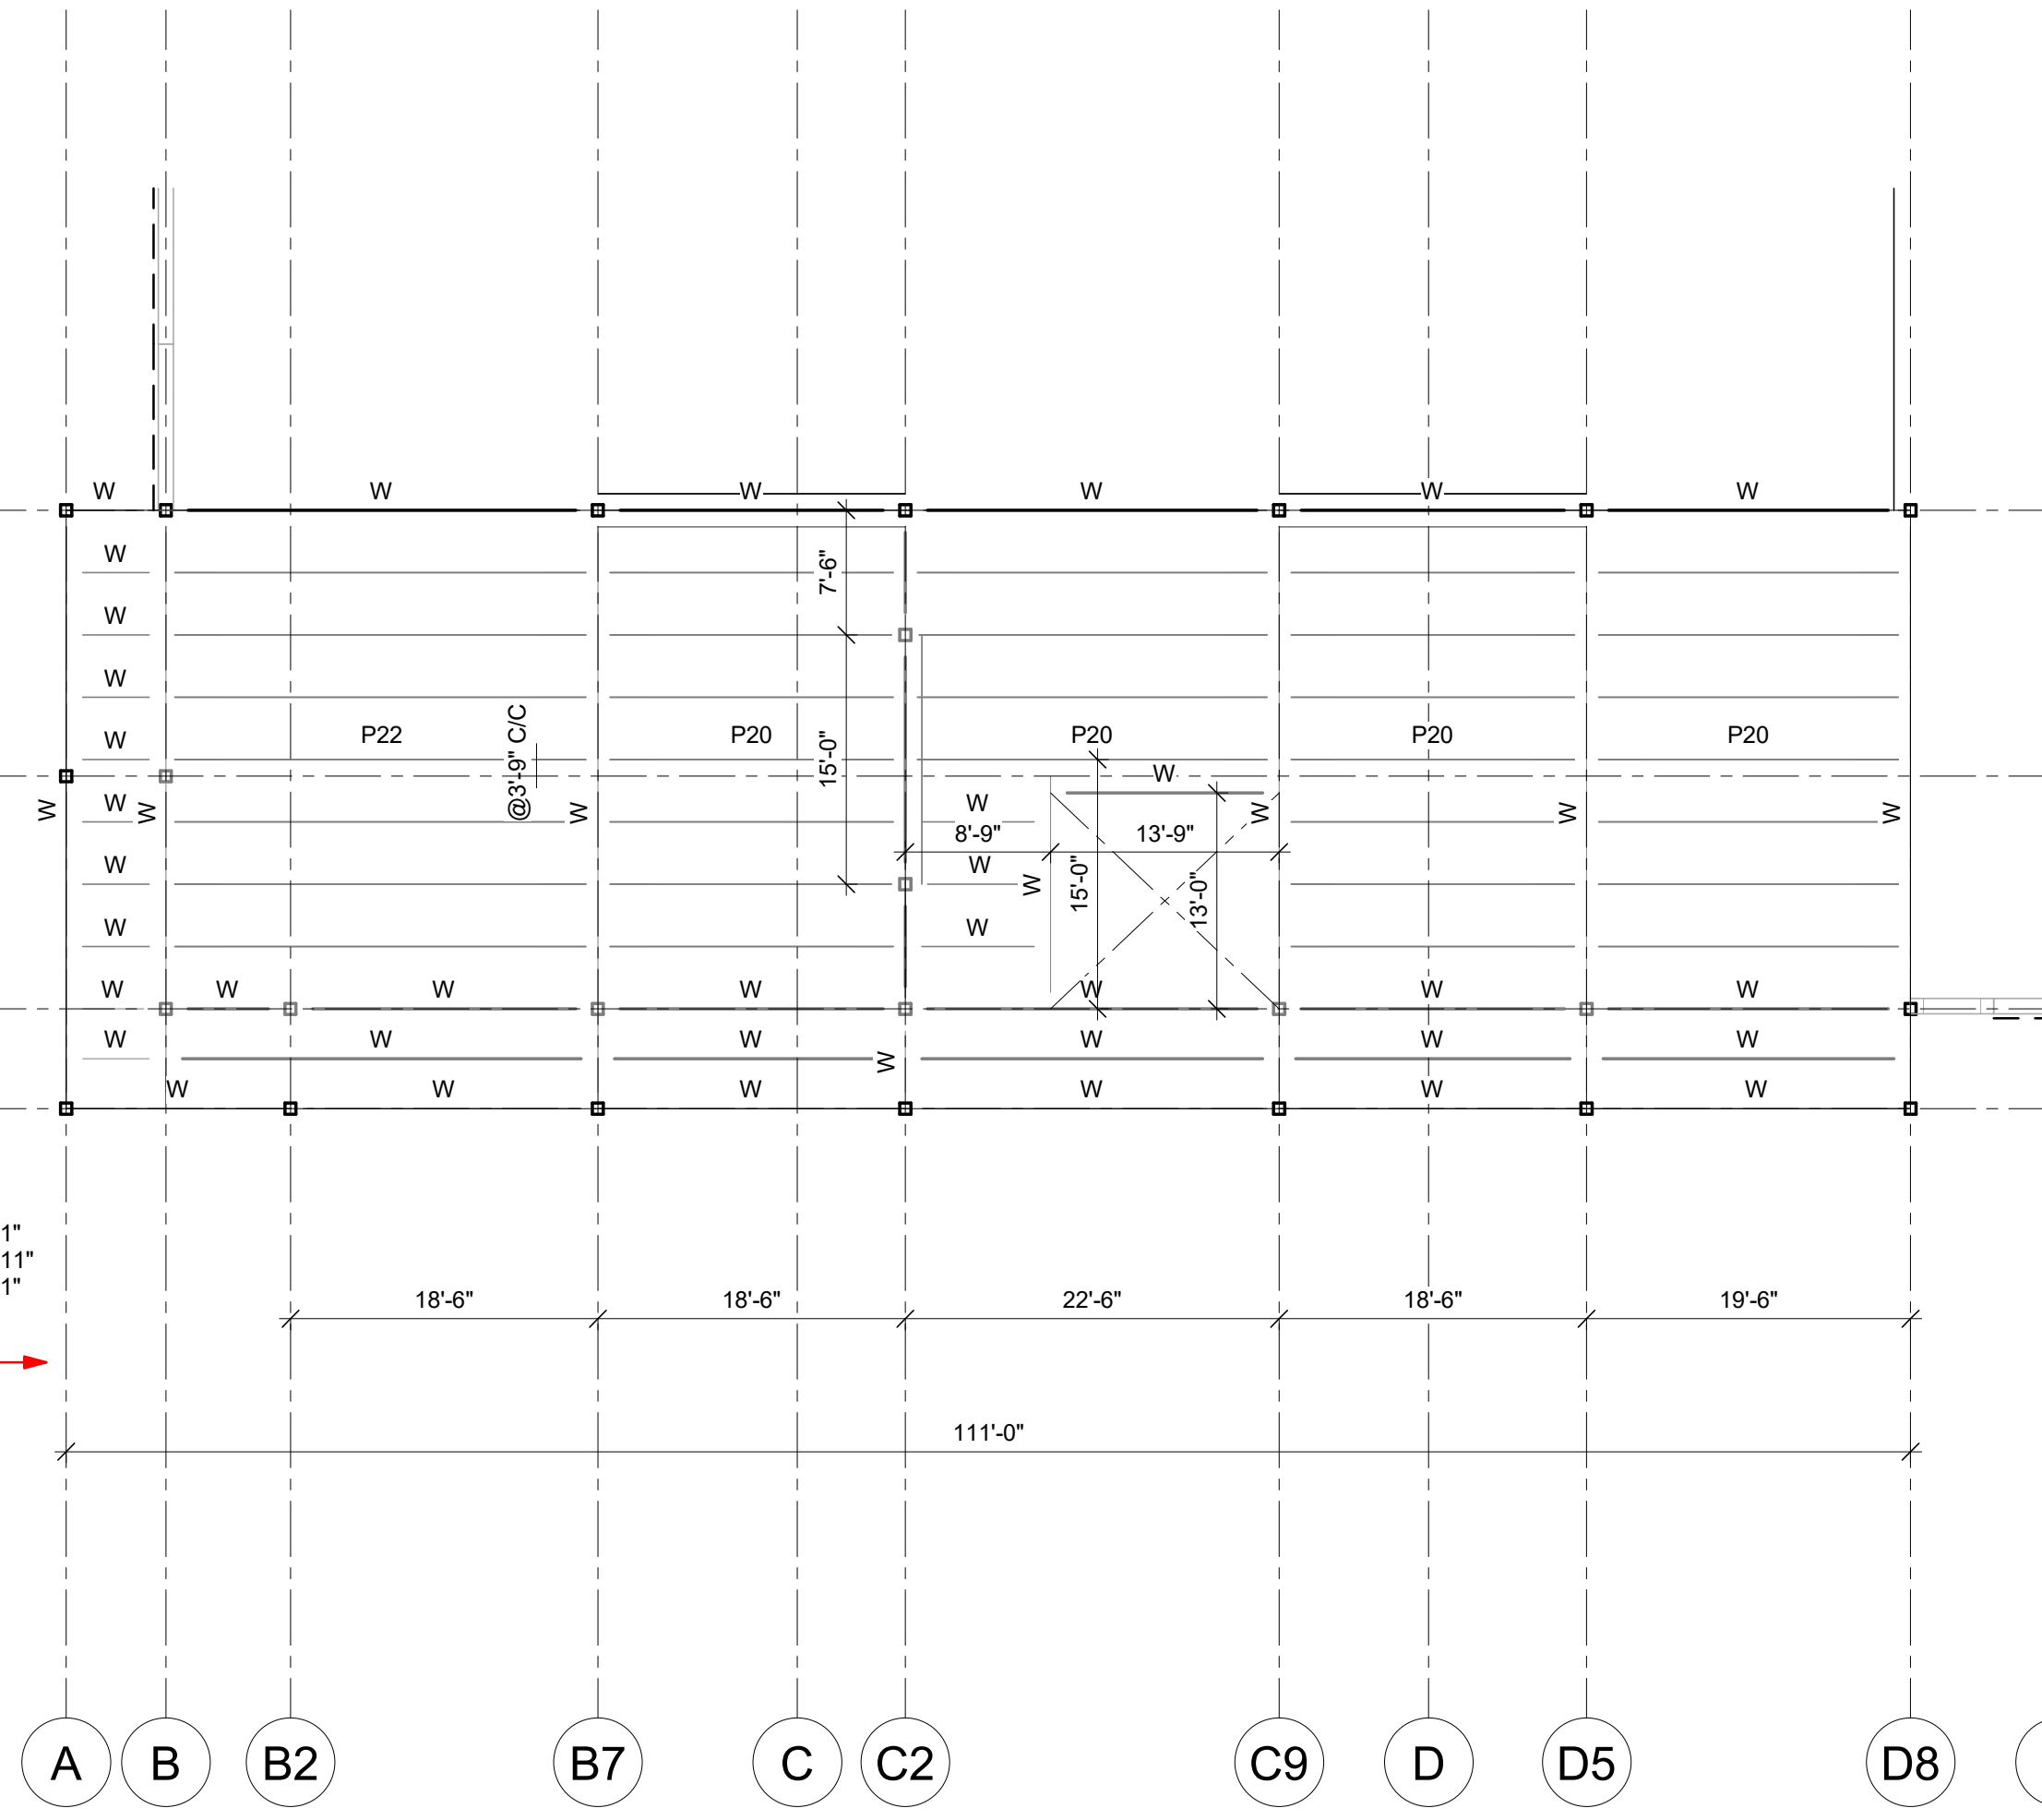

PLAN DE MEZZANINE
3/32" = 1'-0"

DIAGRAMME DE SOULEVEMENT BRUT (NON PONDERE)

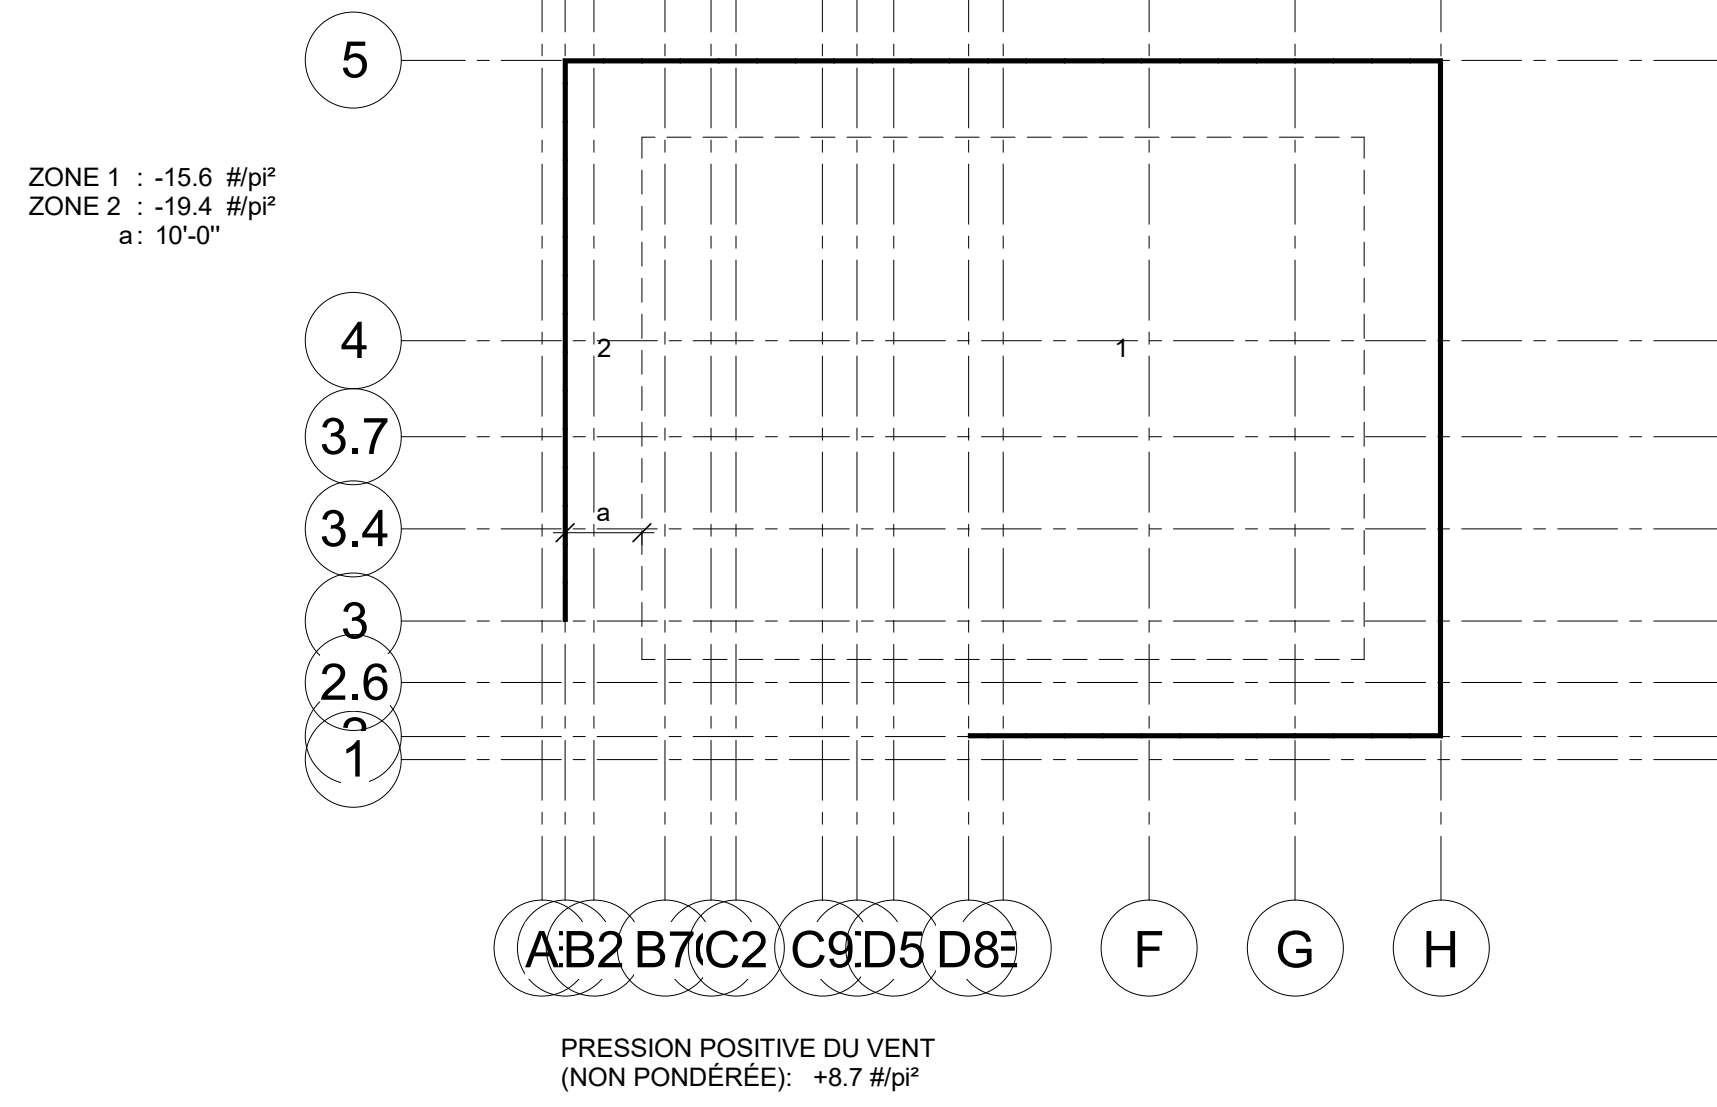

NOTE POUR LE CONTRACTEUR/ÉRECTEUR:
IL EST STRICTEMENT DÉFENDU DE MODIFIER, COPIER, REPRODUIRE OU DE DISTRIBUER CES DESSINS OU QUELQUES REPRÉSENTATIONS DE CES DESSINS, PAR TOUTES SOURCES DE MÉDIA INCLUANT ÉLECTRONIQUEMENT, SANS L'APPROBATION ÉCRITE DE GROUPE CANAM INC.

TOIT
DESSUS DE PILASTRE DOP : 98'-0"
DESSUS DE PILASTRE : 99'-0"
DESSUS DE LA DALLE : 100'-0"
DESSUS DE LA FONDATION BUREAU : 100'-0"
DESSUS DE LA FONDATION TYP. : 102'-0"
HAUTEUR LIBRE : 21'-6"
DESSUS D'ACIER : 125'-4"
HAUTEUR DE PARAPET : 1'-2"
DESSUS DE PARAPET : 126'-8"

CHARGES
C.M. : 18 lbs/p²
Cdl : 5 lbs/p²
Sd : 58.5 lbs/p²
Sv : 12.53 lbs/p²
Cb x Cw : 0.82
C.V. au toit : 0 lbs/p²
It : 1.0
Charge de neige au toit : 60.4 lbs/p²
Vent q = 1/50 : 7.84 lbs/p²
Seisme (Sol de classe D assumé)

It : 1.0
S_u(0.2) : 0.482
S_u(0.5) : 0.476
S_u(1.0) : 0.294
S_u(2.0) : 0.143
S_u(5.0) : 0.0405
S_u(10.0) : 0.0128
PGA : 0.267
PGV : 0.325

• Code Applicable : Code National du Bâtiment du Canada
Code du bâtiment du Québec, dernières éditions adoptées
Code de Pratique Standard ICCA.

• Type de sol assumé : classe D

• NOTE:
1. Si toutefois la catégorie d'emplacement devient E ou F selon le rapport géotechnique, le concept structural préliminaire (localisation et géométrie des contreventements, etc.) devra être validé et coordonné par l'ingénieur de Canam.

PRÉLIMINAIRE

NE DOIT PAS SERVIR À LA
CONSTRUCTION

REVISER	DATE	DESCRIPTION	DESS	VER
DESSIN DE PROJET				
DESSIN				
DESSINÉ PAR	CONÇU PAR	INGÉNIEUR DU PROJET	ÉCHELLE	
Donald Piché			Comme indiqué	
VÉRIFIÉ PAR	INGÉNIEURS CONSEILS / ARCHITECTES	DATE (mm/aaaa)		
		27-01-2026		

CLIENT:

CANAM

11505, 1re Avenue, bureau 500, Saint-Georges Beauséjour
Québec, Canada, G3Y 7X3
Téléphone : (418) 228-8031
Sans frais : (877) 459-8049
www.canam.com

SCAUX PROFESSIONNEL

PROJET

St-Georges, Québec

TITRE
CROQUIS PRÉLIMINAIRE - PLAN DE
TOIT & MEZZANINE

NUMÉRO CONTRAT	NUMÉRO DESSIN	DIVISION	REVISION
P2026-014	EsMx401		