




1/24

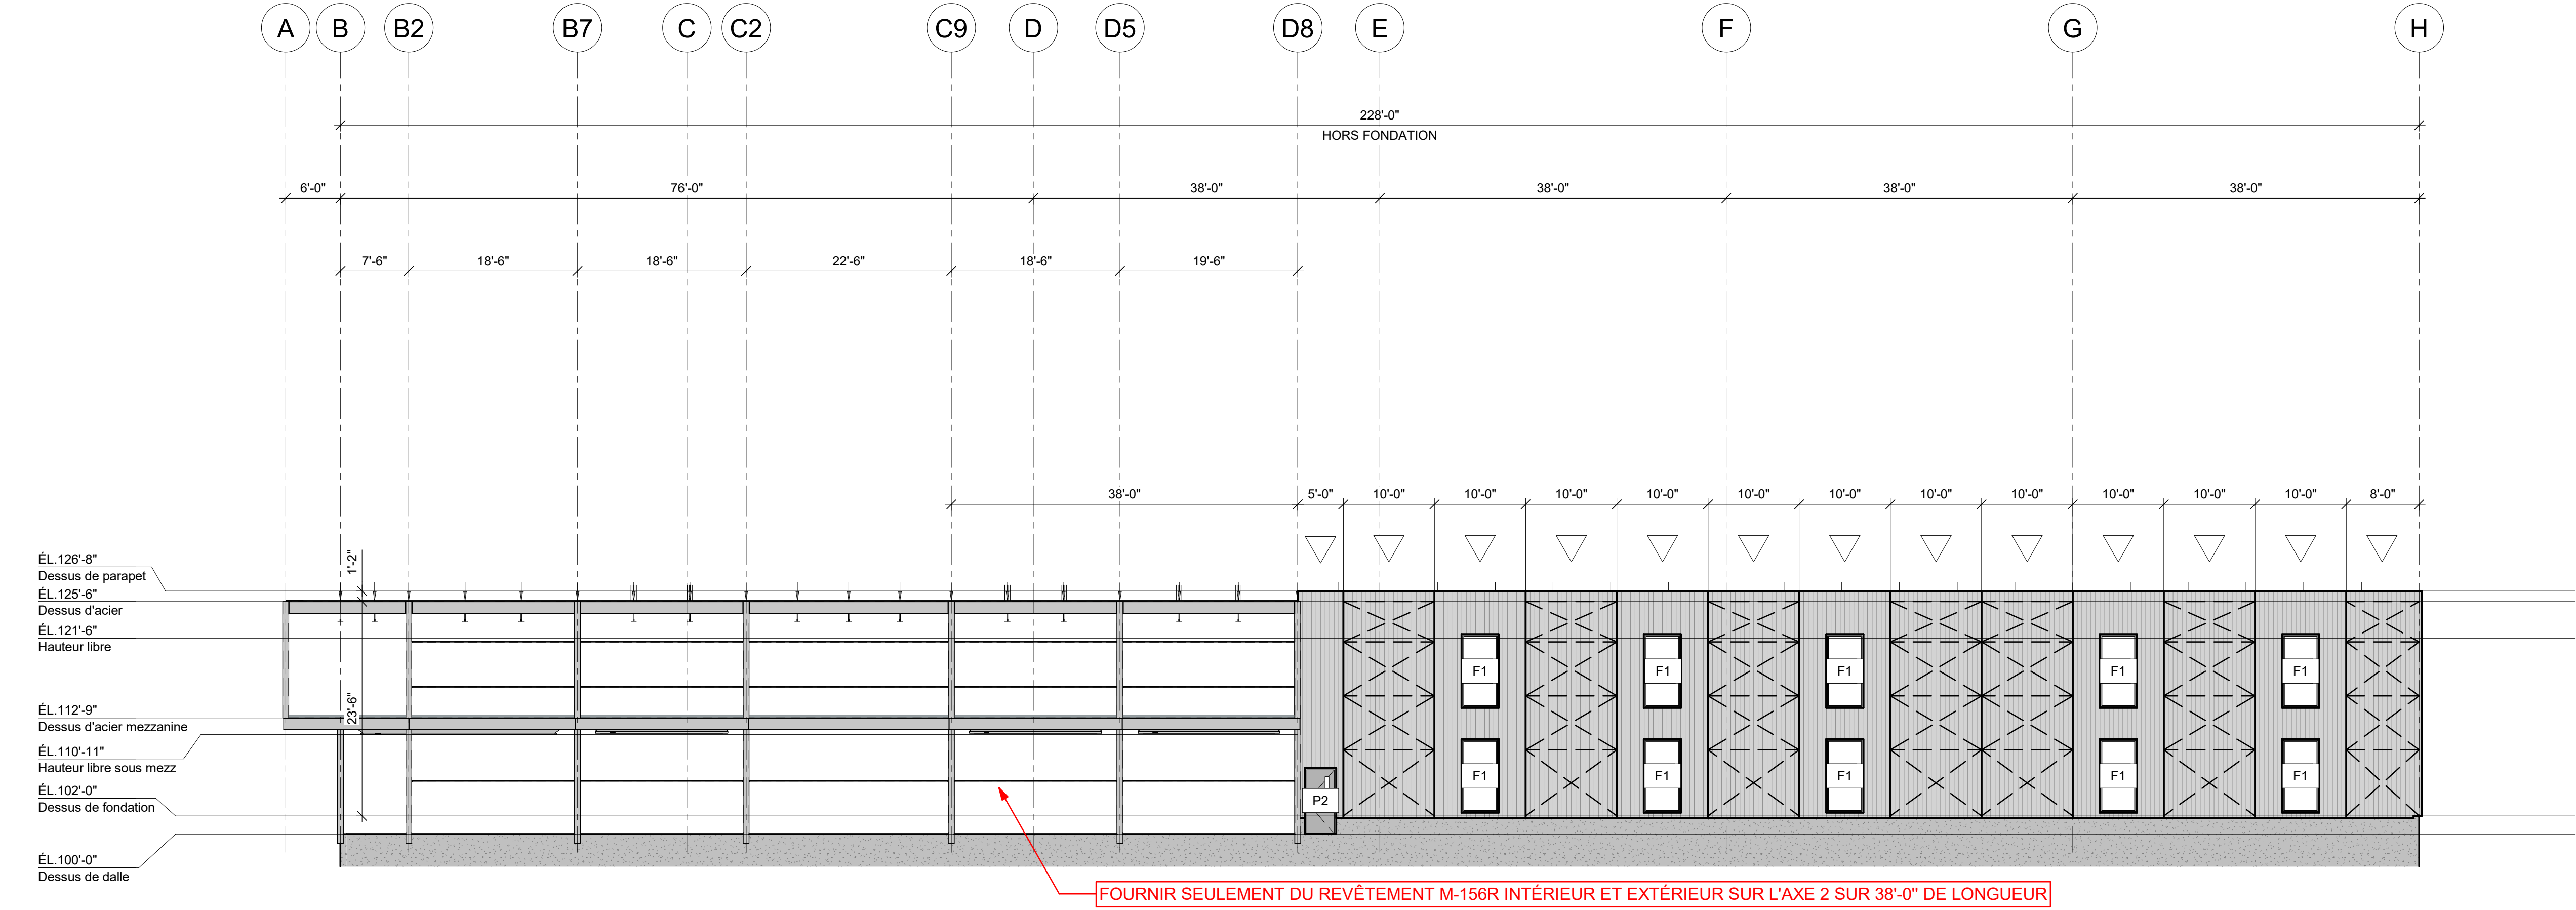


ÉLEVATION AXE 1 & 2 (SUD)  
3/32" = 1'-0"

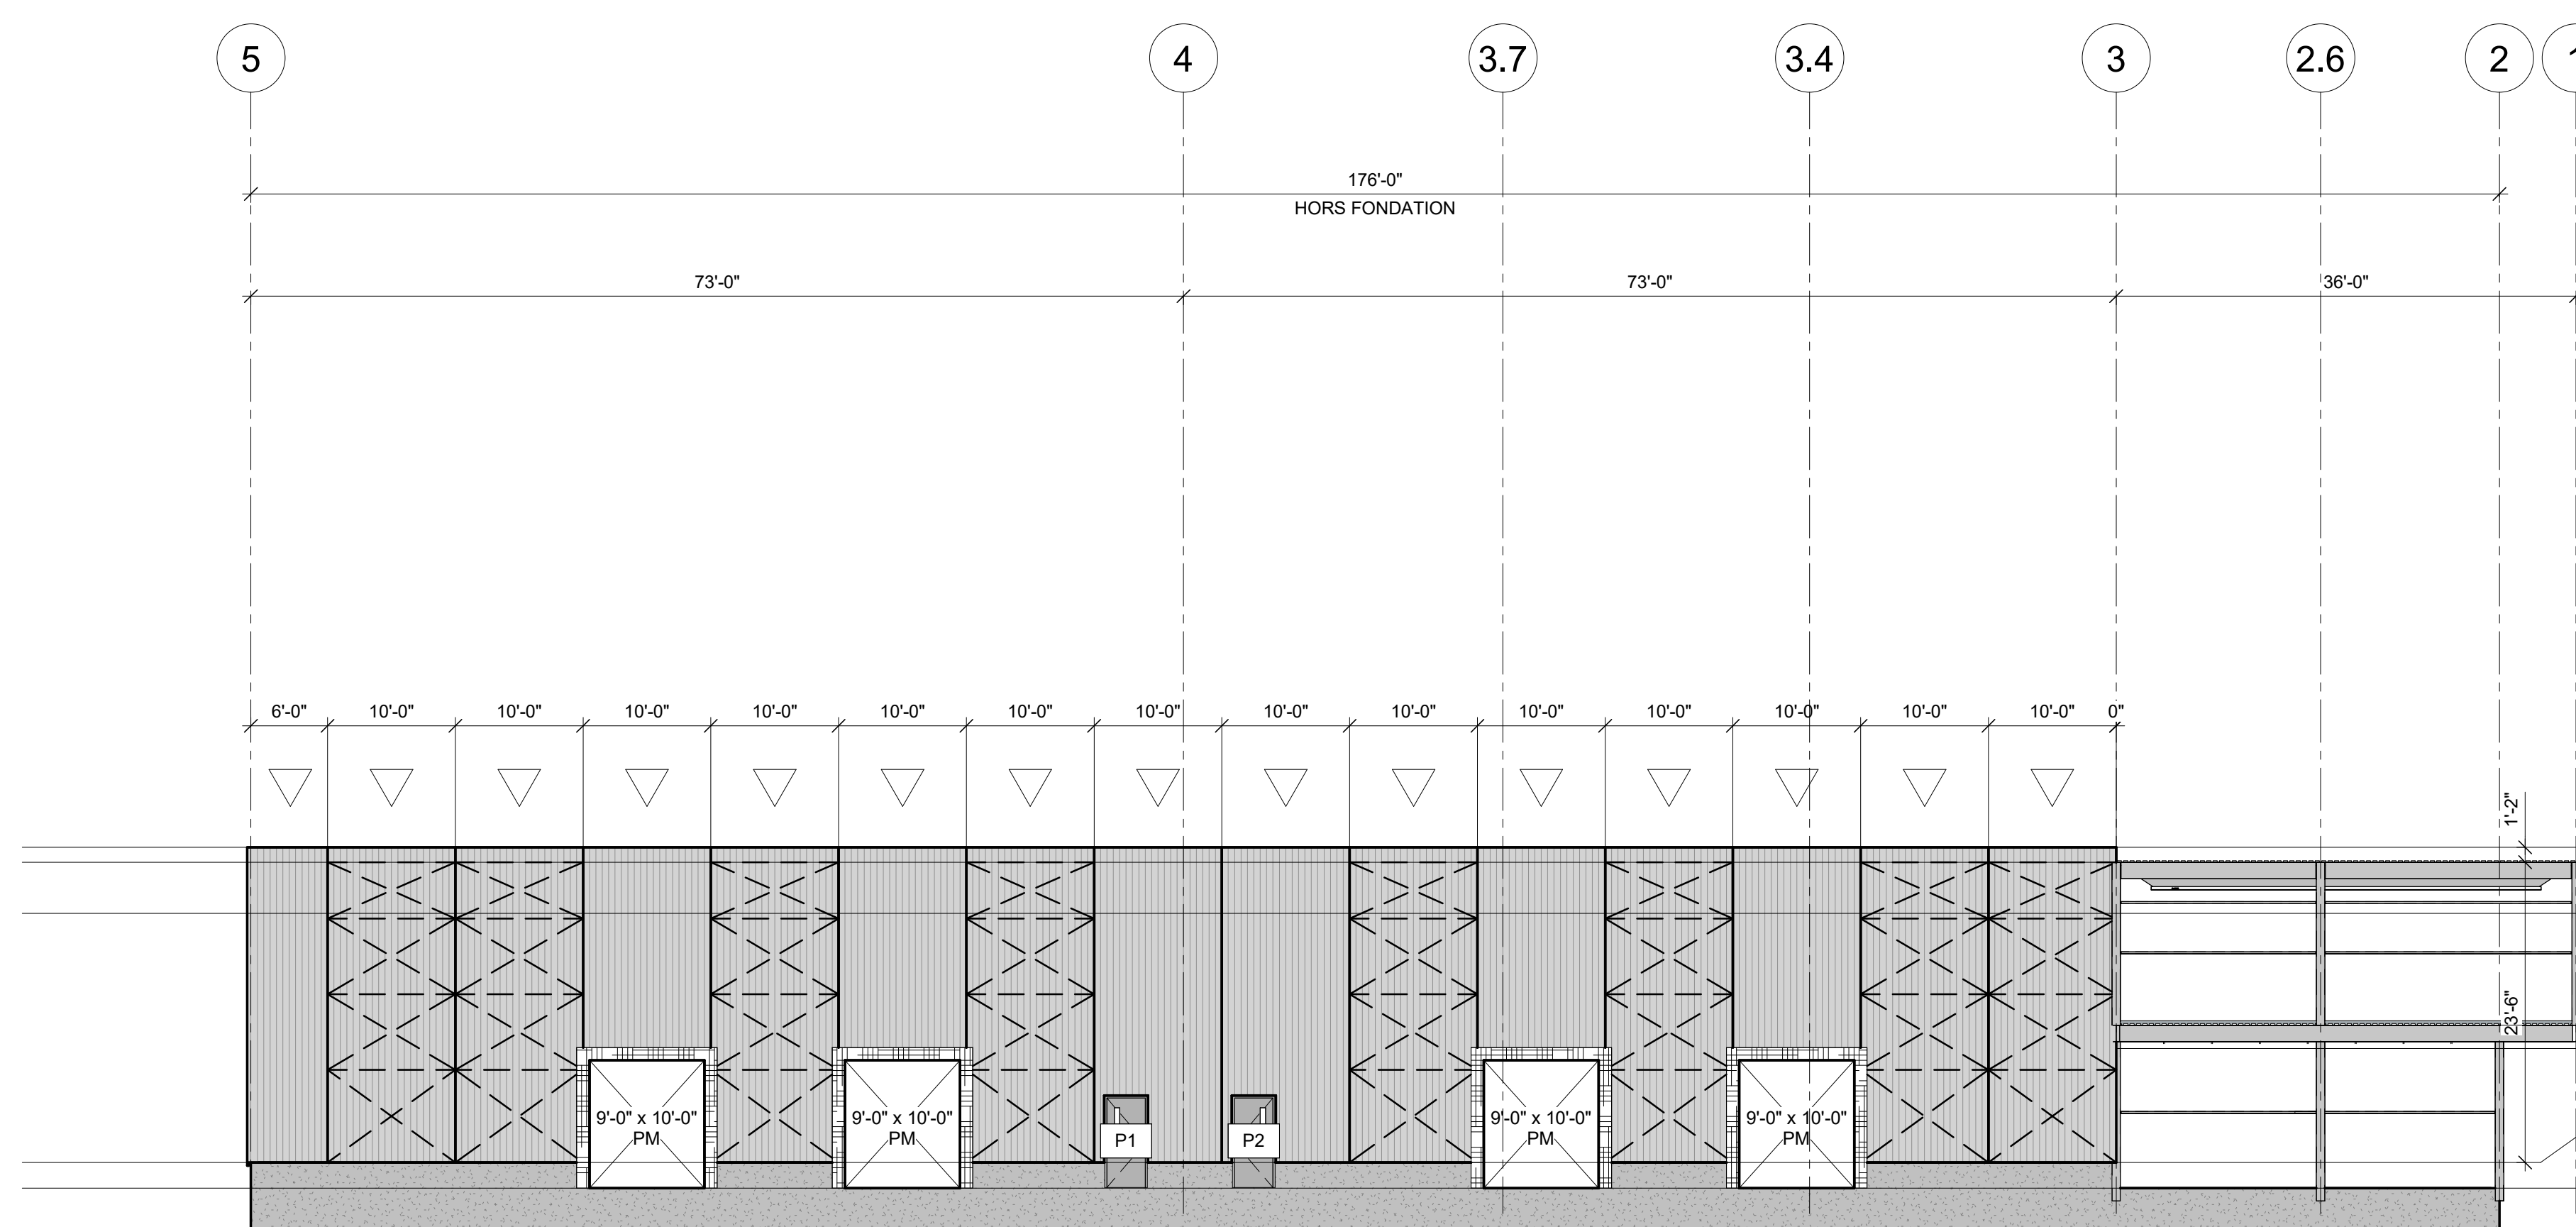


ÉLEVATION AXE A & B (OUEST)  
3/32" = 1'-0"

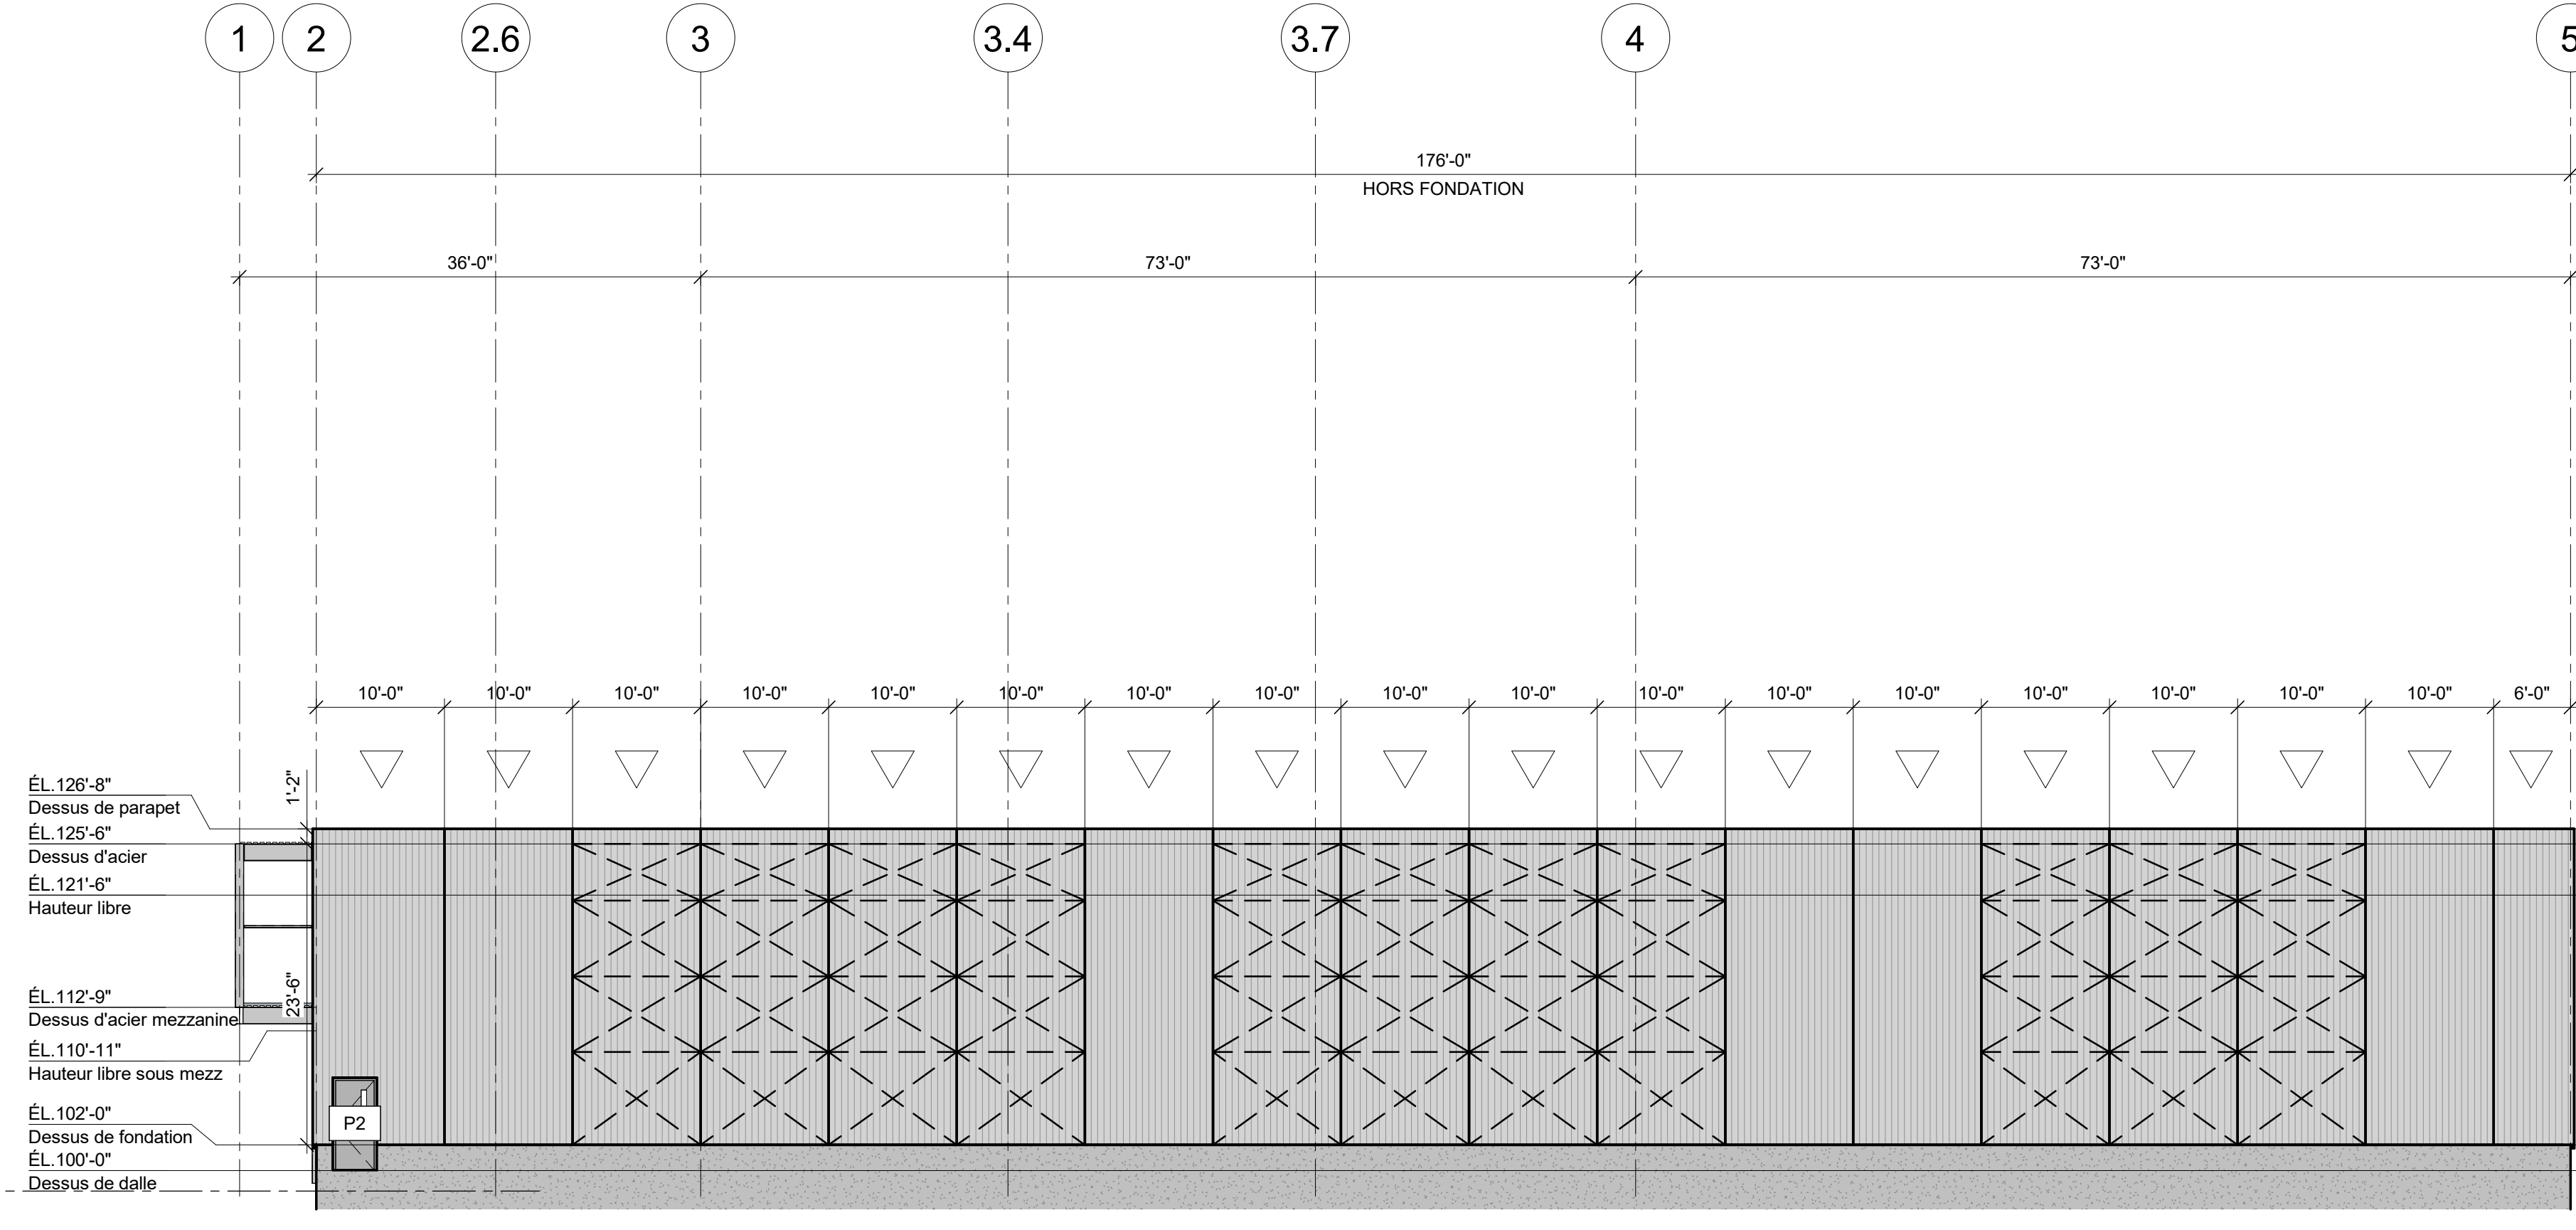


ÉLEVATION AXE D8 & H (EST)  
3/32" = 1'-0"

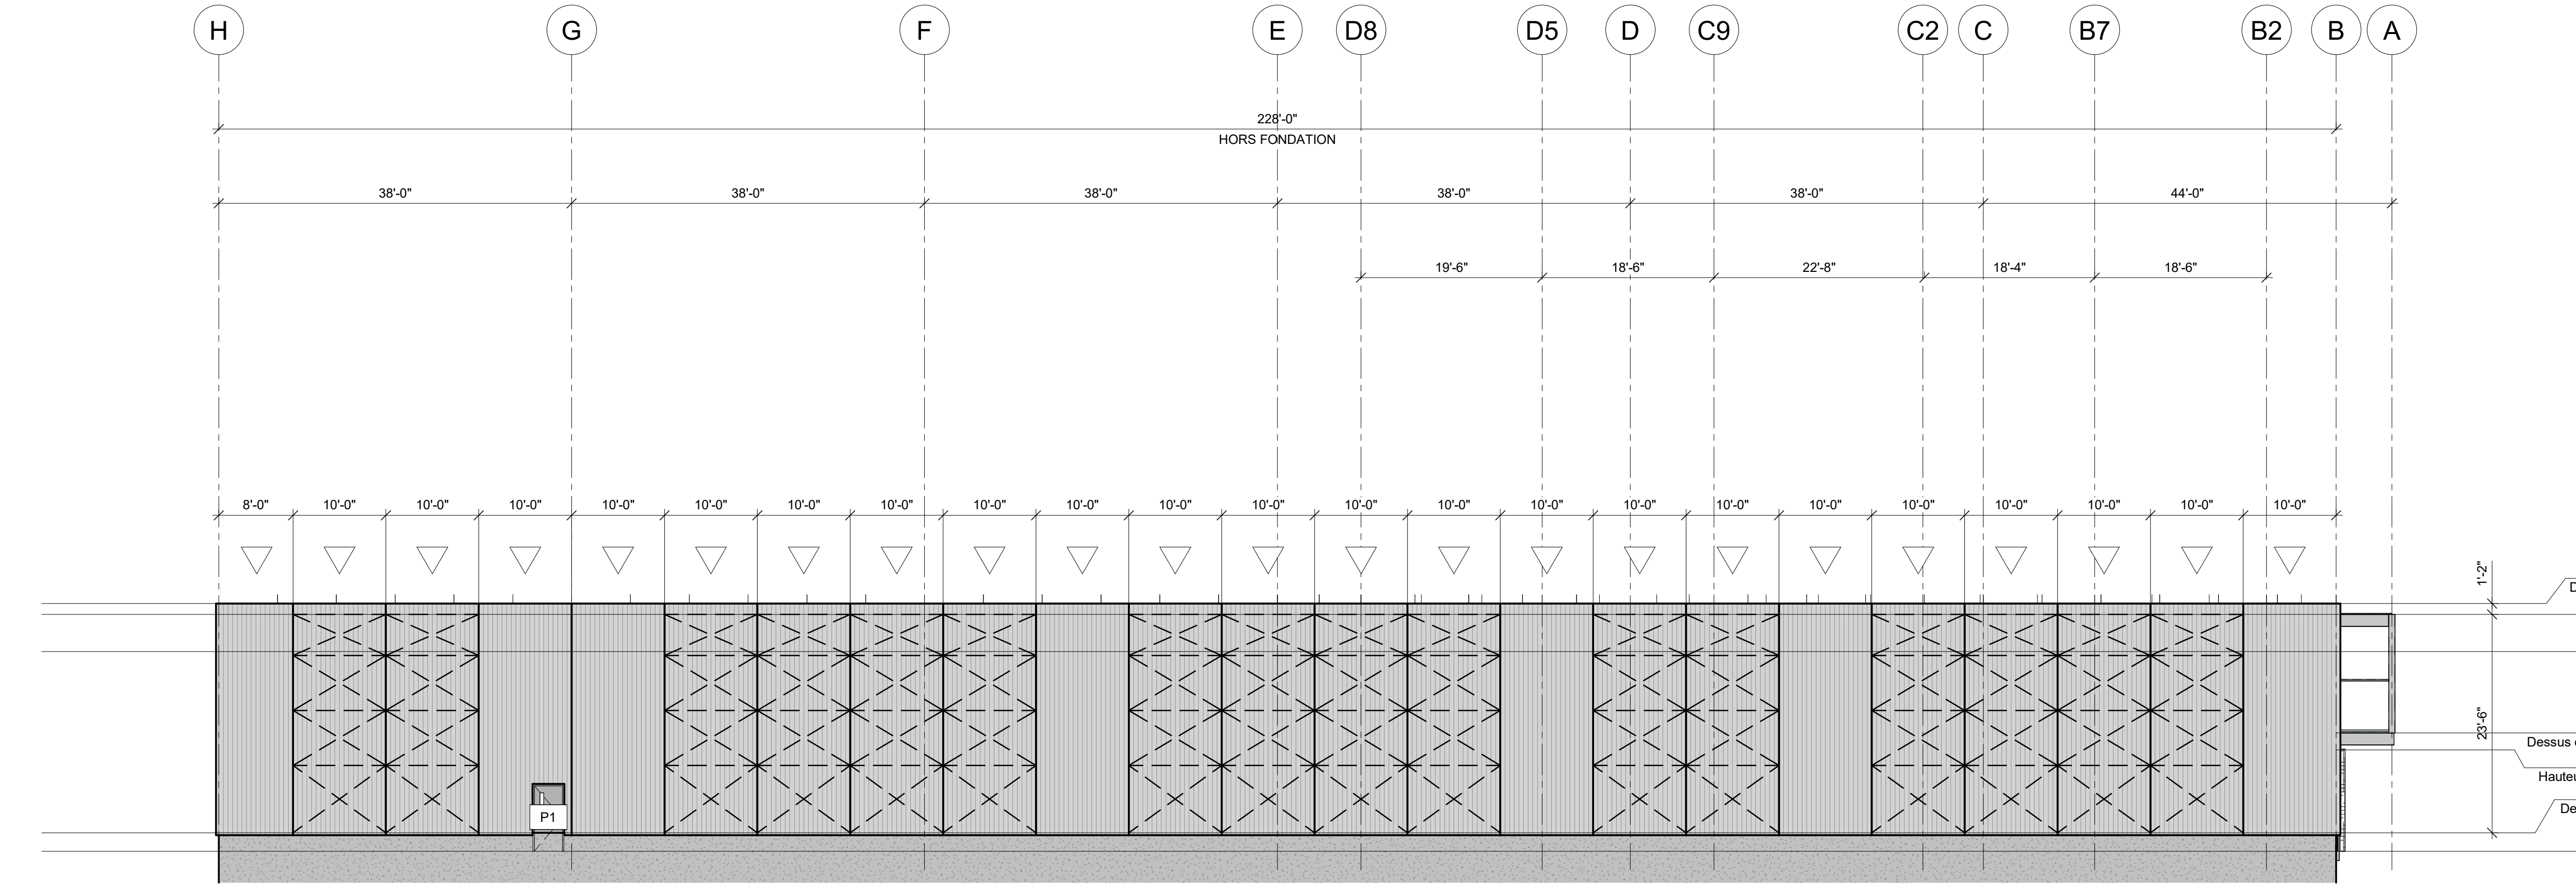

ÉLEVATION AXE 3 & 5 (NORD)  
3/32" = 1'-0"

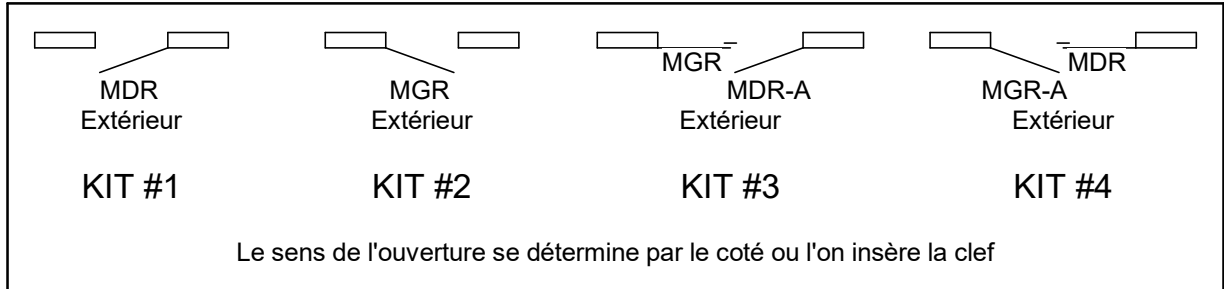

Quincaillerie standard du fournisseur:  
- Charnières : Stanley FBB 179 4.5" x 4"  
- Barre panique : Von Duprin 22 x 680 avec poignée extérieure 230L  
- Cylindre permanent : Schlage 20001C 638  
- Ferme-porte : LCN 1261 689  
- Coupe-froid de tête et des montants : Unique 1650  
- Coupe-froid du bas : Unique D54  
- Seuil : Voir la remarque dans la "Cédule de porte"

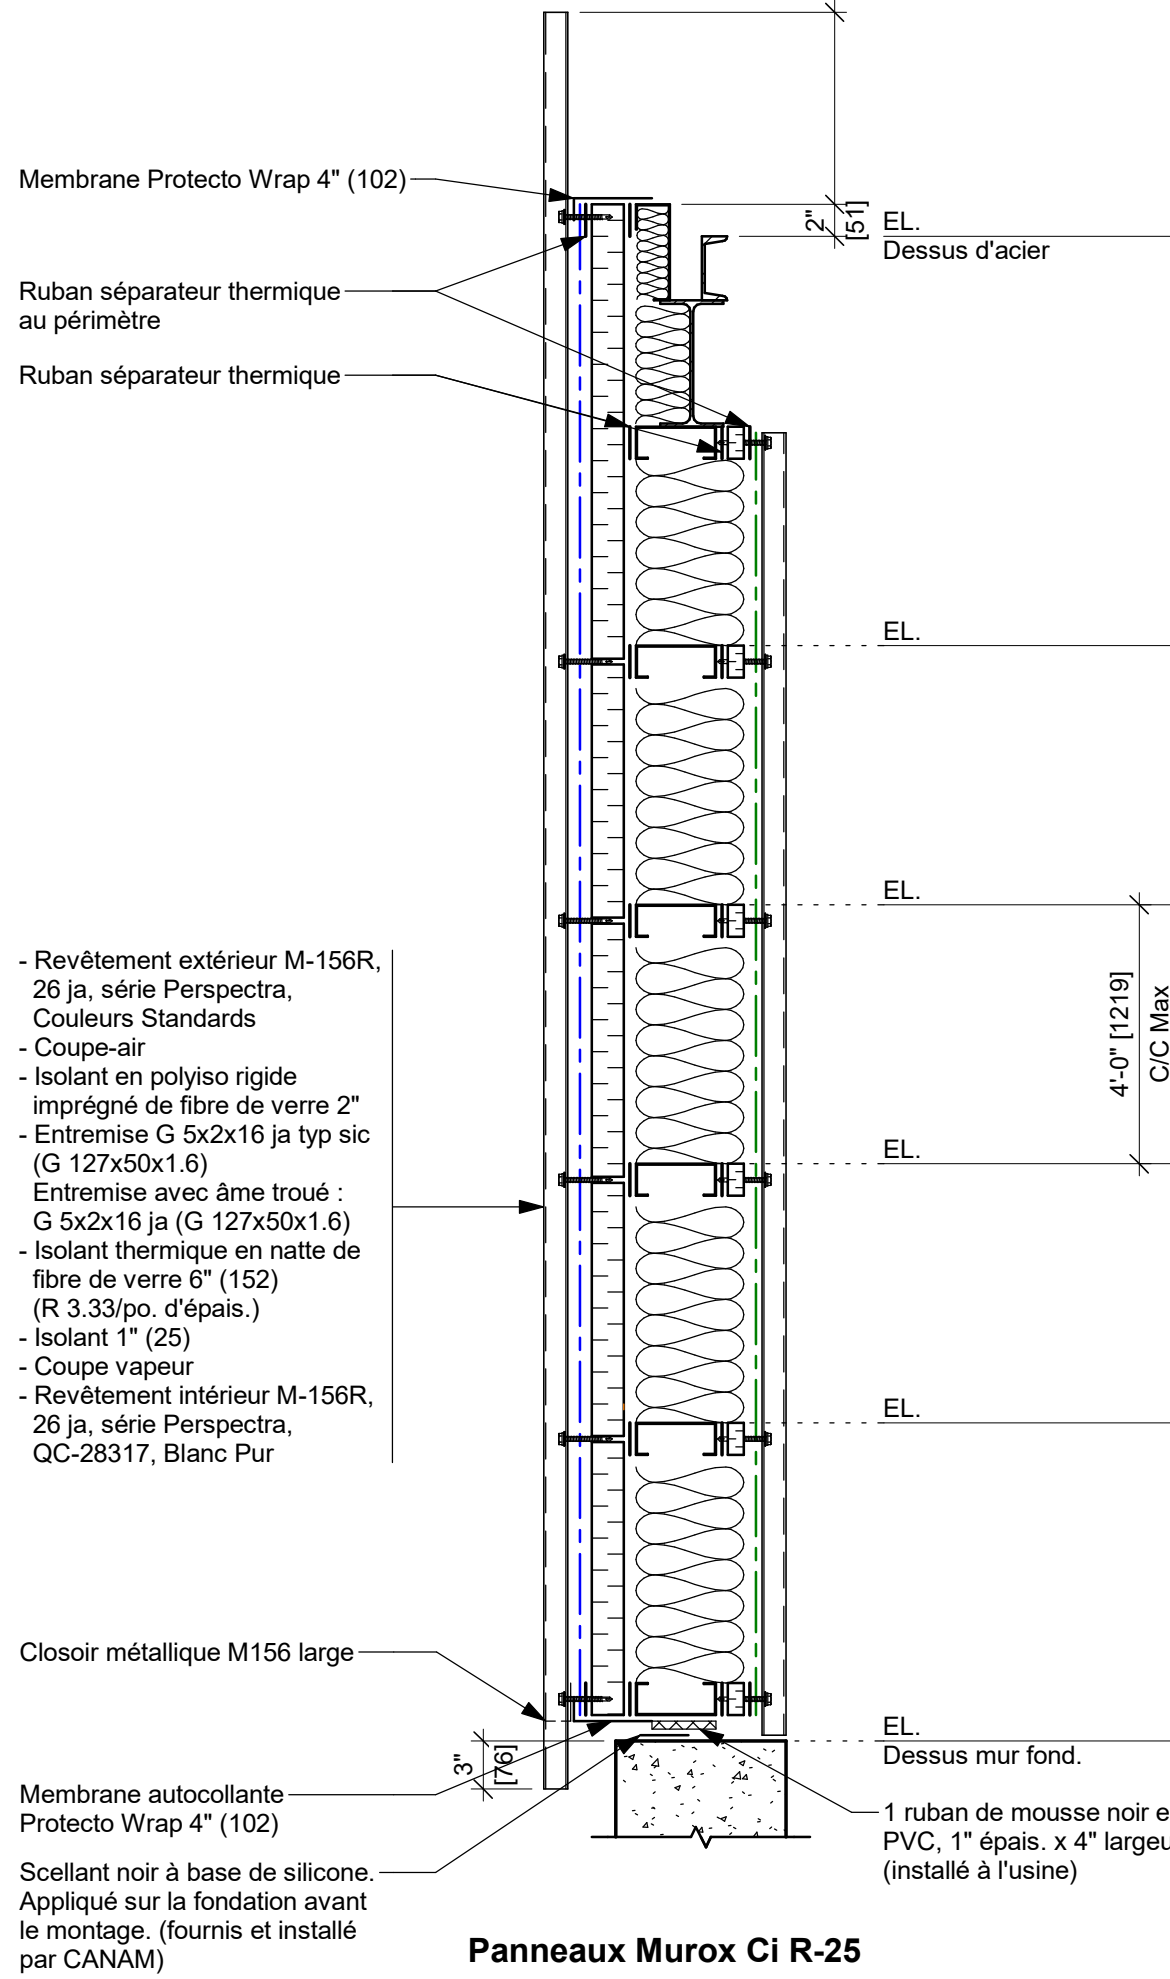

COUPE DE MUR - TYPE  
1" = 1'-0"

| CÉDULE DES FENÊTRES |     |              |                                                                                   |                                         |                                        |
|---------------------|-----|--------------|-----------------------------------------------------------------------------------|-----------------------------------------|----------------------------------------|
| Identifiant         | Qté | Installation | Description                                                                       | Dimensions ext. cadre largeur X hauteur | Couleur du cadre                       |
| F1                  | 10  |              | Fenêtre en aluminium fixe avec bris thermique et verre scellé + Low-E argon clair | 4'-0" x 8'-0"                           | Cadre d'Aluminium (Blanc ext. et int.) |
| Remarques           |     |              |                                                                                   |                                         |                                        |

| CÉDULE DES OUVERTURES |      |     |              |
|-----------------------|------|-----|--------------|
| Total                 | Type | Tag | Commentaires |

| CÉDULE DES PORTES |     |              |                 |               |           |         |         |                                          |                          |                   |                                      |                                      |                                    |
|-------------------|-----|--------------|-----------------|---------------|-----------|---------|---------|------------------------------------------|--------------------------|-------------------|--------------------------------------|--------------------------------------|------------------------------------|
| Porte 18 ja.      |     |              |                 | Vitrage       |           |         |         | Quincaillerie                            |                          |                   |                                      |                                      |                                    |
| Identifiant       | Qté | Installation | Isolation (R12) | Dimensions    | Sens ouv. | Largeur | Hauteur | Cadre d'acier 16 ja. avec bris thermique | (3) Pentures @ tige fixe | Poignée seulement | Barre panique sans poignée ext. 22EO | Barre panique avec poignée ext. 230L | Verrou en surface (Porte inactive) |
| P1                | 2   |              |                 | 3'-0" x 7'-0" |           | 5"      | 1'-8"   |                                          |                          |                   |                                      |                                      |                                    |
| P2                | 3   |              |                 | 3'-0" x 7'-0" |           | 9"      | 1'-0"   |                                          |                          |                   |                                      |                                      |                                    |
| Remarques         |     |              |                 |               |           |         |         |                                          |                          |                   |                                      |                                      |                                    |

| CÉDULE DES P.M. ET DES OUVERTURES |                |     |              |
|-----------------------------------|----------------|-----|--------------|
| Total                             | Type           | Tag | Commentaires |
| 4                                 | 9'-0" x 10'-0" | PM  |              |
| Total général: 4                  |                |     |              |

Initiales

PRÉLIMINAIRE

NE DOIT PAS SERVIR À LA CONSTRUCTION

| REVISION         | DATE                              | DESCRIPTION         | DESS               | VER |
|------------------|-----------------------------------|---------------------|--------------------|-----|
| GERANT DE PROJET |                                   |                     |                    |     |
|                  |                                   | -                   |                    |     |
|                  |                                   | -                   |                    |     |
| DESSIN           |                                   |                     |                    |     |
| DESSINÉ PAR      | CONÇU PAR                         | INGÉNIEUR DU PROJET | ECHELLE:           |     |
| INITIALE         |                                   |                     | Comme indiqué      |     |
| VÉRIFIÉ PAR      | INGÉNIEURS CONSEILS / ARCHITECTES |                     | DATE (gg/mm/aaaa): |     |
|                  |                                   |                     | 27-01-2026         |     |



11505, 1re Avenue, bureau 500, Saint-Georges Beauce  
Québec, Canada, G5Y 7G5  
Téléphone : (418) 228-8031  
Sans frais : (877) 459-8049  
www.canam.com

SCAUX PROFESSIONNEL

PROJET

St-Georges, Québec

CROQUIS PRÉLIMINAIRE - ÉLEVATIONS

| NUMÉRO CONTRAT | NUMÉRO DESSIN | DIVISION | REVISION |
|----------------|---------------|----------|----------|
| P2026-014      | EsMx501       |          |          |