




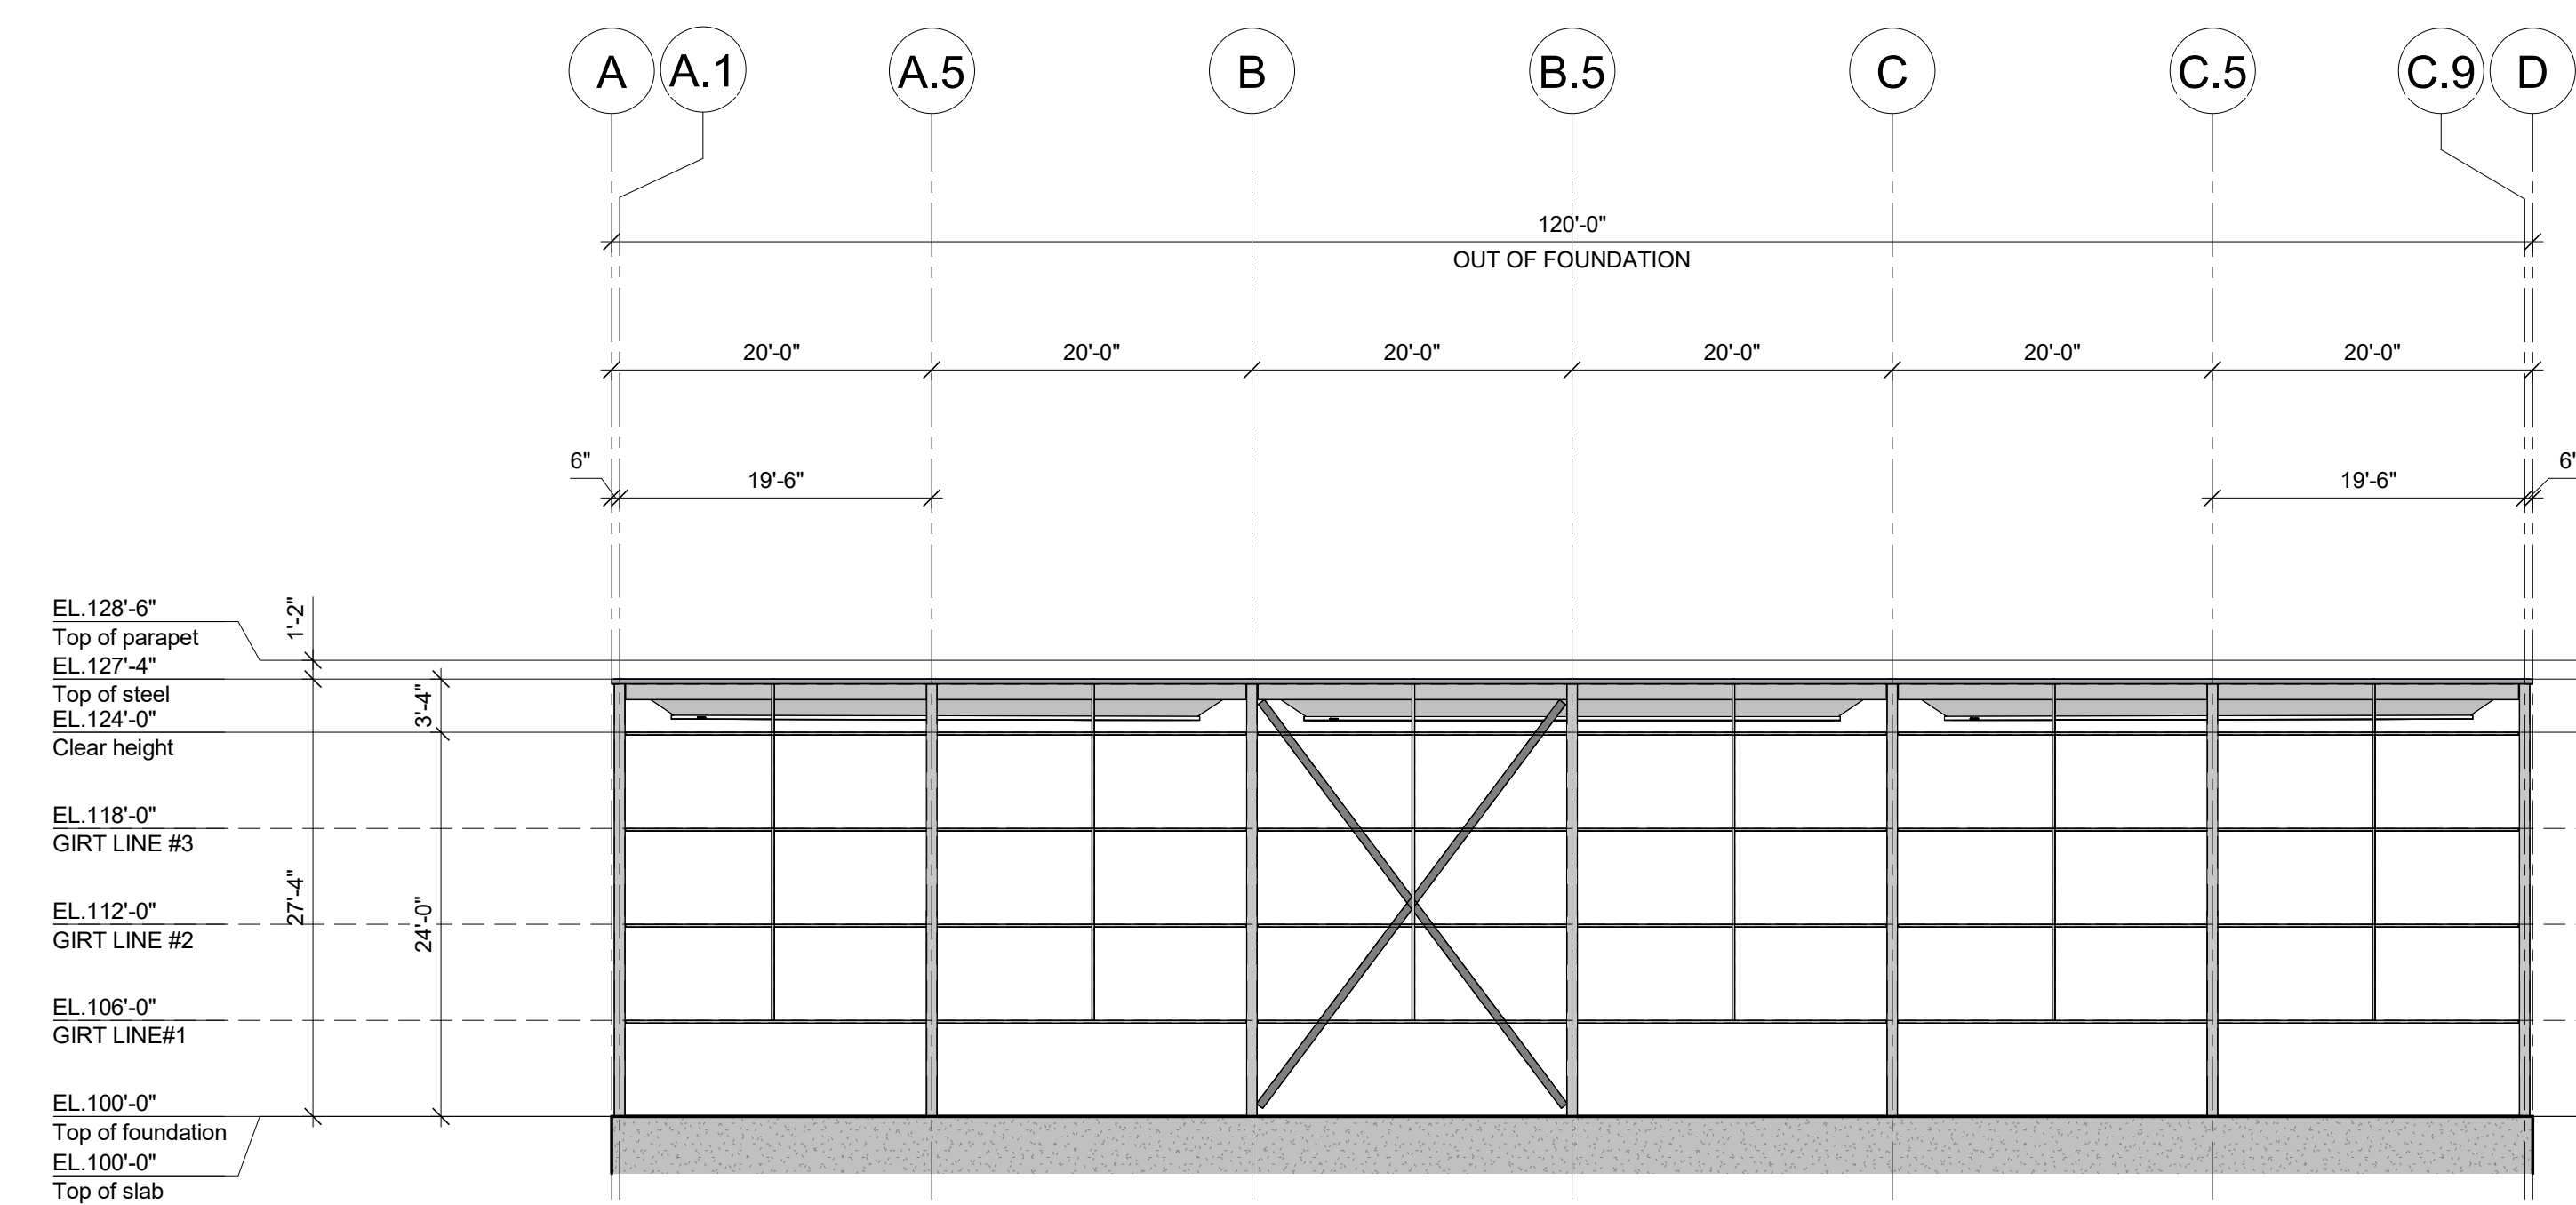


ELEVATION LINE 1 (SOUTH)
3/32" = 1'-0"

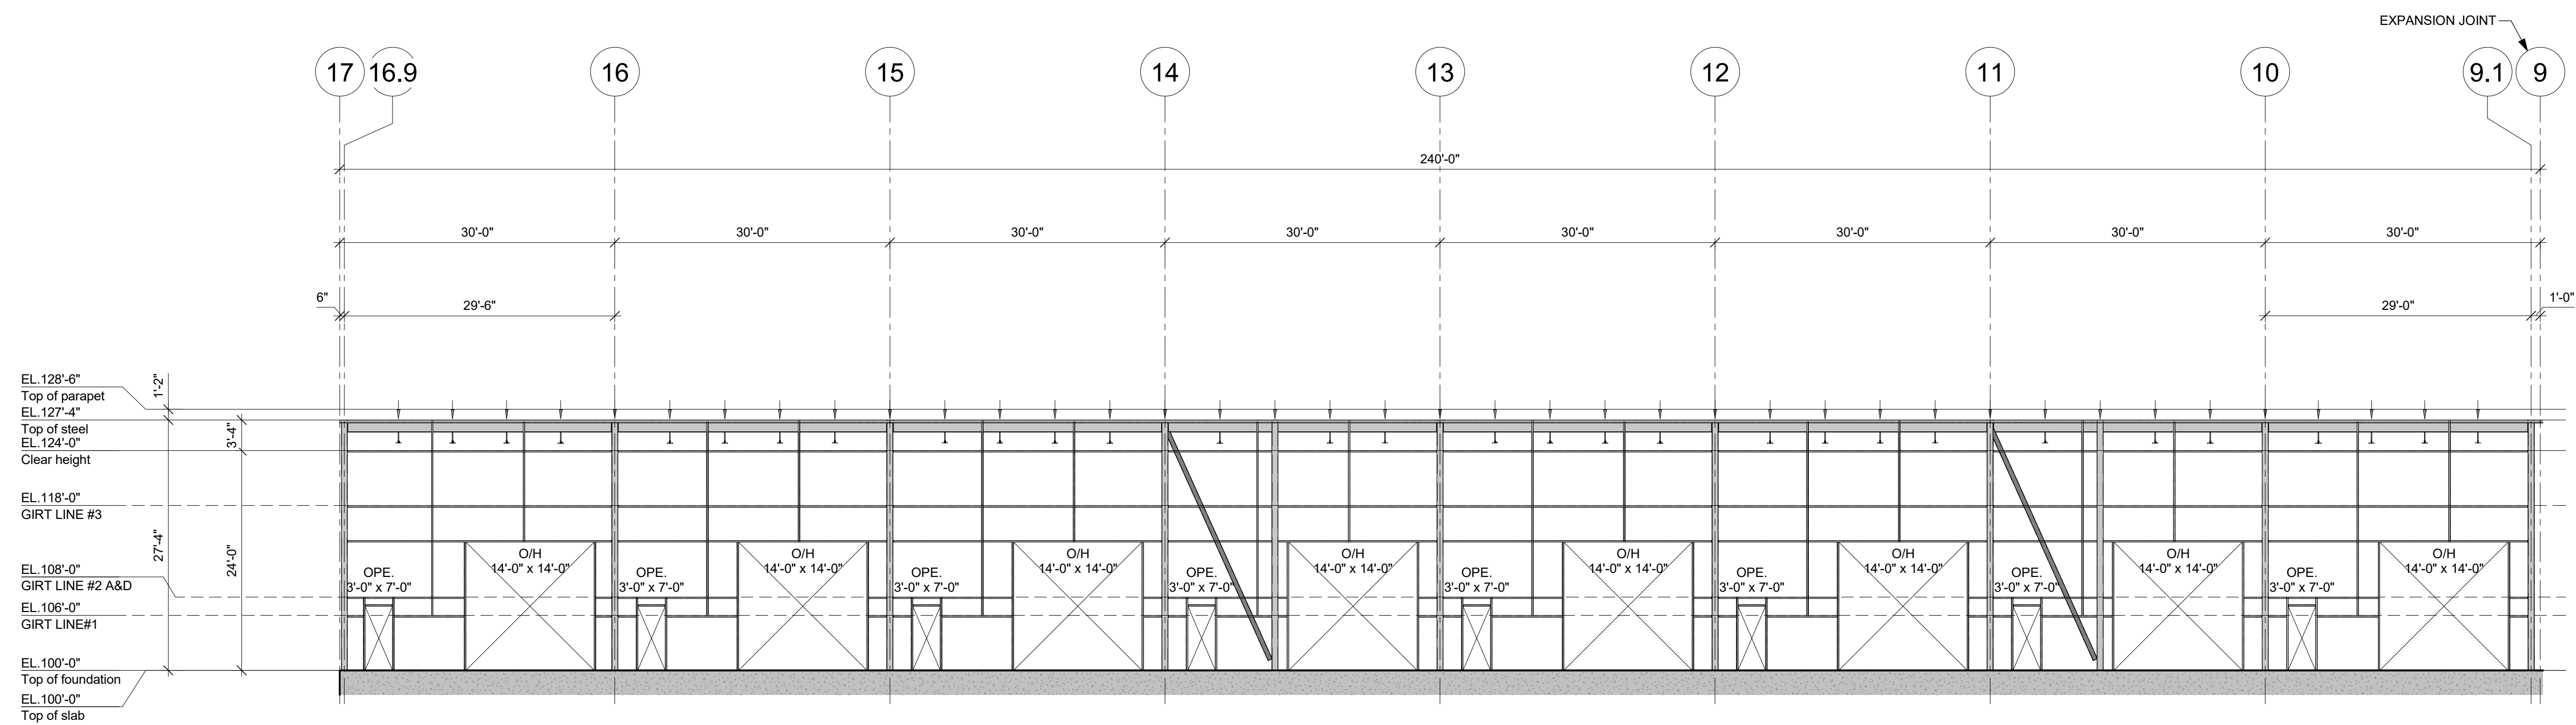

ELEVATION LINE A (WEST) - LINE 17 @ 9
3/32" = 1'-0"

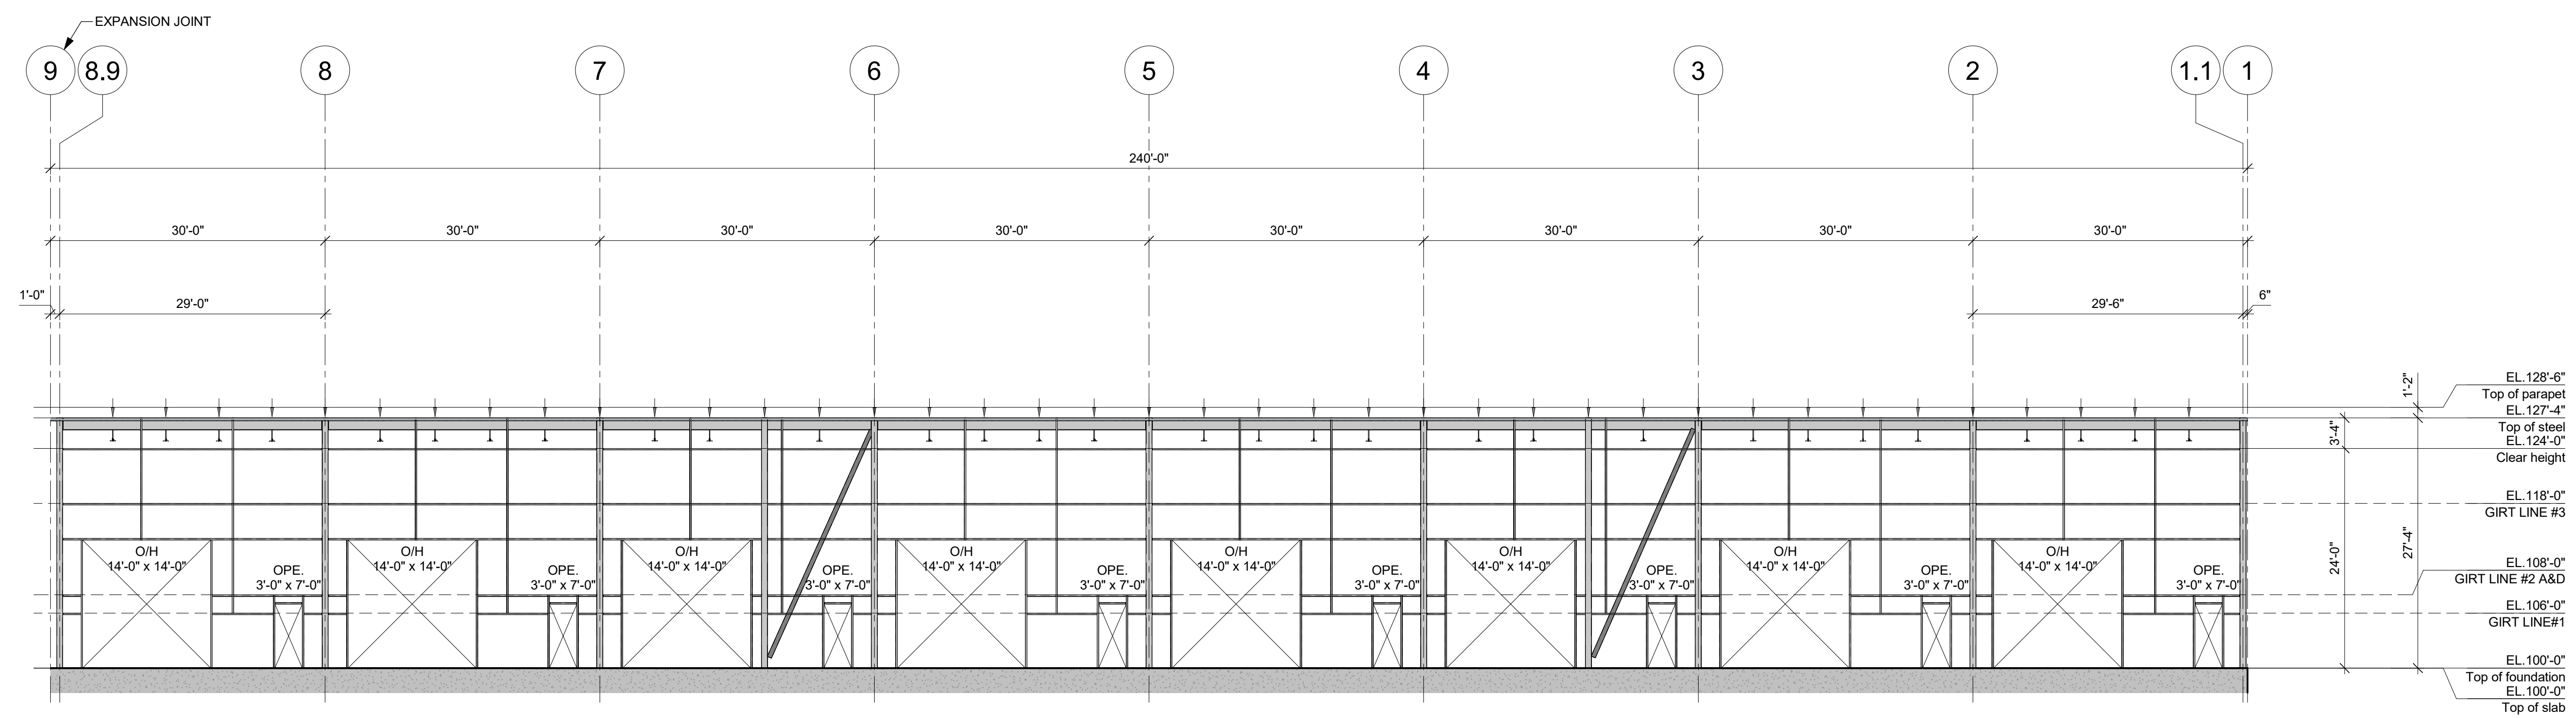

ELEVATION LINE A (WEST) - LINE 9 @ 1
3/32" = 1'-0"

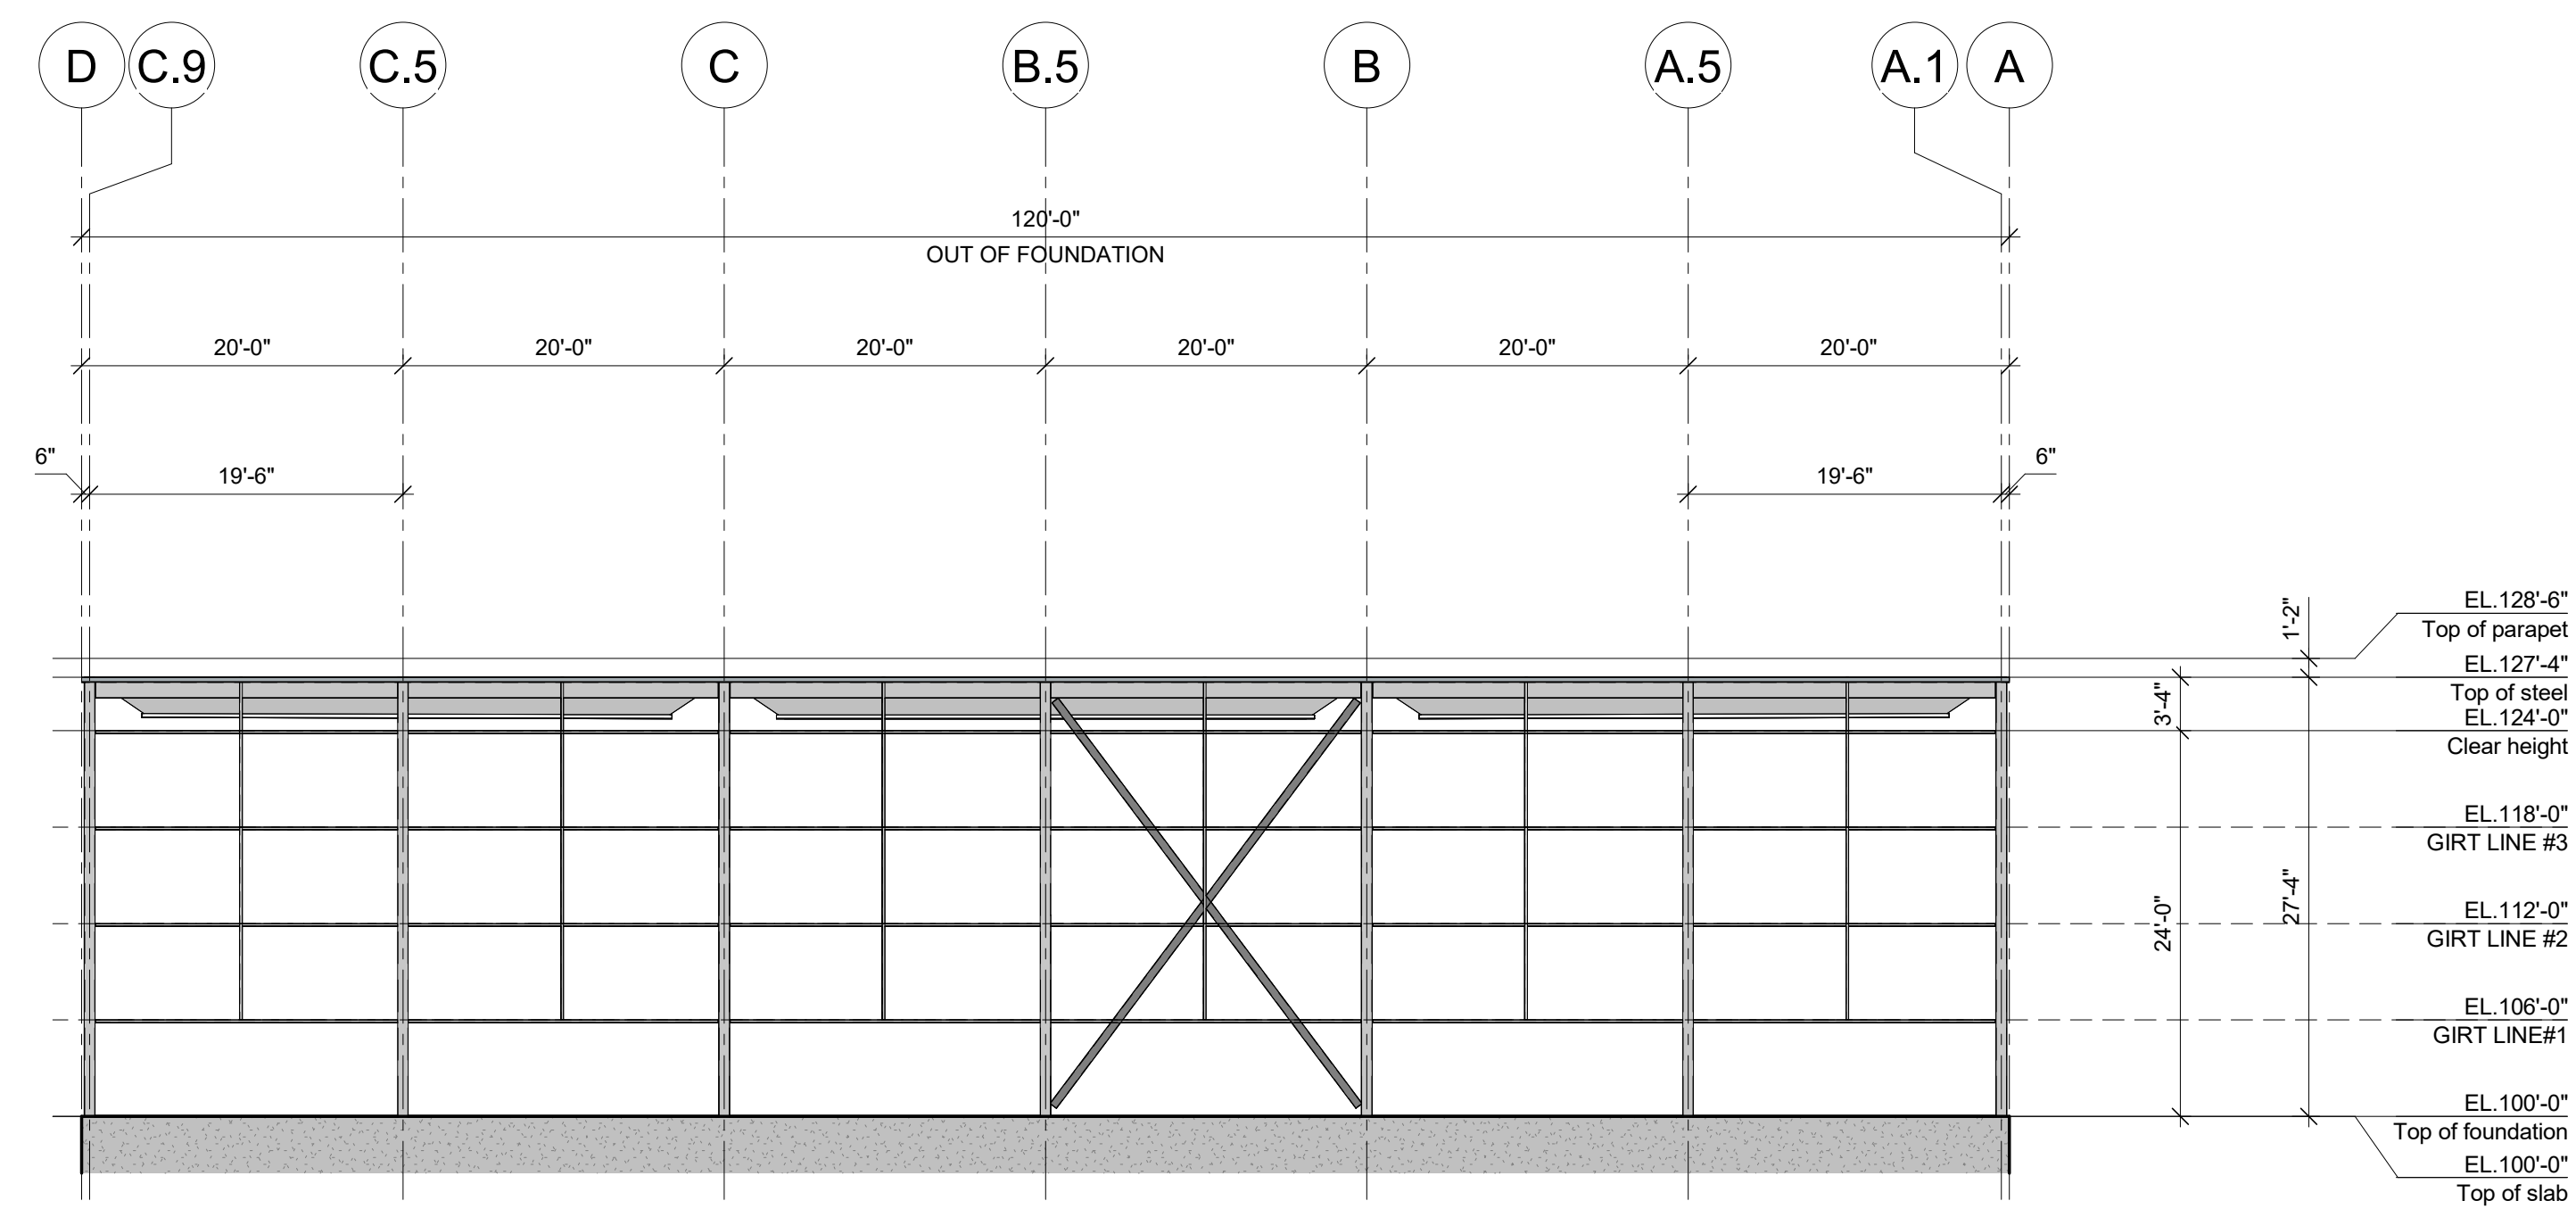

ELEVATION LINE 17 (NORTH)
3/32" = 1'-0"