



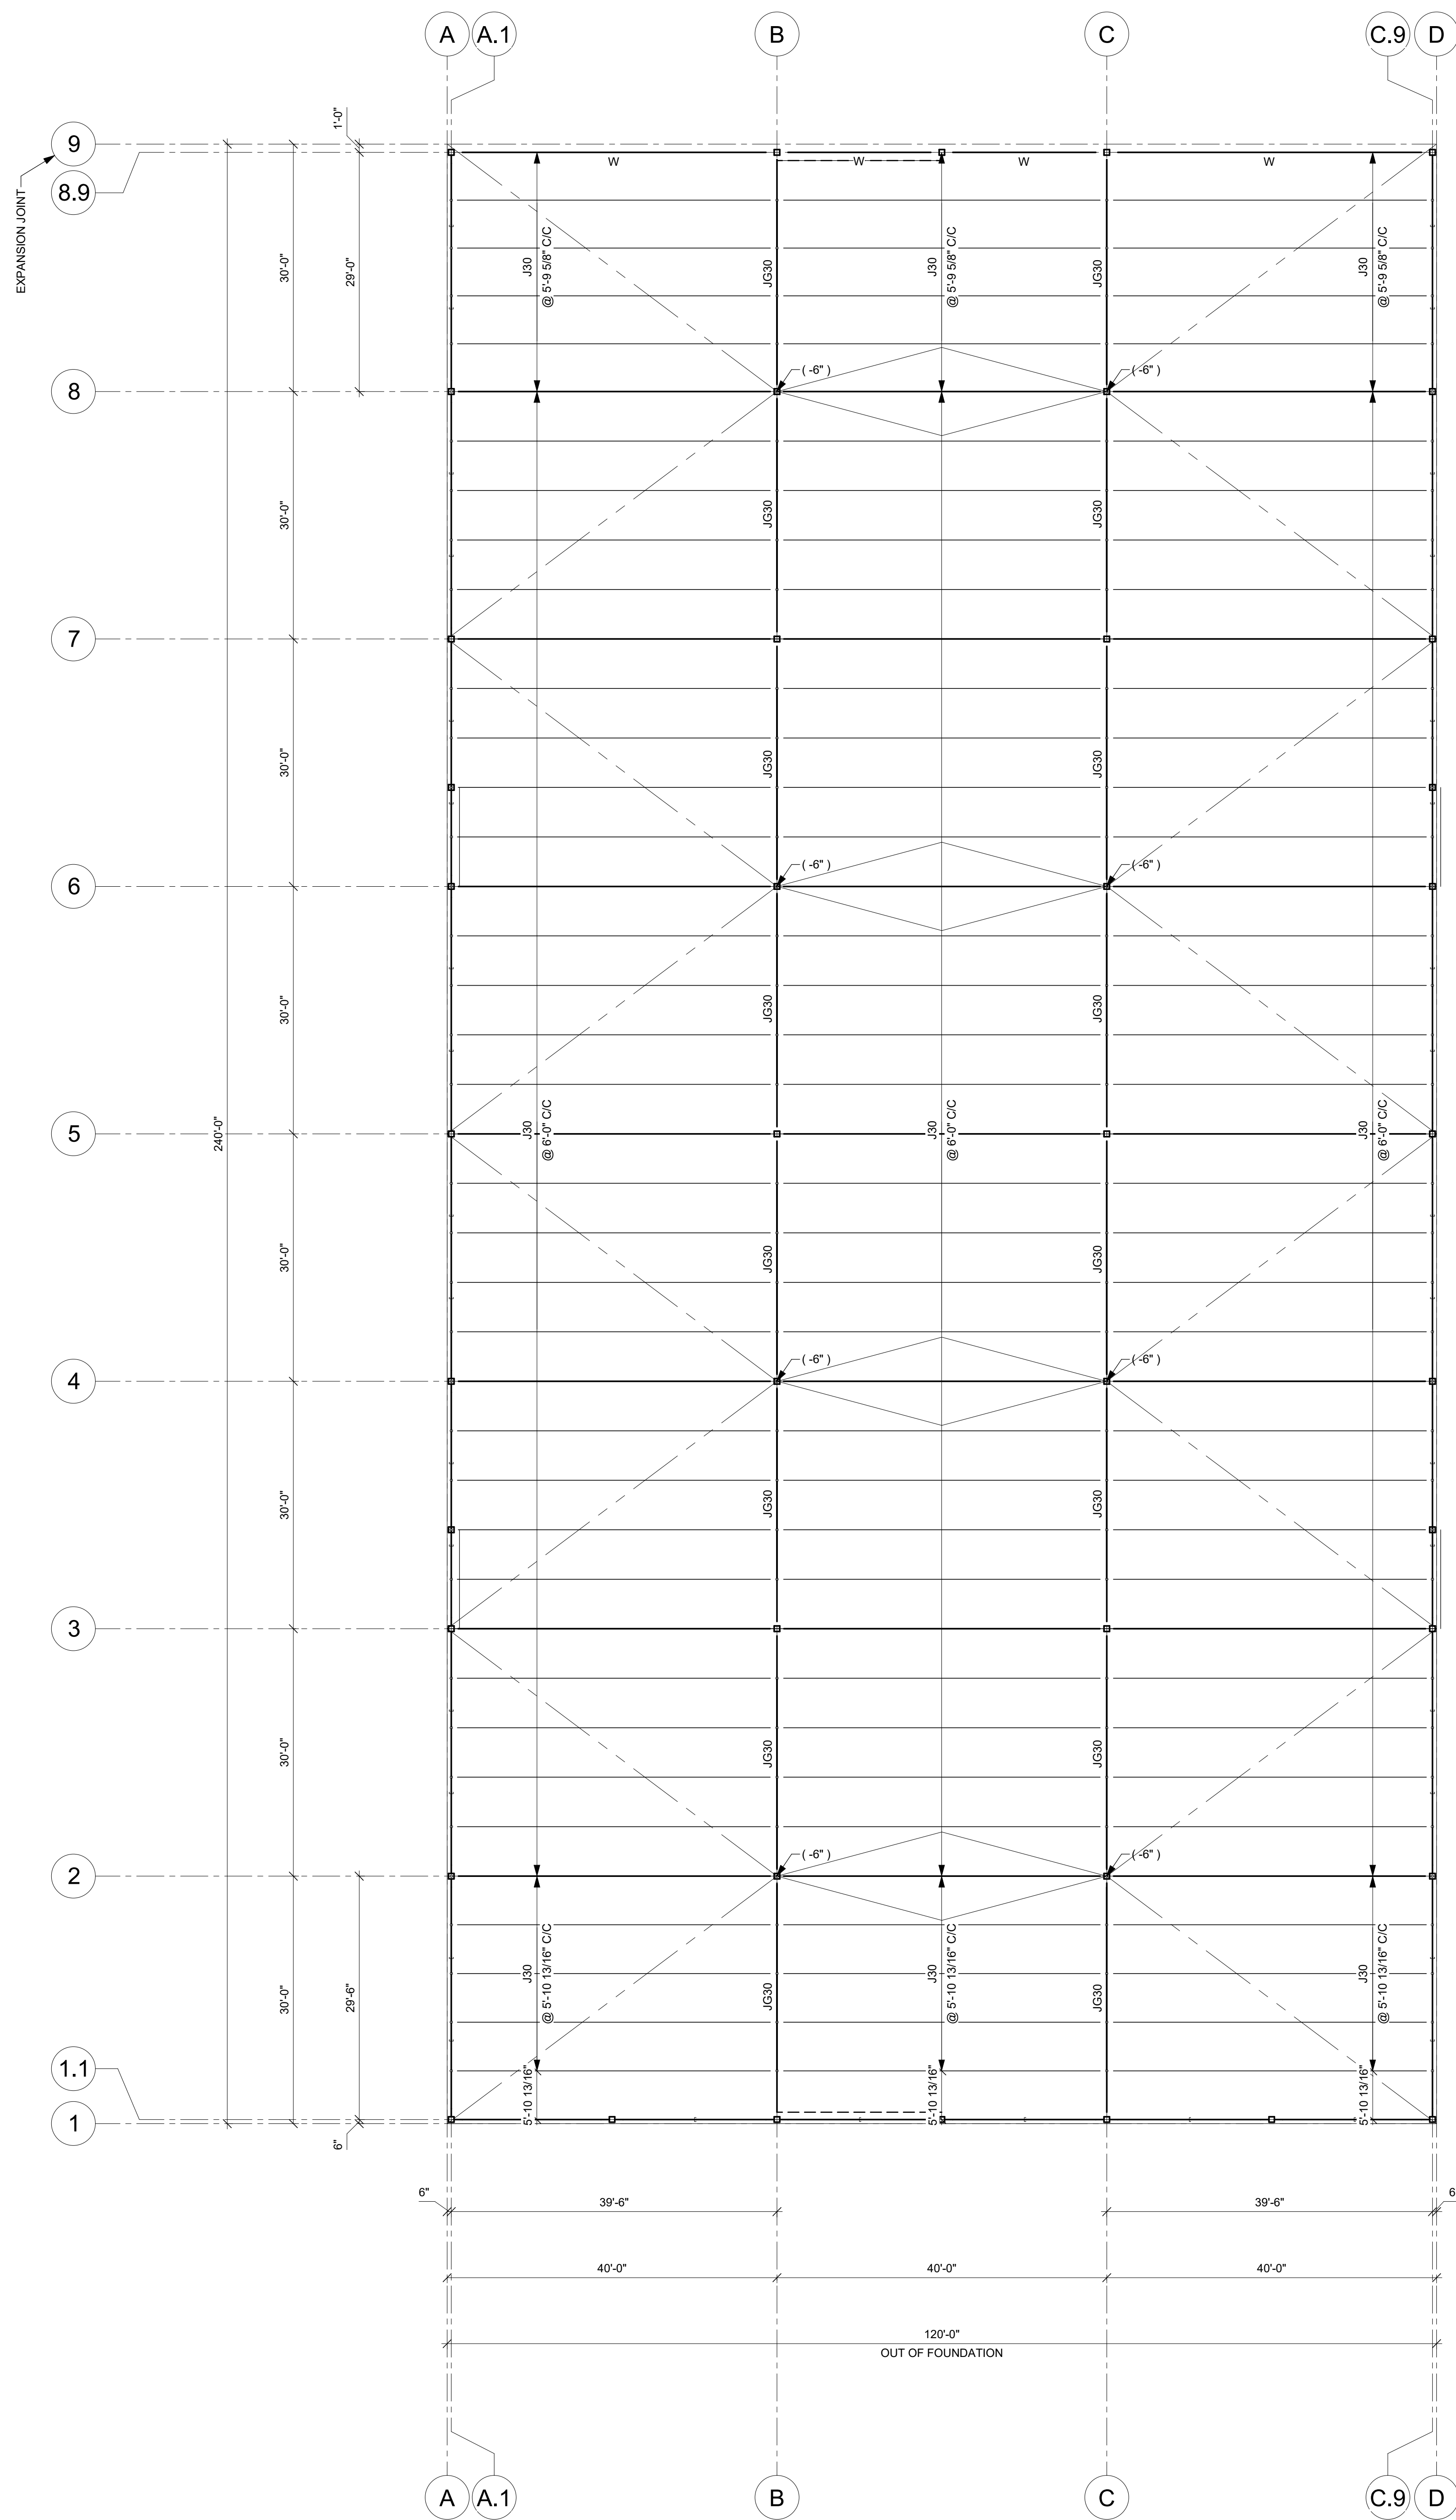


ROOF PLAN 1 @ 9  
3/32" = 1'-0"


GROSS UPLIFT DIAGRAM (UNFACTORED):

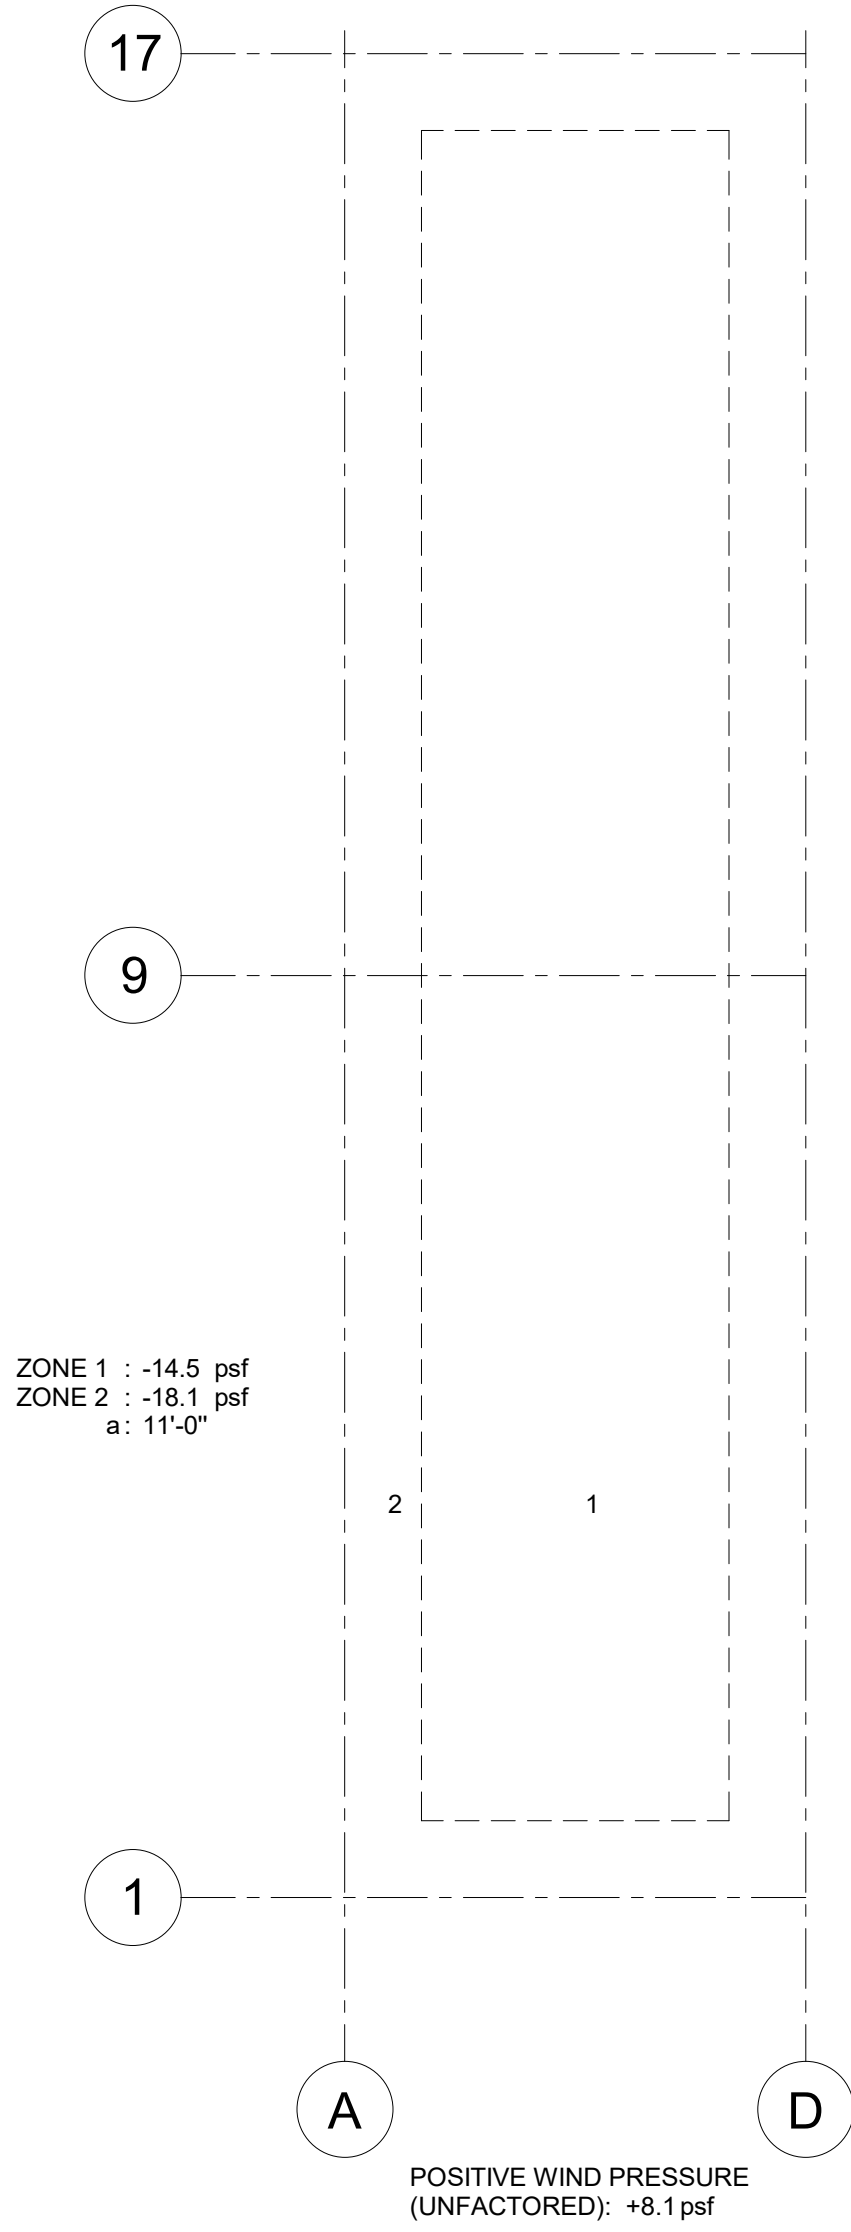

SNOW LOAD ACCUMULATION

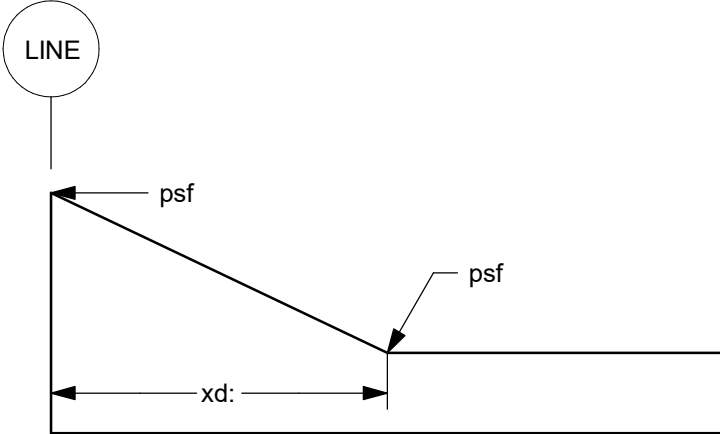

RAIN LOAD + ADDITIONAL LIVE LOAD

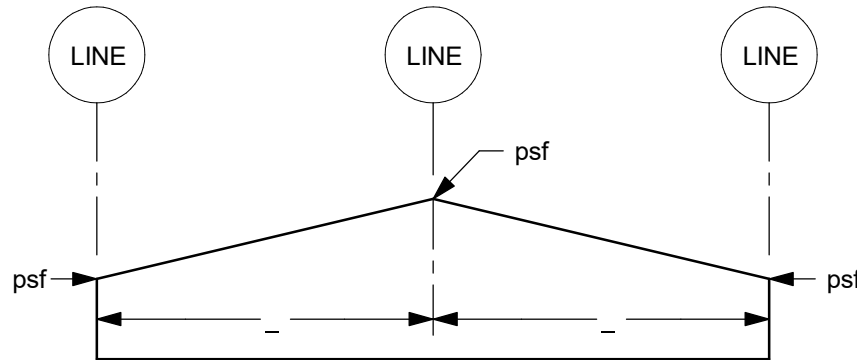

CONTRACTOR/RECTOR NOTE:

IT IS PROHIBITED TO MODIFY, COPY, REPRODUCE OR OTHERWISE  
DISTRIBUTE THIS DRAWING OR ANY REPRESENTATION OF THIS  
DRAWING, OR ANY MEDIA, INCLUDING ELECTRONIC, WITHOUT THE  
PRIOR WRITTEN APPROVAL OF CANAM GROUP INC.

ROOF

TOP OF PLASTER RWL : 98'-0"  
TOP OF PLASTER : 99'-0"  
TOP OF SLAB : 100'-0"  
TOP OF FOUNDATION : 100'-0"  
CLEAR HEIGHT : 124'-0"  
TOP OF STEEL : 127'-4"  
PARAPET HEIGHT : 1'-2"  
TOP OF PARAPET : 128'-6"

LOADS

D.L. : 18 psf  
Coll. : 5 psf  
S<sub>u</sub> : 23.0 psf  
S<sub>r</sub> : 2.1 psf  
C<sub>D</sub> + C<sub>w</sub> : 0.9  
Roof L.L. : 0 psf  
I<sub>s</sub> : 1.0  
Roof snow load : 21 psf  
I<sub>w</sub> : 1.0  
Wind q = 150 : 10.0 psf

Seismic (Site class: D (Assumed))

S<sub>u</sub> (0.2) : 0.309  
S<sub>u</sub> (0.5) : 0.266  
S<sub>u</sub> (1.0) : 0.149  
S<sub>u</sub> (2.0) : 0.0765  
S<sub>u</sub> (5.0) : 0.0345  
S<sub>u</sub> (10.0) : 0.0193  
PGA : 0.149  
PGV : 0.140

• Code Applicable : National building Code of Canada  
Quebec Building Code, latest adopted editions  
Code of Standard Practice CISC.

• Assumed soil site class: D

• NOTE :  
1. If, however, the seismic site class is determined to be E or F according to the  
geotechnical report, the preliminary structural concept (location and geometry  
of bracings, etc.) must be validated and coordinated by a Canam's engineer.

PRELIMINARY

NOT TO BE USED FOR CONSTRUCTION

| REVISION        | DATE                              | DESCRIPTION       | ISS          | VER |
|-----------------|-----------------------------------|-------------------|--------------|-----|
| PROJECT MANAGER |                                   |                   |              |     |
|                 |                                   |                   |              |     |
|                 |                                   |                   |              |     |
|                 |                                   |                   |              |     |
|                 |                                   |                   |              |     |
| DRAFTING        |                                   |                   |              |     |
| DRAWN           | DESIGNED                          | PROJECT ENGINEER  | SCALE        |     |
| J.B.            |                                   |                   | AS INDICATED |     |
| CHECKED         | CONSULTING ENGINEERS / ARCHITECTS | DATE (yyyy/mm/dd) |              |     |
|                 |                                   | 2028/01/29        |              |     |

CUSTOMER:

**CANAM**  
11505, 1re Avenue, bureau 500, Saint-Georges Beauséjour  
Québec, Canada, G3Y 7G3  
Phone : (418) 228-8031  
Toll free : (877) 499-6049  
www.canam.com

PROFESSIONAL SEAL

PROJECT

Calgary, Alberta

DRAWING TITLE

PRELIMINARY SKETCH - ROOF PLAN -  
LINE 1 @ 9

| CONTRACT NUMBER | DRAWING NUMBER | DIVISION | REVISION |
|-----------------|----------------|----------|----------|
| P2026-017       | EsMx401        |          |          |