




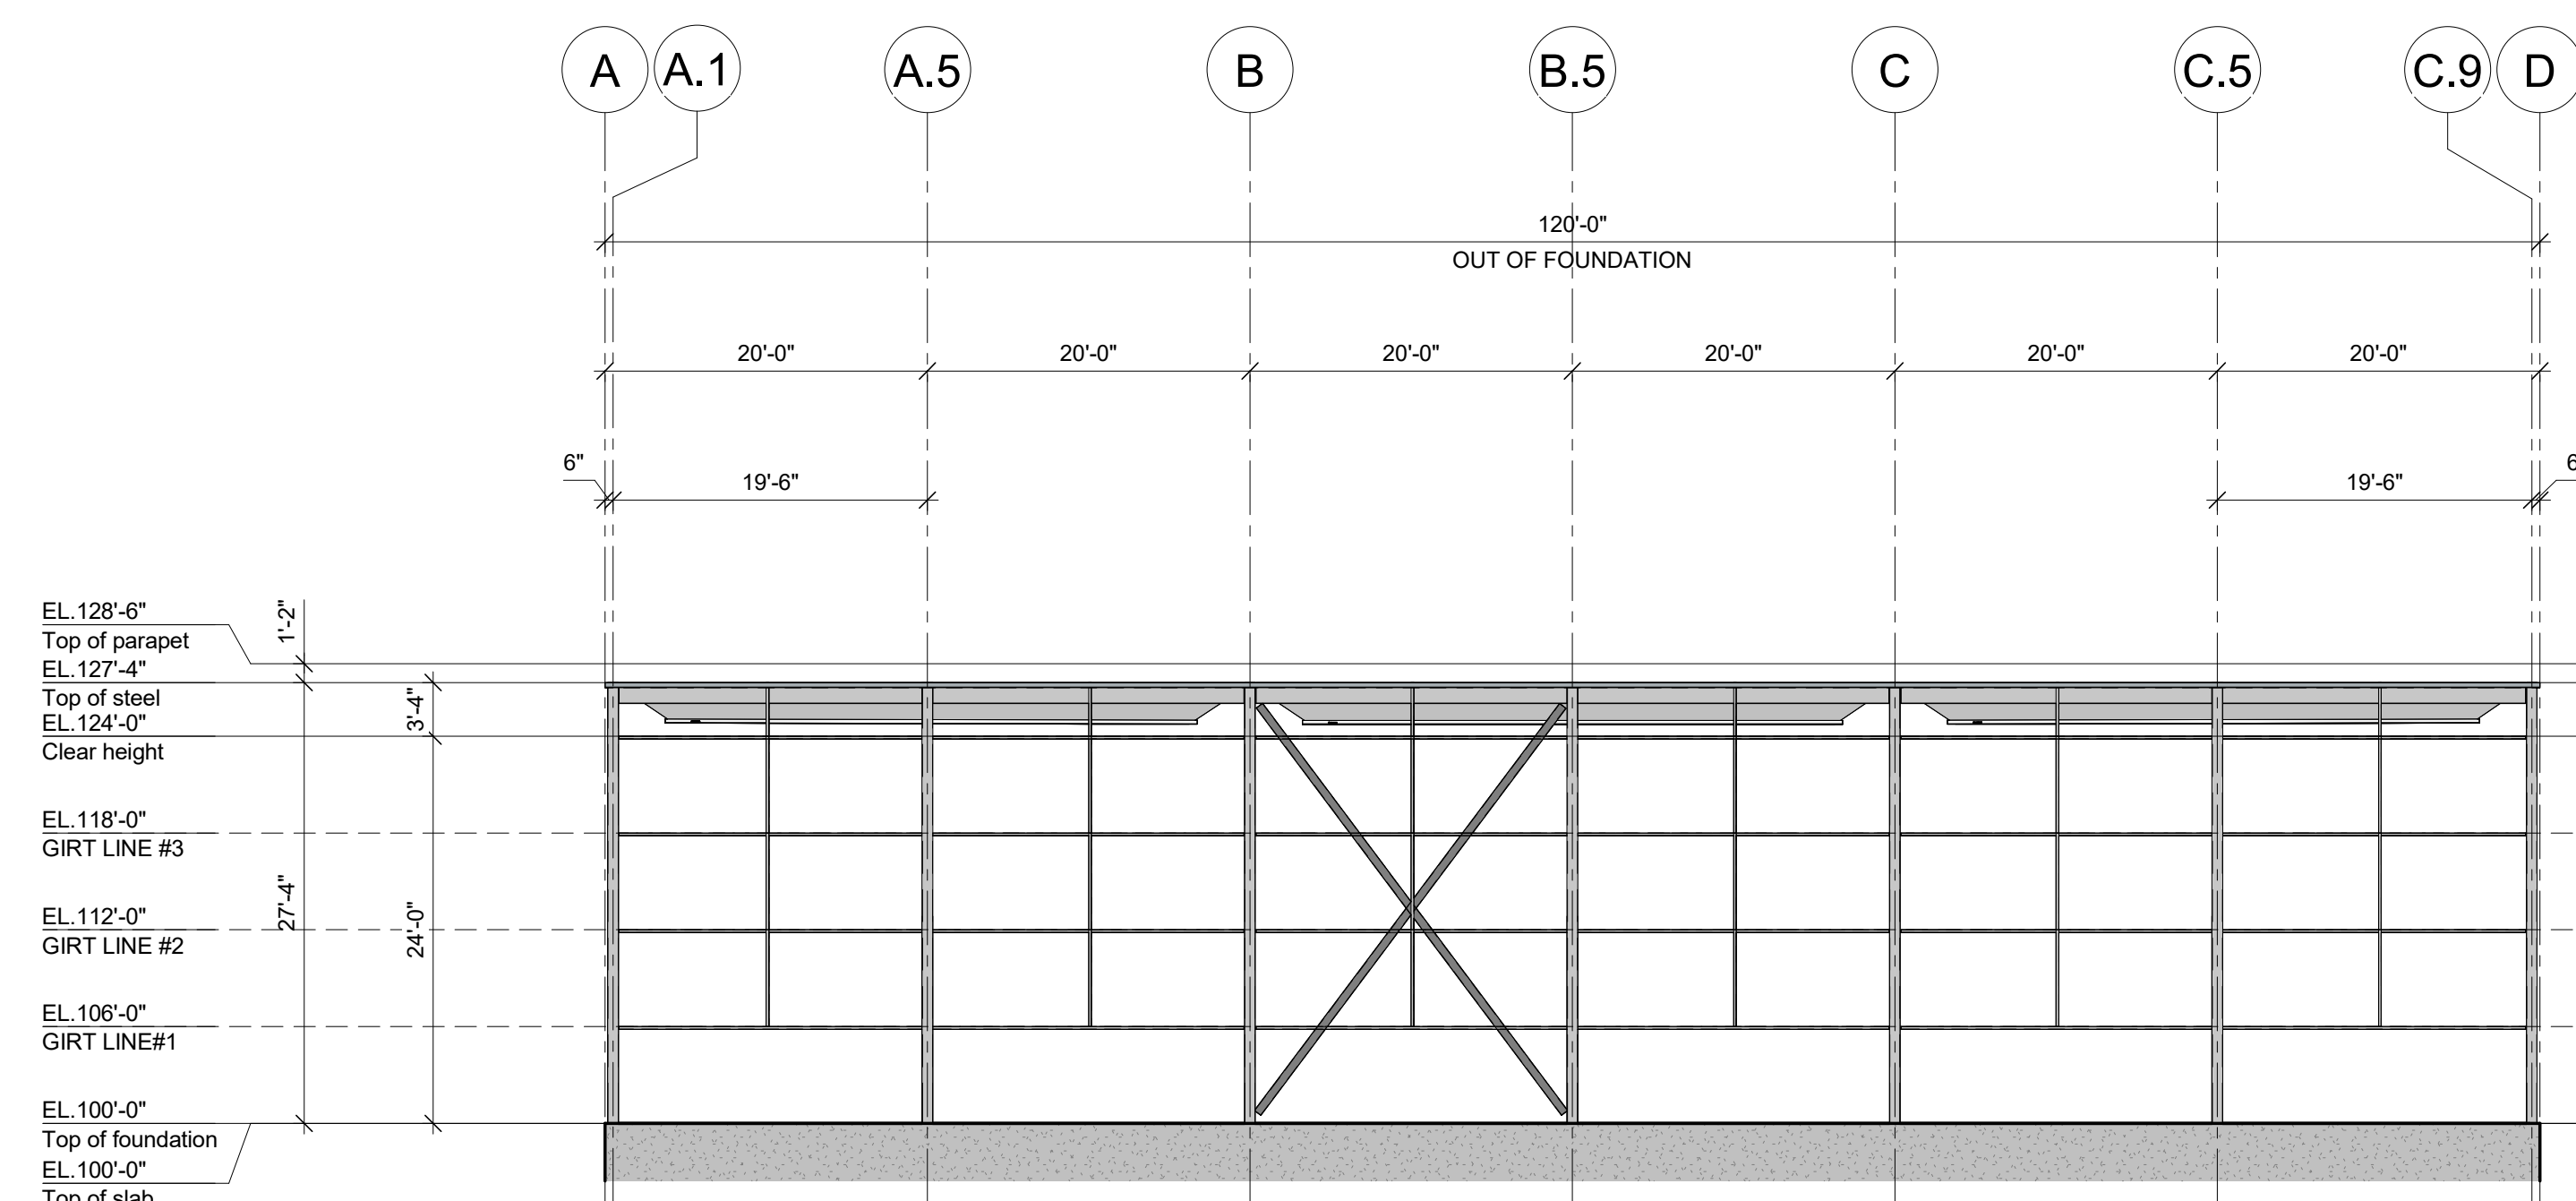


ELEVATION LINE 1 (SOUTH)
3/32" = 1'-0"

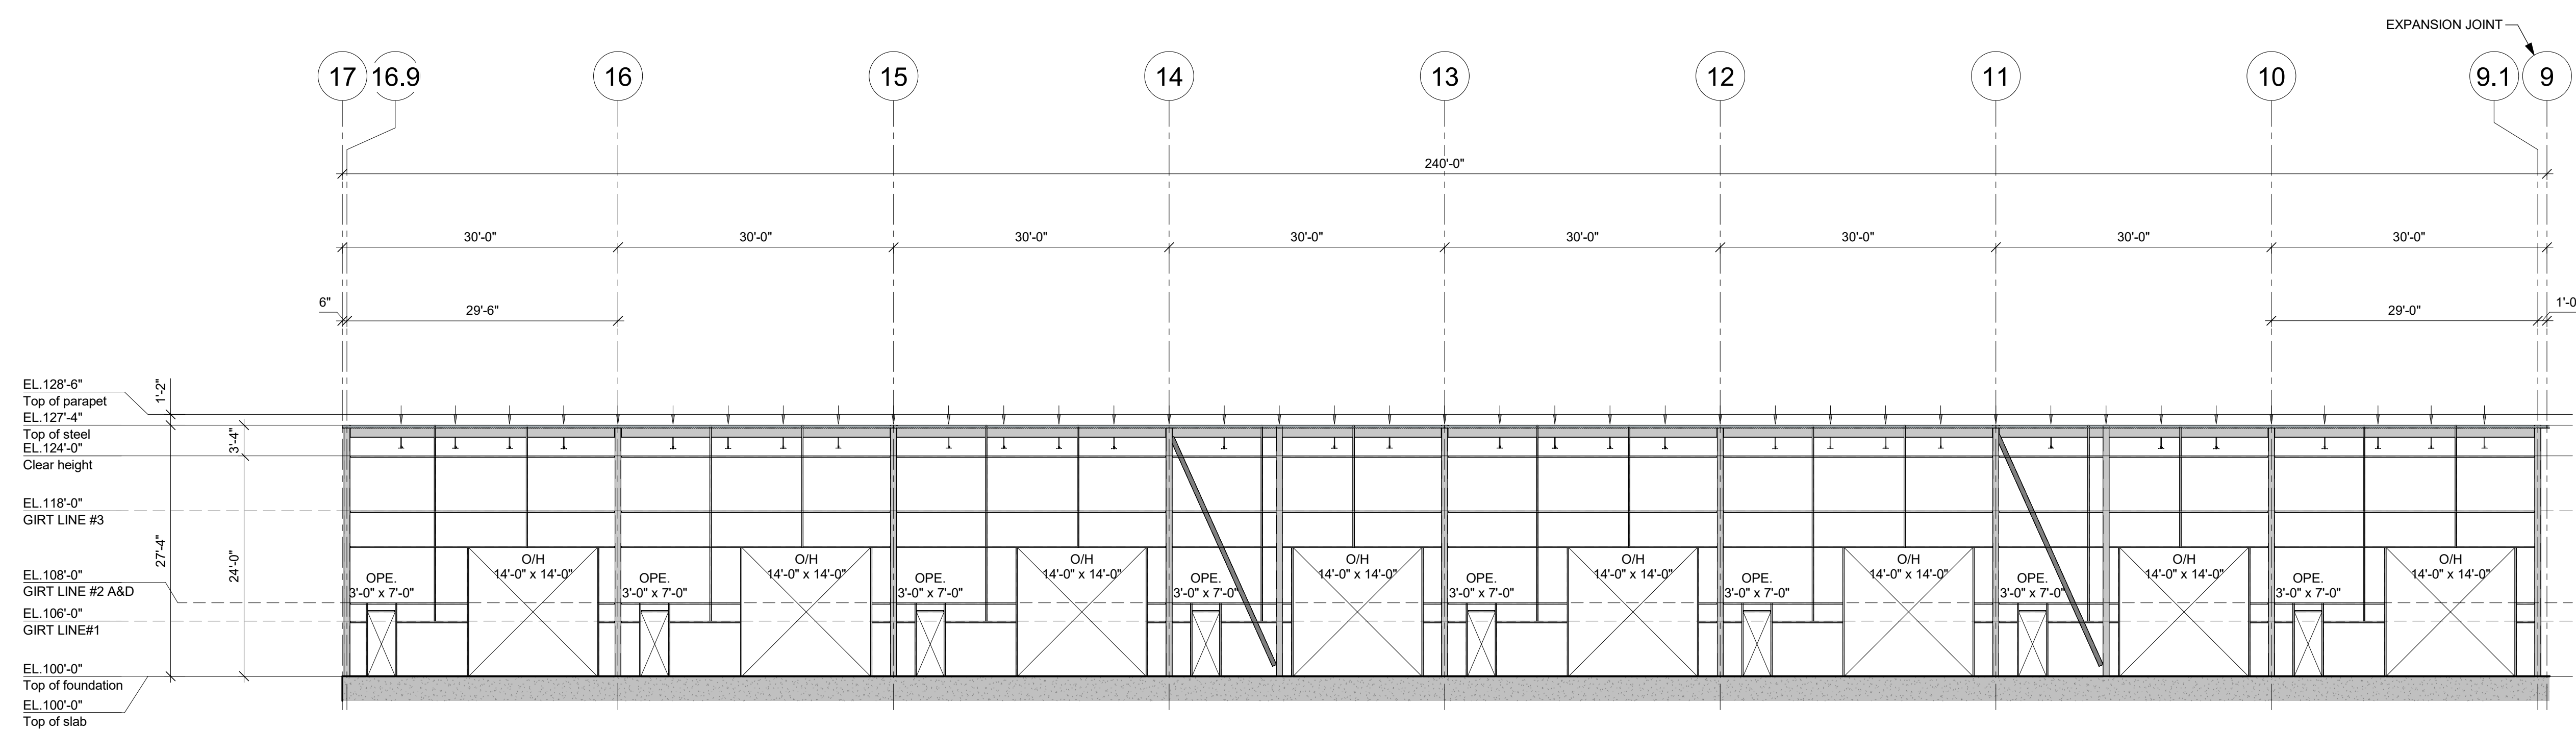

ELEVATION LINE A (WEST) - LINE 17 @ 9
3/32" = 1'-0"

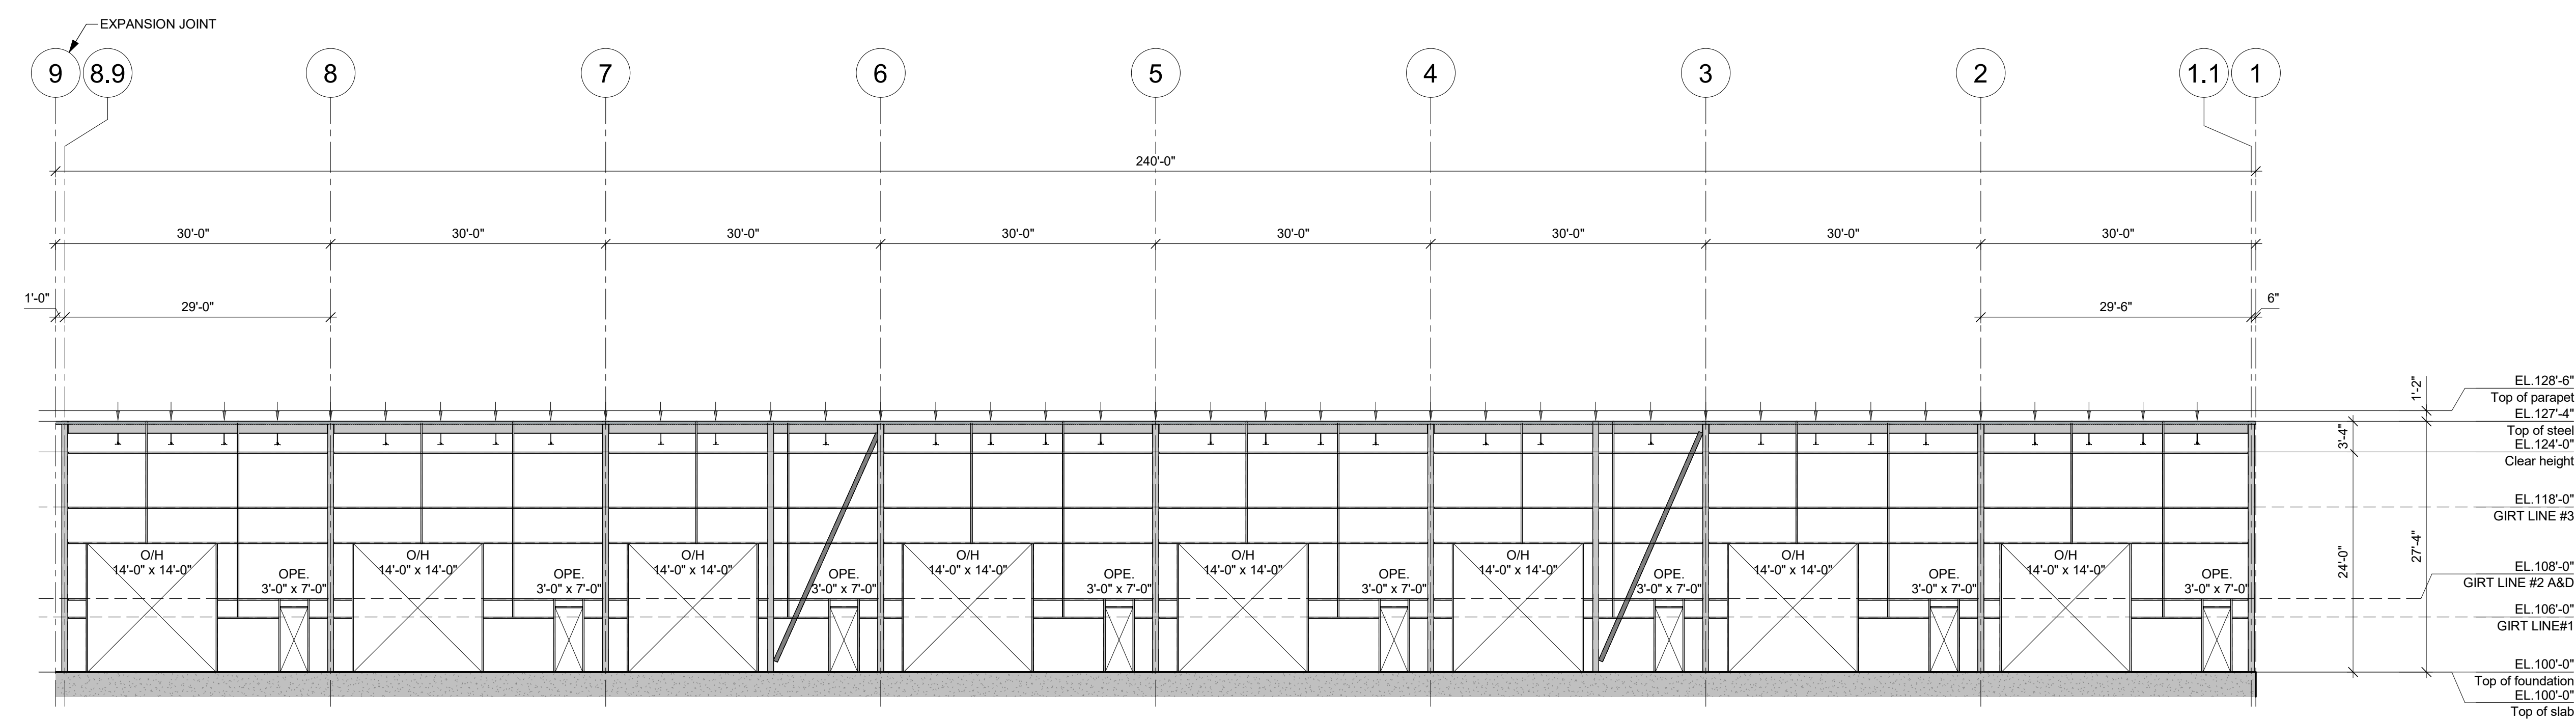

ELEVATION LINE A (WEST) - LINE 9 @ 1
3/32" = 1'-0"

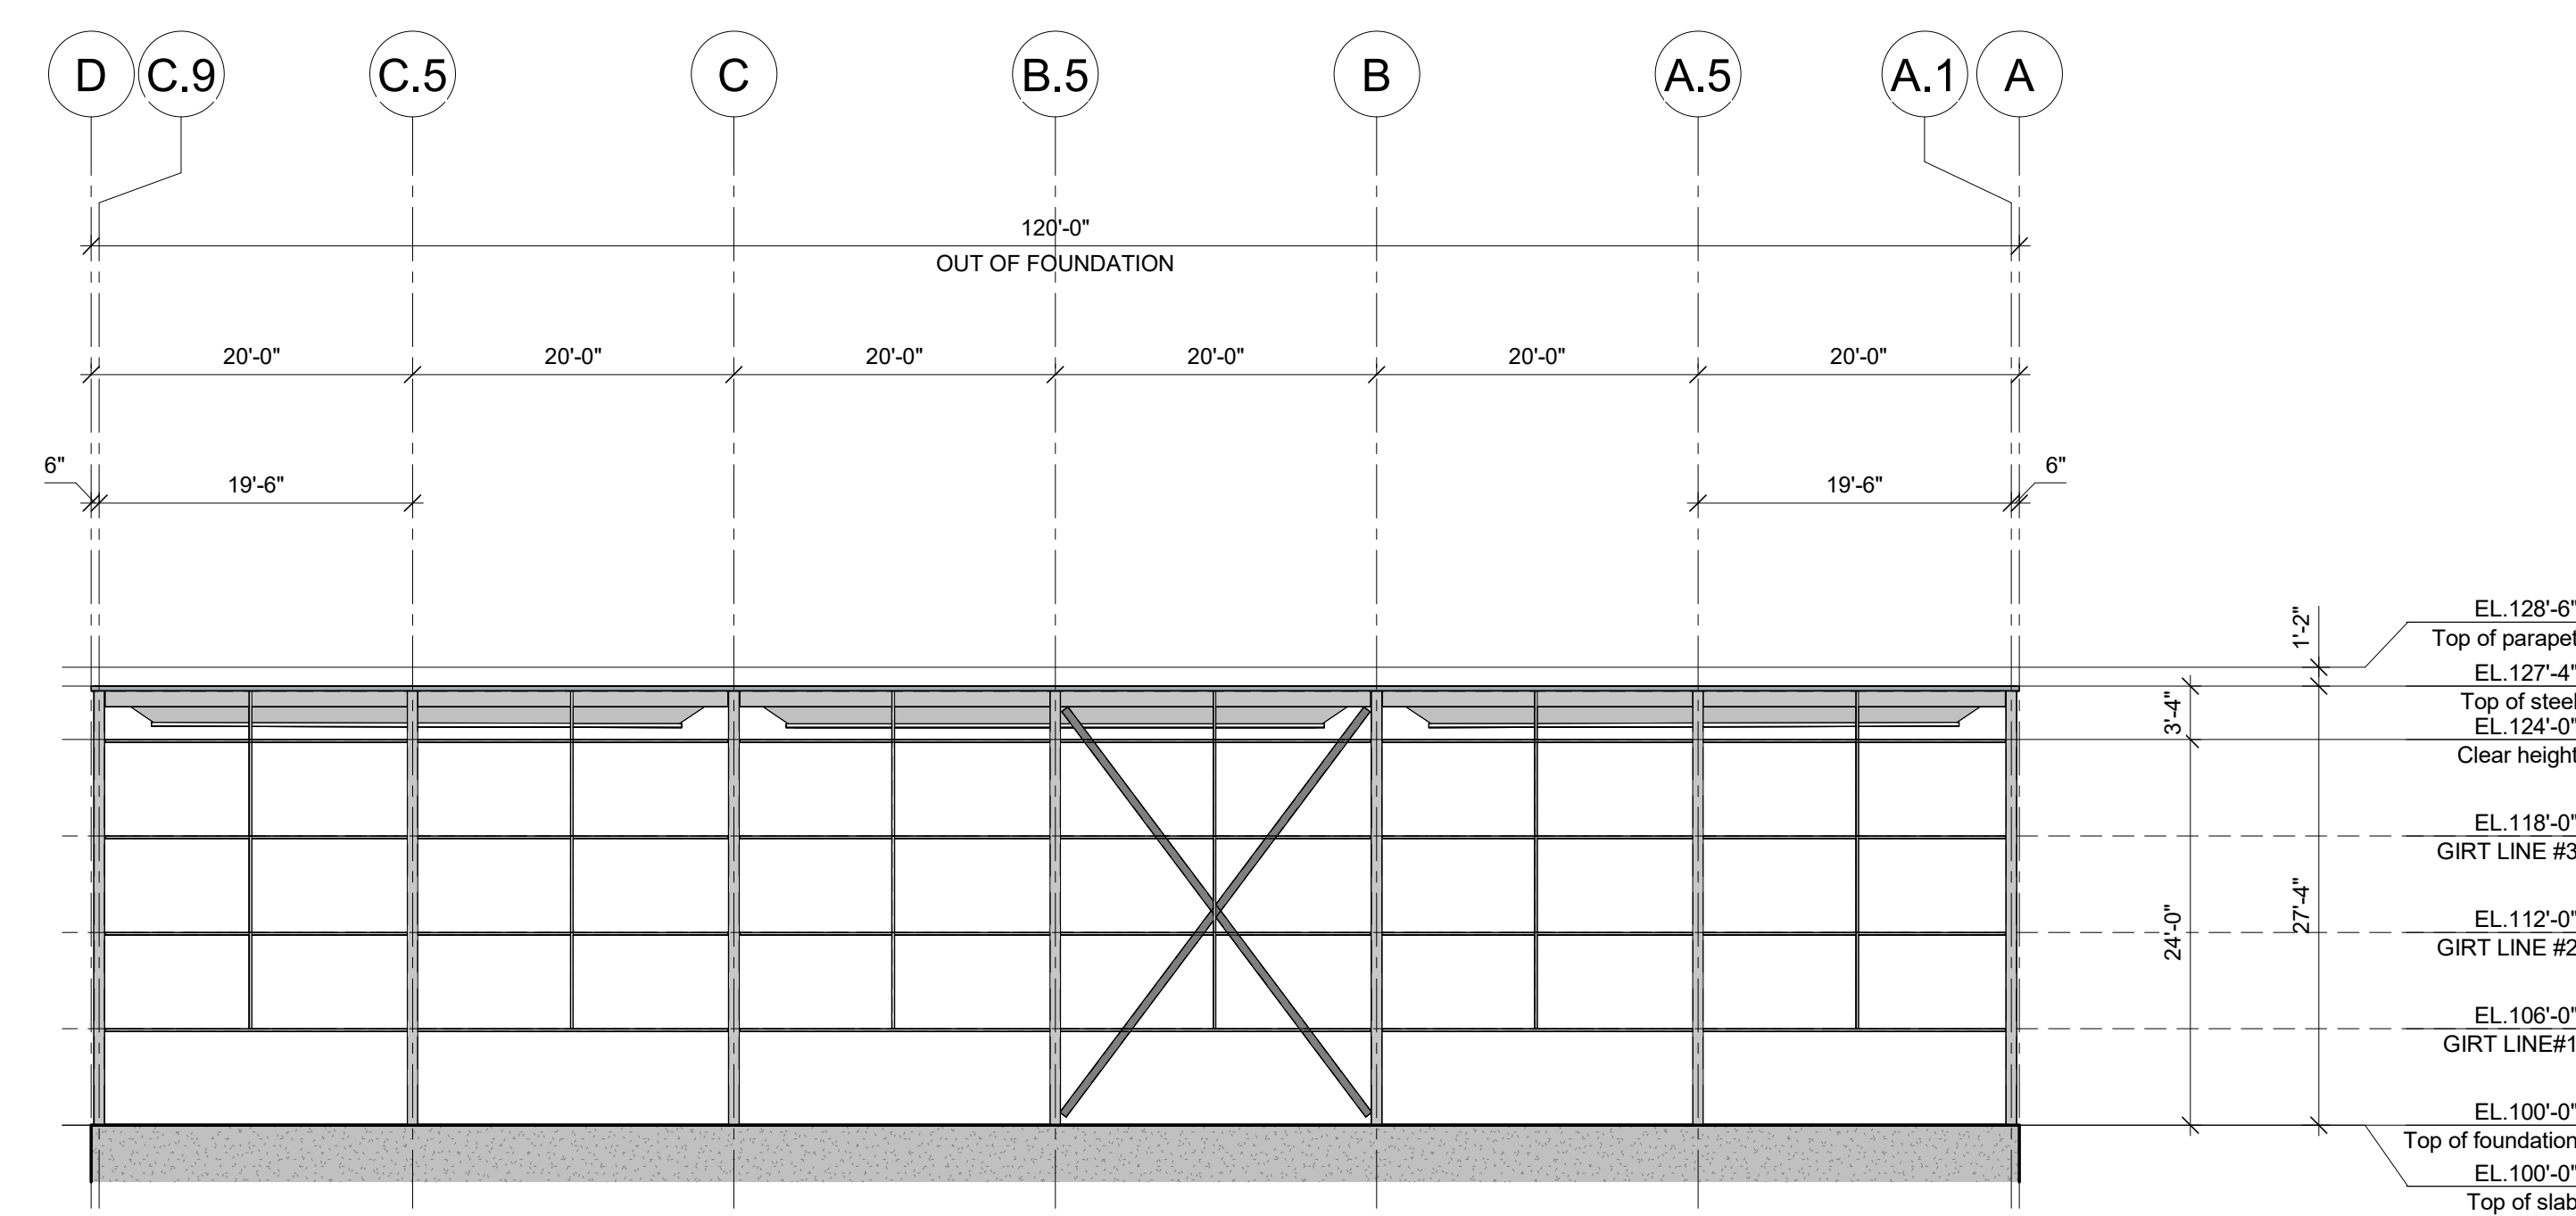

ELEVATION LINE 17 (NORTH)
3/32" = 1'-0"

CONTRACTOR/ERECTOR NOTE:
IT IS PROHIBITED TO MODIFY, COPY, REPRODUCE OR OTHERWISE
DISTRIBUTE THIS DRAWING OR ANY REPRESENTATION OF THIS
DRAWING, OR ANY MEDIA, INCLUDING ELECTRONIC, WITHOUT THE
PRIOR WRITTEN APPROVAL OF CANAM GROUP INC.

PRELIMINARY

NOT TO BE USED FOR CONSTRUCTION

REVISION	DATE	DESCRIPTION	DESK	VER
PROJECT MANAGER				
		-		
		-		
		-		
		-		
DRAWING				
		-		
DRAWN	DESIGNED	PROJECT ENGINEER	SCALE	
J.B			3/32" = 1'-0"	
CHECKED	CONSULTING ENGINEERS / ARCHITECTS		DATE (yyyy/mm/dd)	
			2026/01/29	

11505, 1re Avenue, bureau 500, Saint-Georges Beauce
Quebec, Canada, G5Y 7X3
Phone : (418) 228-8031
Toll free : (877) 499-6049
www.canam.com

PROFESSIONAL SEAL

PROJECT

Calgary, Alberta

DRAWING TITLE

PRELIMINARY SKETCH - ELEVATIONS

CONTRACT NUMBER P2026-017	DRAWING NUMBER EsMx501	DIVISION	REVISION 
------------------------------	---------------------------	----------	---