


Scale

WINDOW SCHEDULE						
Identity	Qty	Installation	Description	Sizes (Ext. of frame) (width & height)	Frame color	Remarks


OPENING SCHEDULE			
Total	Type	Tag	Remarks

DOOR SCHEDULE																				
Door 18 ga.					Glass		Hardware													
Identity	Qty	Installation	Insulation (R12)	Dimensions	Swing side	Width	Height	Steel frame 18 ga. with thermal break	(3) Hinges non-rising with removable pin	Door lock & latch set	Panic bar without outside trim 22EO	Panic bar with outside trim 23OL	Surface bolt Inactive door	Threshold	Astragal for Inactive door	Door closer	Door chain stop	Weatherstrip	Head cap	Remarks


OH & OPENING SCHEDULE			
Total	Type	Tag	Remarks

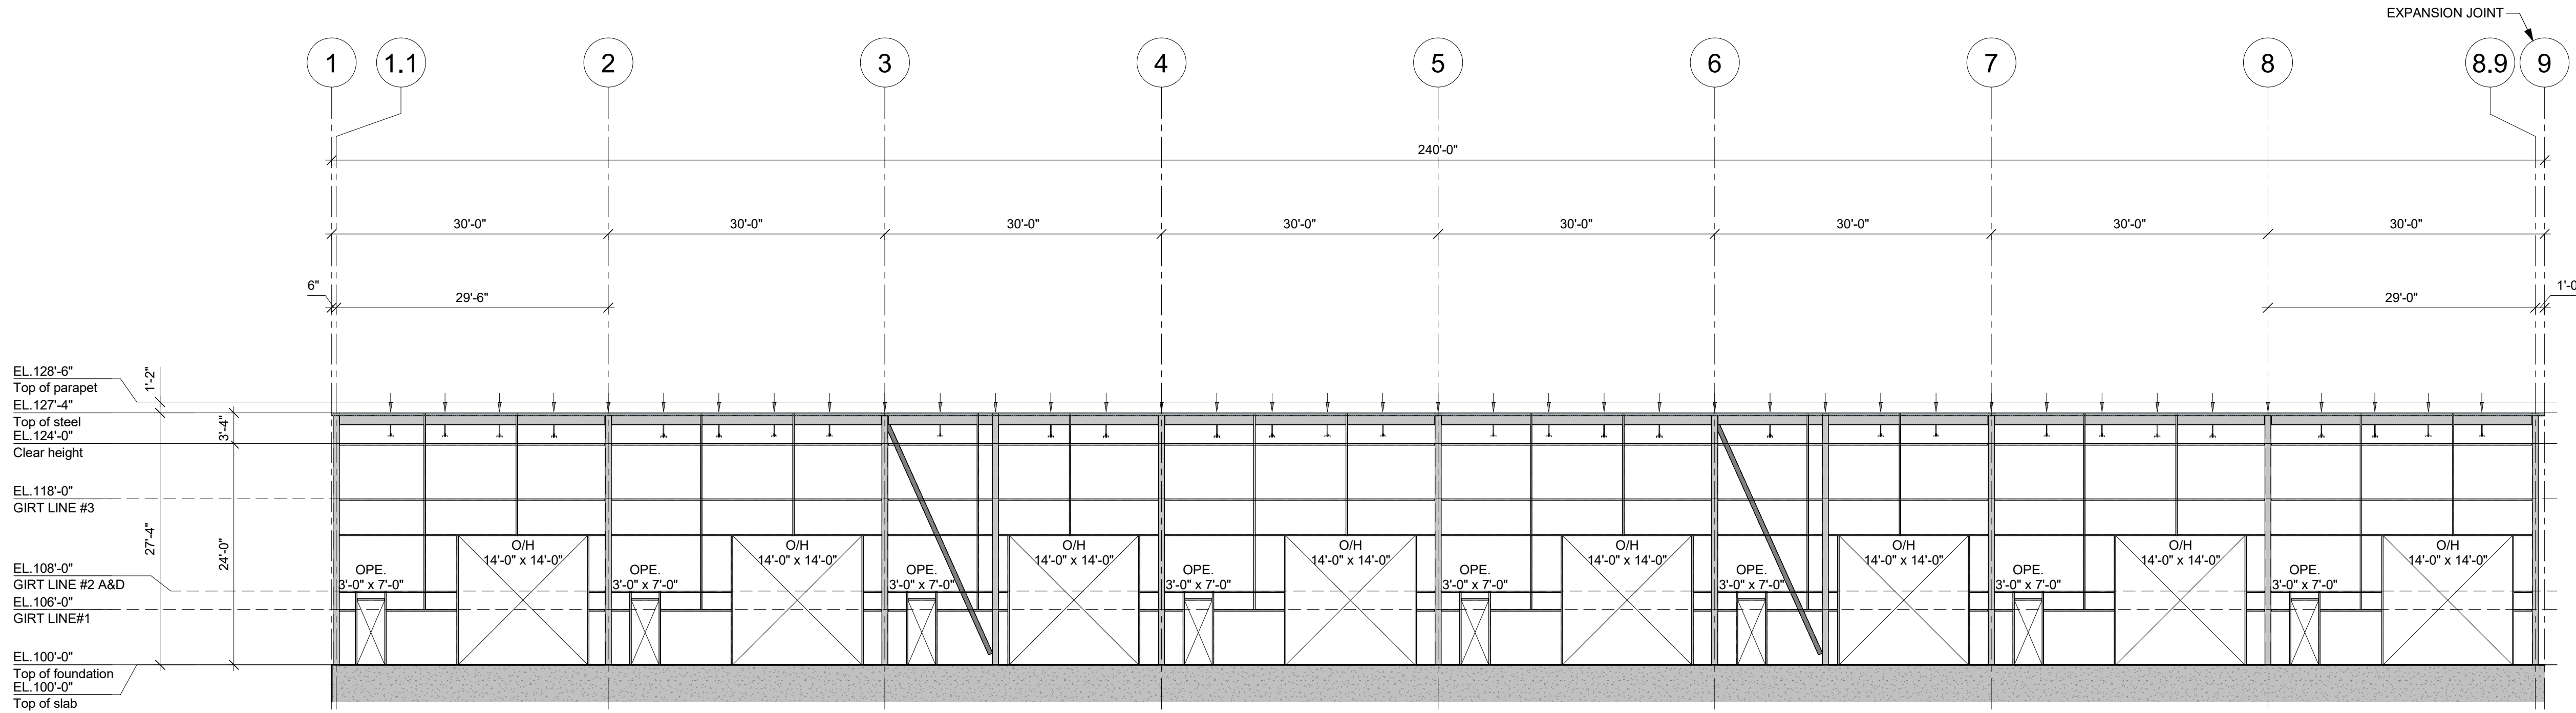


ELEVATION LINE D (EAST) - LINE 1 @ 9
3/32" = 1'-0"

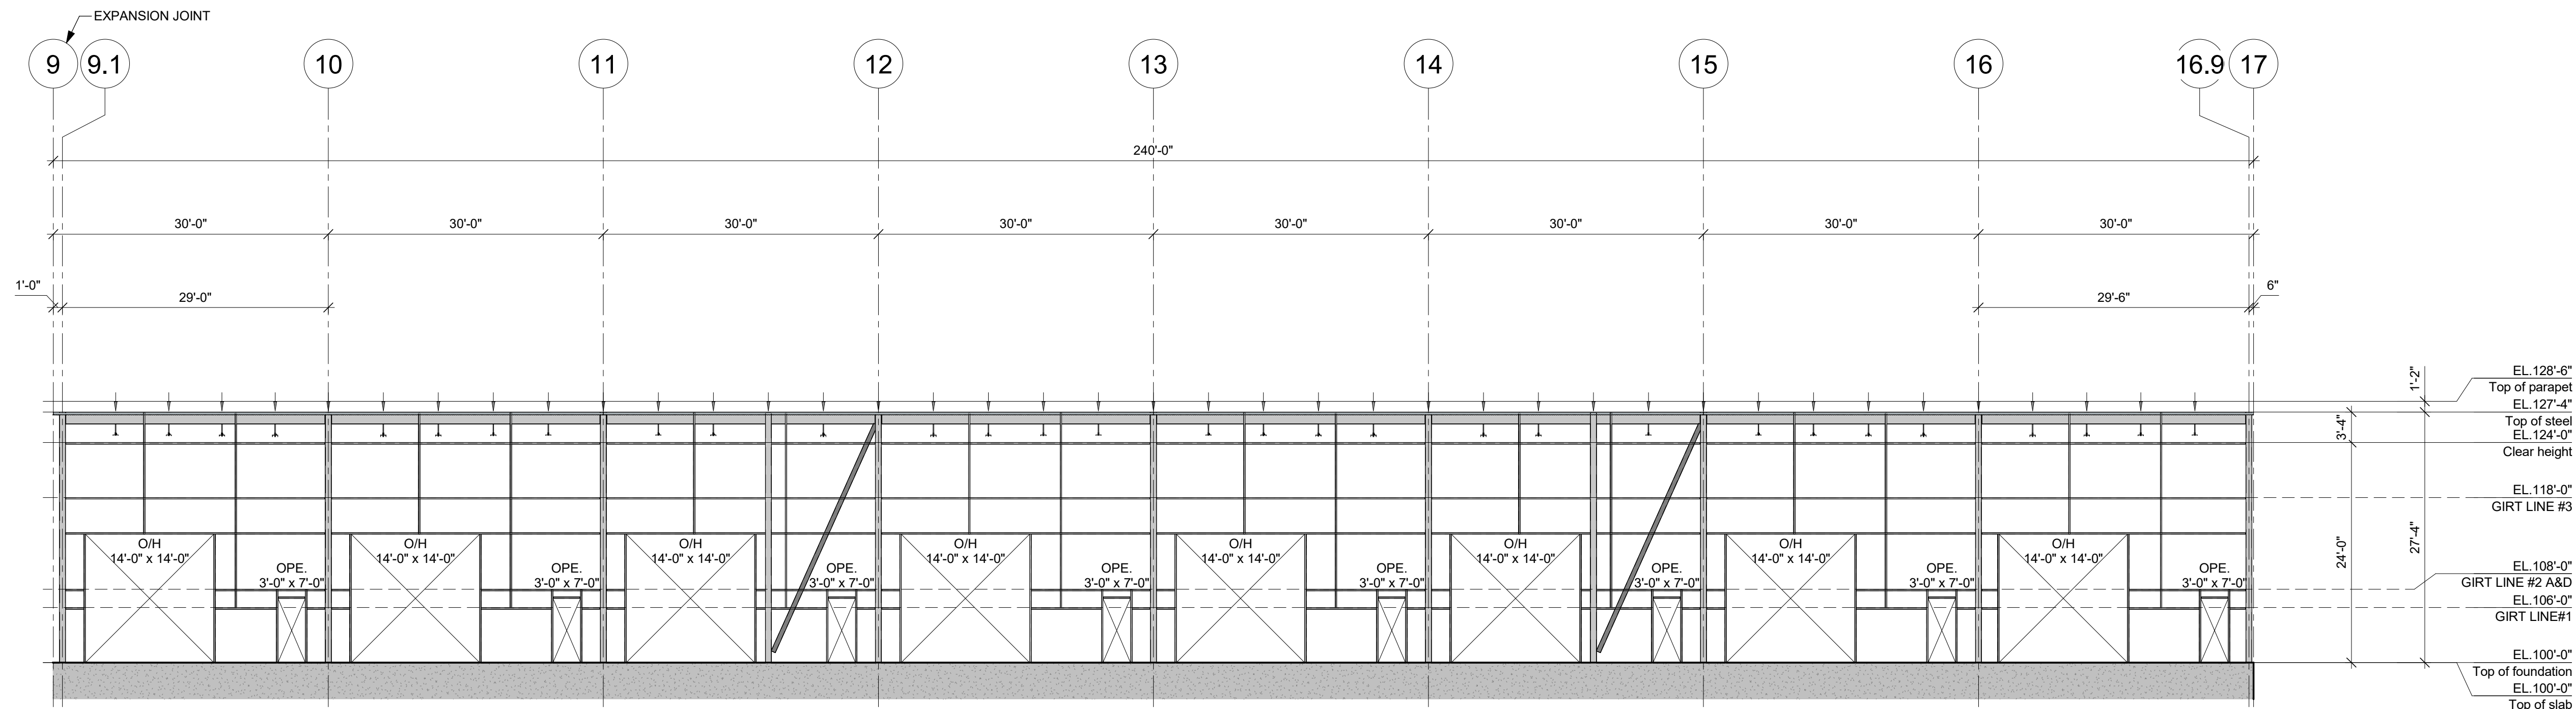

ELEVATION LINE D (EAST) - LINE 9 @ 17
3/32" = 1'-0"

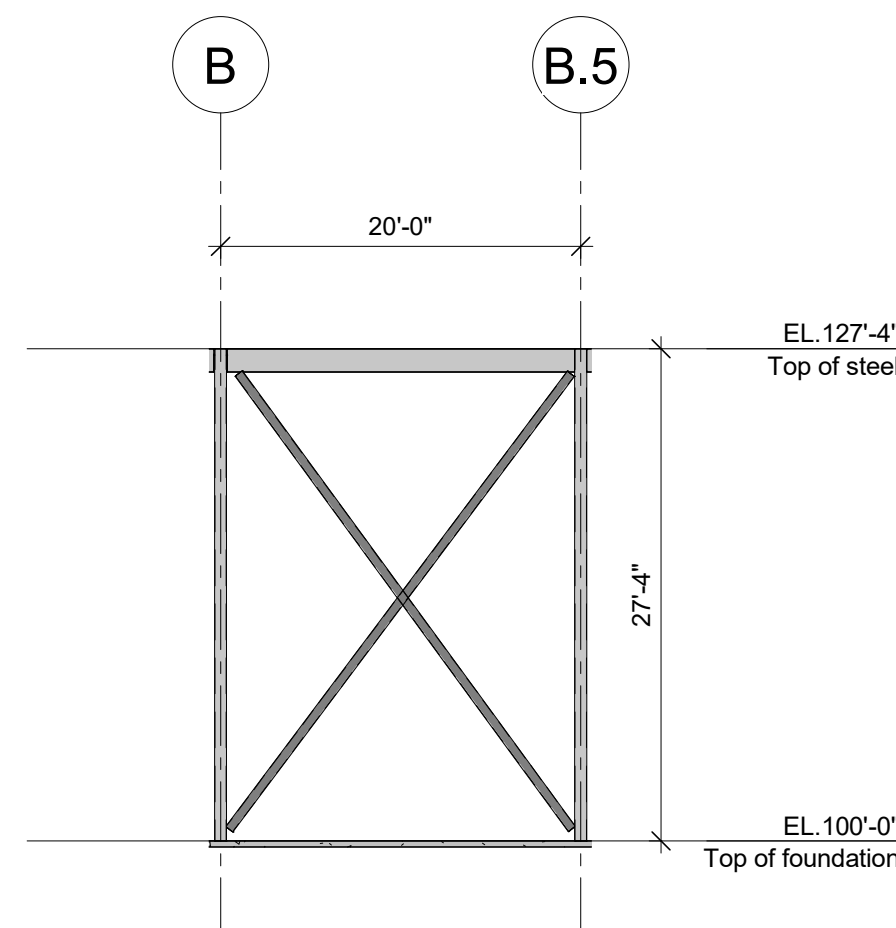

BRACING ELEVATION LINE 8.9
3/32" = 1'-0"

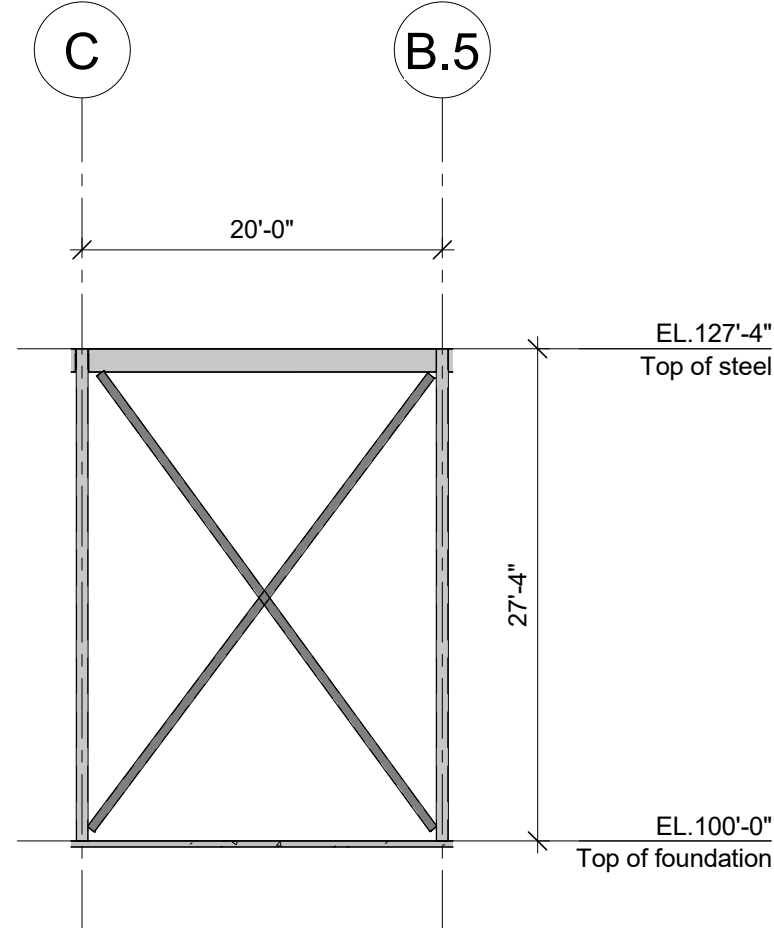

BRACING ELEVATION LINE 9.1
3/32" = 1'-0"

RHR	LHR	LHR	RHR-A	RHR
Exterior	Exterior	Exterior	Exterior	Exterior
KIT #1	KIT #2	KIT #3	KIT #4	KIT #5

Swing designation is always determined by insert key

Supplier's standard hardware:
- Hinges: Stanley FB8175 4.5" x 4"
- Exit device: Von Duprin 22 x 689 with outside trim 23OL
- Permanent cylinder: Schlage 2001C 628
- Door closure: LCN 1261 680
- Head and jamb seal: Unique 1650
- Bottom seal: Unique DS4
- Threshold: See the remarks in "Door schedule"

CONTRACTOR/RECTOR NOTE:

IT IS PROHIBITED TO MODIFY, COPY, REPRODUCE OR OTHERWISE DISTRIBUTE THIS DRAWING OR ANY REPRESENTATION OF THIS DRAWING OR ANY MEDIA, INCLUDING ELECTRONIC, WITHOUT THE PRIOR WRITTEN APPROVAL OF CANAM GROUP INC.

PRELIMINARY

NOT TO BE USED FOR CONSTRUCTION

REVISION	DATE	DESCRIPTION	ISSUE	VER
----------	------	-------------	-------	-----

PROJECT MANAGER				
-				
-				
-				

DRAFTING				
-				

DRAWN	DESIGNED	PROJECT ENGINEER	SCALE
J.B.			AS INDICATED

CHECKED	CONSULTING ENGINEERS / ARCHITECTS	DATE (yyyy/mm/dd)
		2028/01/29

CUSTOMER:	

CANAM
11505, 1re Avenue, bureau 500, Saint-Georges Beauce
Quebec, Canada, G5Y 7G3
Phone : (418) 228-8031
Toll free : (877) 499-6049
www.canam.com

PROFESSIONAL SEAL

PROJECT

Calgary, Alberta


DRAWING TITLE

PRELIMINARY SKETCH - ELEVATION,
WALL SECTION AND SCHEDULES

CONTRACT NUMBER	DRAWING NUMBER	DIVISION	REVISION
-----------------	----------------	----------	----------

P2026-017	EsMx502		
-----------	---------	--	--

Initials

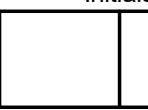

Initials

