



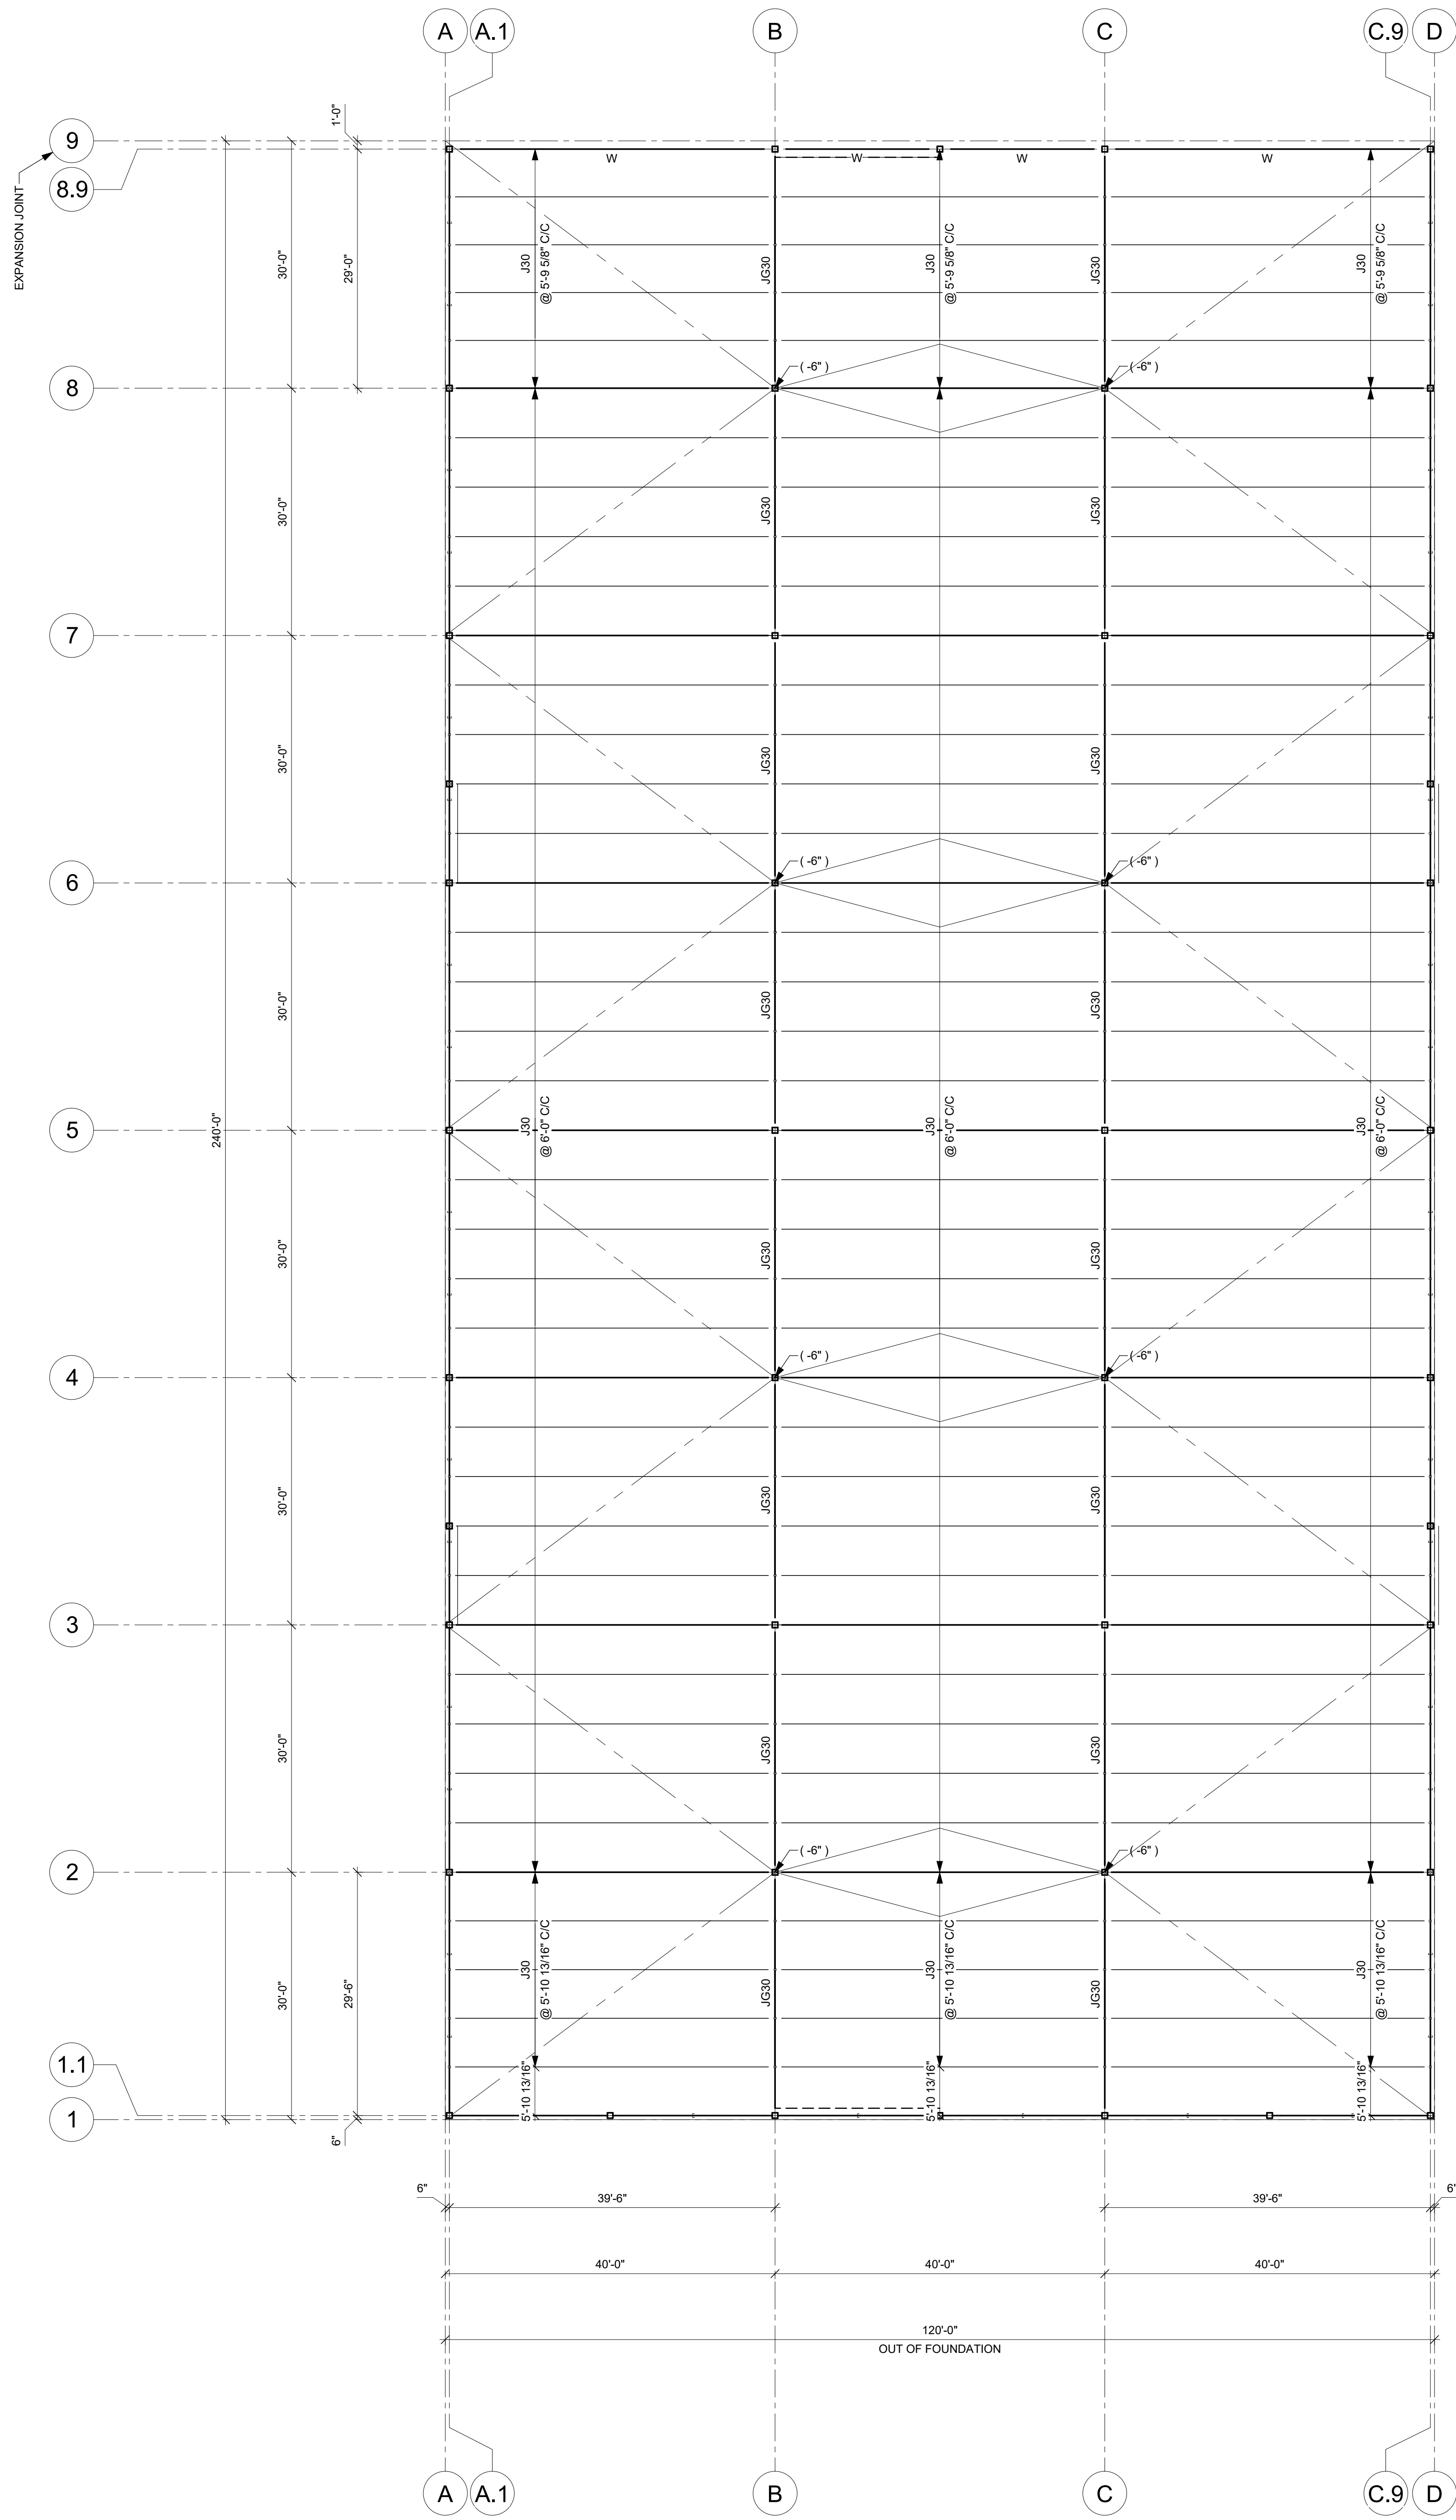


ROOF PLAN 1 @ 9
3/32" = 1'-0"

GROSS UPLIFT DIAGRAM (UNFACTORED):

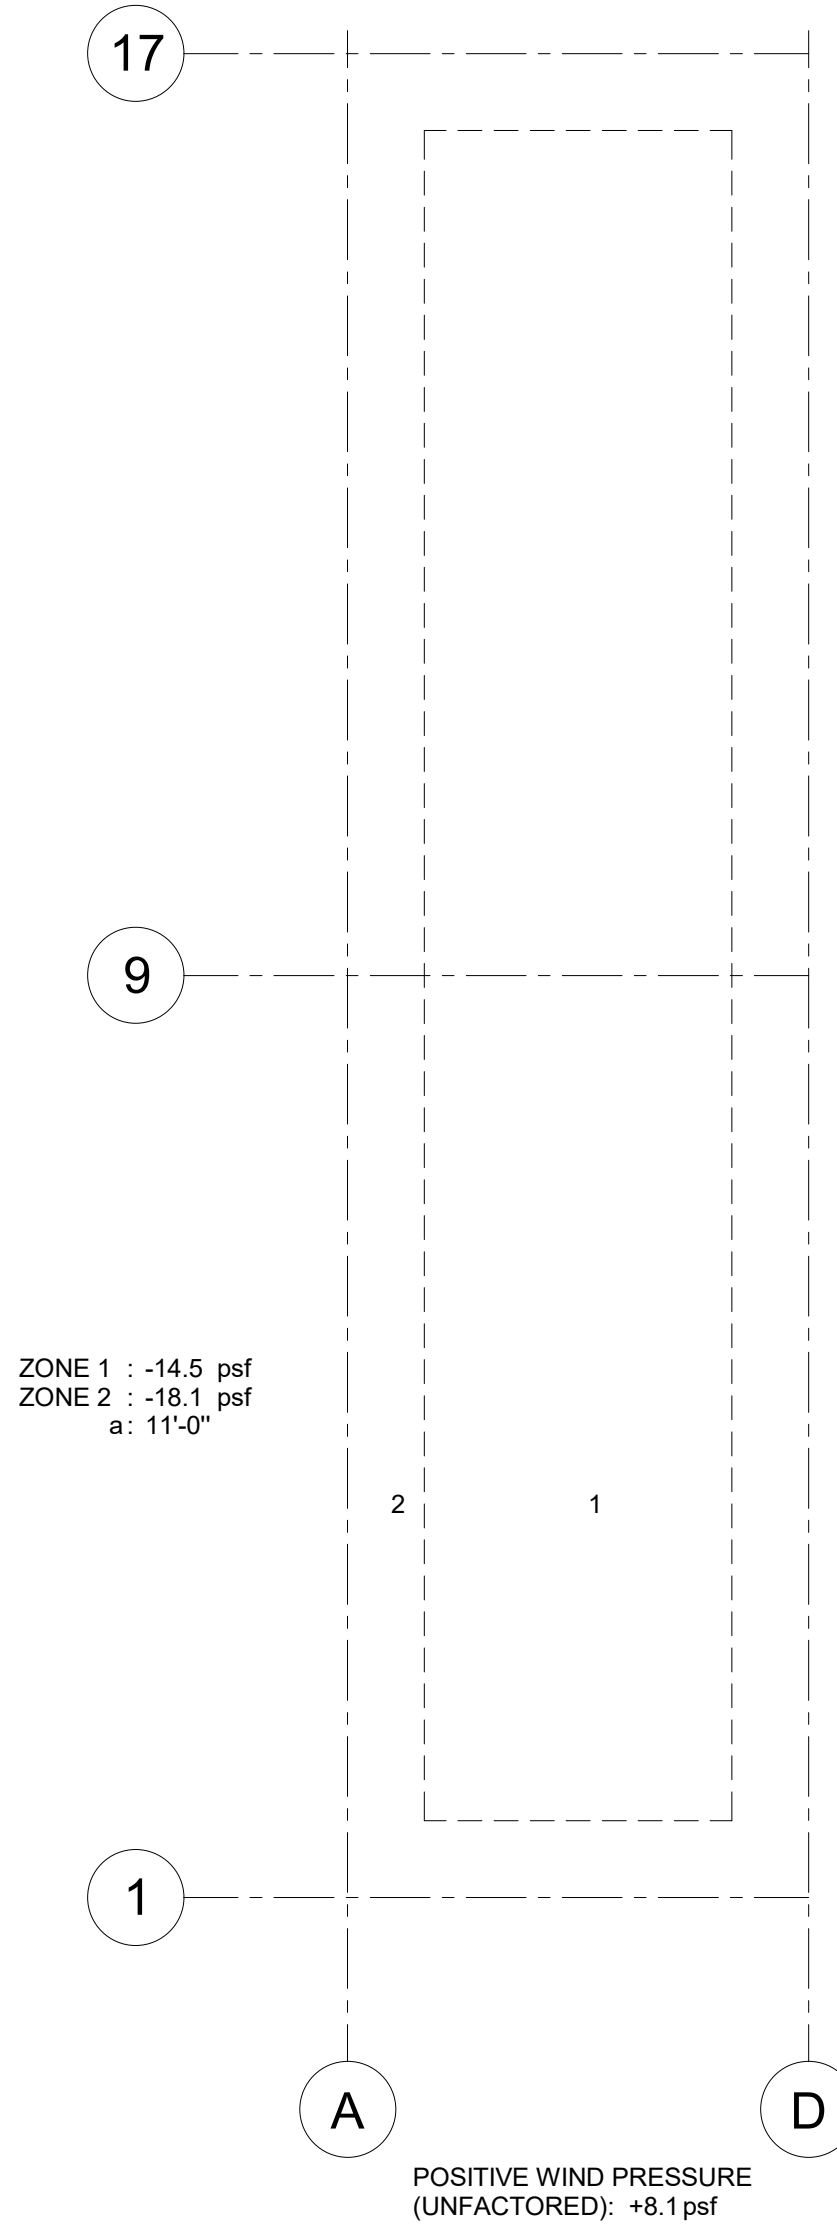

SNOW LOAD ACCUMULATION

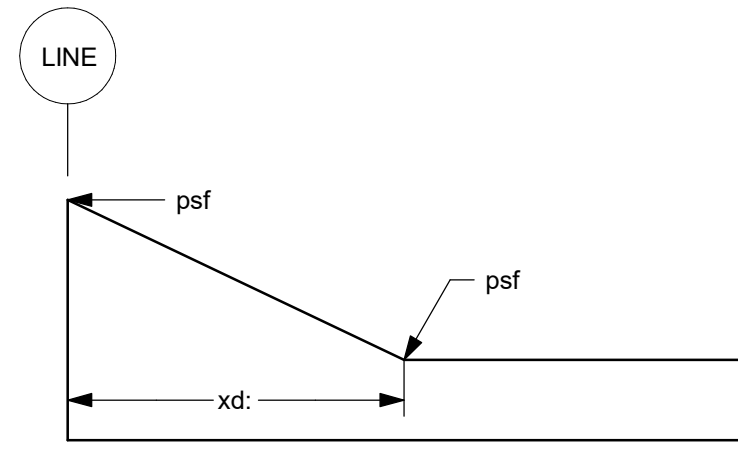

RAIN LOAD + ADDITIONNAL LIVE LOAD

