

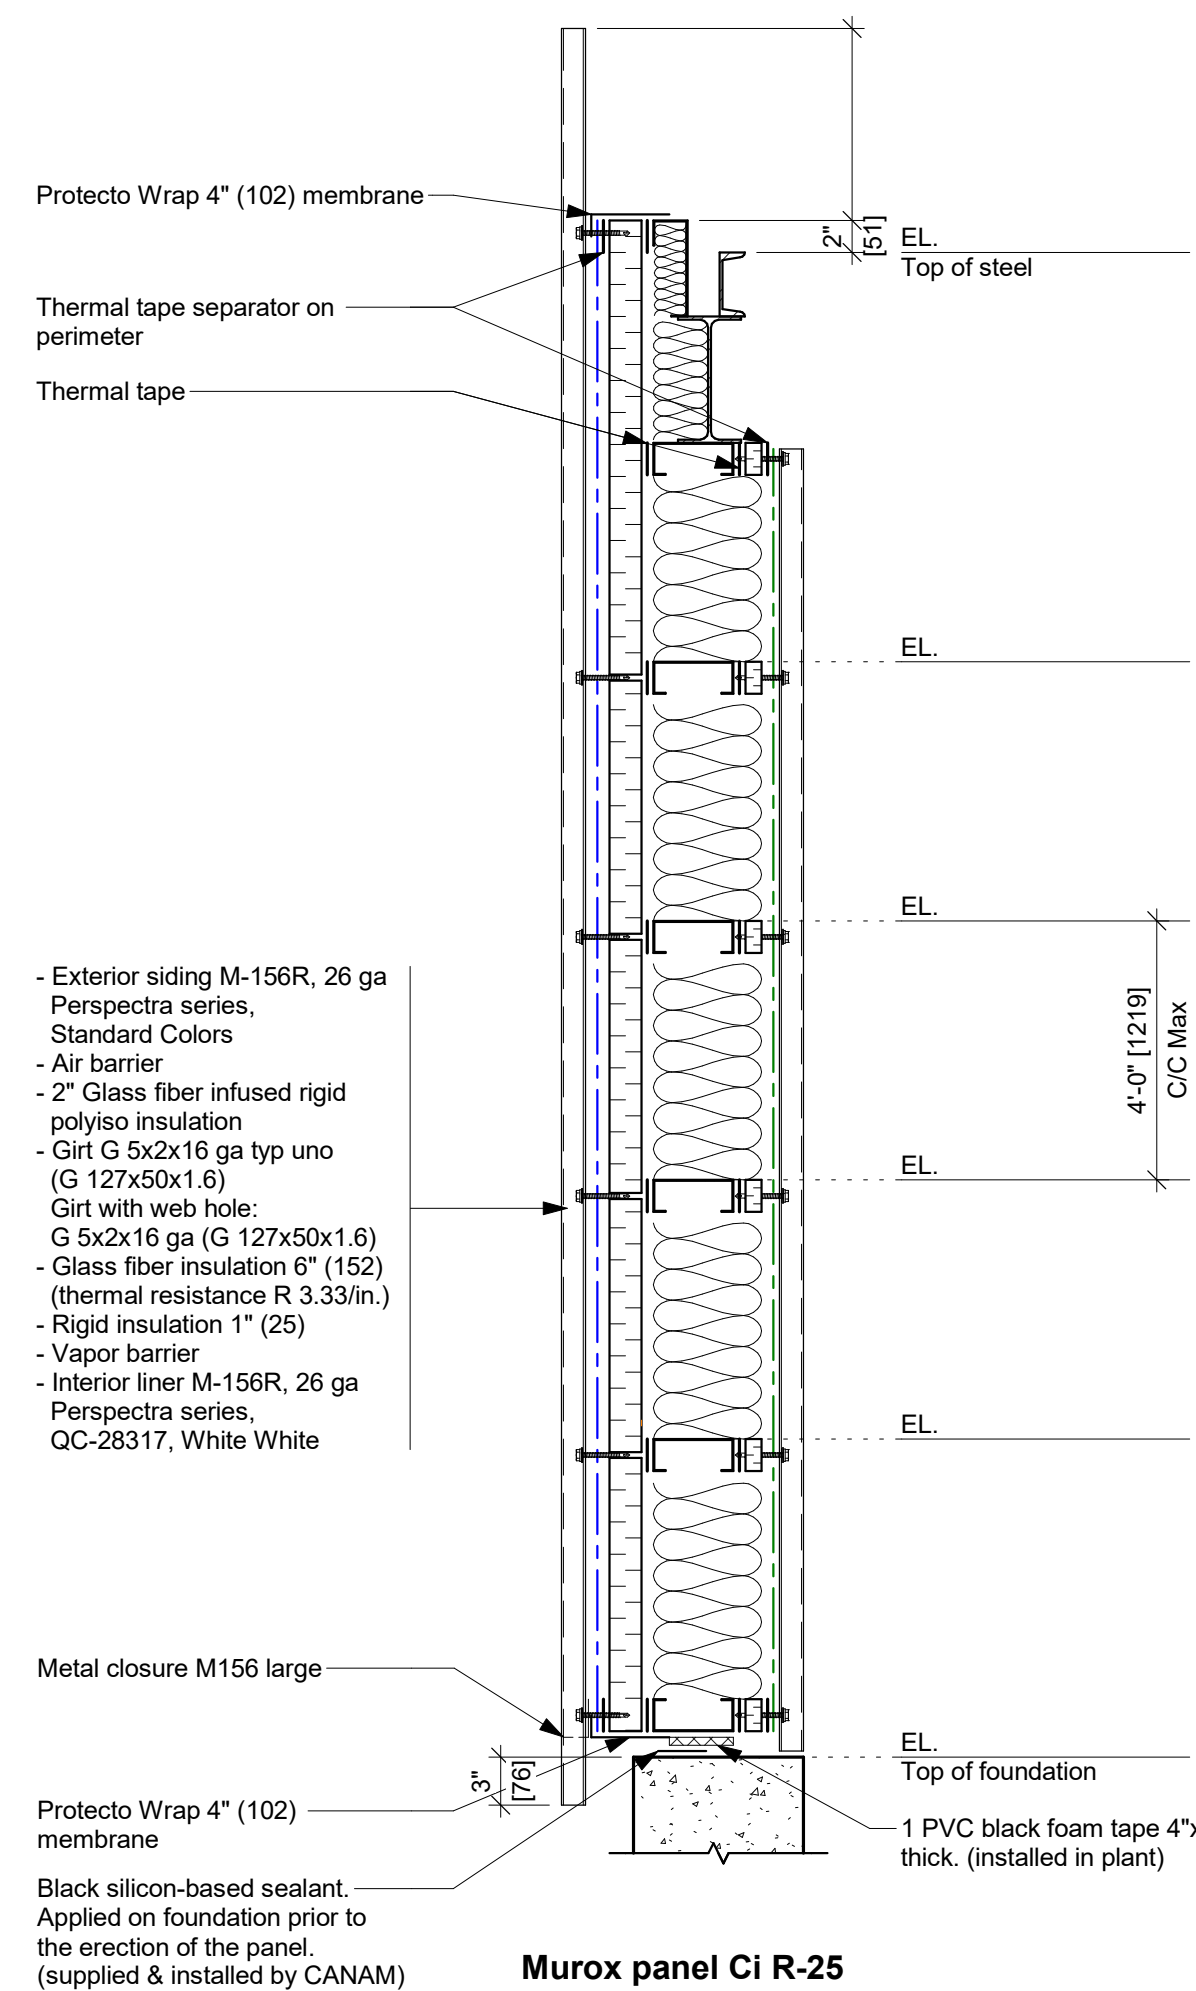
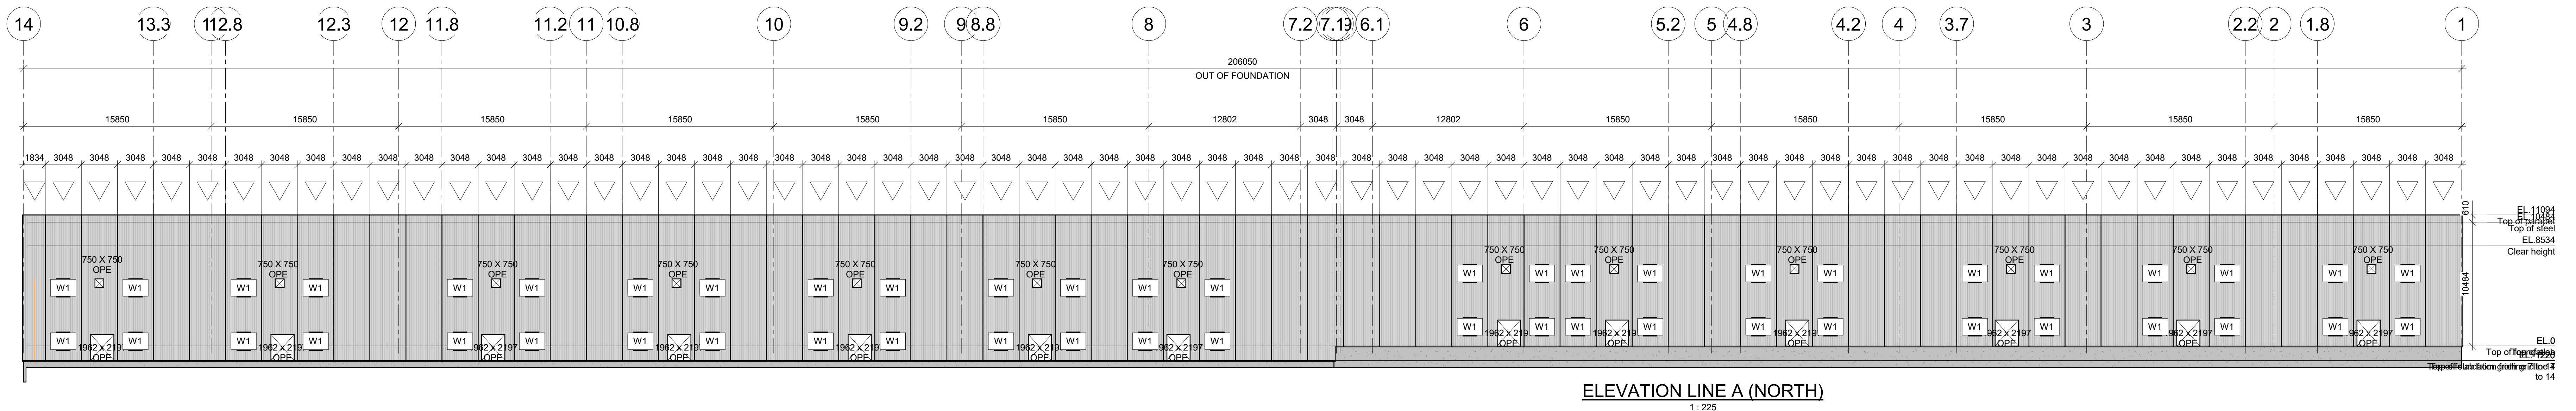
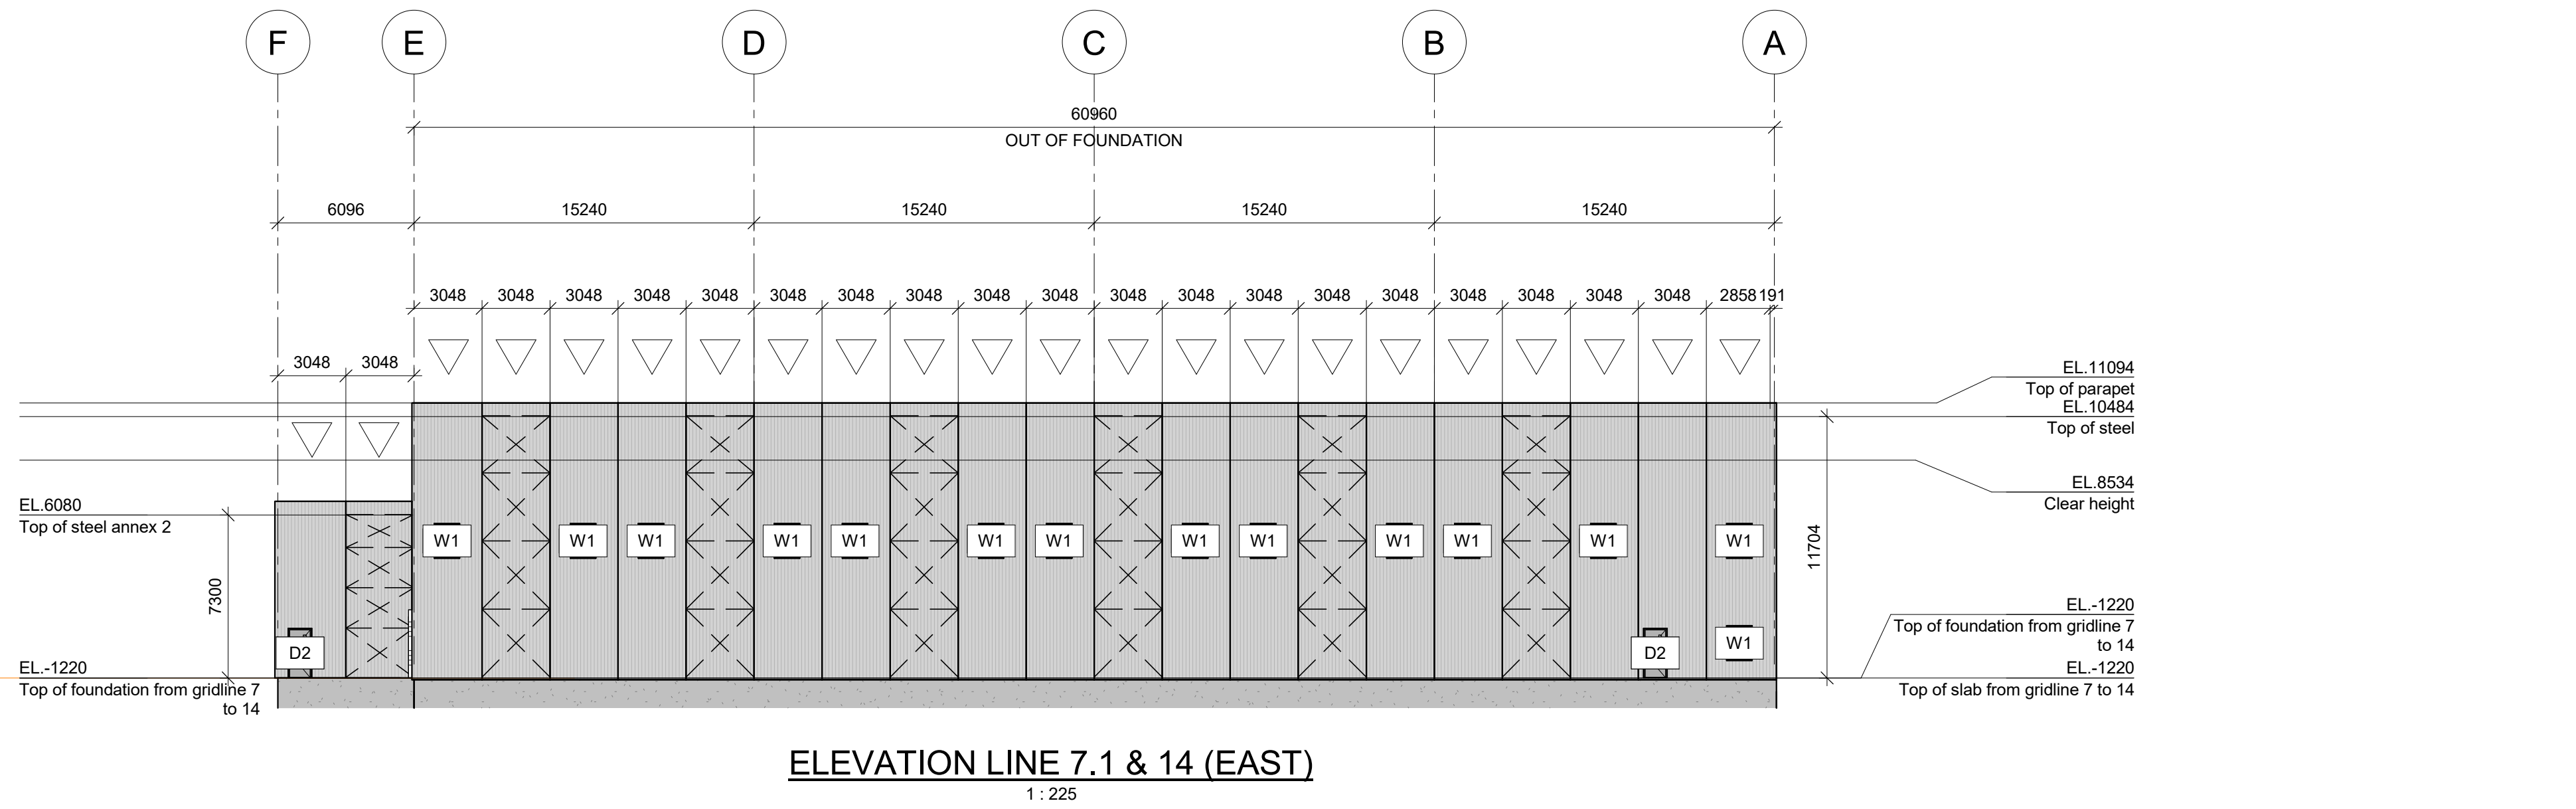
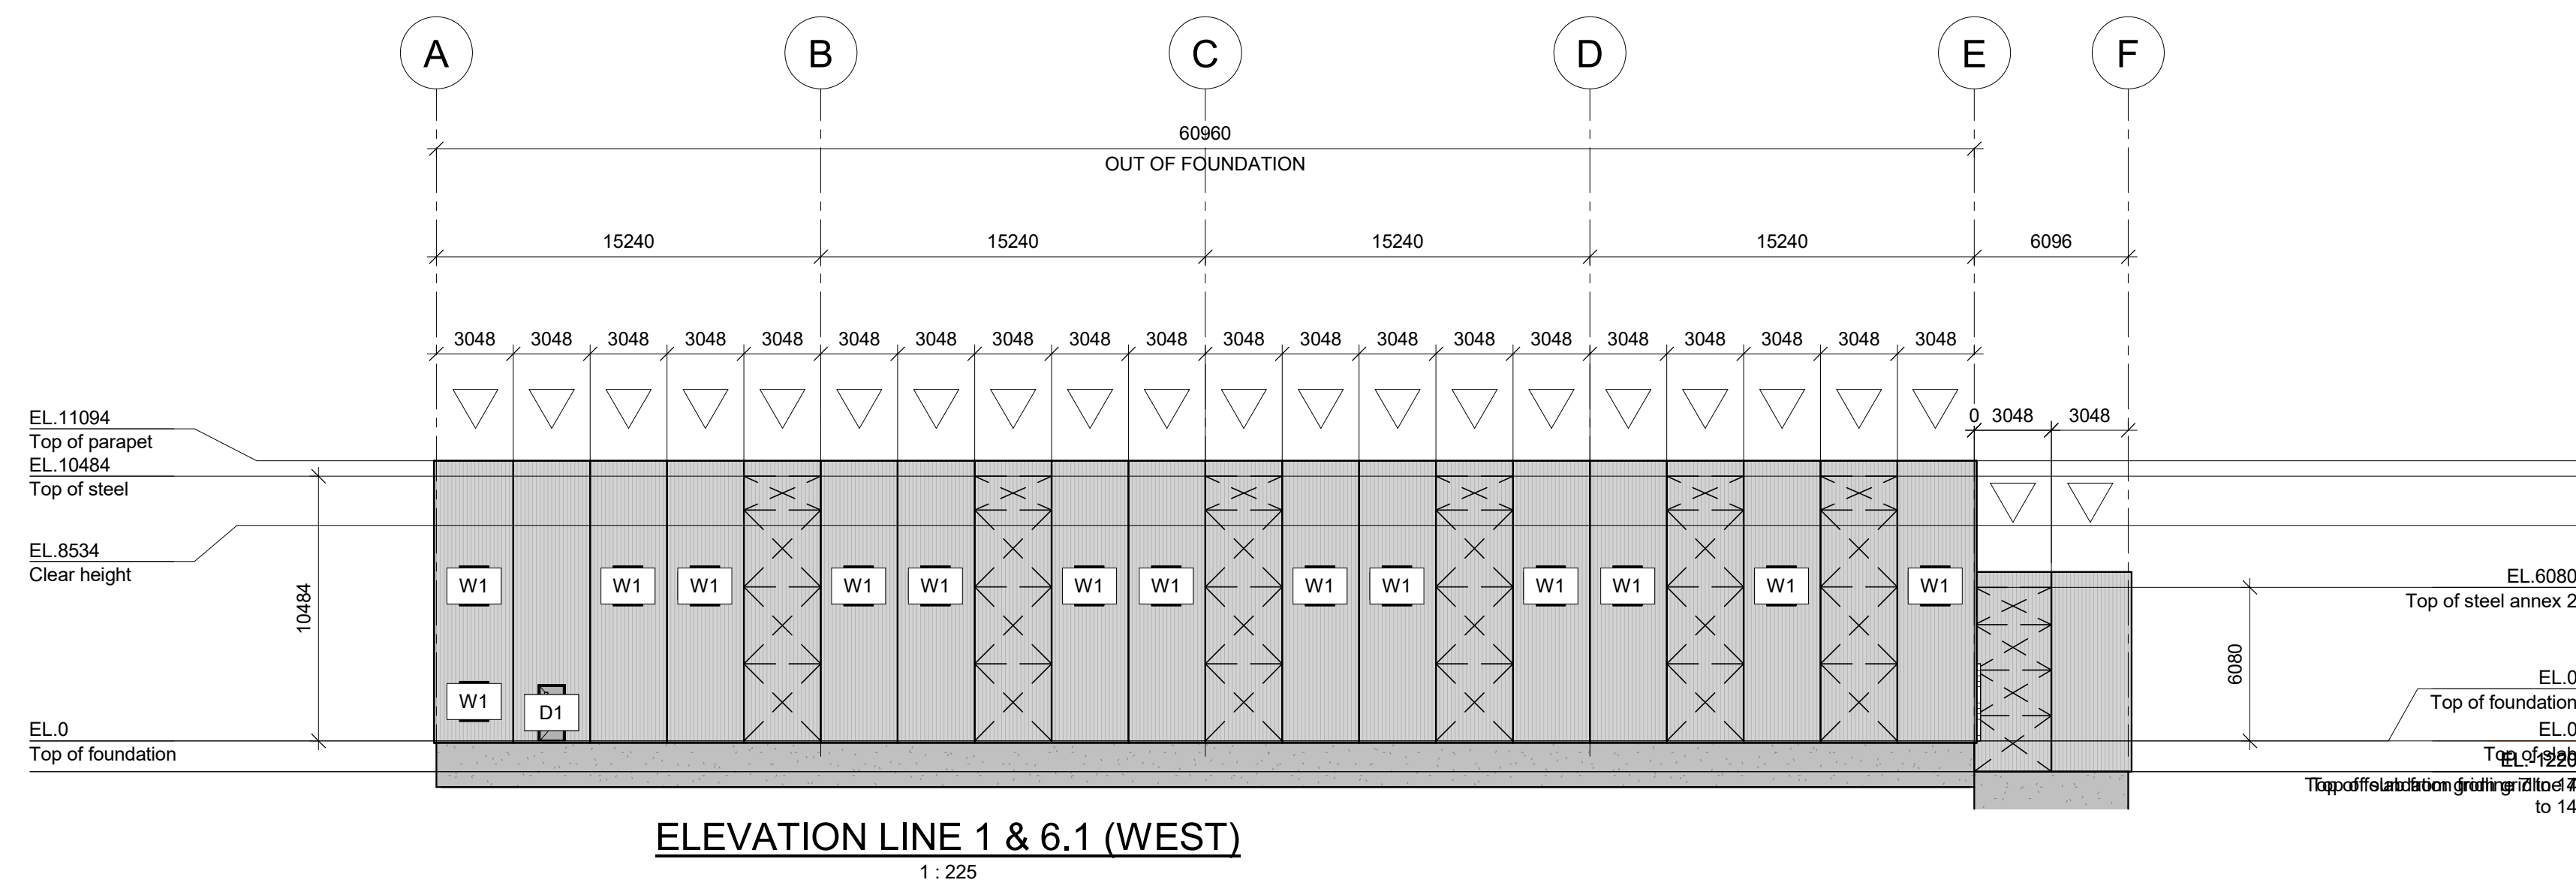


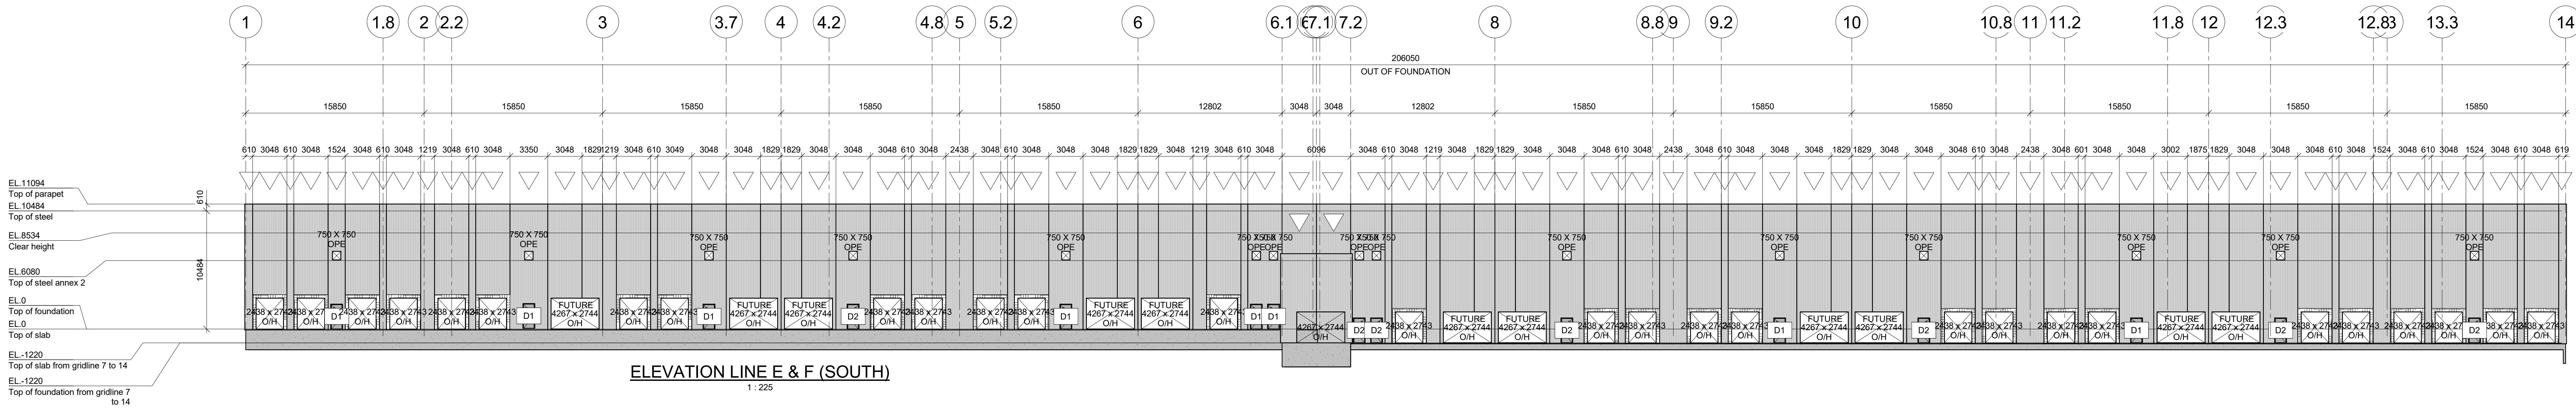

WINDOW SCHEDULE					
Identity	Qty	Installation	Description	Sizes (Ext. of frame) (width x height)	Frame color
W1	60		Fixed aluminium window with thermal break and sealed glass + Low-E argon clear	1105 x 1524	Aluminum Frame (no color)

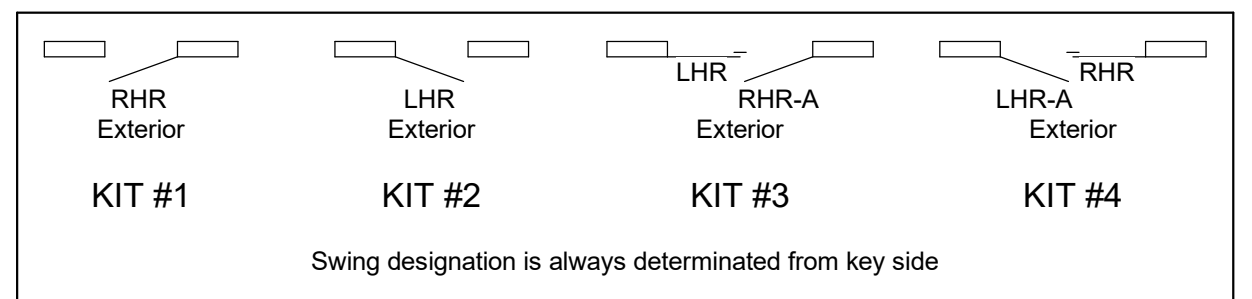

DOOR SCHEDULE													
Door 18 ga.				Glass				Hardware					
Identity	Qty	Installation	Insulation (R12)	Dimensions	Swing side	Width	Height	Steel frame 16 ga. with thermal break	(3) Hinges non-rising removable pin	Door lock & latch set	Panic bar without outside trim Z2EO	Panic bar with outside trim 230L	Surface bolt inactive door
D1	9			914 x 2134	127	127	508						
D2	9			914 x 2134	127	127	508						