



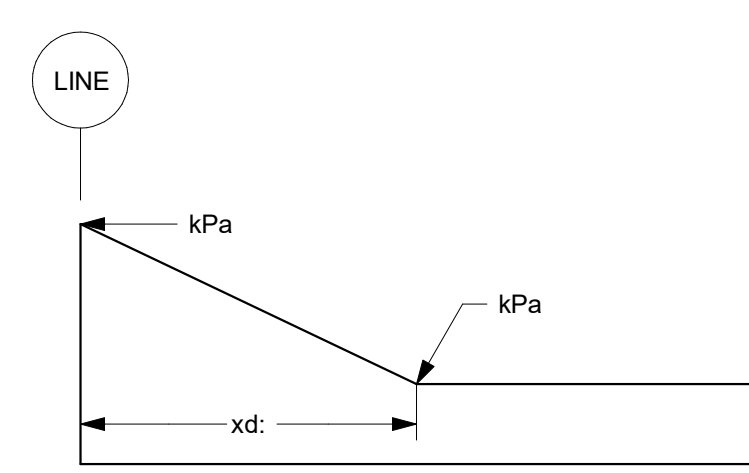

### SNOW LOAD ACCUMULATION

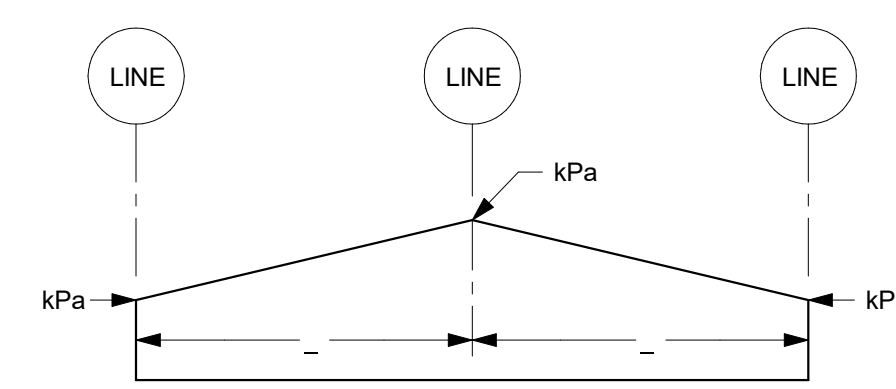


### RAIN LOAD + ADDITIONAL LIVE LOAD




ZONE 1 : -0.86 kPa  
ZONE 2 : -1.07 kPa  
a : 4700 mm

### GROSS UPLIFT DIAGRAM (UNFACTORED)

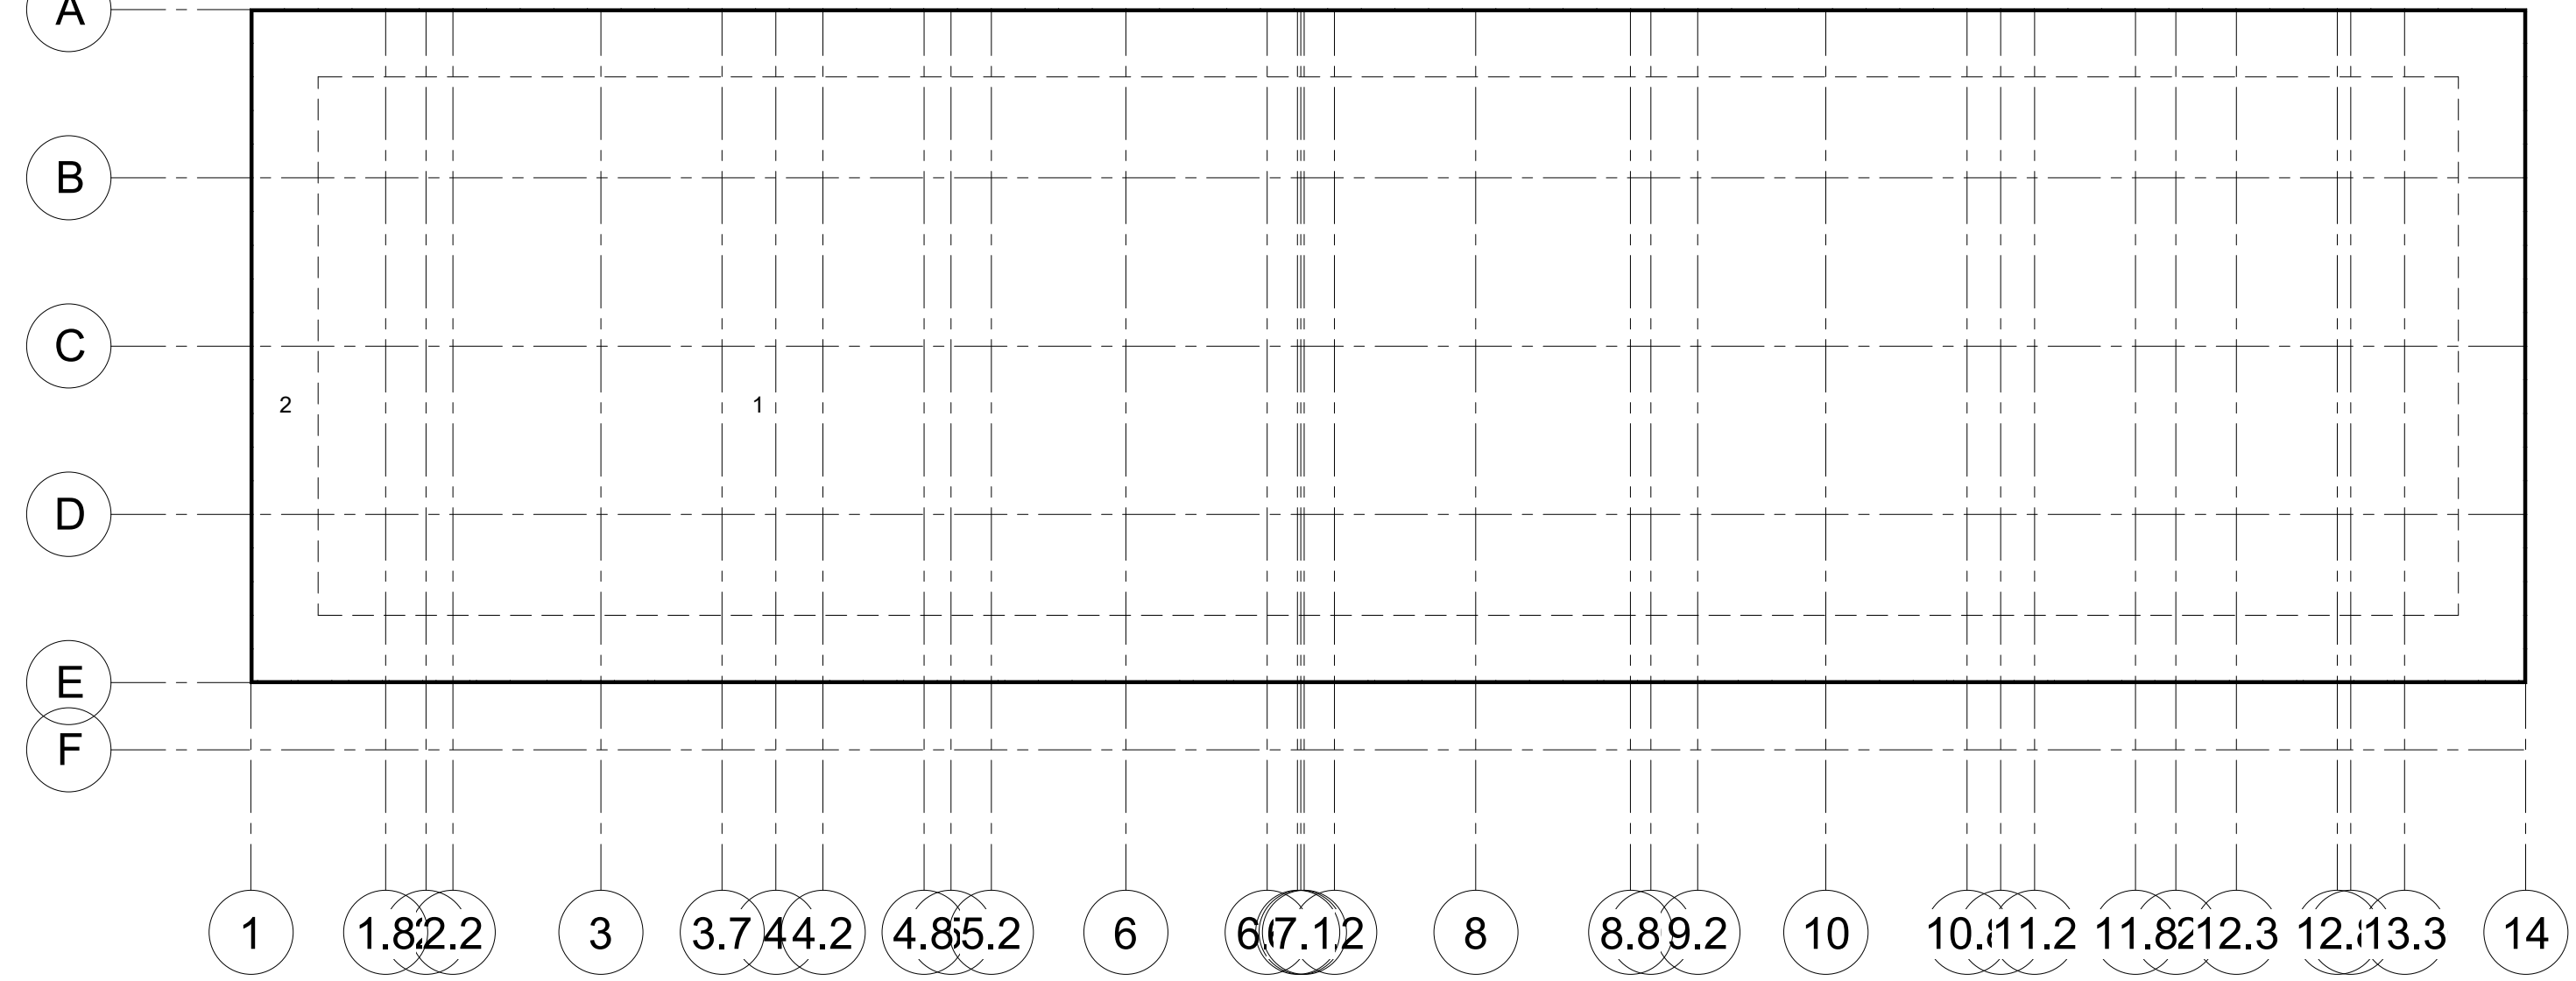

POSITIVE WIND PRESSURE  
(UNFACTORED) : +0.46 psf

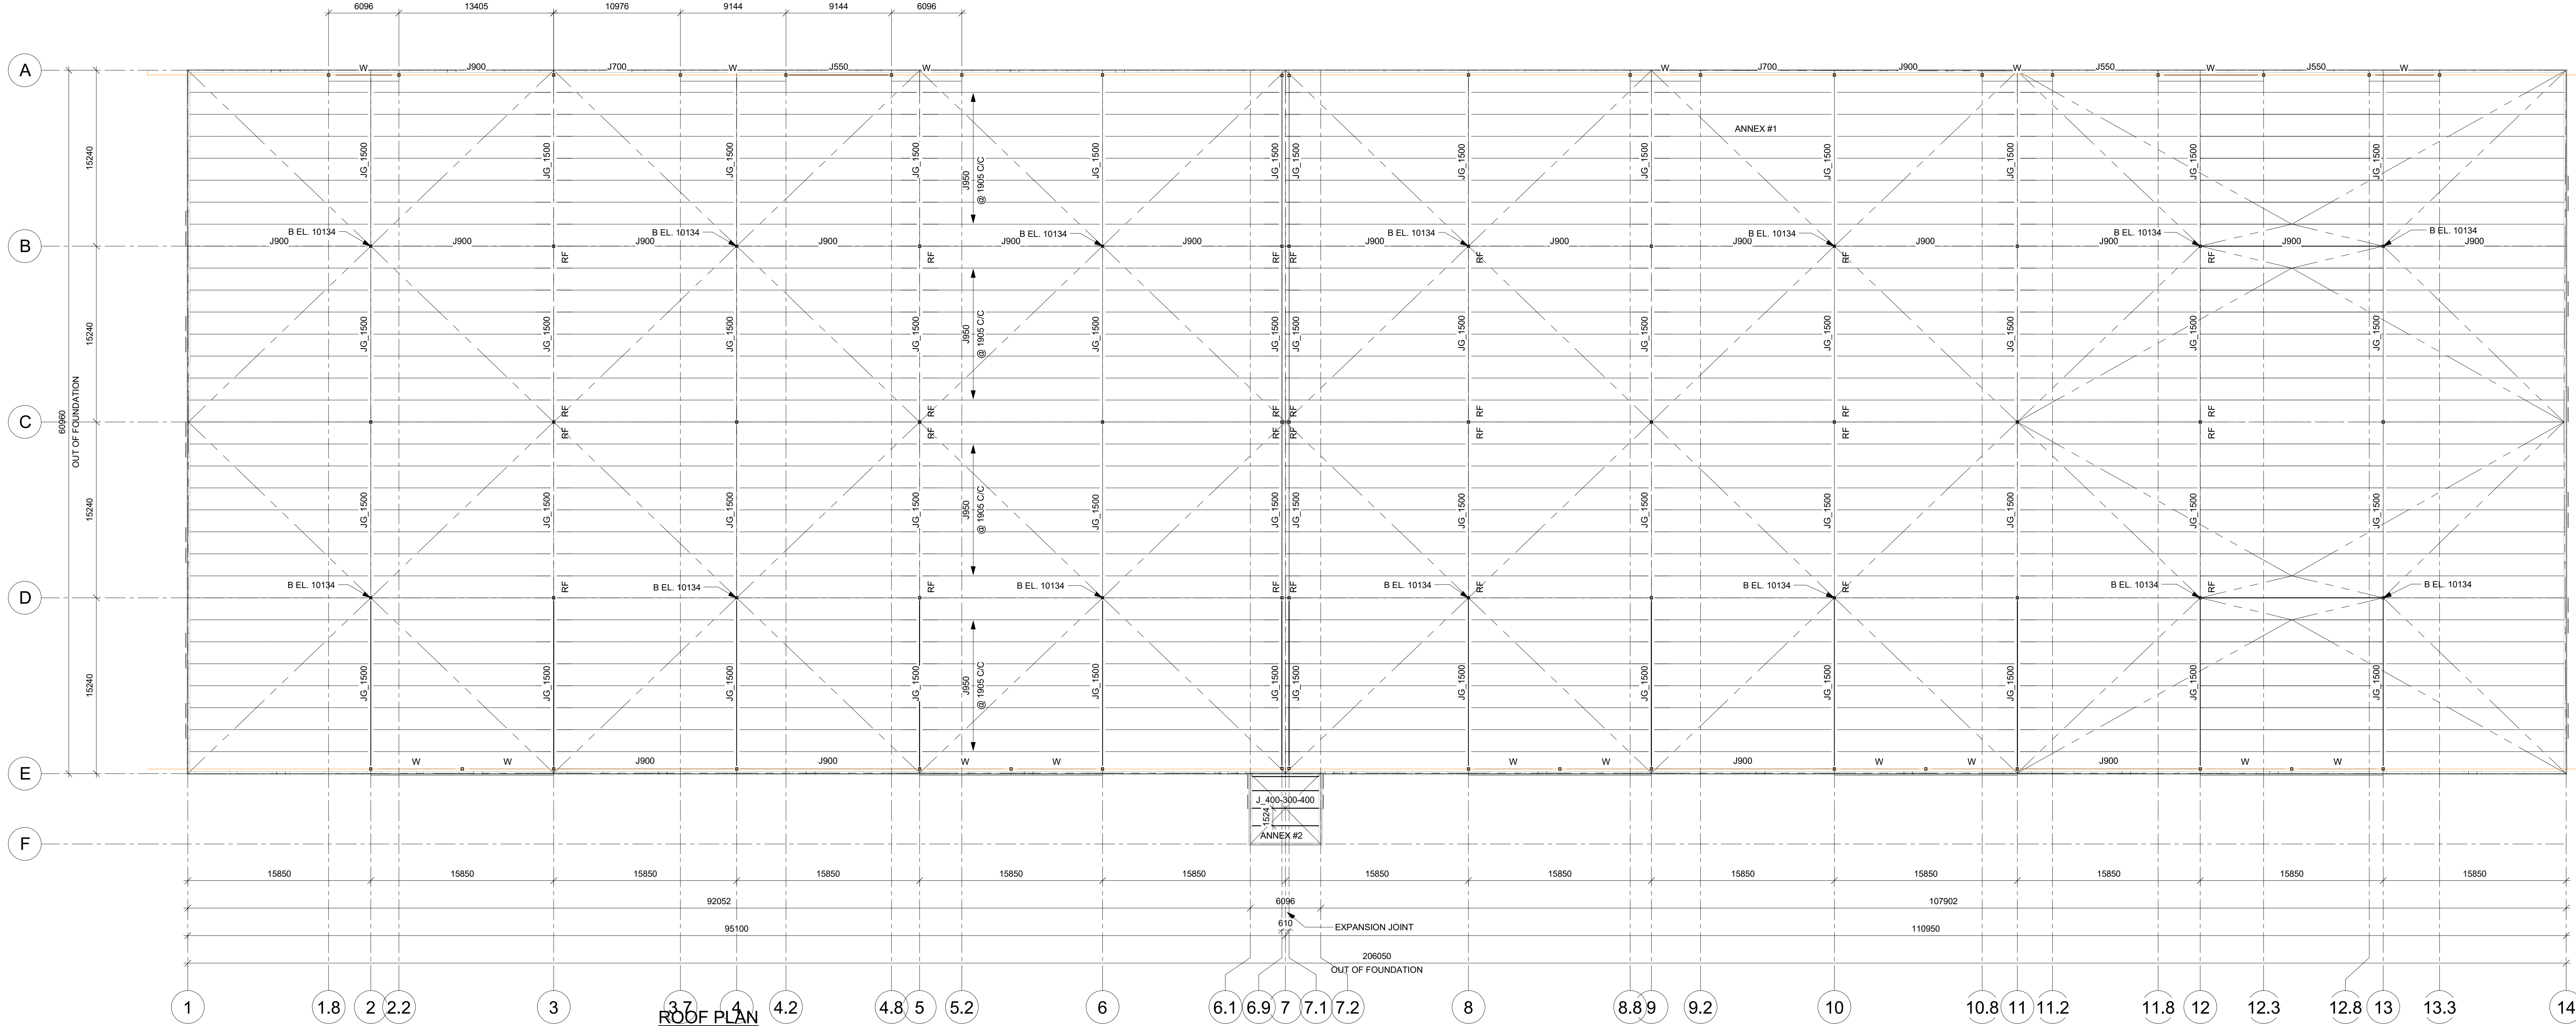

ROOF PLAN

1 - 225

### CONTRACTOR/RECTOR NOTE:

IT IS PROHIBITED TO MODIFY, COPY, REPRODUCE OR OTHERWISE DISTRIBUTE THIS DRAWING OR ANY REPRESENTATION OF THIS DRAWING ON ANY MEDIA, INCLUDING ELECTRONIC, WITHOUT THE PRIOR WRITTEN APPROVAL OF CANAM GROUP INC.

### ROOF

TOP OF PLASTER RWL : -600  
TOP OF PLASTER : -500  
TOP OF SLAB : 0  
CLEAR HEIGHT : 6834  
TOP OF STEEL : 10484  
PARAPET HEIGHT : 610  
TOP OF PARAPET : 11094

### ANNEX #1

TOP OF PLASTER RWL : -1820  
TOP OF PLASTER : -1520  
TOP OF SLAB : -1220  
TOP OF FOUNDATION : -1220  
CLEAR HEIGHT : 9754  
TOP OF STEEL : 10484  
PARAPET HEIGHT : 610  
TOP OF PARAPET : 11094

### ANNEX #2

TOP OF PLASTER RWL : -1820  
TOP OF PLASTER : -1520  
TOP OF SLAB : -1220  
TOP OF FOUNDATION : -1220  
CLEAR HEIGHT : 6900  
TOP OF STEEL : 6900  
PARAPET HEIGHT : 610  
TOP OF PARAPET : 6900

### LOADS

D.L. : 0.72 kPa  
C.O.L. : 0.24 kPa  
S<sub>a</sub> : 2.4 kPa  
S<sub>v</sub> : 0.4 kPa  
C<sub>b</sub> x C<sub>w</sub> : 0.86  
Roof L.L. : 1.0  
Roof snow load : 2.46 kPa  
I<sub>v</sub> : 1.0  
Wind q<sub>t</sub> 1/50 : 0.41 kPa

Seismic (Site class: D (Assumed))

I<sub>e</sub> : 1.0  
S<sub>a</sub>(0.2) : 0.739  
S<sub>a</sub>(0.5) : 0.550  
S<sub>a</sub>(1.0) : 0.326  
S<sub>a</sub>(2.0) : 0.154  
S<sub>a</sub>(5.0) : 0.043  
S<sub>a</sub>(10.0) : 0.013  
PGA : 0.444  
PGV : 0.389

• Code Applicable : National building Code of Canada  
Quebec Building Code, latest adopted editions  
Code of Standard Practice CISC.

• Assumed soil site class: D

### NOTE:

1. If, however, the seismic site class is determined to be E or F according to the geotechnical report, the preliminary structural concept (location and geometry of bracings, etc.) must be validated and coordinated by a Canam's engineer.

PRELIMINARY

NOT TO BE USED FOR CONSTRUCTION

| REVISION | DATE | DESCRIPTION | DESIGN | VER |
|----------|------|-------------|--------|-----|
| 1        |      |             |        |     |
| 2        |      |             |        |     |
**CANAM**  
11505, 1<sup>re</sup> Avenue, bureau 500, Saint-Georges Beauce  
Châteauguay, Québec, G5Y 7Y3  
Phone : (418) 228-8031  
Toll free : (877) 499-6049  
www.canam.com

PROFESSIONAL SEAL

PROJECT

Vars Development BLDG 1  
Vars, On

DRAWING TITLE

PRELIMINARY SKETCH - ROOF PLAN

| CONTRACT NUMBER | DRAWING NUMBER | DIVISION | REVISION |
|-----------------|----------------|----------|----------|
| P2026-021       | EsMx401        |          |          |

Initials