
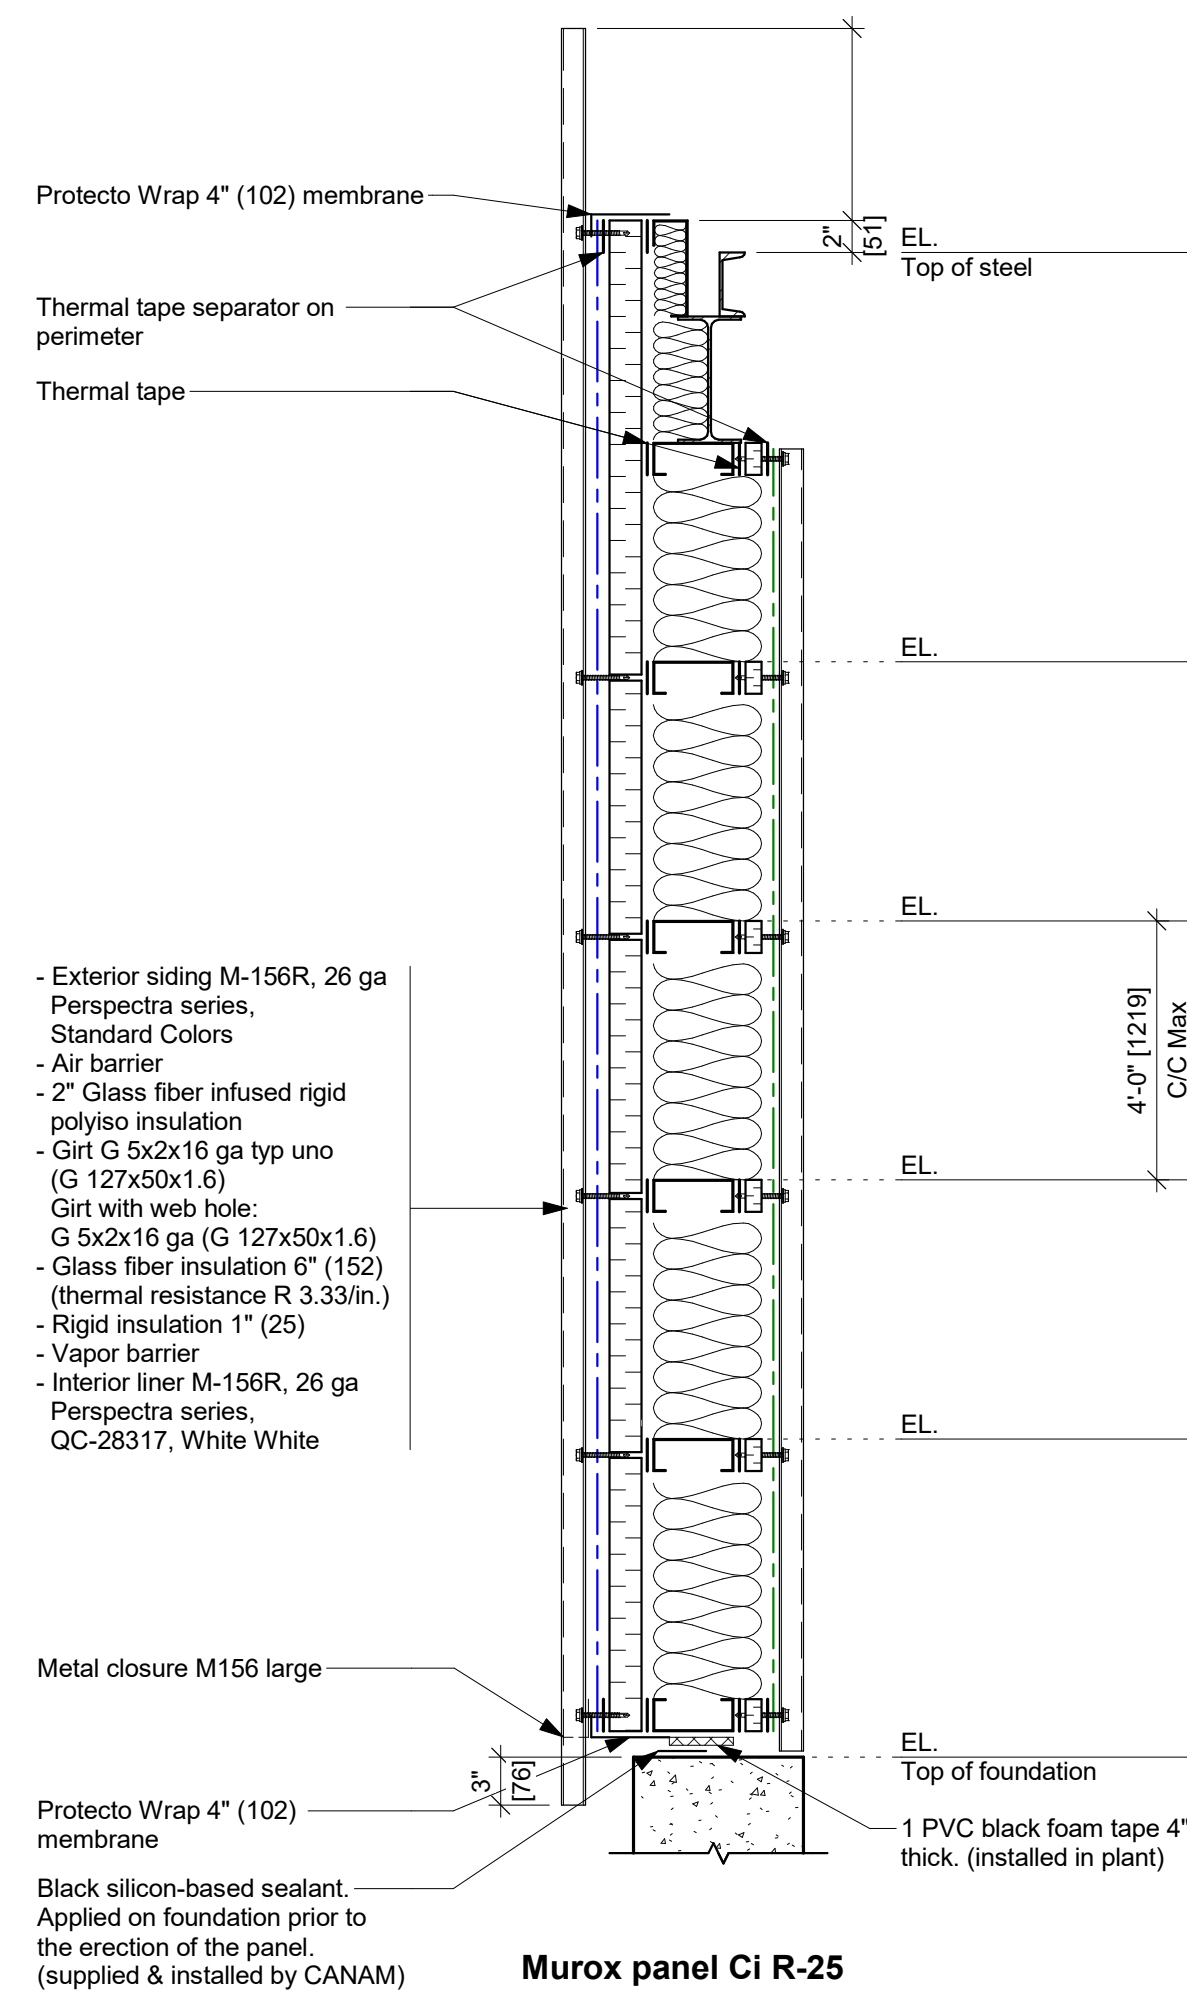
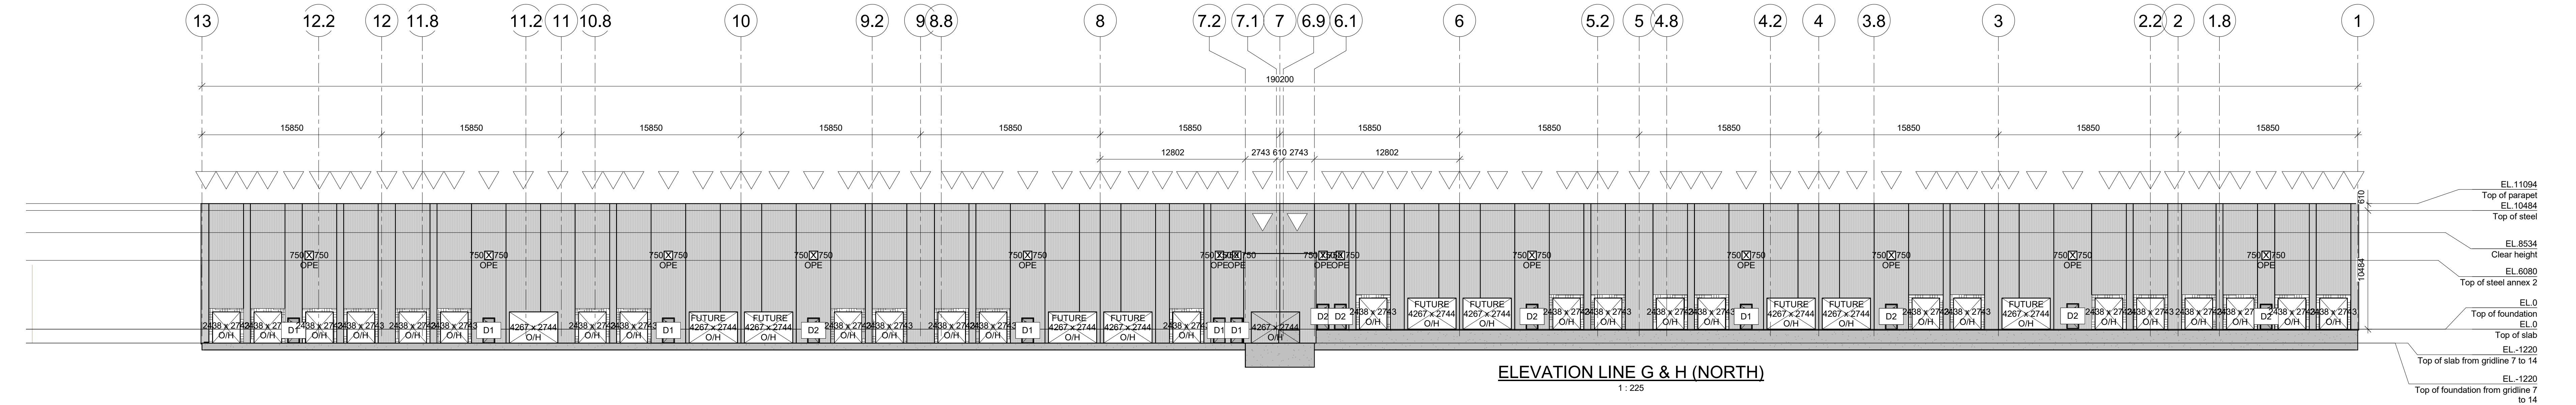
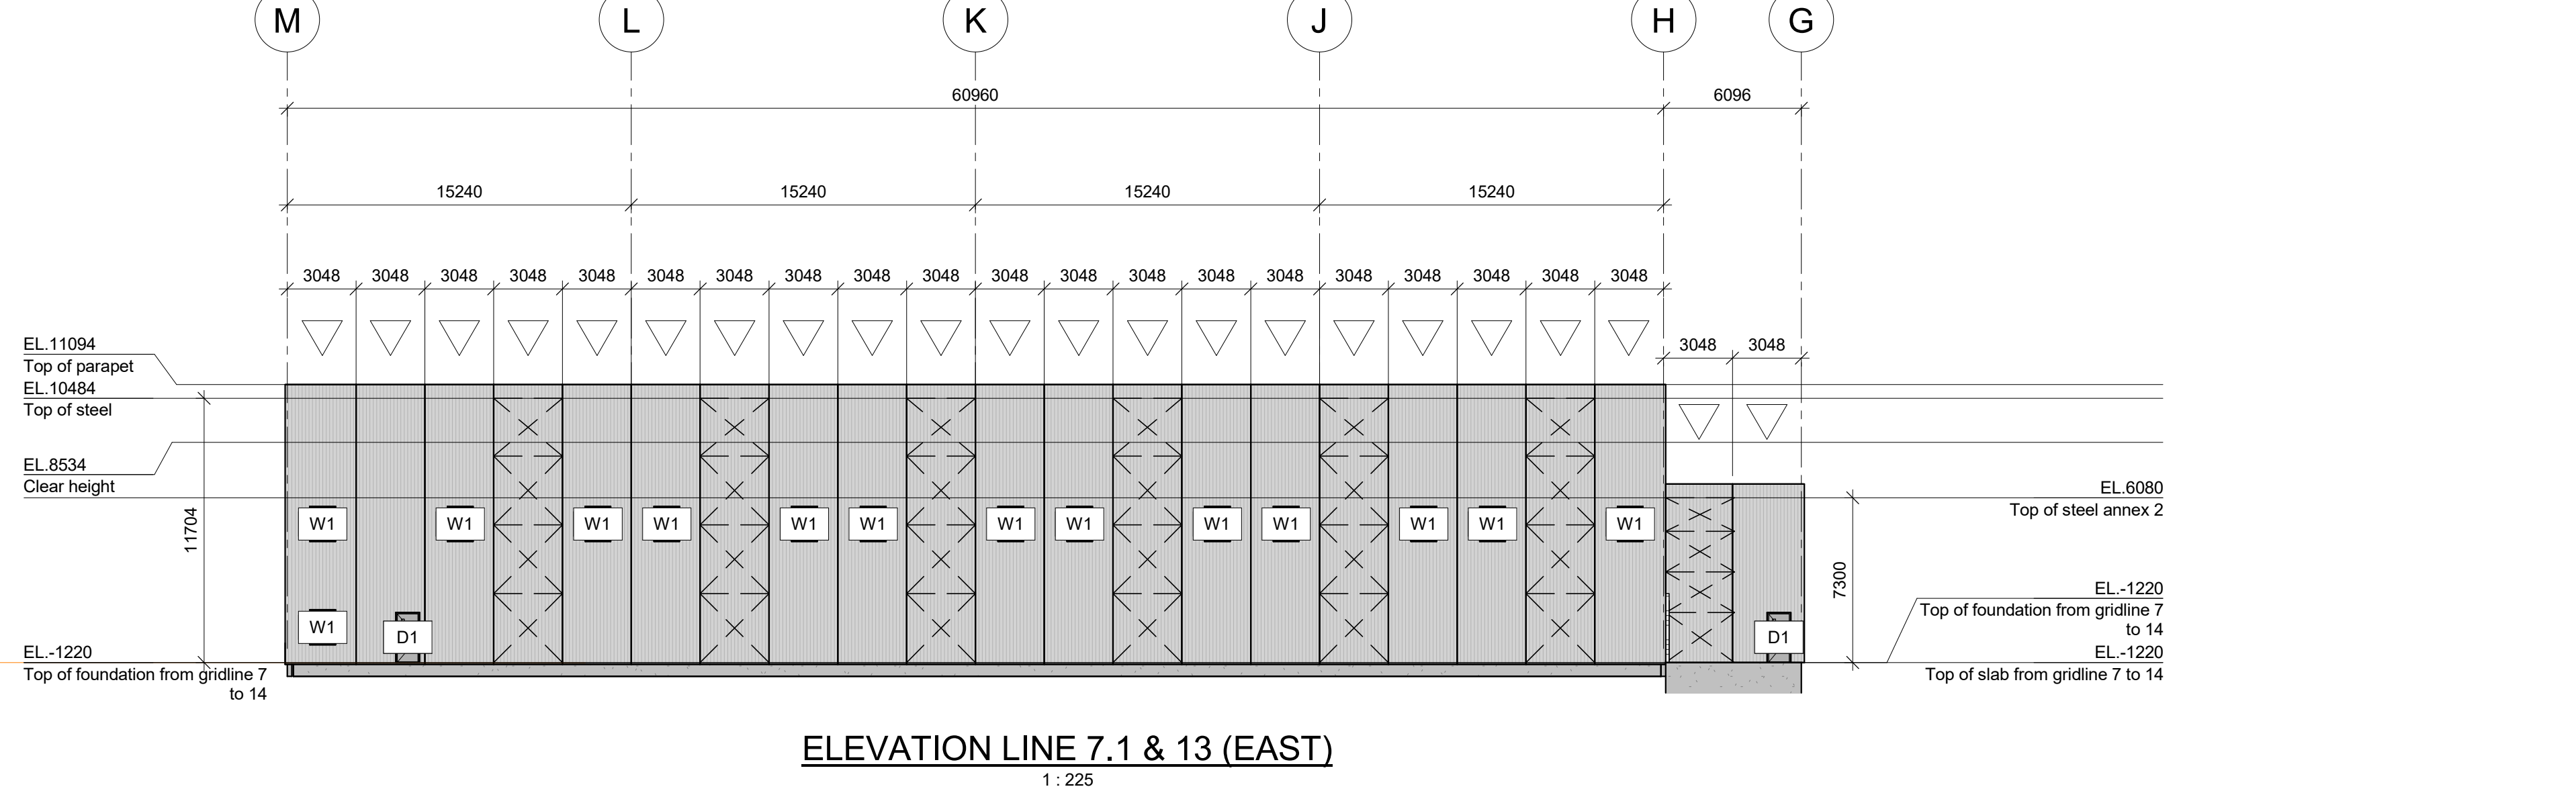
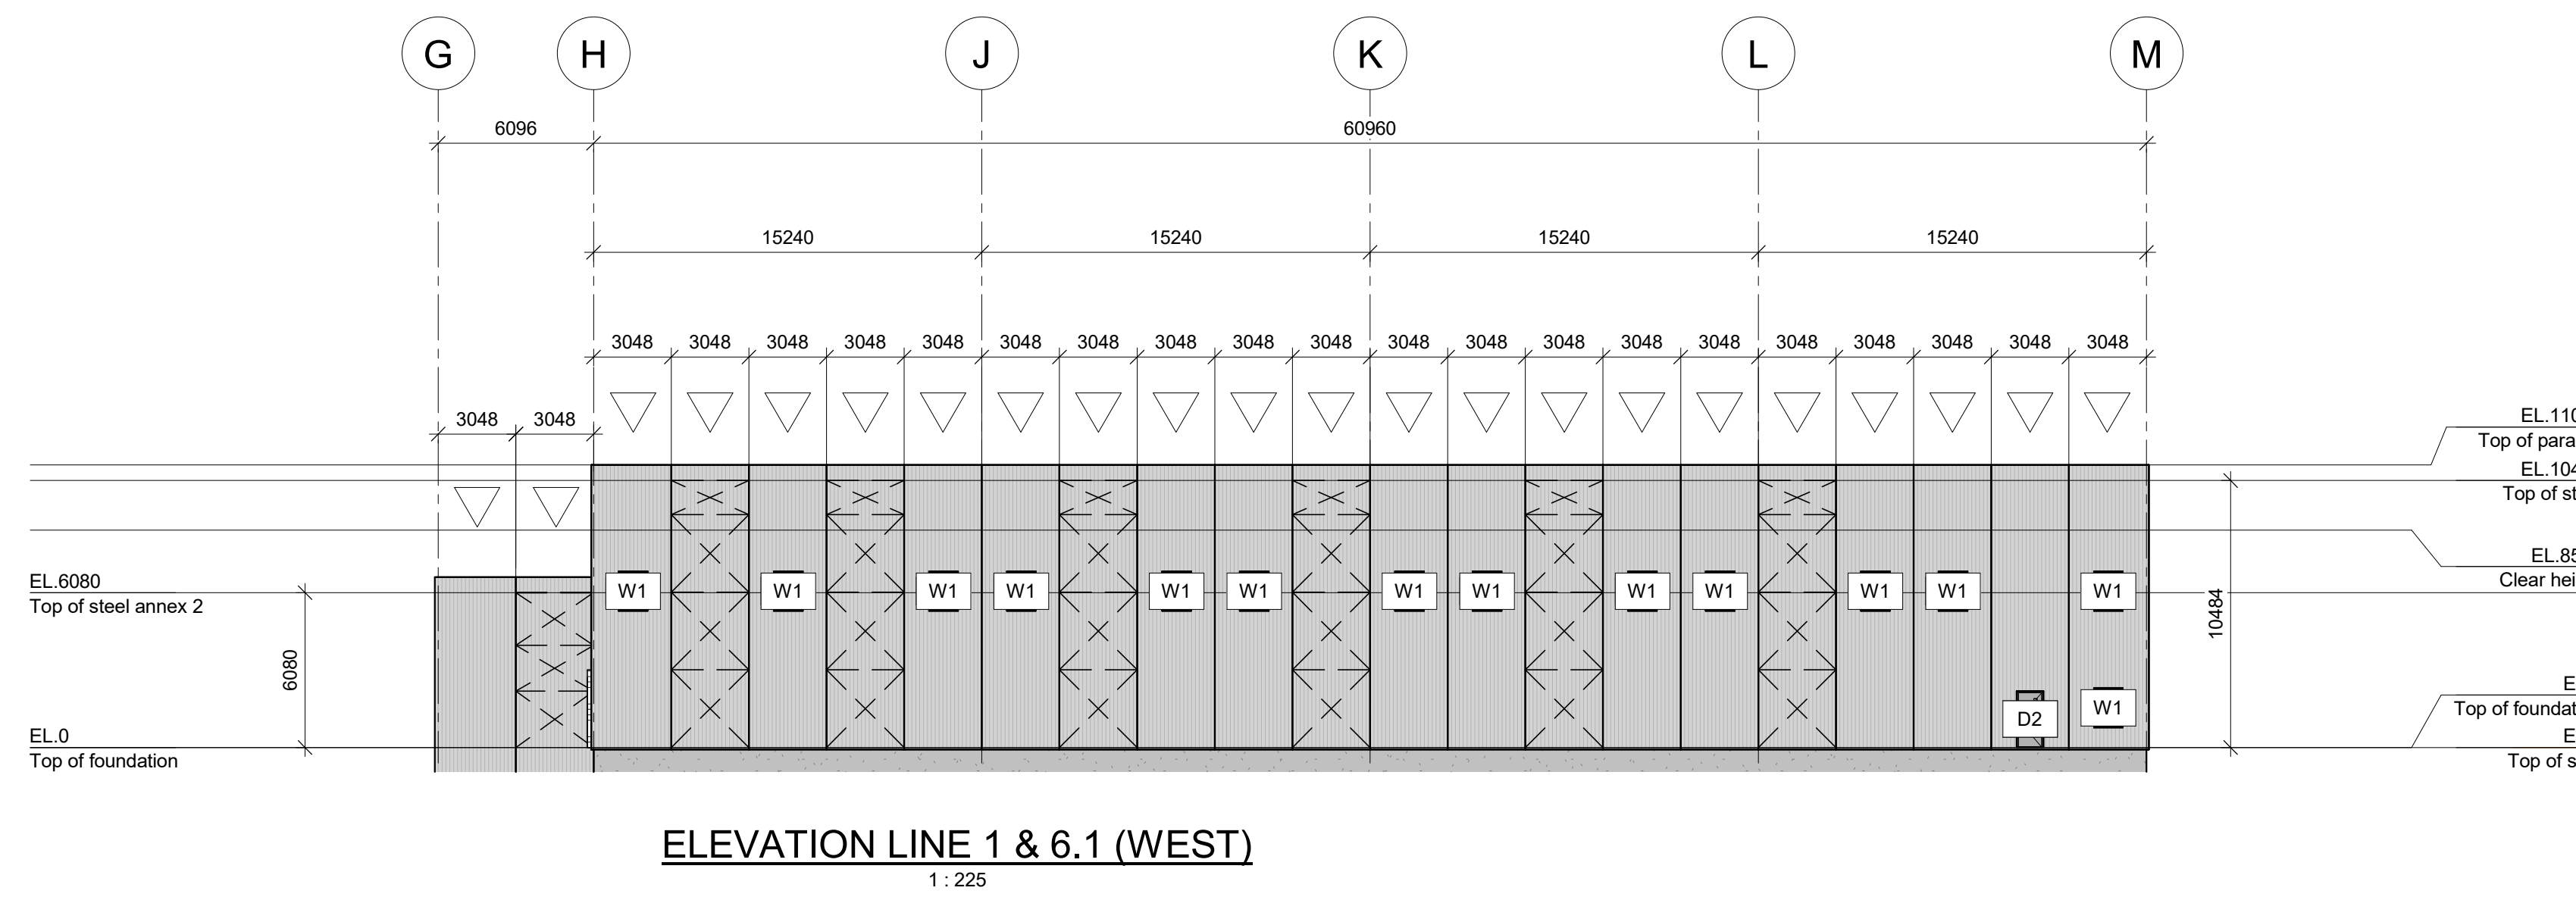


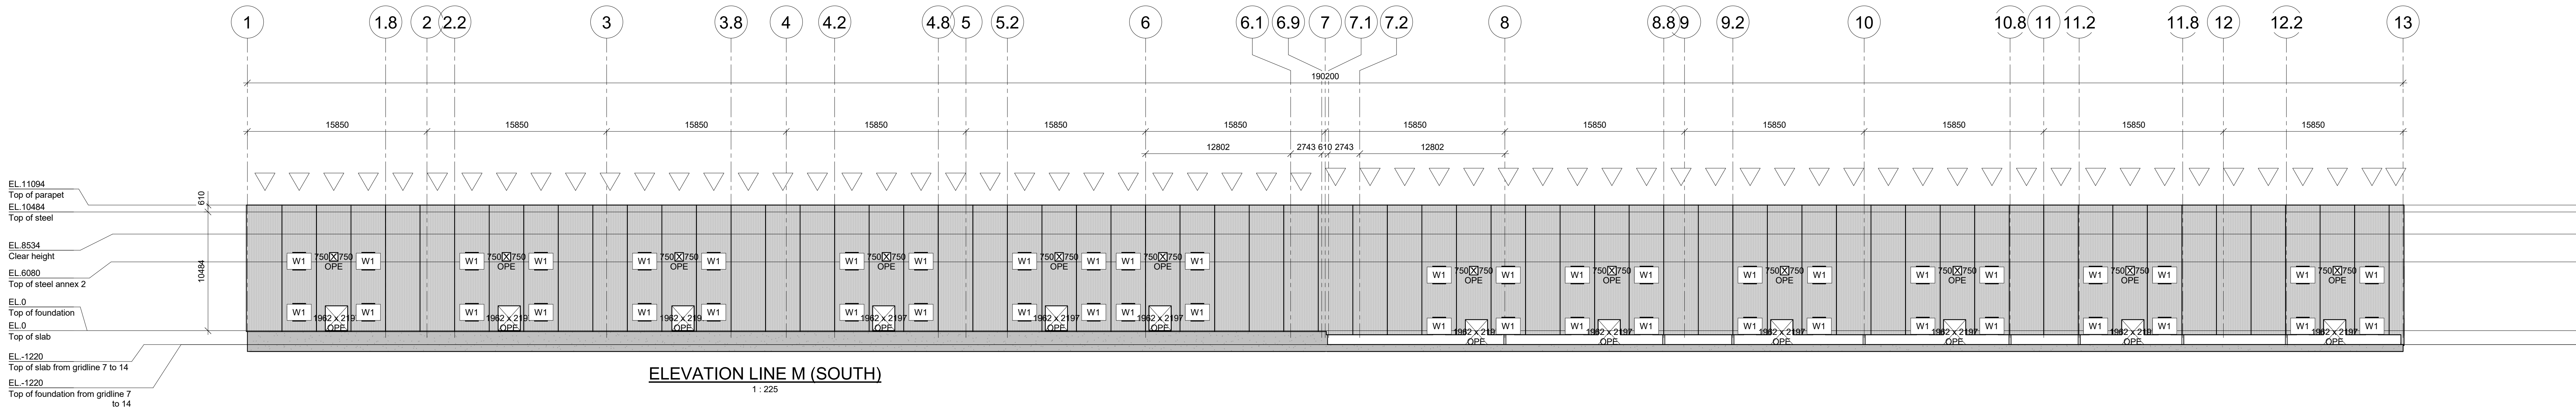

WINDOW SCHEDULE					
Identity	Qty	Installation	Description	Sizes (Ext. of frame) (width & height)	Frame color
W1	76		Fixed aluminum window with thermal break and sealed glass + Low-E argon clear	1105 x 1524	Aluminum Frame (no color)

Identity	Qty	Installation	Description	Sizes (Ext. of frame) (width & height)	Frame color
KIT #1	9		RHR Exterior	1105 x 1524	Aluminum Frame (no color)
KIT #2	8		LHR Exterior	1105 x 1524	Aluminum Frame (no color)
KIT #3	8		LHR-A Exterior	1105 x 1524	Aluminum Frame (no color)
KIT #4	8		RHR Exterior	1105 x 1524	Aluminum Frame (no color)

Supplier's standard hardware:

- Hinges : Stanley FBB179 4.5" x 4"
- Exit device : Von Dupon 22 x 689 with outside trim 230L
- Permanent cylinder : Schlage 0001C 626
- Door closure : LCN 1261 669
- Head and jamb seal : Unique 1650
- Bottom seal : Unique DS4
- Threshold : See the remarks in "Door schedule"

DOOR SCHEDULE													
Door 18 ga.				Glass				Hardware					
Identity	Qty	Installation	Insulation (R12)	Dimensions	Swing side	Width	Height	Steel frame 16 ga. with thermal break	(3) Hinges non-rising removable pin	Door lock & latch set	Panic bar without outside trim Z2EO	Panic bar with outside trim 230L	Astragal for inactive door
D1	9			914 x 2134	127	127	508						
D2	8			914 x 2134	127	127	508						