

CONTRACTOR/ERECTOR NOTE:

IT IS PROHIBITED TO MODIFY, COPY, REPRODUCE OR OTHERWISE DISTRIBUTE THIS DRAWING OR ANY REPRESENTATION OF THIS DRAWING, OR ANY MEDIA, INCLUDING ELECTRONIC, WITHOUT THE PRIOR WRITTEN APPROVAL OF CANAM GROUP INC.

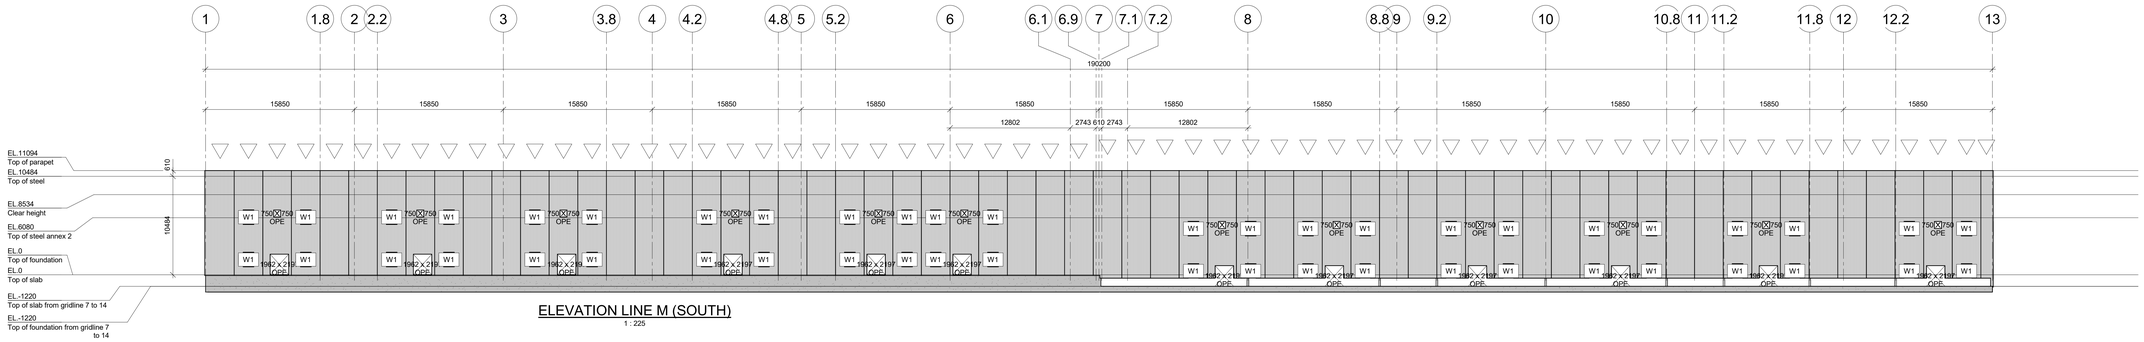


ELEVATION LINE M (SOUTH)

1 : 225

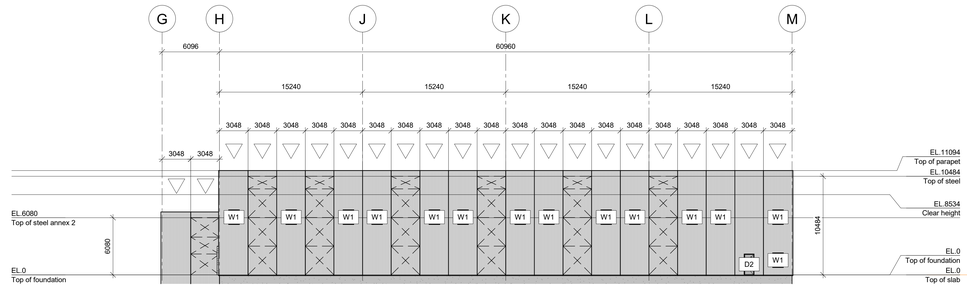


ELEVATION LINE 1 & 6.1 (WEST)

1 : 225

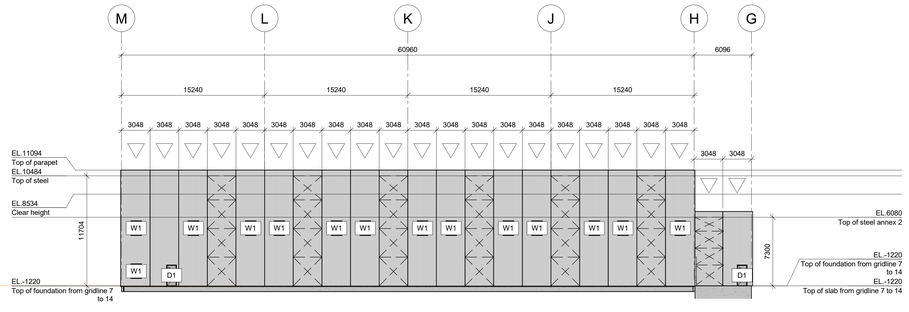


ELEVATION LINE 7.1 & 13 (EAST)

1 : 225

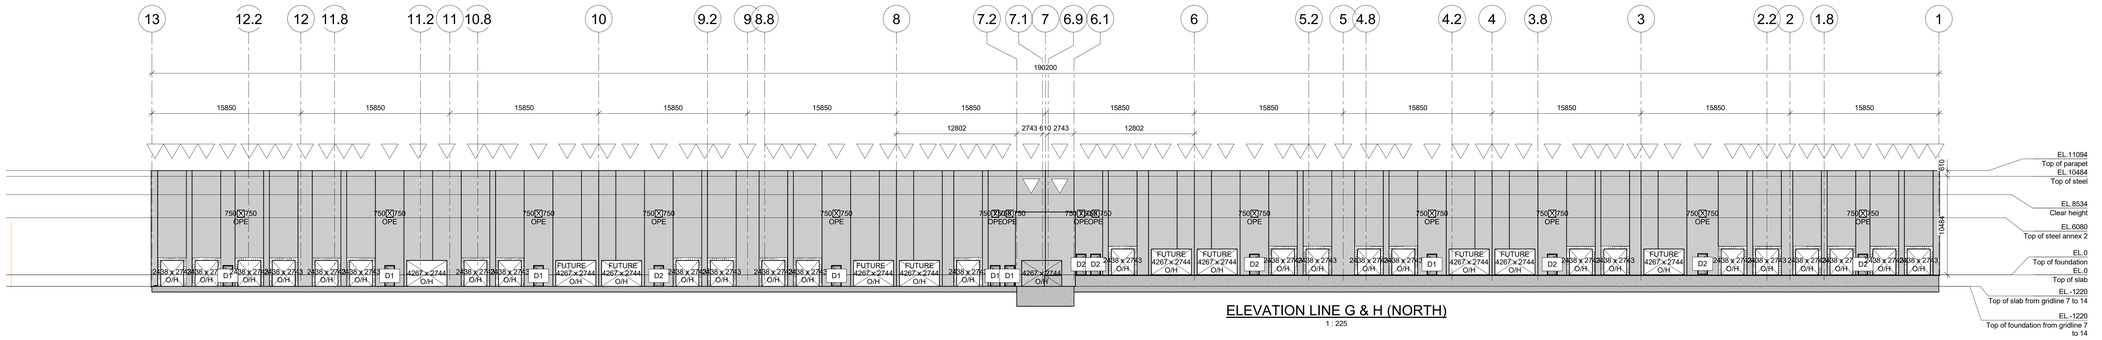

ELEVATION LINE G & H (NORTH)

1 : 225

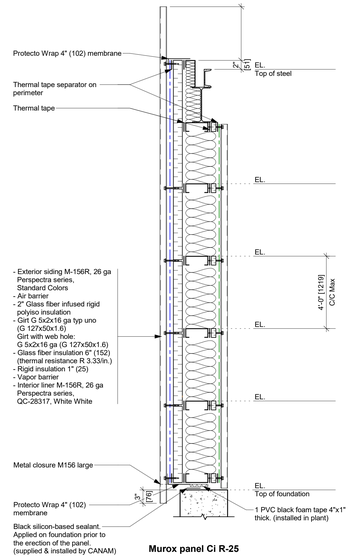

Murox panel Ci R-25

COUPE DE MUR - TYPE

1 : 12

WINDOW SCHEDULE

Identity	Qty.	Installation	Description	Sizes (Ext. of frame) (width & height)	Frame color	Remarks
W1	76		Fixed aluminium window with thermal break and sealed glass + Low-E argon clear	1105 x 1524	Aluminum Frame (no color)	

RHR Exterior — KIT #1
LHR Exterior — KIT #2
LHR RHR-A Exterior — KIT #3
LHR-A RHR Exterior — KIT #4

Swing designation is always determinated from key side

Supplier's standard hardware:
- Hinges : Stanley FBB179 4.5" x 4"
- Exit device : Von Duprin 22 x 689 with outside trim 230L
- Permanent cylinder : Schlage 20001C 626
- Door closure : LCN 1261 689
- Head and jamb seal : Unique 1650
- Bottom seal : Unique DS4
- Threshold : See the remarks in "Door schedule"

DOOR SCHEDULE

		Door 18 ga.				Glass		Hardware												
Identity	Qty.	Installation	Insulation (R12)	Dimensions	Swing side	Width	Height	Steel frame 16 ga. with thermal break	(3) Hinges non-rising removable pin	Door lock & latch set	Panic bar without outside trim 22EO	Panic bar with outside trim 230L	Surface bolt Inactive door	Threshold	Astragal for inactive door	Door closer	Door chain stop	Weatherstrip	Head cap	Remarks
D1	9			914 x 2134		127	508													
D2	8			914 x 2134		127	508													

PRELIMINARY

NOT TO BE USED FOR CONSTRUCTION

REVISION	DATE	DESCRIPTION	DESS.	VER.

PROJECT MANAGER

DRAFTING:

DRAWN	DESIGNED	PROJECT ENGINEER	SCALE:
Donald Piché			Comme indiqué
CHECKED	CONSULTING ENGINEERS / ARCHITECTS		DATE (yyy/mm/dd) : 2026-02-09

CUSTOMER: Megha Holdings Inc.

CANAM
11505, 1re Avenue, bureau 500, Saint-Georges Beauce
Quebec, Canada, G6Y 7X3
Phone : (418) 228-8031
Toll free : (877) 499-6049
www.canam.com

PROFESSIONAL SEAL

PROJECT

Vars Development BLDG 2
Vars, On

DRAWING TITLE

PRELIMINARY SKETCH - ELEVATIONS

CONTRACT NUMBER	DRAWING NUMBER	DIVISION	REVISION
P2026-021	EsMx501		

Initials