



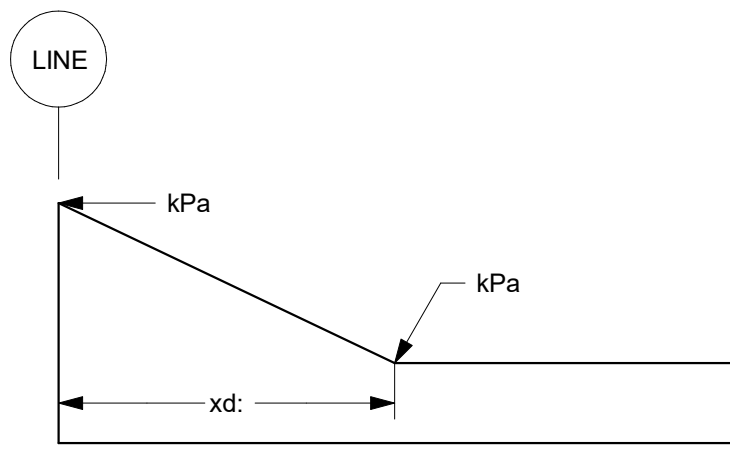

SNOW LOAD ACCUMULATION

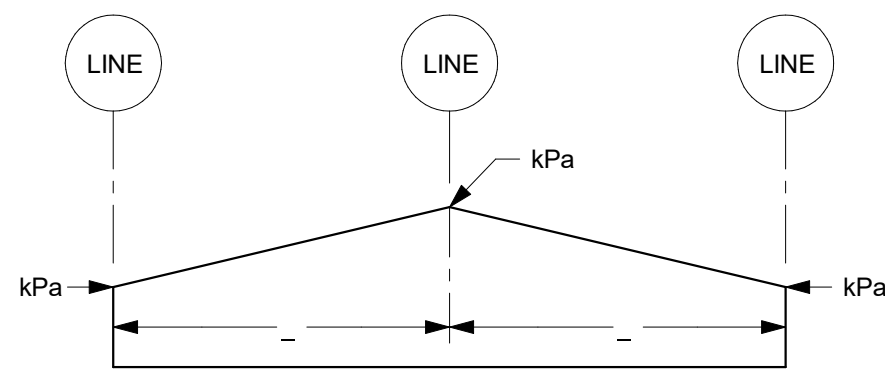


RAIN LOAD + ADDITIONNAL LIVE LOAD



1 1.8 2 2.2 3 3.8 4 4.2 4.8 5 5.2 6 6.1 6.9 7 7.1 7.2 8 8.8 9 9.2 10 10.8 11 11.2 11.8 12 12.2 13


G
H
J
K
L
M

GROSS UPLET DIAGRAM (UNFACTORED):

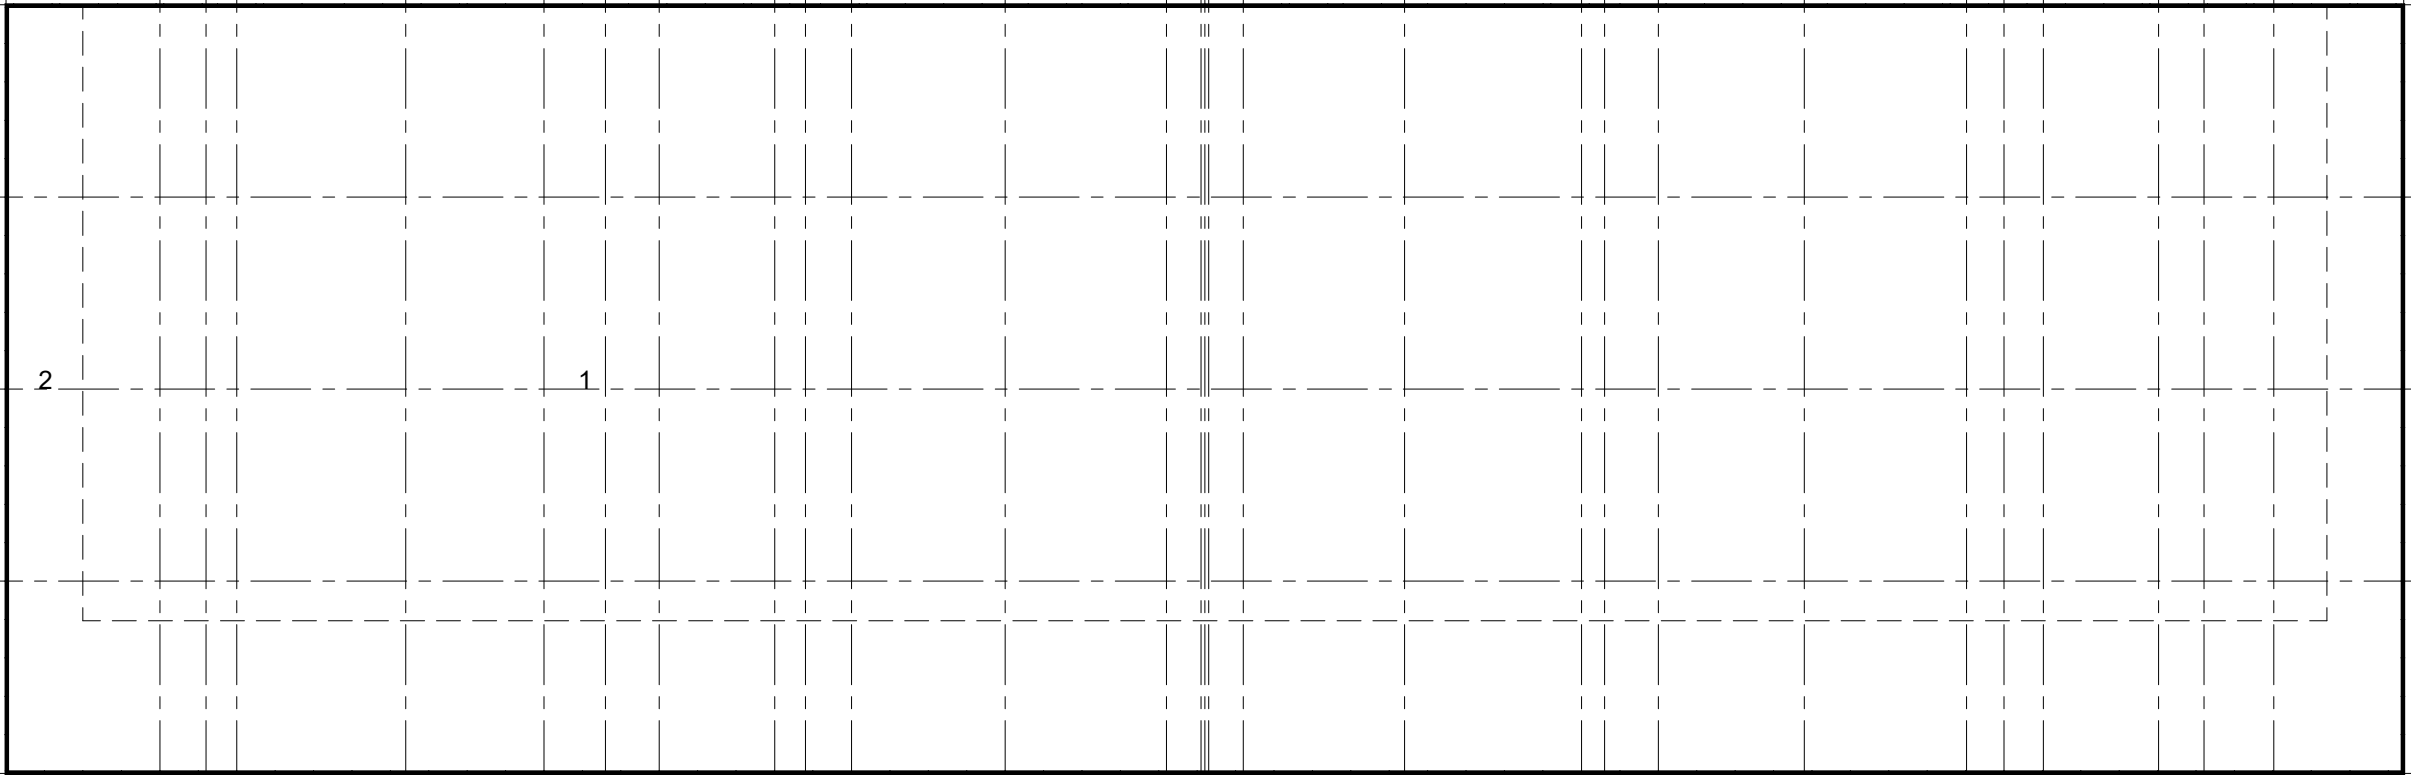

ZONE 1 : -0.88 kPa
ZONE 2 : -1.07 kPa
a : 4700

POSITIVE WIND PRESSURE
(UNFACTORED): +0.46 psf

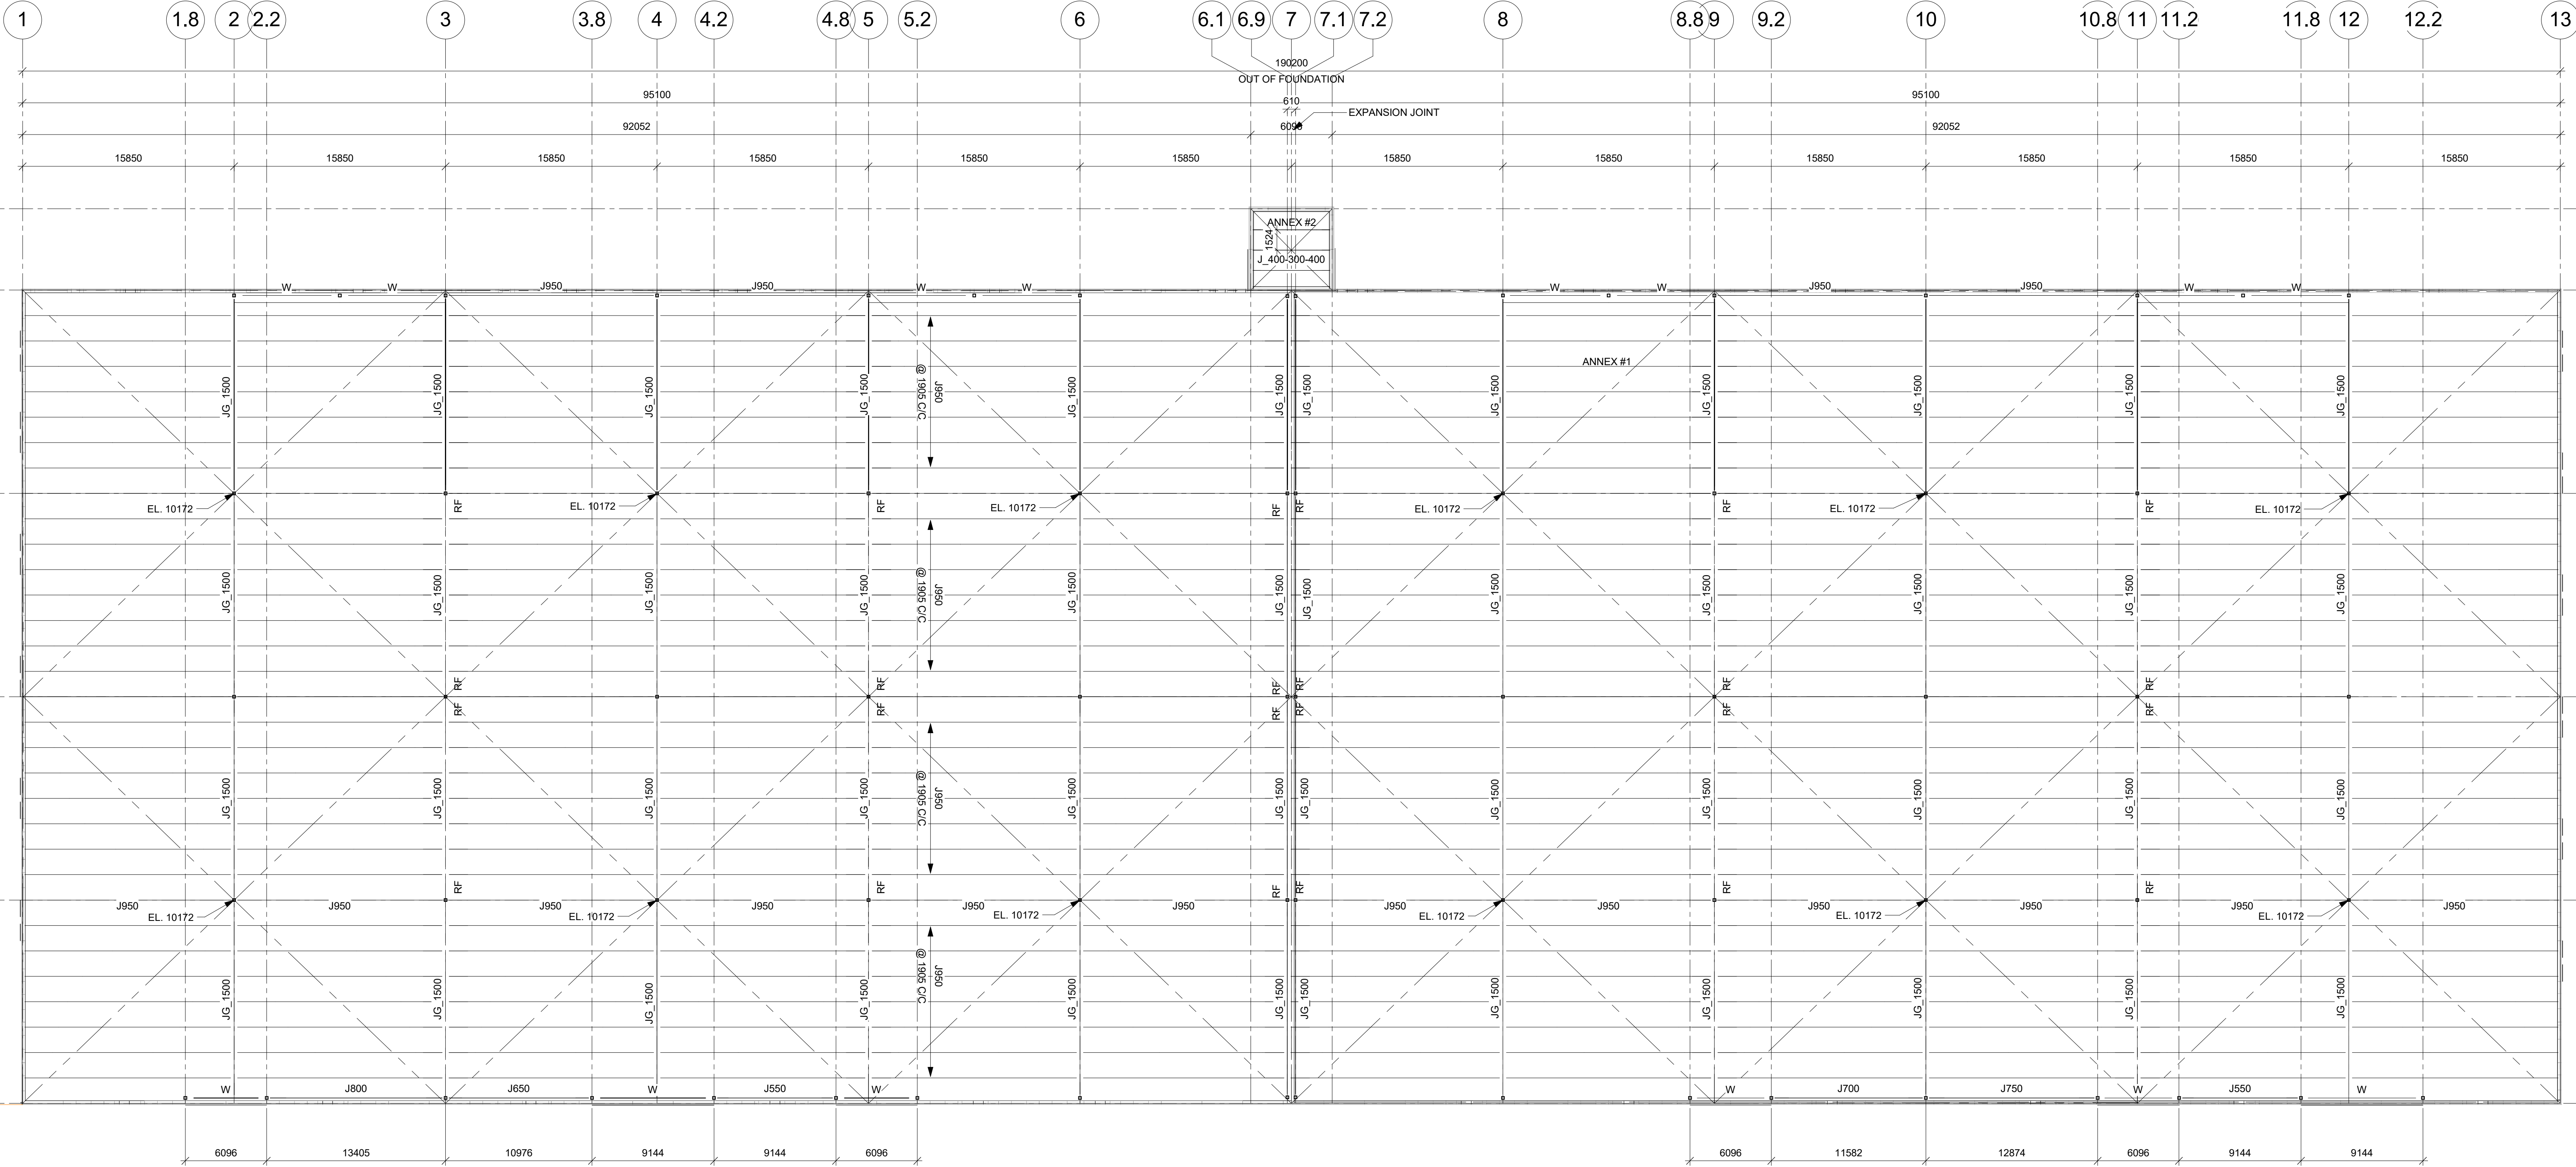

ROOF PLAN
1 : 225