




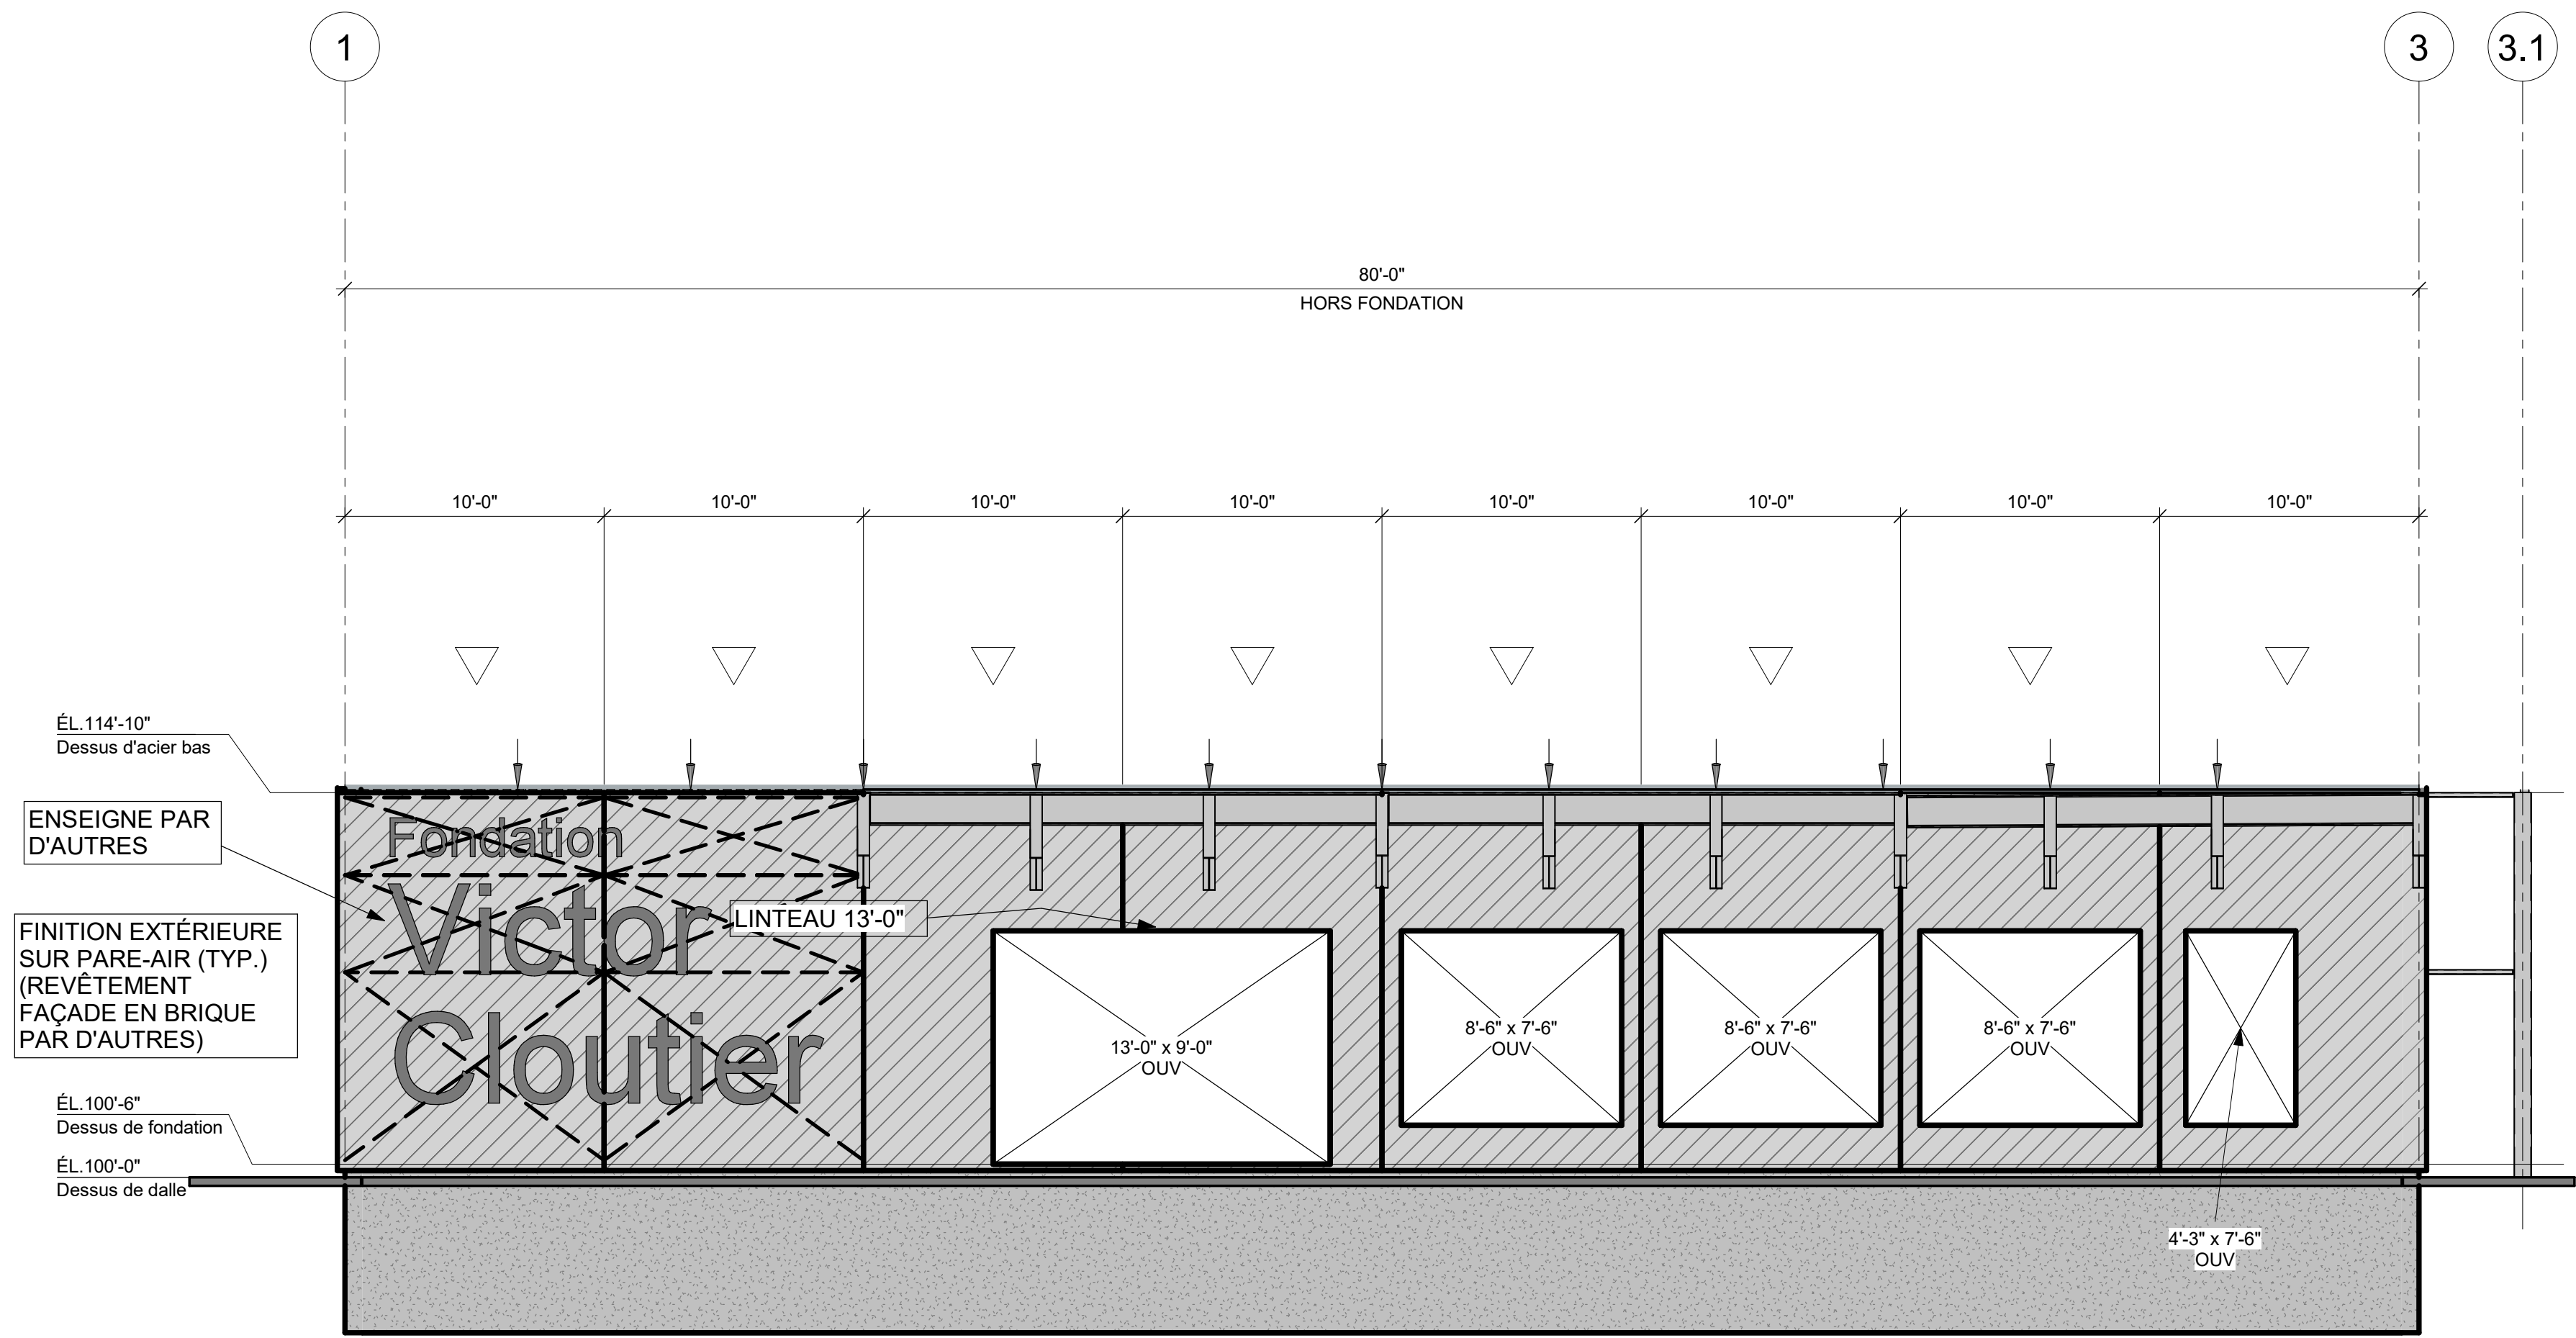


ÉLEVATION AXE B (SUD)
3/16" = 1'-0"

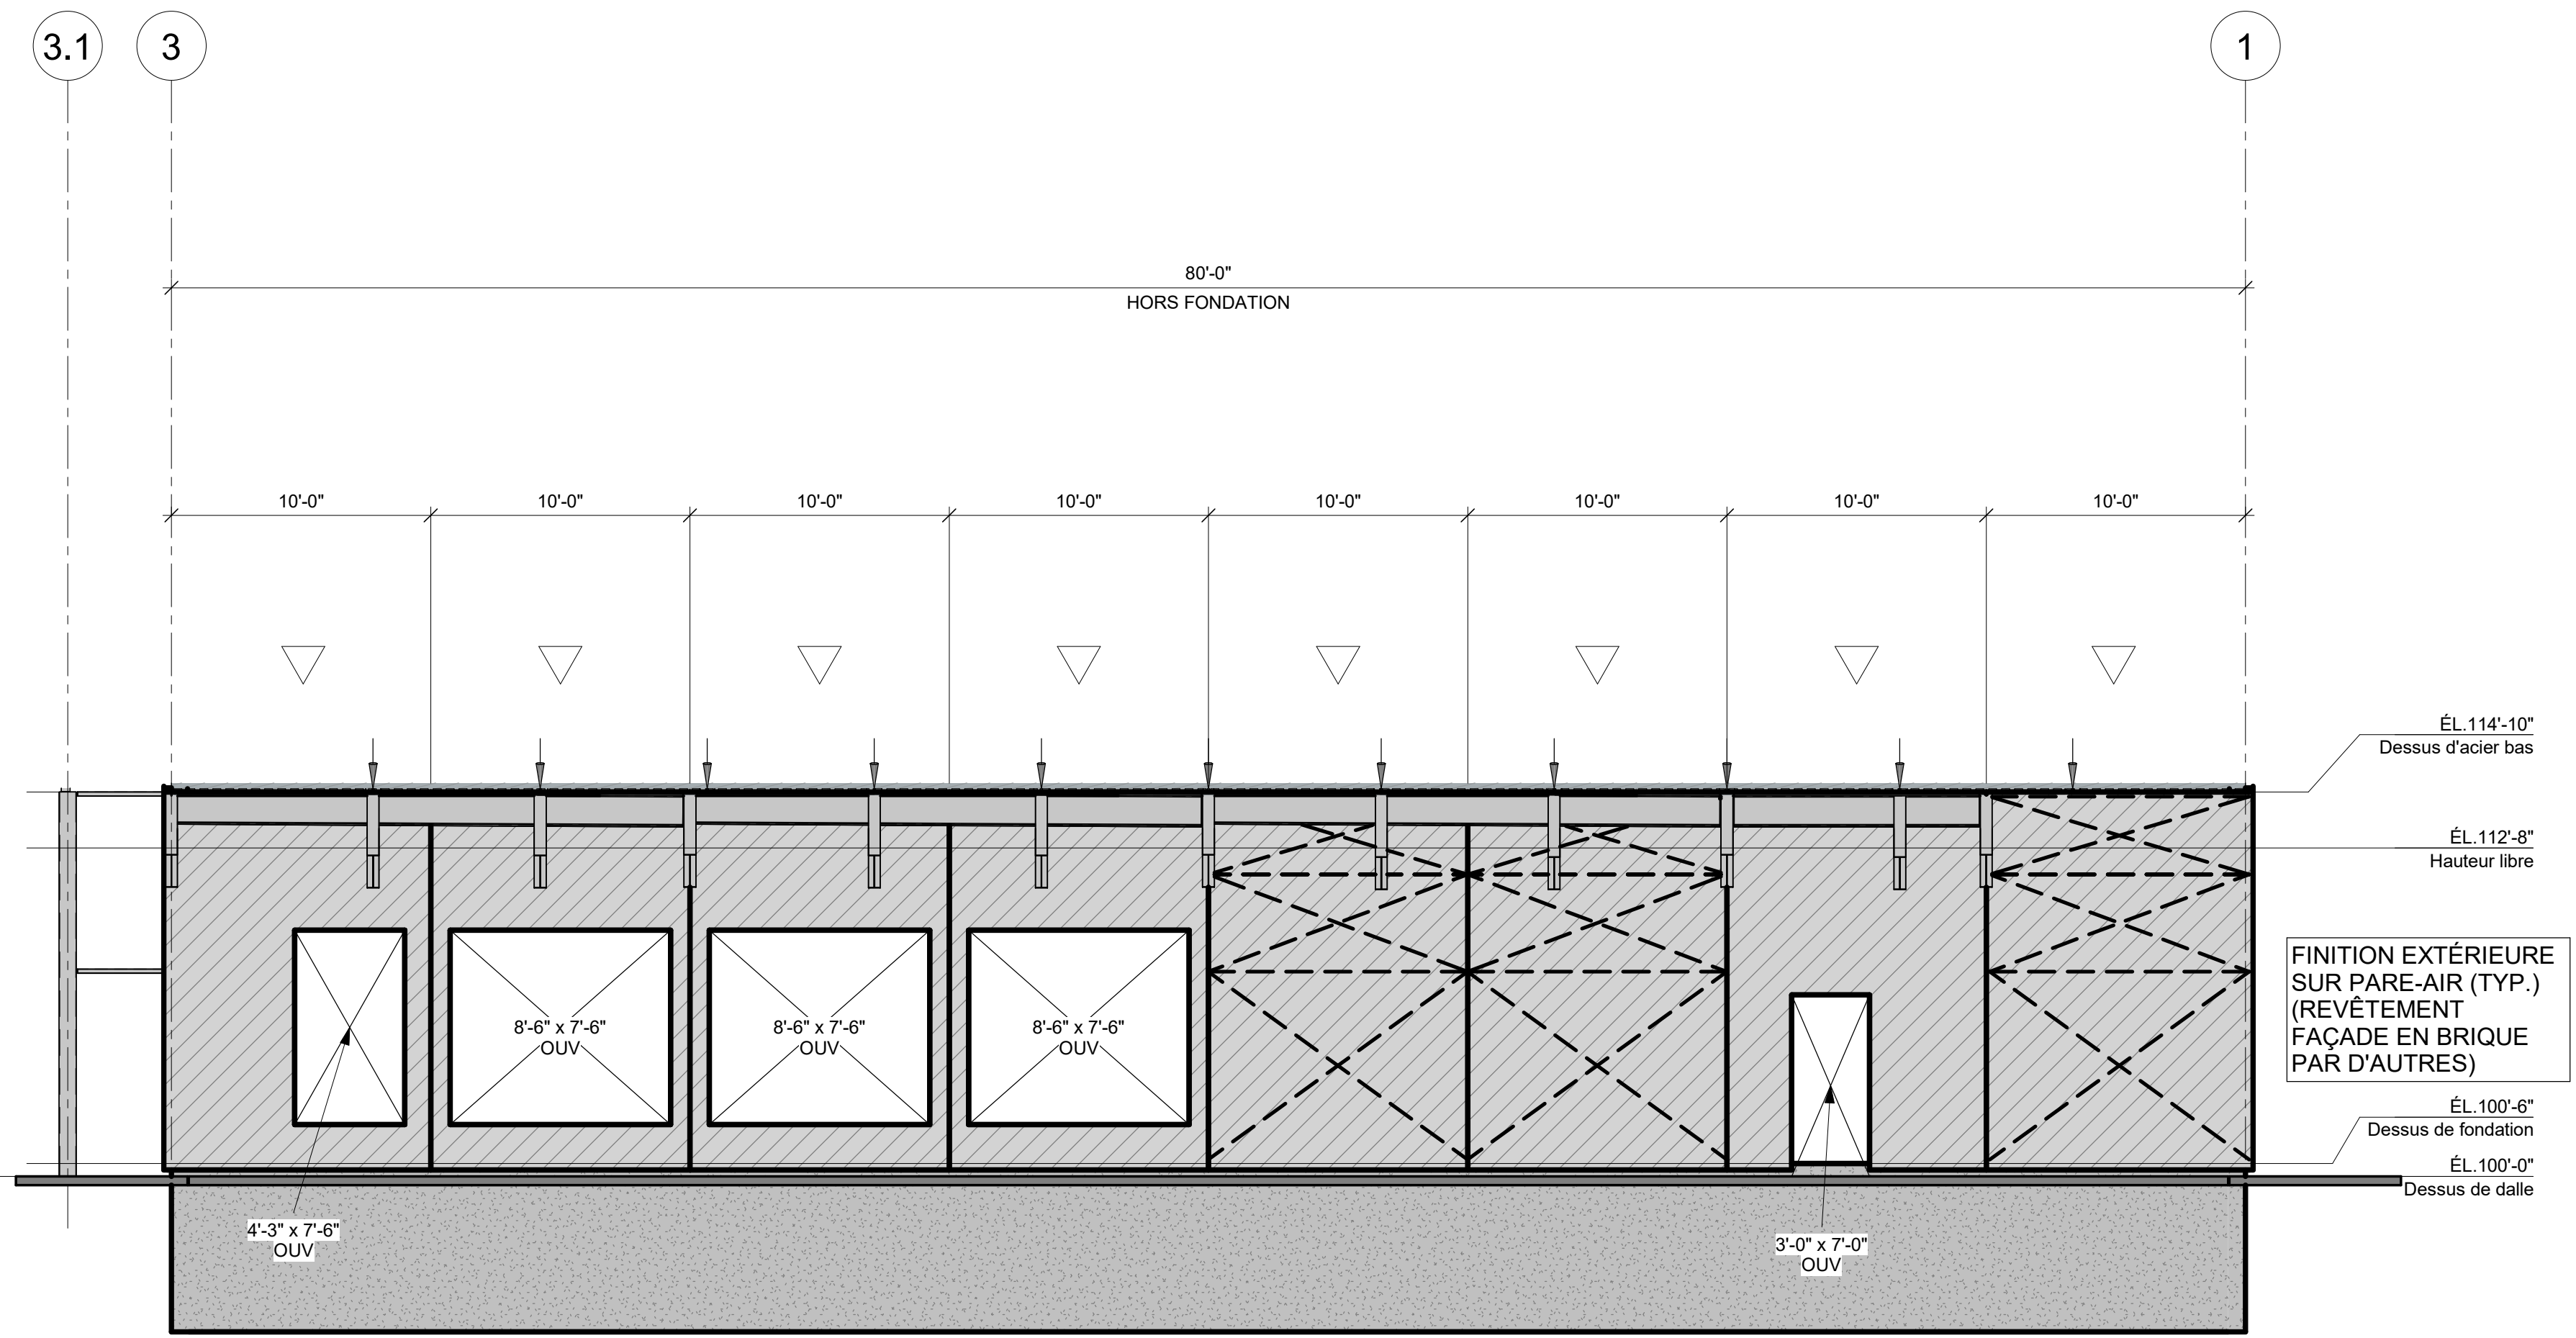


ÉLEVATION AXE E (NORD)
3/16" = 1'-0"

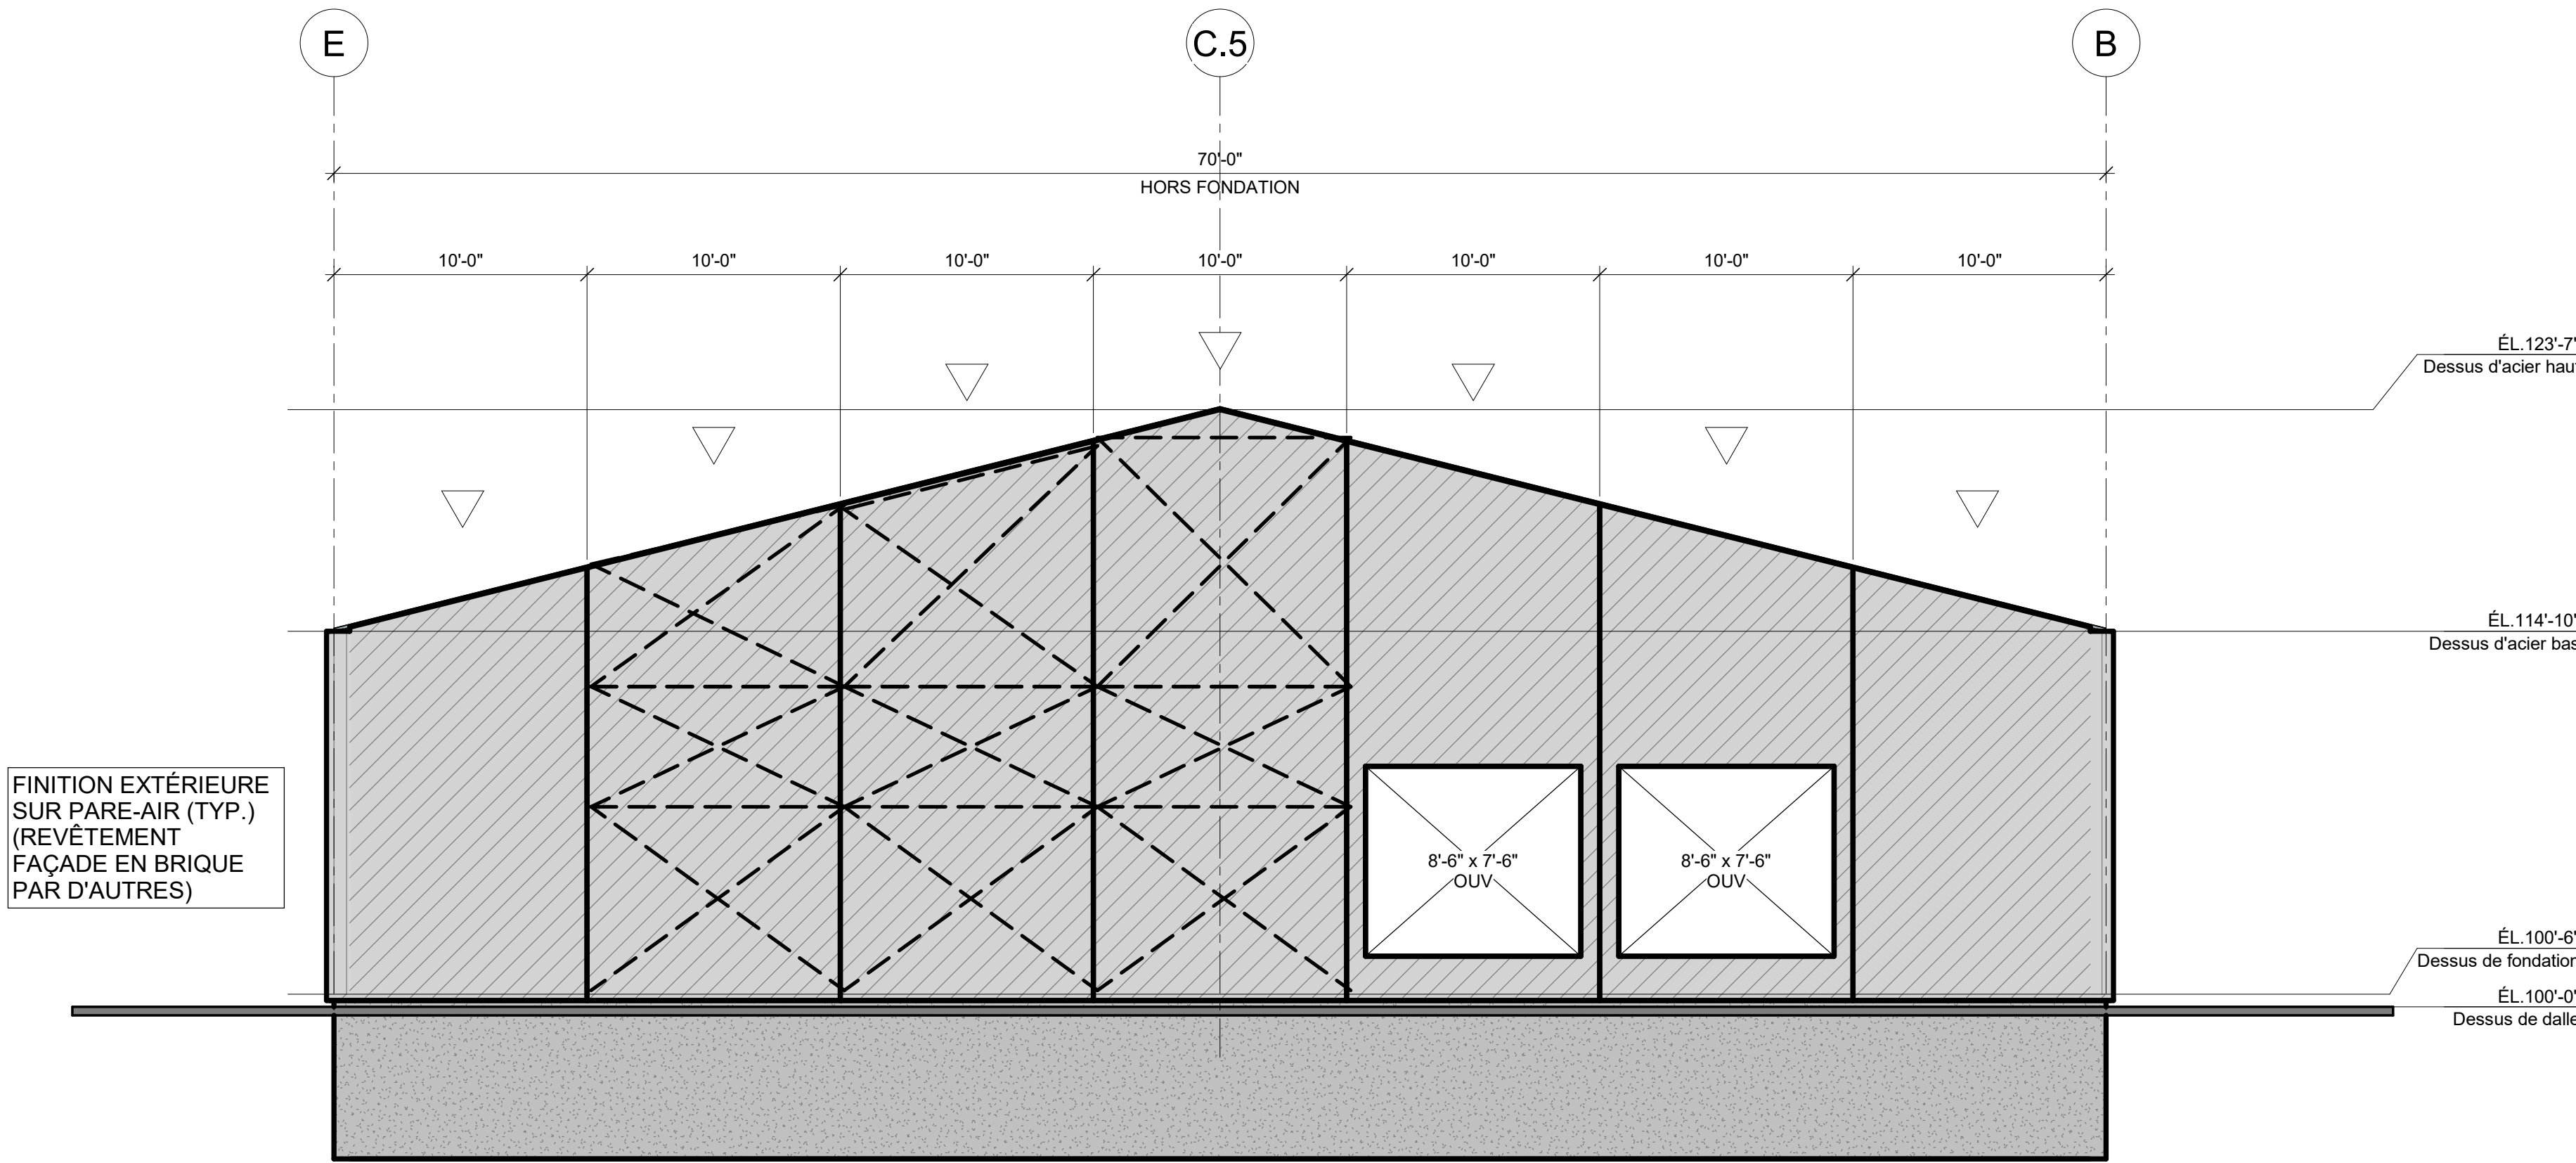


ÉLEVATION AXE 1 (OUEST)
3/16" = 1'-0"

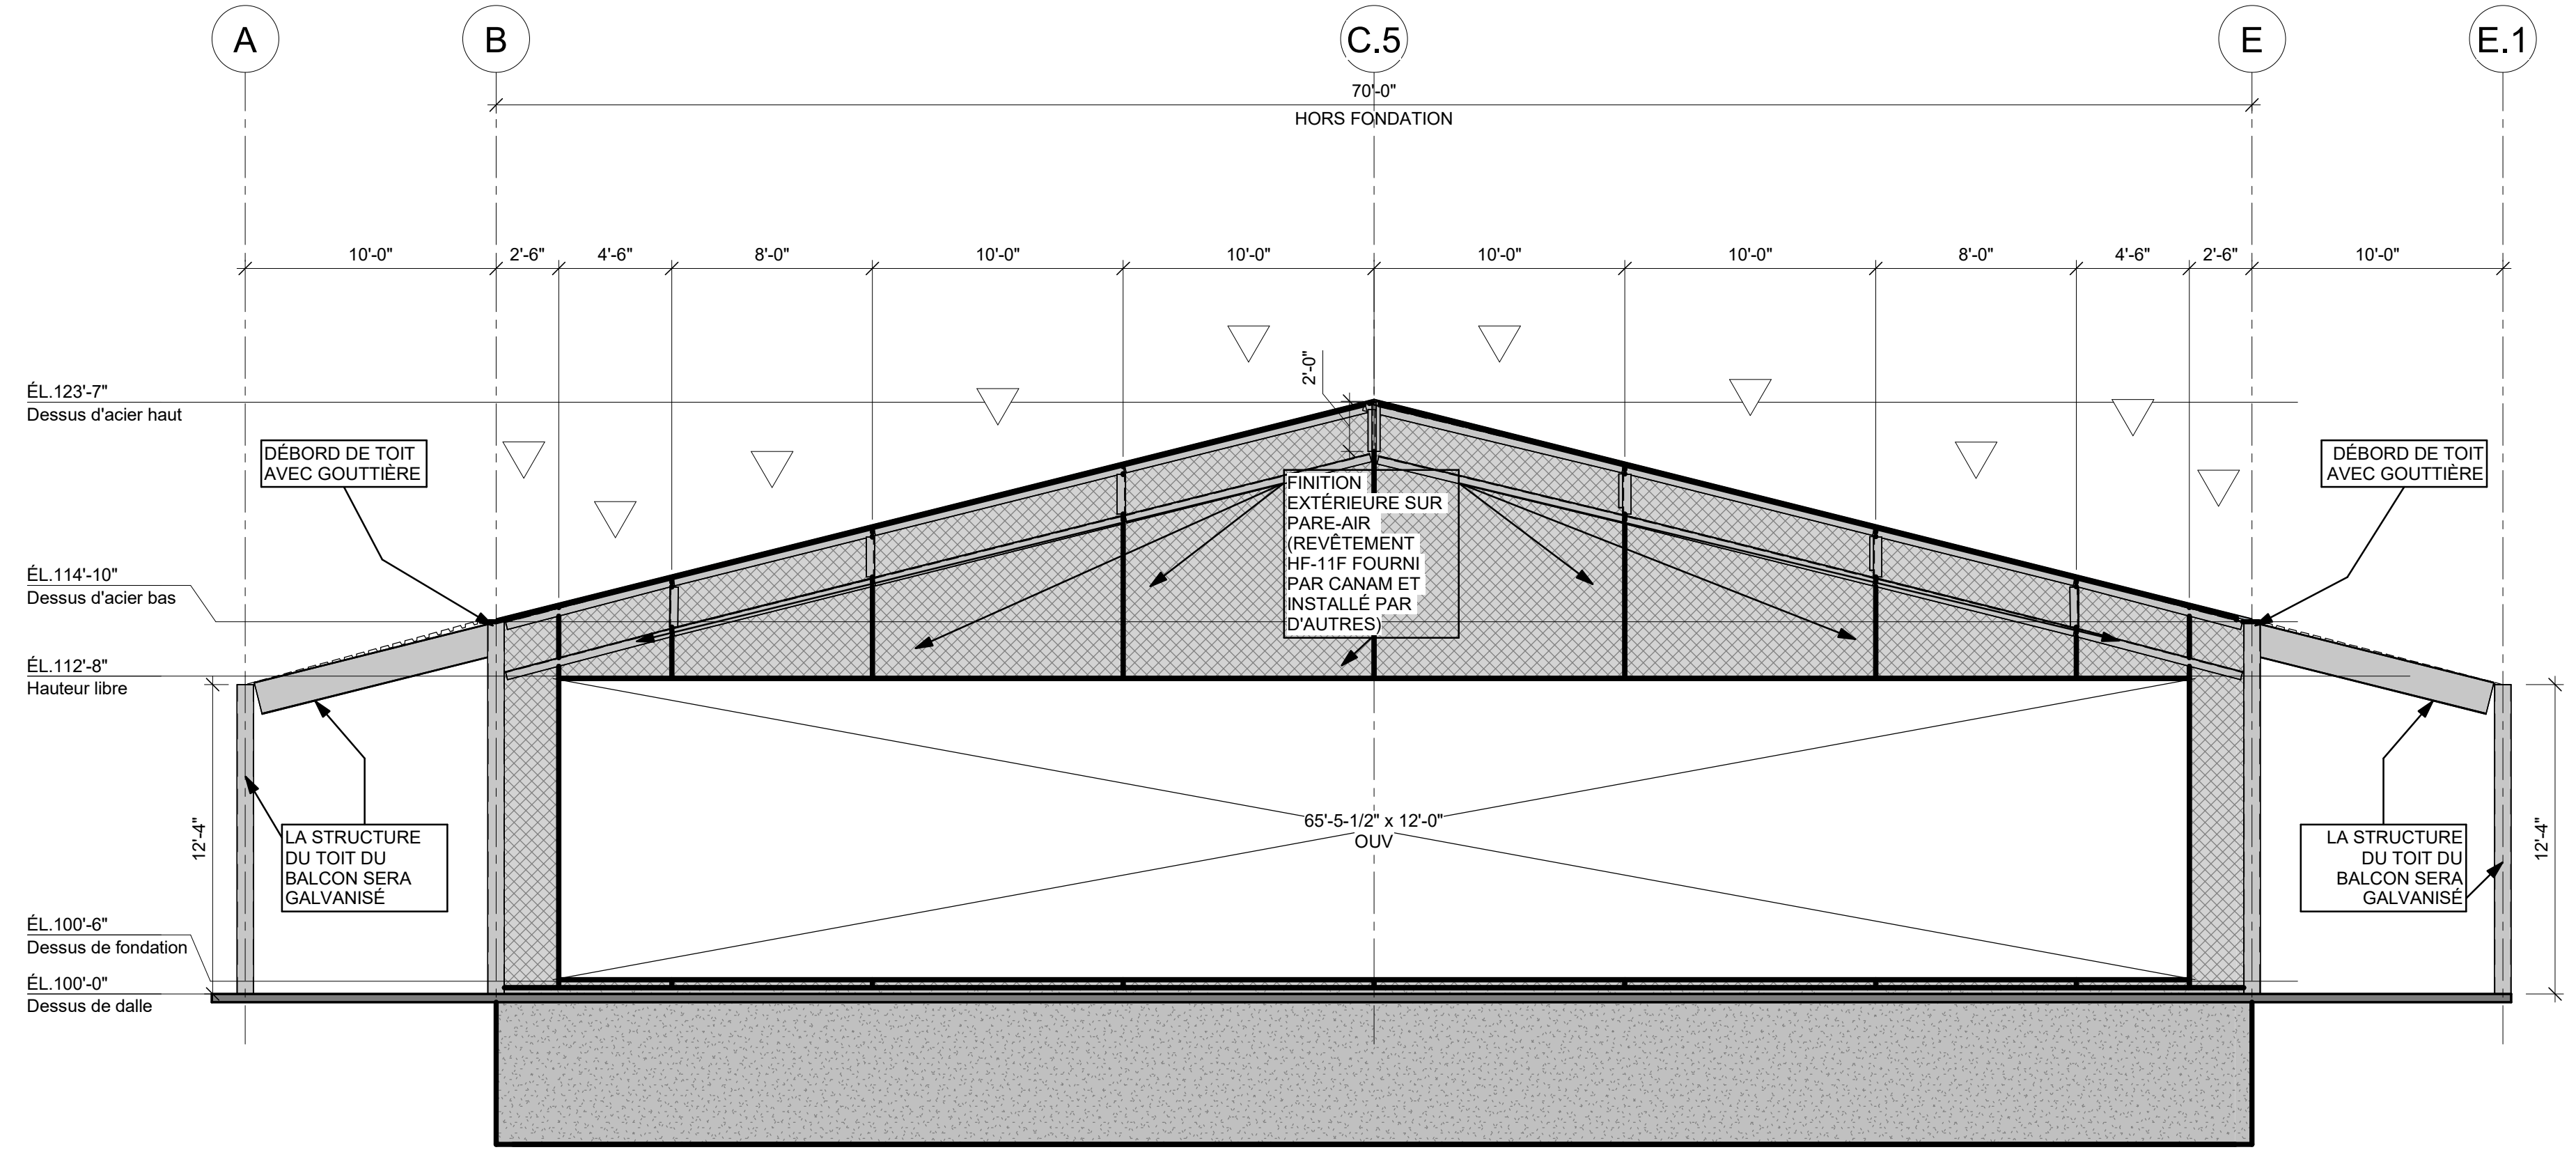

ÉLEVATION AXE 3 (EST)
3/16" = 1'-0"

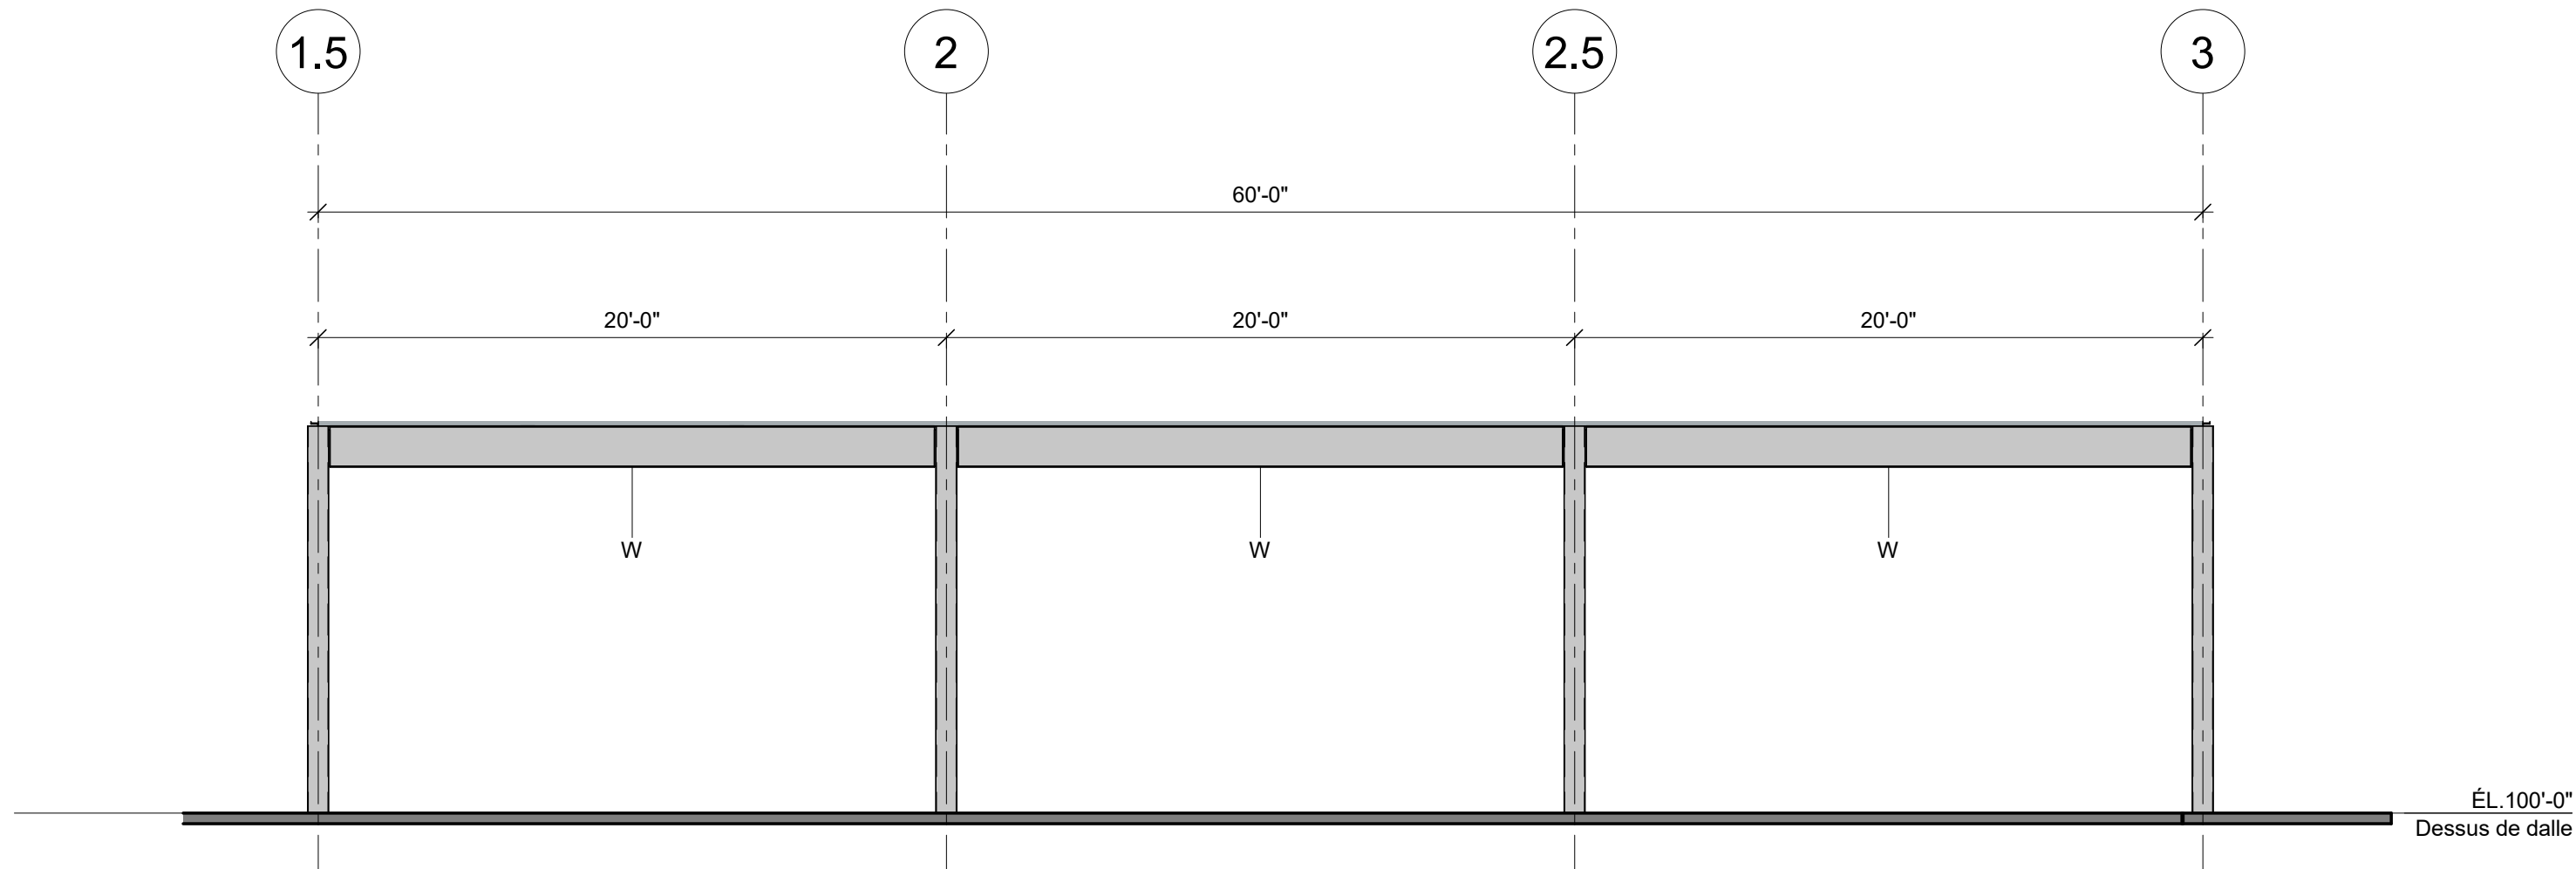

ÉLEVATION AXE A (STRUCTURE BALCON #1)
3/16" = 1'-0"

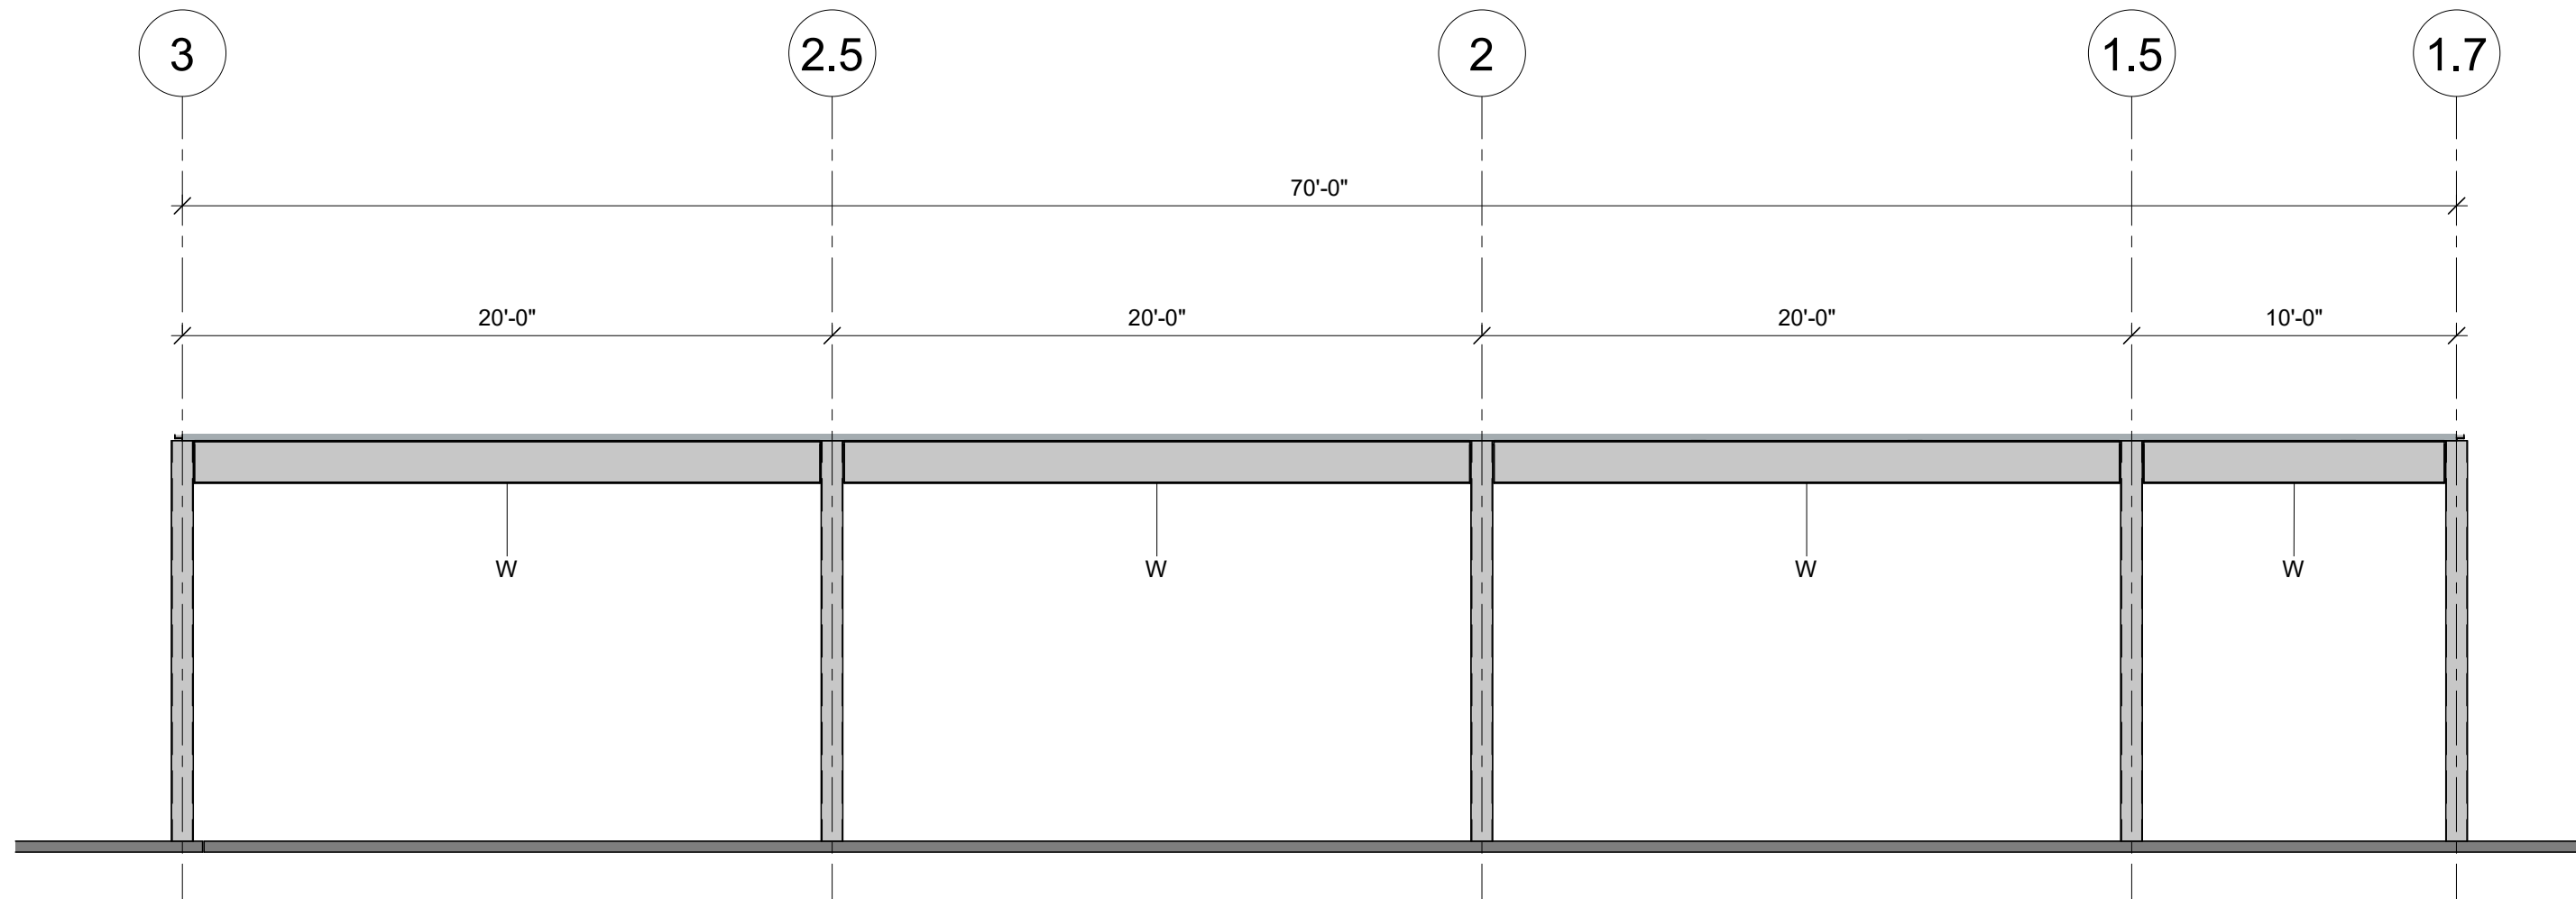

ÉLEVATION AXE E.1 (STRUCTURE BALCON #2)
3/16" = 1'-0"