




NORD POUR
L'ÉRECTION

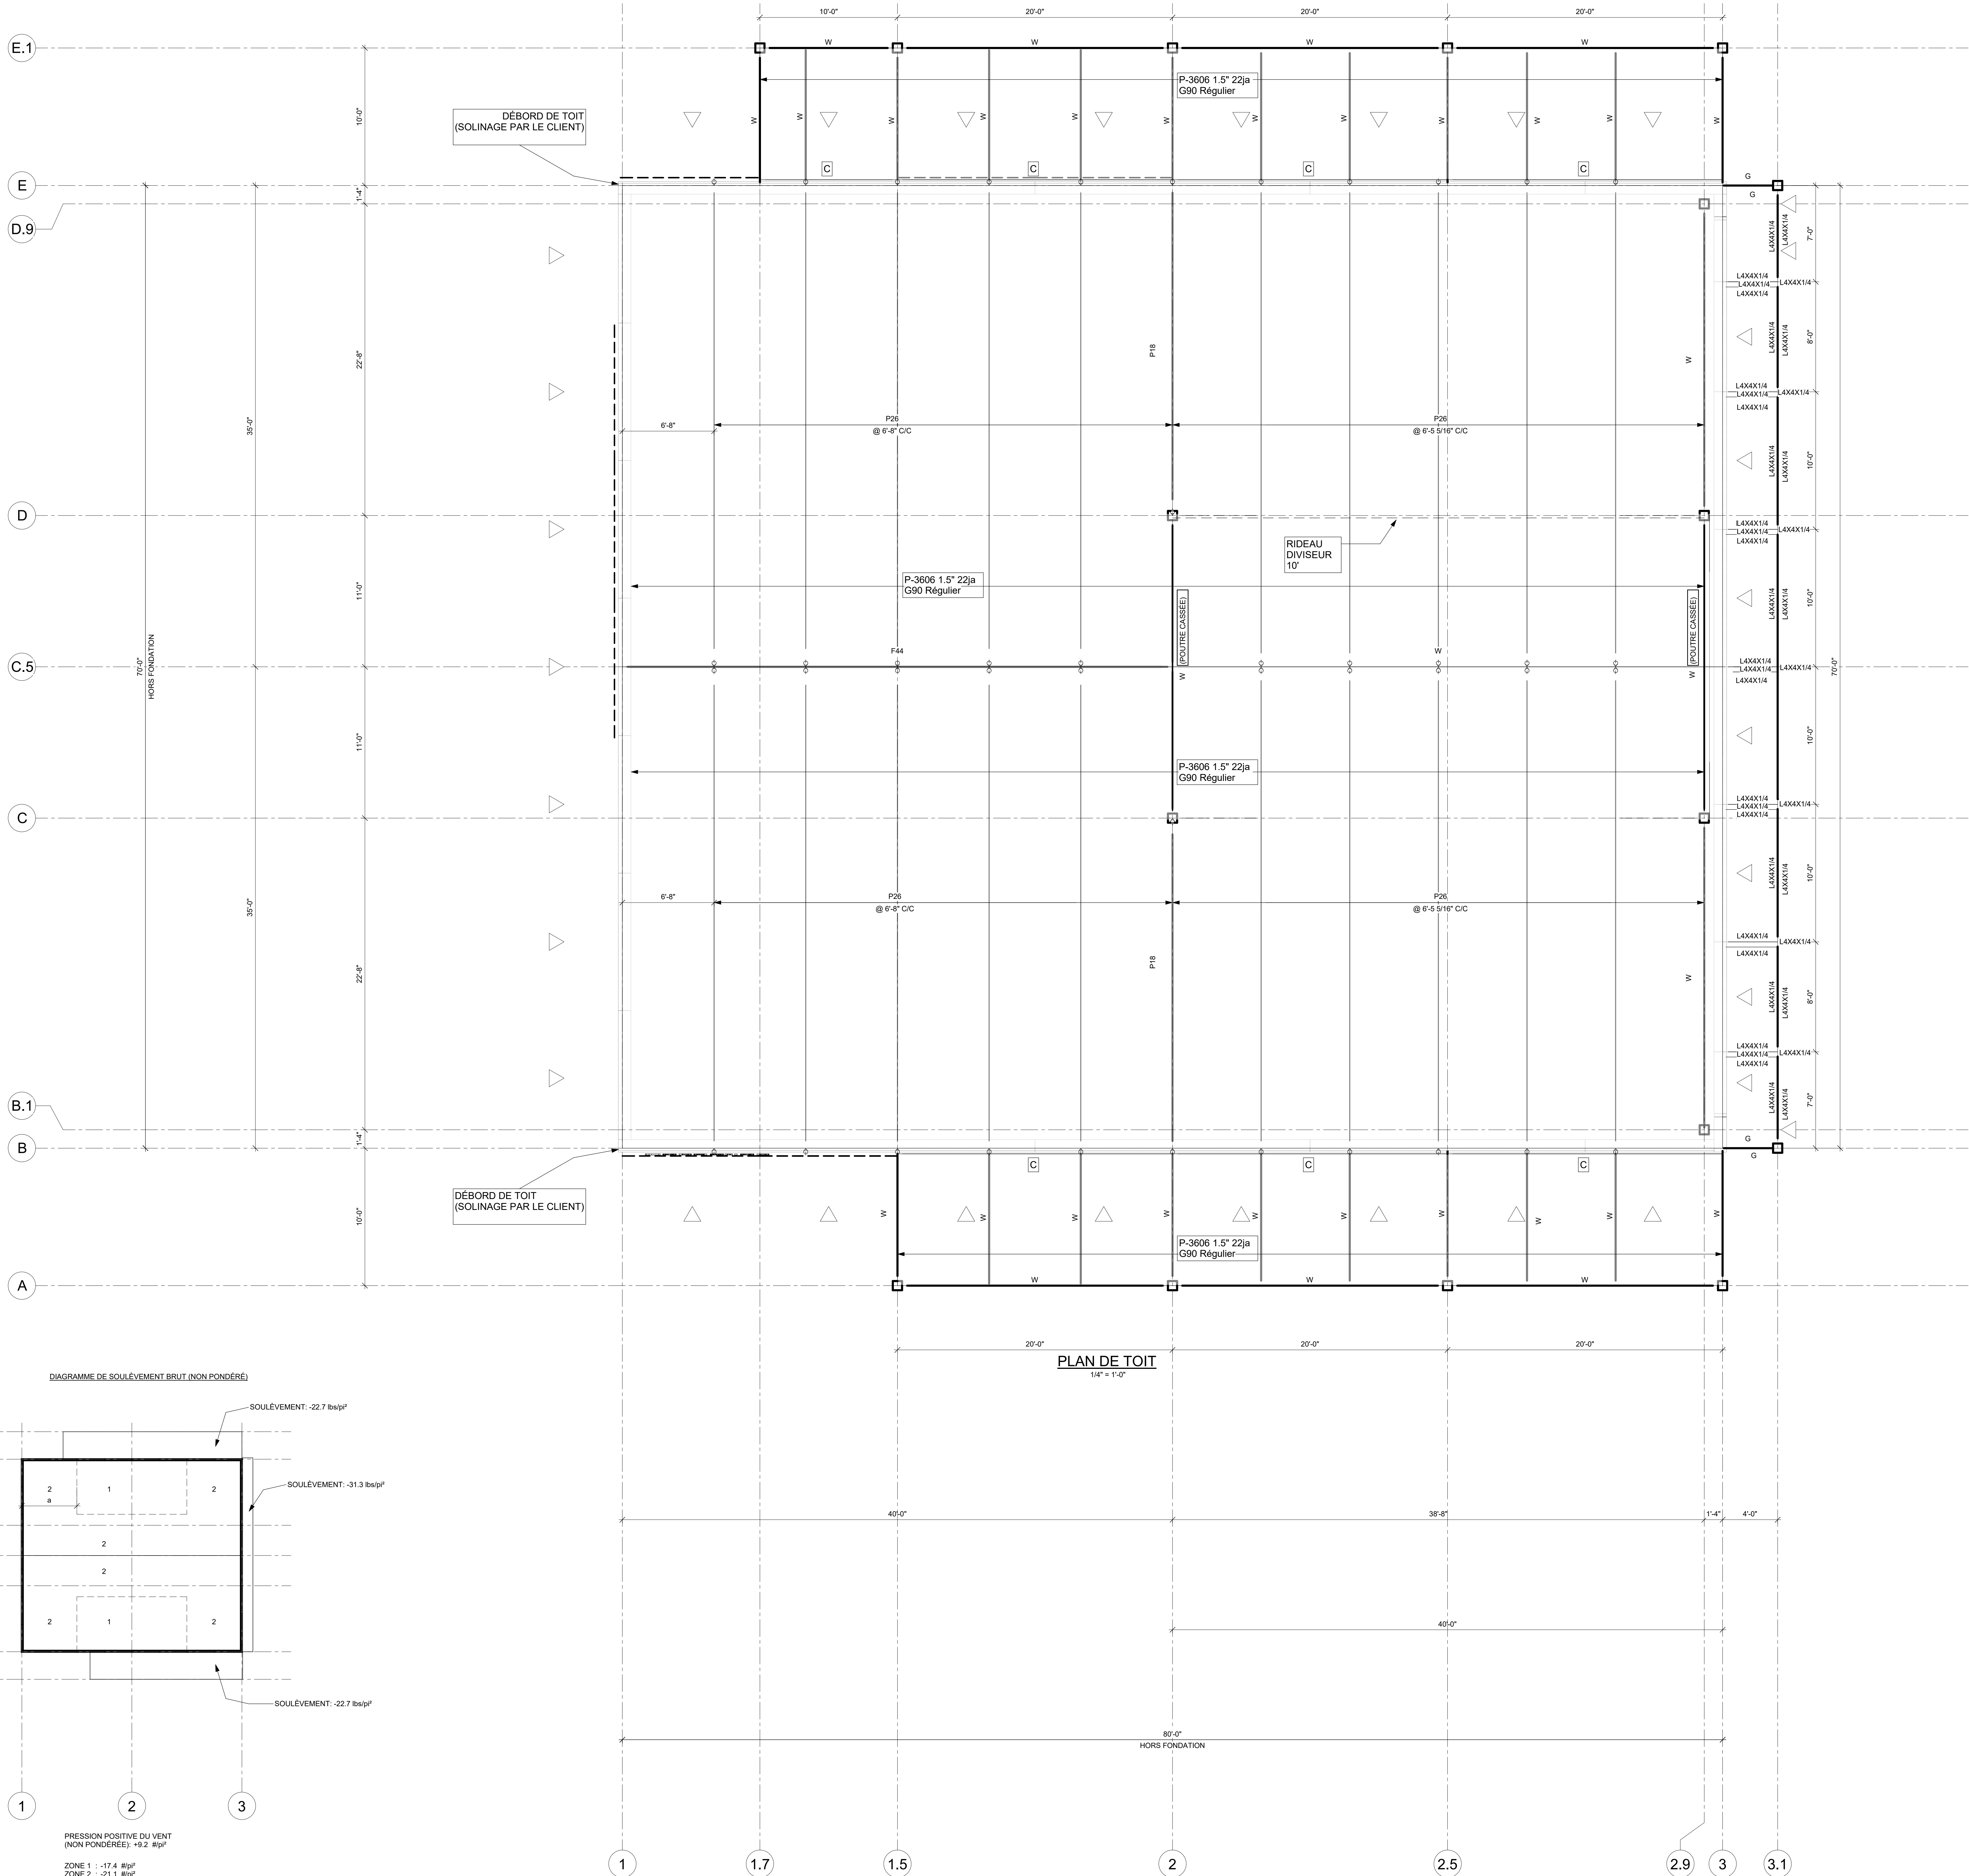

NOTE POUR LE CONTRACTEUR/ÉRECTEUR:
IL EST STRICTEMENT DEFENDU DE MODIFIER, COPIER, REPRODUIRE OU
DE DISTRIBUER CES DESSINS OU QUELQUES REPRÉSENTATIONS DE
CES DESSINS, PAR TOUTES SOURCES DE MÉDIA INCLUANT
ÉLECTRONIQUEMENT, SANS L'APPROBATION ÉCRITE DE GROUPE
CANAM INC.

TOIT

DESSUS DE PILASTRE : 99'-0"
DESSUS DE LA DALLE : 100'-0"
DESSUS DE LA FONDATION : 100'-0"
HAUTEUR LIBRE : 12'-8"
DESSUS D'ACIER : 114'-10"
DESSUS D'ACIER (HAUT) : 123'-7"

CHARGES

C.M. : 18 lbs/p²
Coll. : 4 lbs/p²
Sa : 28.5 lbs/p²
Sr : 12.53 lbs/p²
C.V. : 0.8
C.V. au toit : 0 lbs/p²
C.V. : 1.0
Charge de neige au toit : 59.3 lbs/p²
V. : 1.0
Vent q = 150 : 7.94 lbs/p²
Selon (Sol de classe D assumé)

ts : 1.0
Ss (0.2) : 0.491
Ss (0.5) : 0.483
Ss (1.0) : 0.297
Ss (2.0) : 0.145
Ss (5.0) : 0.041
Ss (10.0) : 0.013
PGA : 0.272
PGV : 0.331

CHARGES

- Charge morte au toit (excluant charge collatérale) : lbs/p²
- Charge collatérale : lbs/p² (incluant éclairage étou mécanique et gicleurs plus petite que 4" de diamètre)
- Charge de neige au toit : lbs/p²
- Charge vive au toit : lbs/p²
- Charge de vent q 1/50 : lbs/p²
- Charge de neige au sol : lbs/p²
- Catégorie de risque : normal
- Coefficient de surcharge de neige : Cs = 0.8
- Coefficient de vent : Cw = 1.0

Code Applicable : Code National du Bâtiment du Canada
Code du bâtiment du Québec, dernières éditions adoptées
Code de Pratique Standard ICCA.

Type de sol assumé : classe D

NOTE:
1. Si toutefois la catégorie d'emplacement devient E ou F selon le rapport géotechnique, le concept structural préliminaire (localisation et géométrie des contreventements, etc.) devra être validé et coordonné par l'ingénieur de Canam.

PRÉLIMINAIRE

NE DOIT PAS SERVIR À LA
CONSTRUCTION

REVISION	DATE	DESCRIPTION	DESS	VER
----------	------	-------------	------	-----

DESSIN	CONÇU	INGÉNIEUR	PROJET	ÉCHELLE
S.L.				Comme indiqué
VERIFIÉ		INGÉNIEURS CONSEILS / ARCHITECTES	DATE (mm/aa/aaaa)	
			09/02/2026	

DESIGN	CONÇU	INGÉNIEUR	PROJET	ÉCHELLE
S.L.				Comme indiqué
VERIFIÉ		INGÉNIEURS CONSEILS / ARCHITECTES	DATE (mm/aa/aaaa)	
			09/02/2026	

CLIENT : LES CONSTRUCTIONS CMI INC.



SCHEAU PROFESSIONNEL

PROJET

FONDATION VICTOR-CLOUTIER
NOTRE-DAME-DES-PINS, QC

TITRE
CROQUIS PRÉLIMINAIRE - PLAN DE
TOIT

NUMÉRO CONTRAT	NUMÉRO DESSIN	DIVISION	REVISION
P2026-024	EsMx401		