




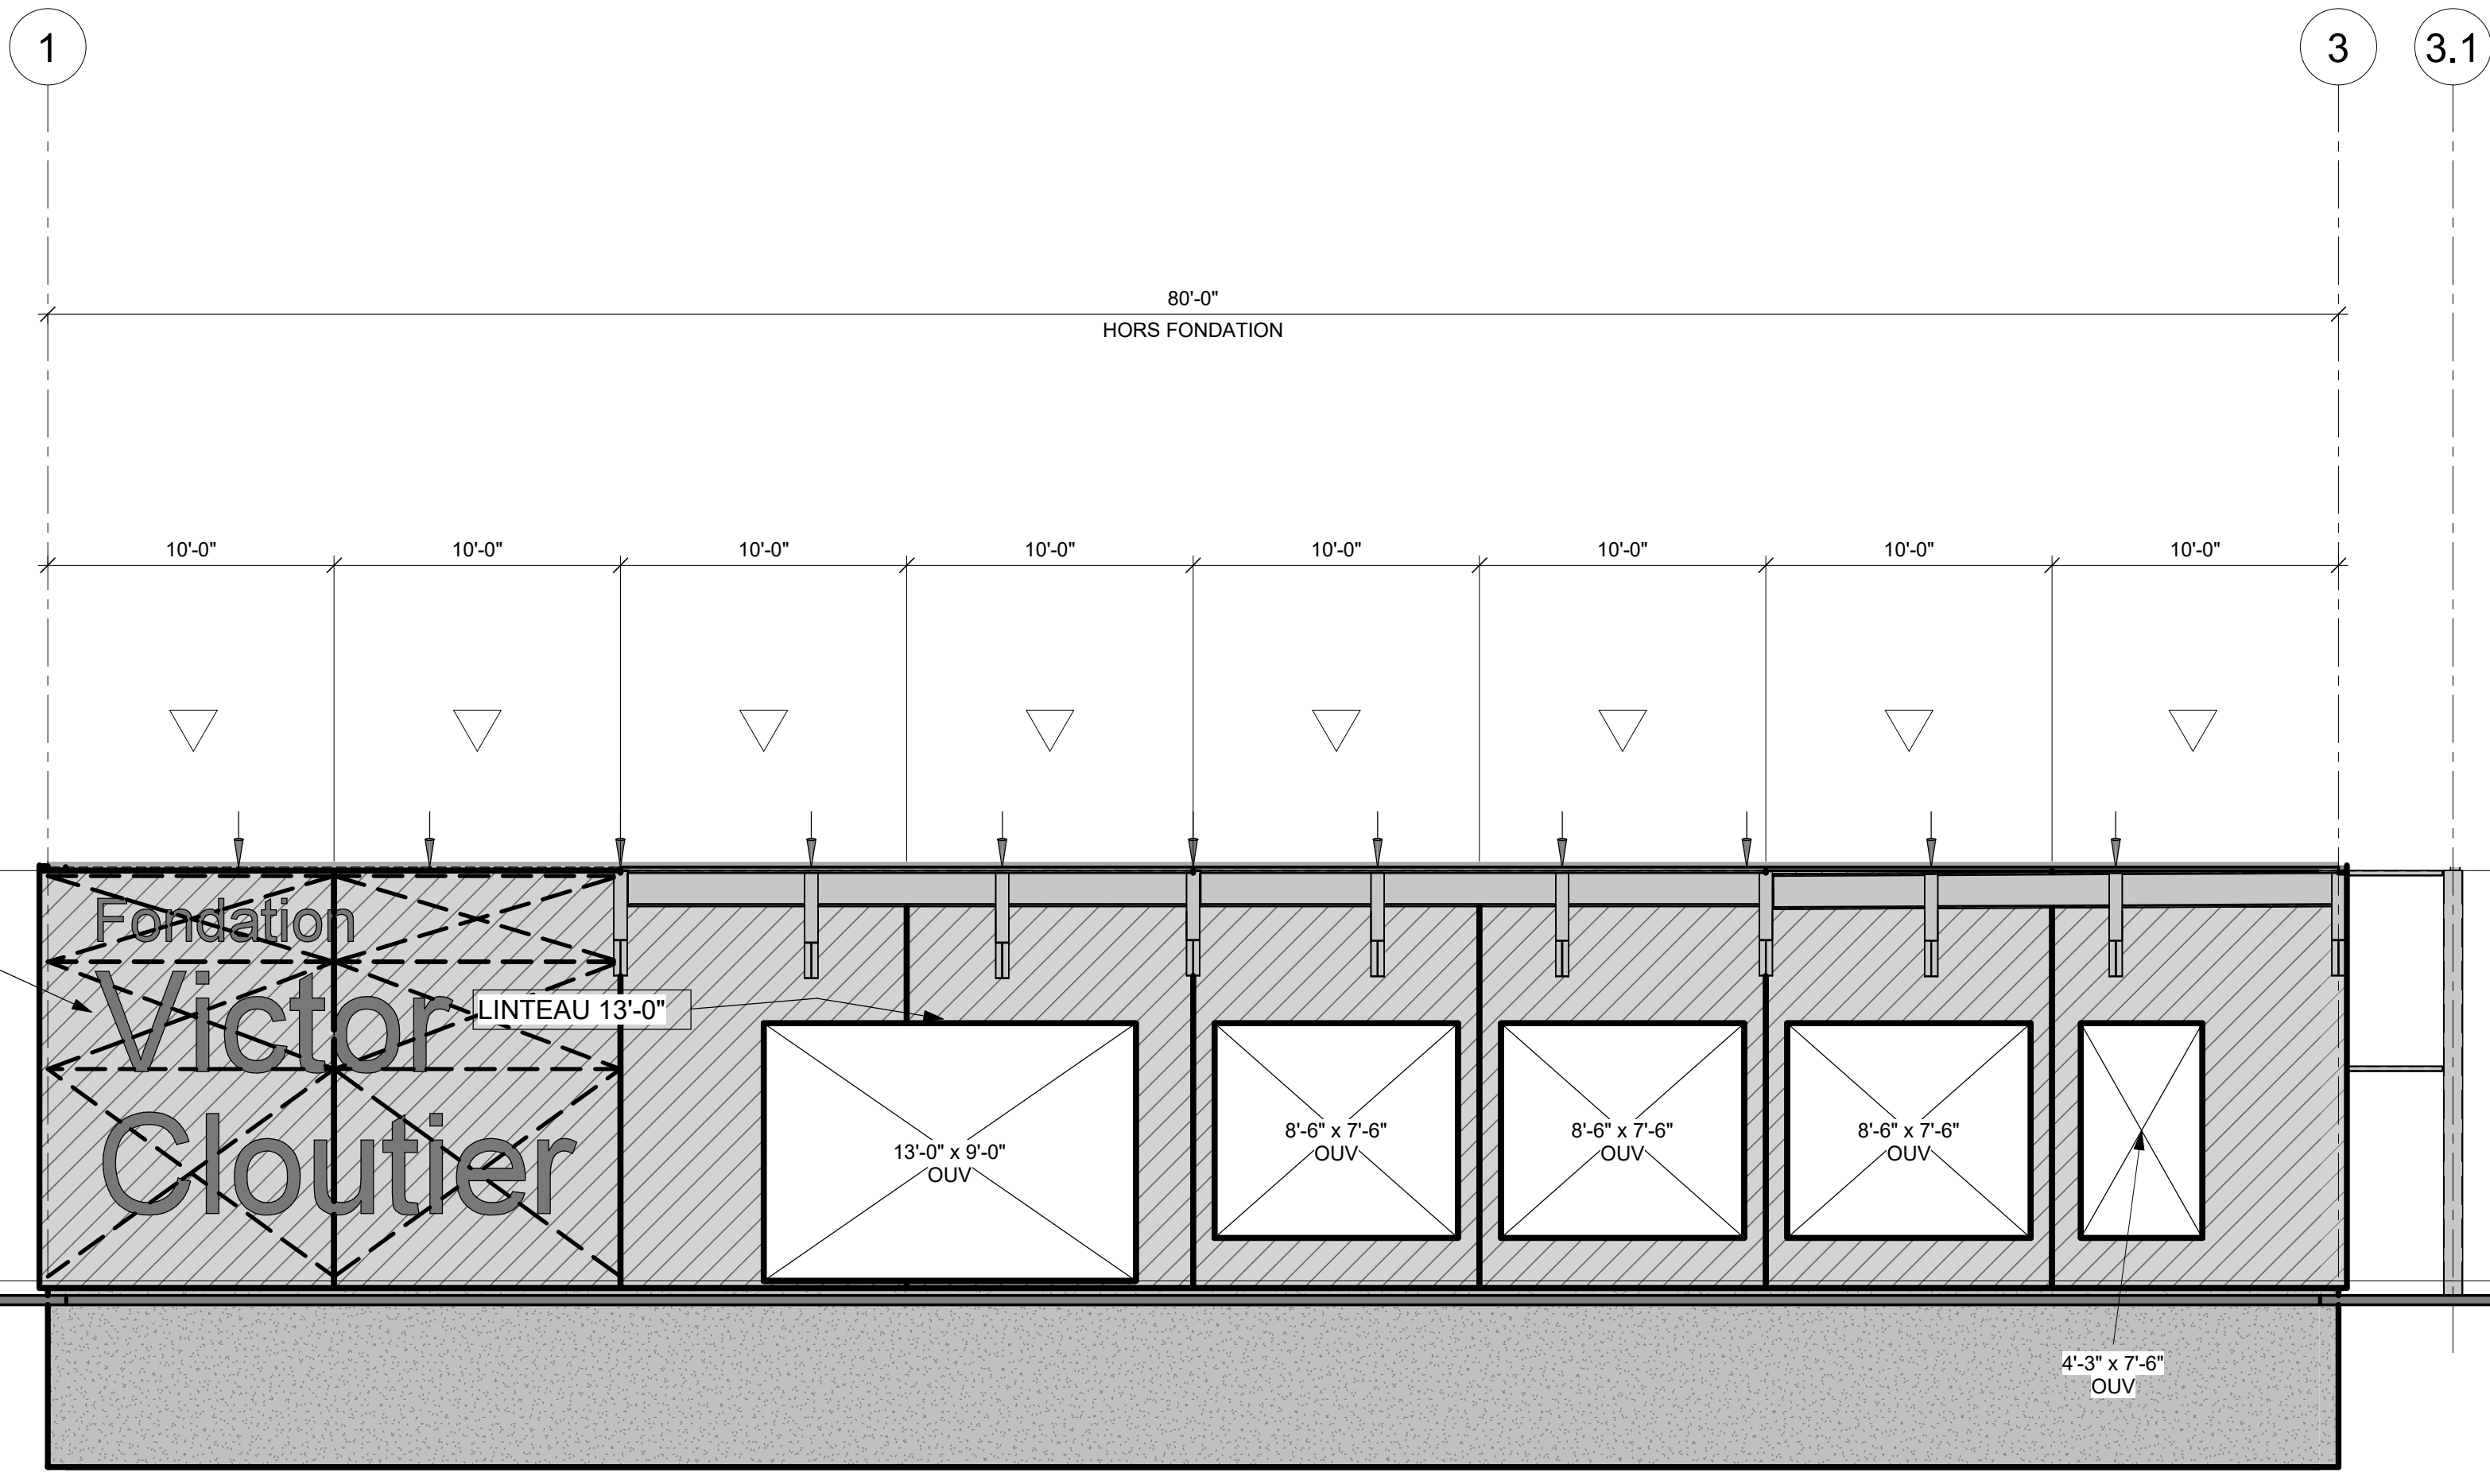


ÉLEVATION AXE B (SUD)
3/16" = 1'-0"

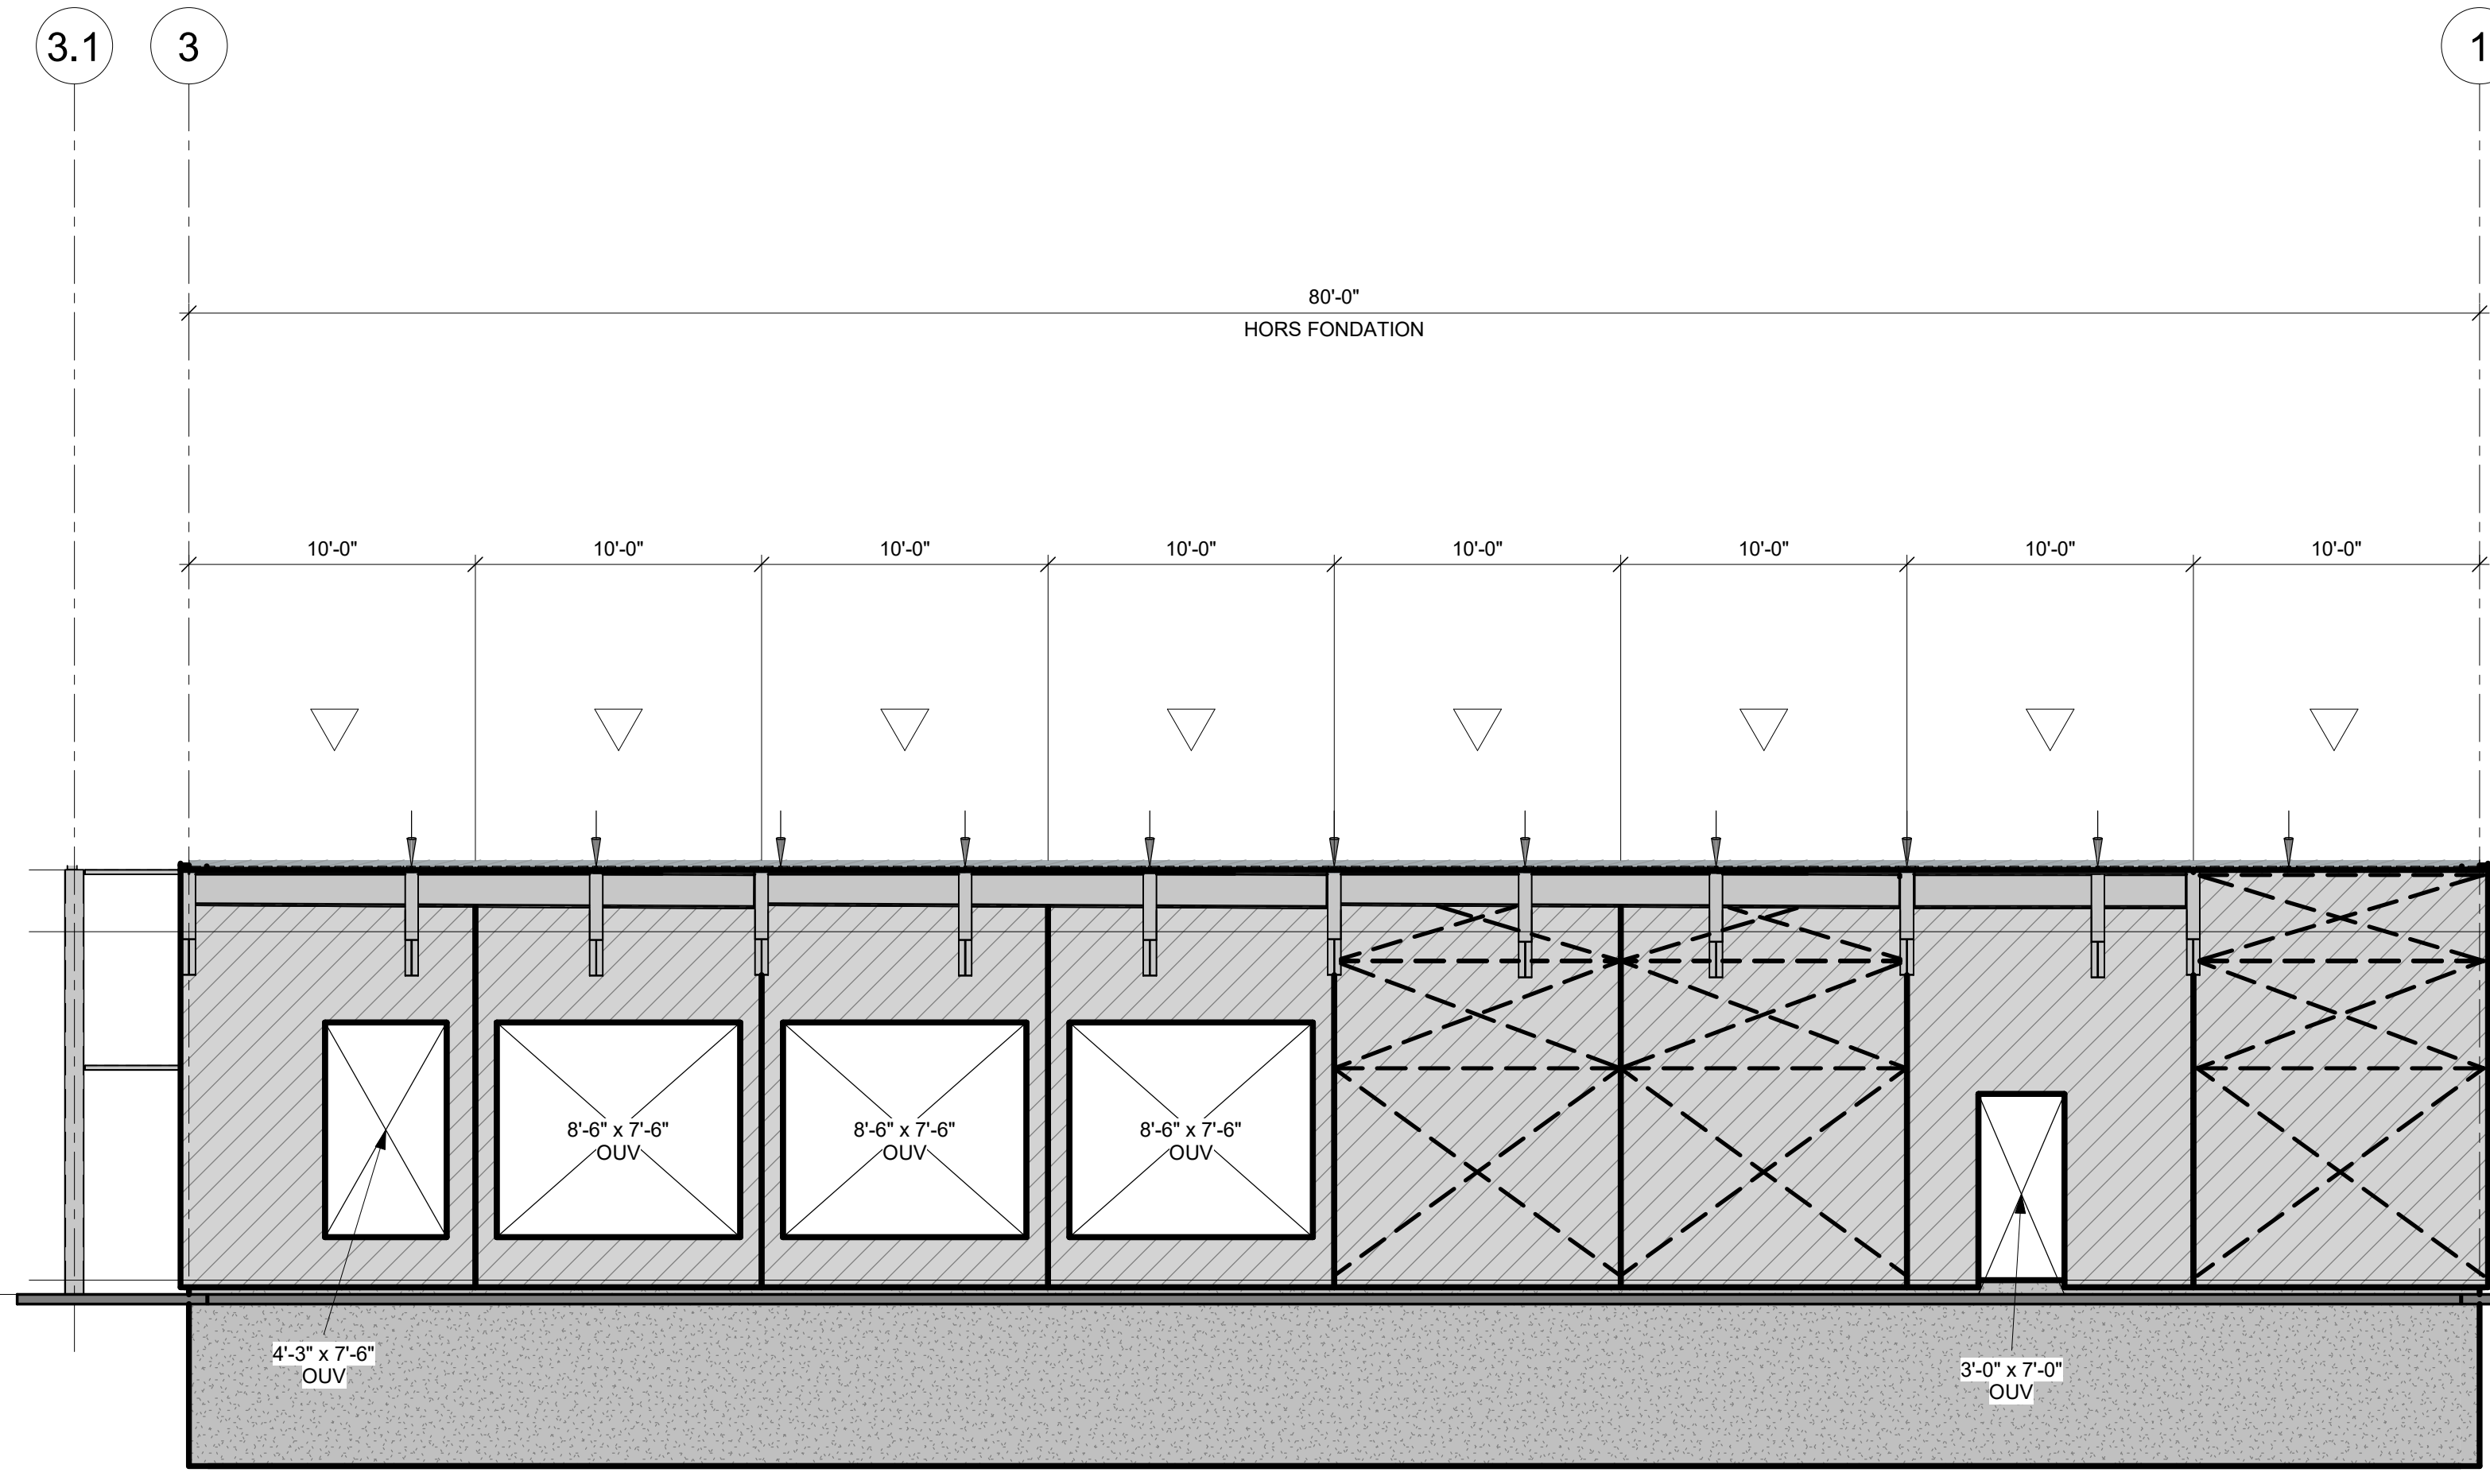


ÉLEVATION AXE E (NORD)
3/16" = 1'-0"

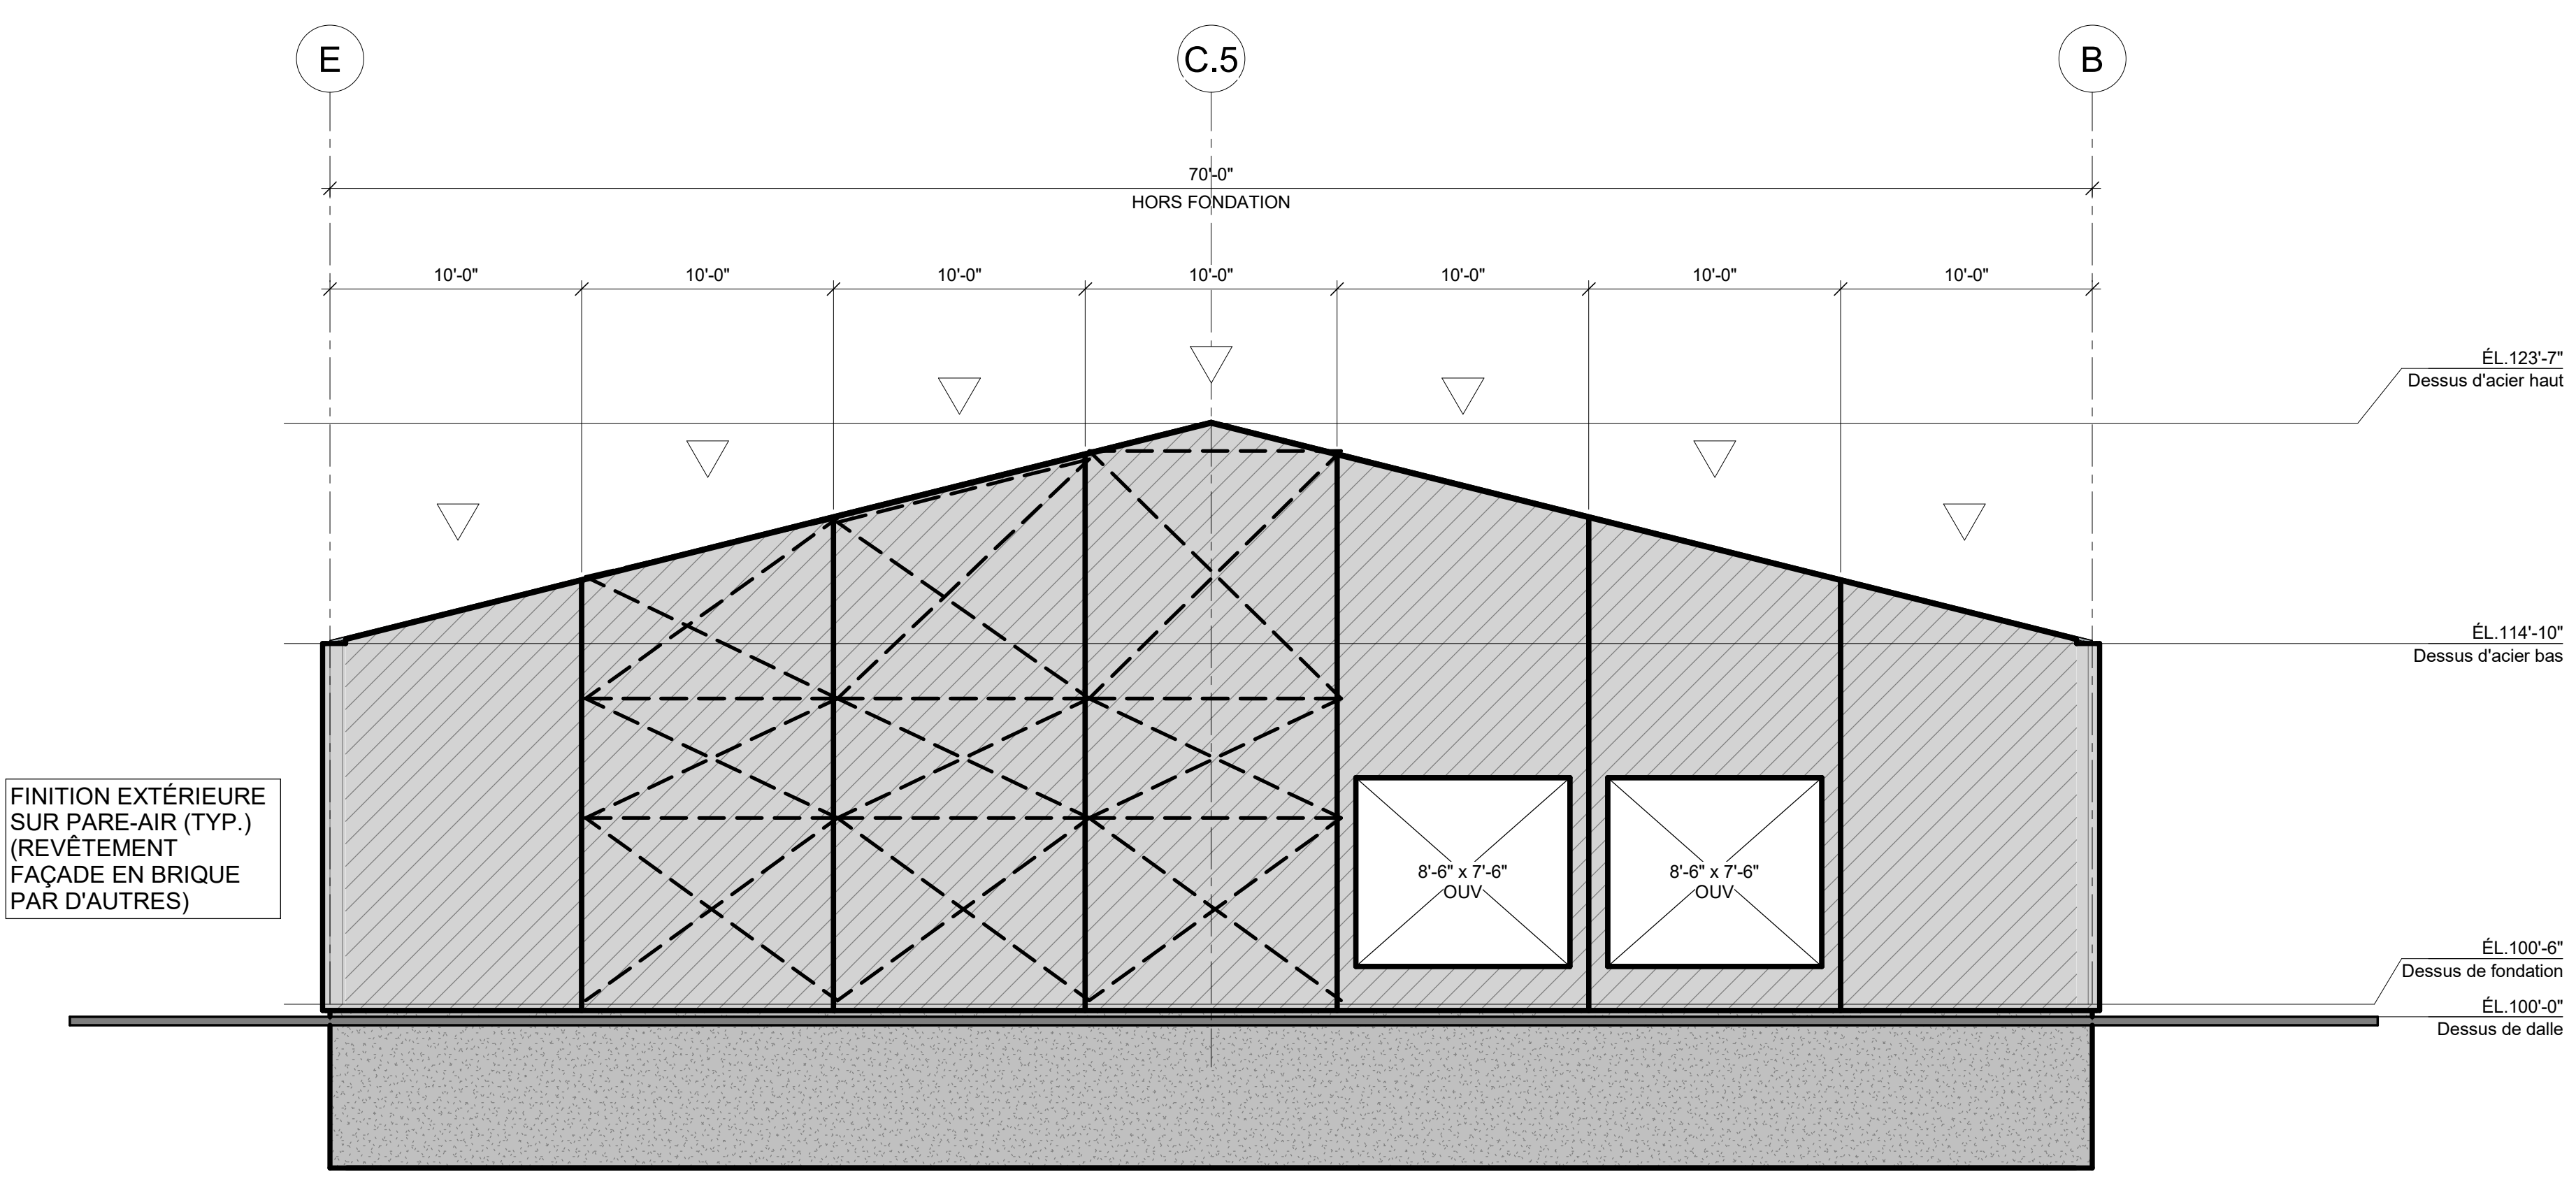


ÉLEVATION AXE 1 (OUEST)
3/16" = 1'-0"

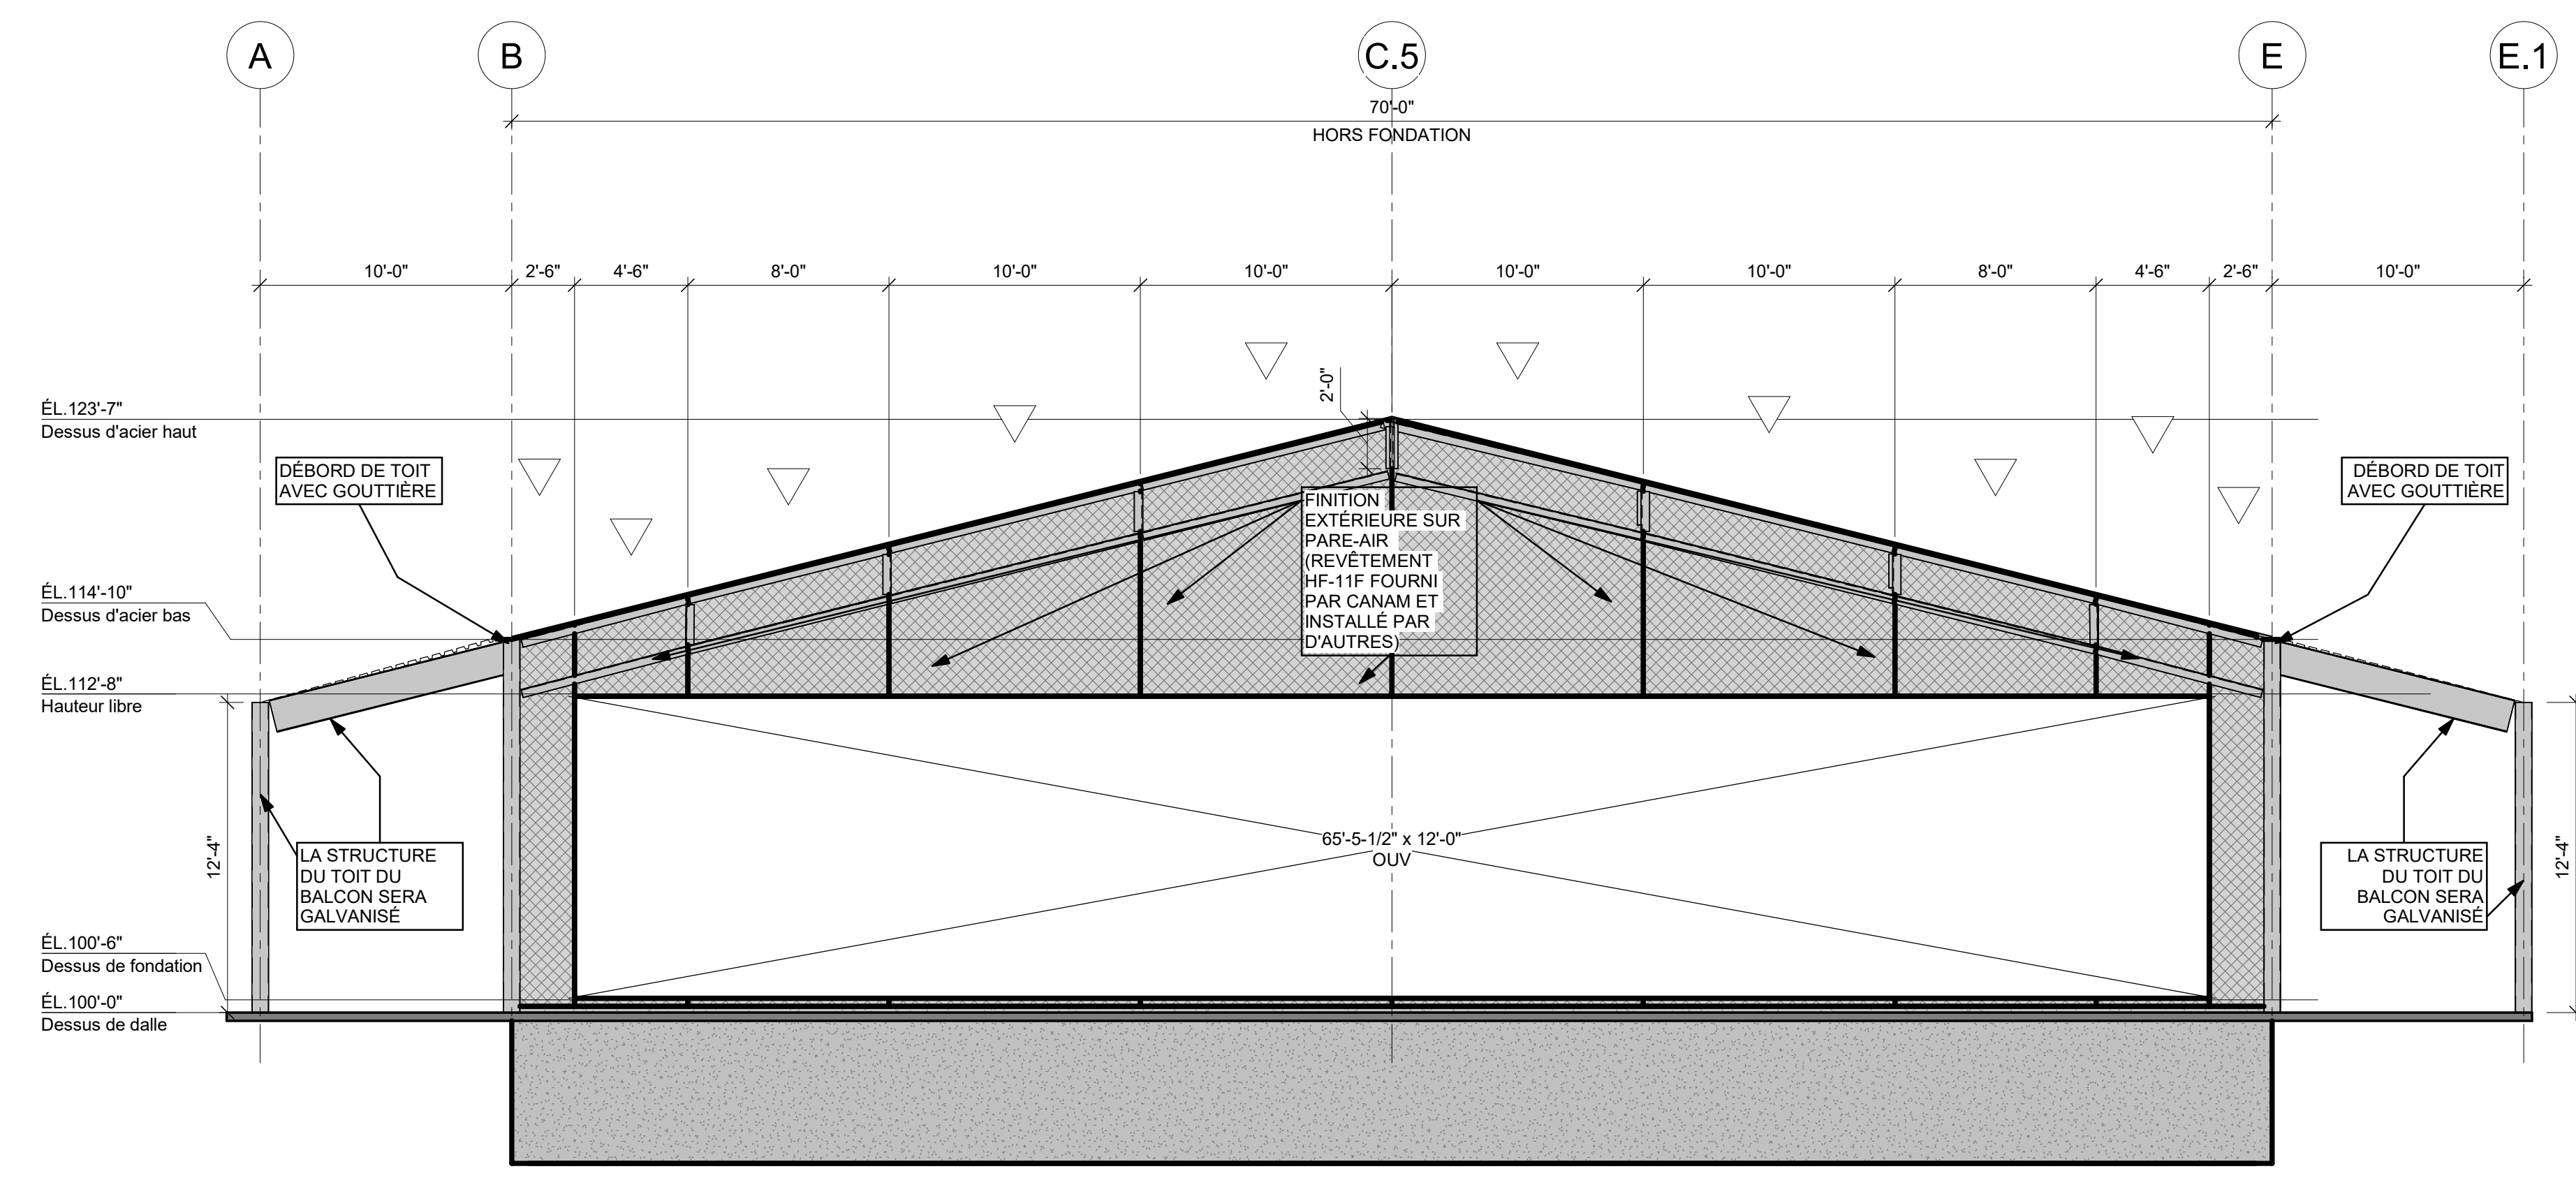

ÉLEVATION AXE 3 (EST)
3/16" = 1'-0"

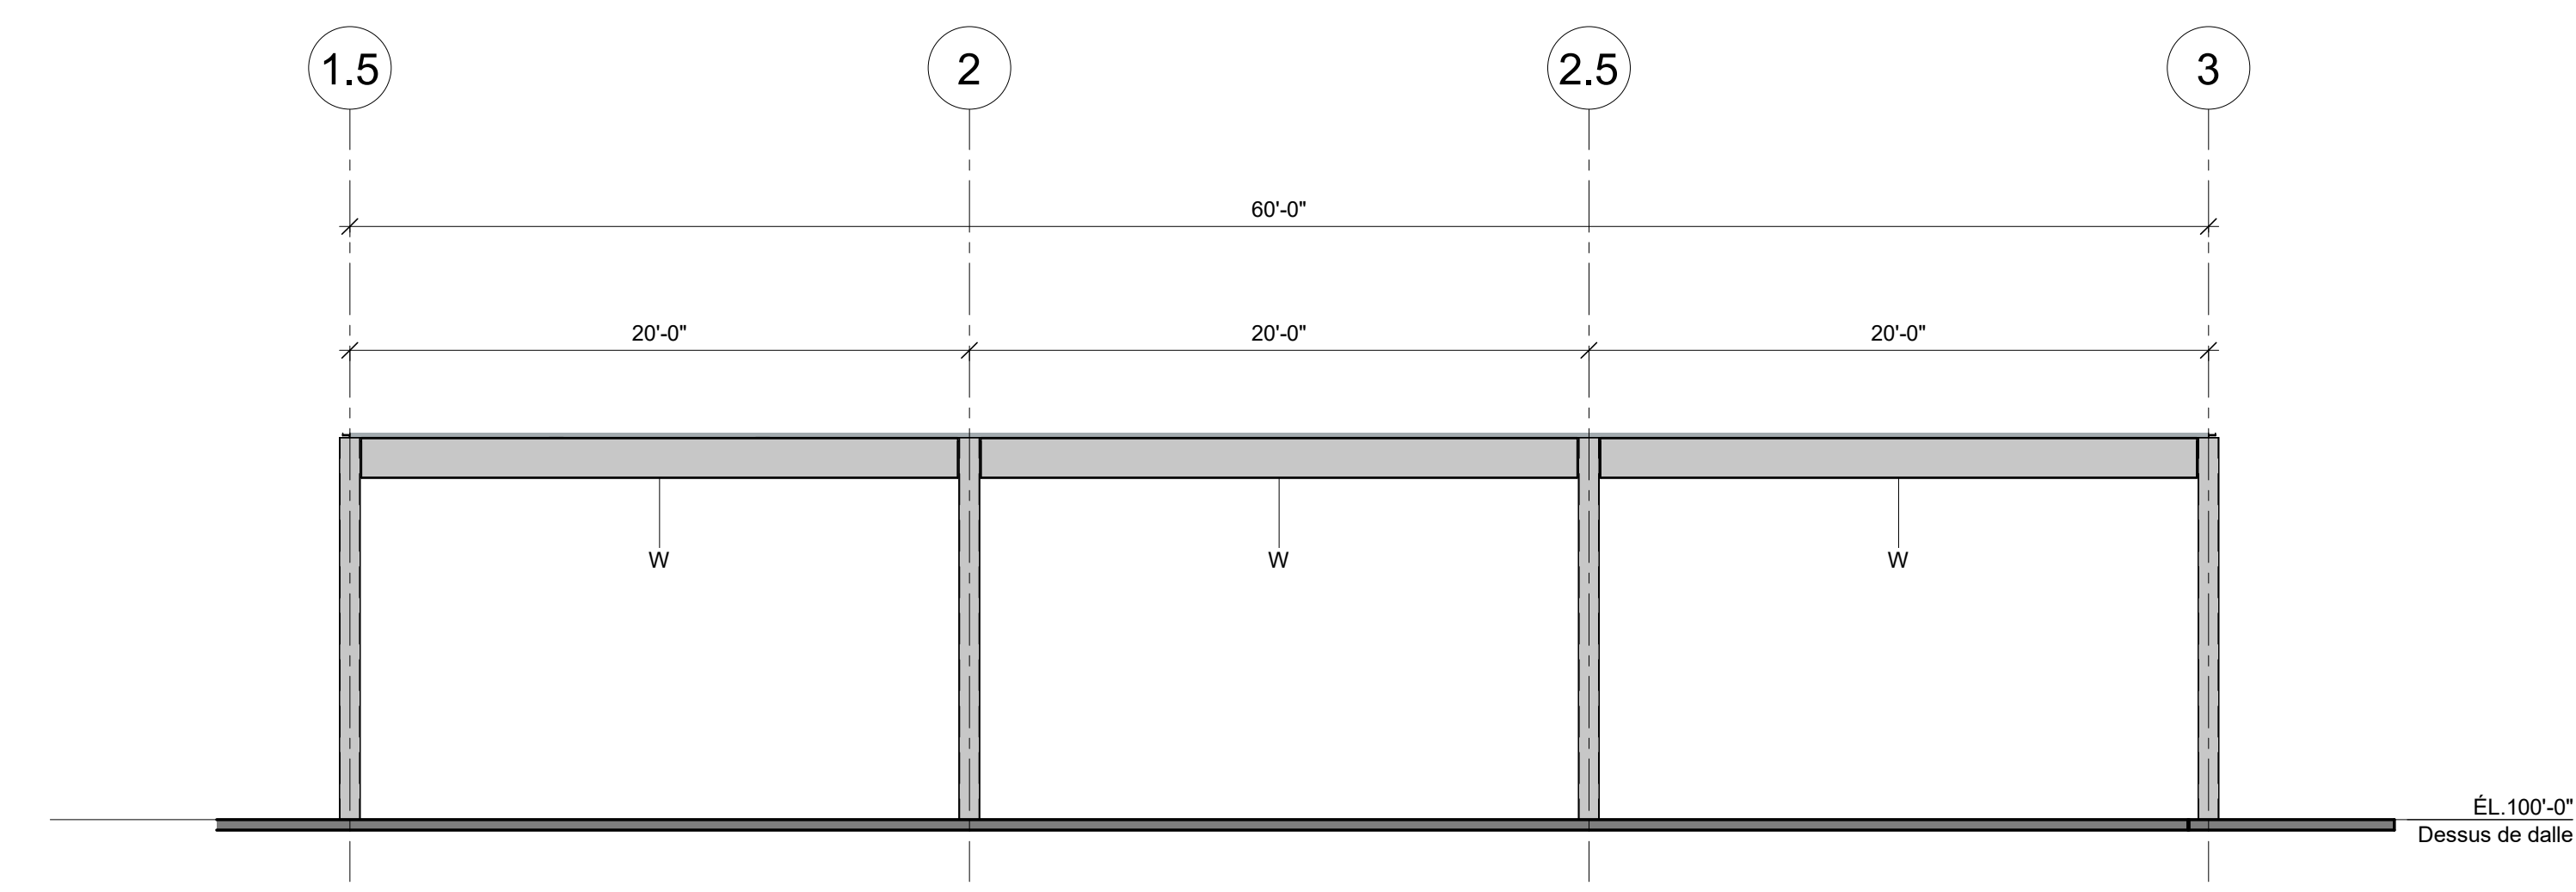

ÉLEVATION AXE A (STRUCTURE BALCON #1)
3/16" = 1'-0"

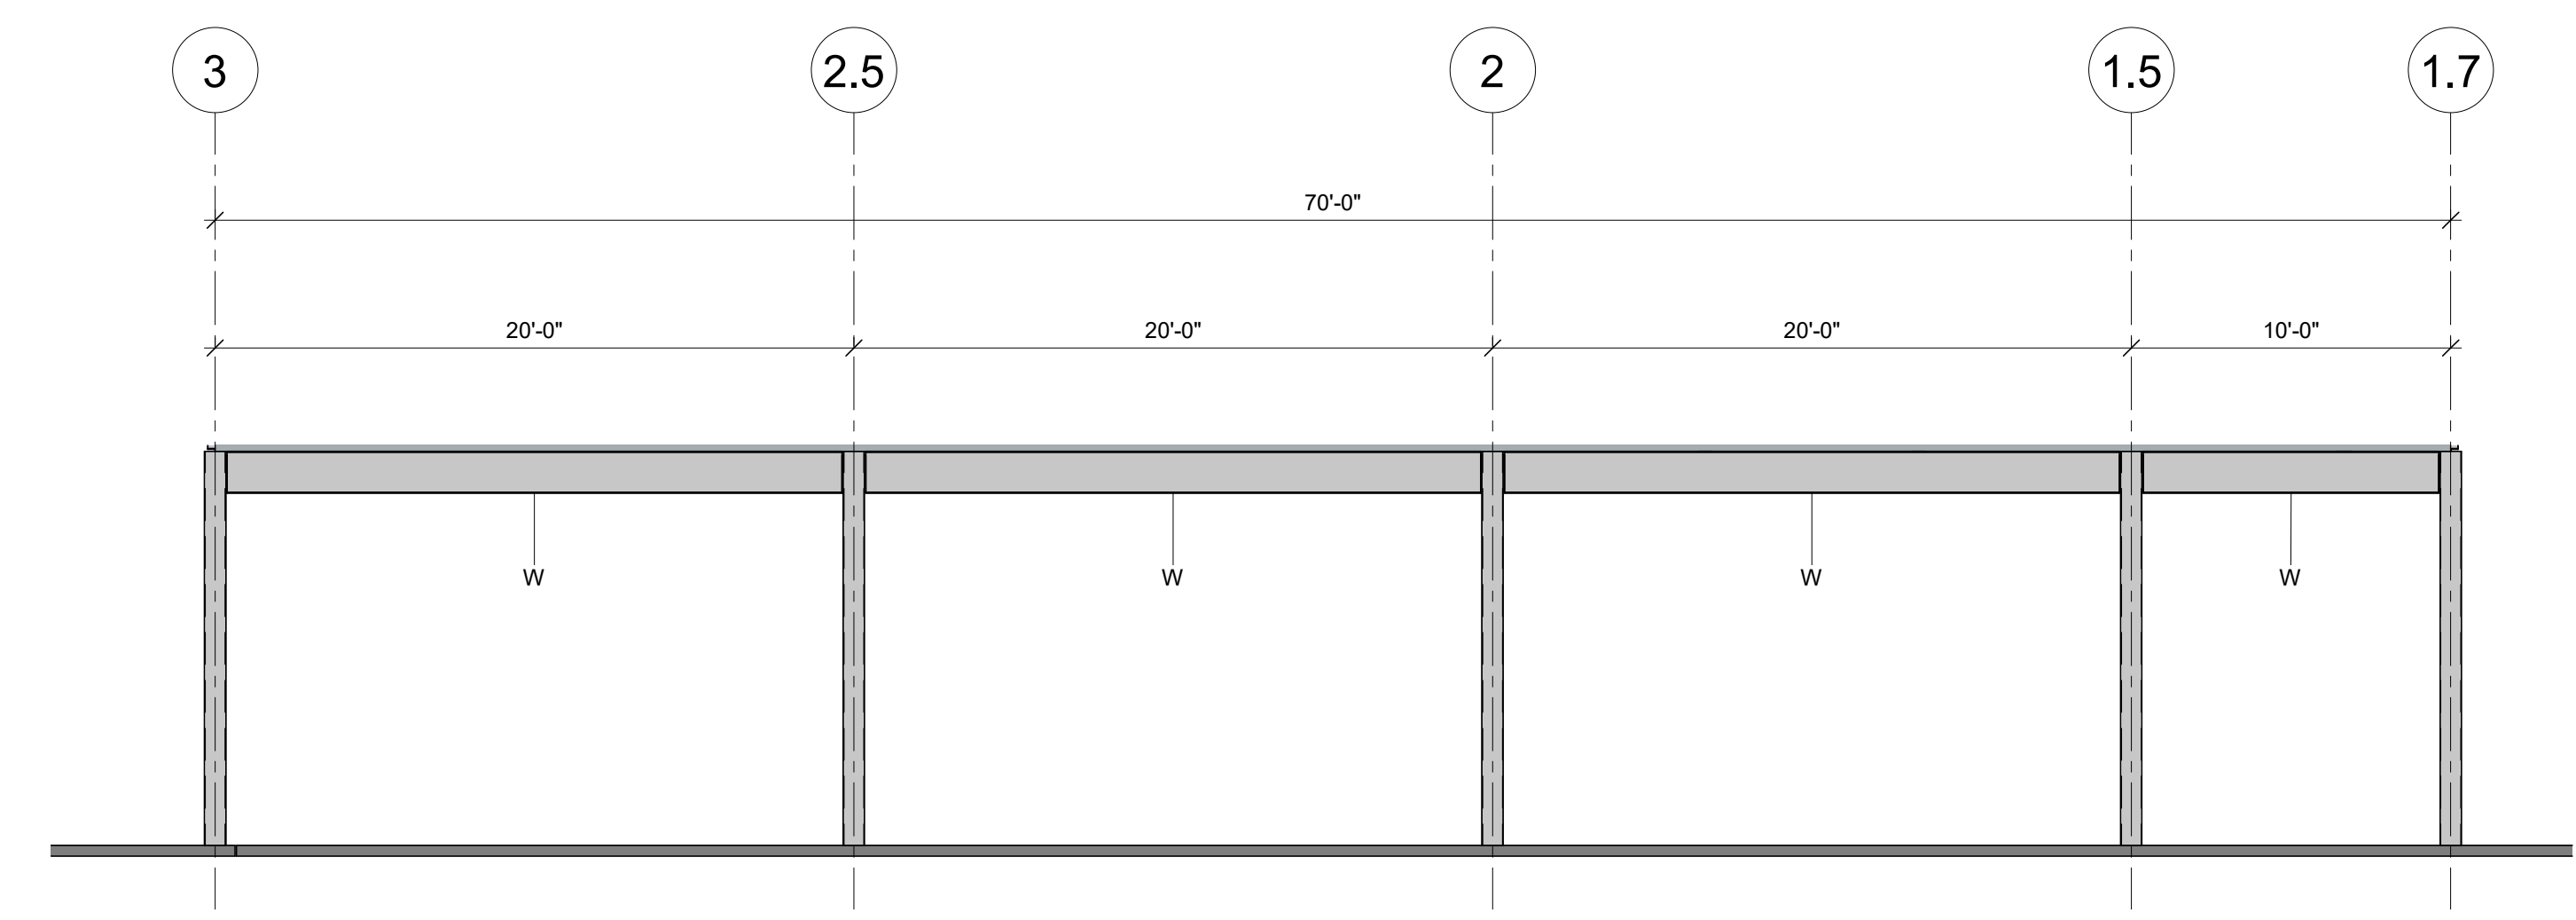

ÉLEVATION AXE E.1 (STRUCTURE BALCON #2)
3/16" = 1'-0"

NOTE POUR LE CONTRACTEUR/ÉRECTEUR:
IL EST STRICTEMENT DÉFENDU DE MODIFIER, COPIER, REPRODUIRE OU DE DISTRIBUER CES DESSINS OU QUELQUES REPRÉSENTATIONS DE CES DESSINS, PAR TOUTES SOURCES DE MÉDIA INCLUANT ÉLECTRONIQUEMENT, SANS L'APPROBATION ÉCRITE DE GROUPE CANAM INC.

PRÉLIMINAIRE

NE DOIT PAS SERVIR À LA CONSTRUCTION

REVISION	DATE	DESCRIPTION	DESS	VER
GERANT DE PROJET			-	
			-	
			-	
			-	
DESSIN				
DESSINÉ PAR	CONÇU PAR	INGÉNIEUR DU PROJET	ÉCHELLE:	
S.L.			3/16" = 1'-0"	
VÉRIFIÉ PAR	INGÉNIEURS CONSEILS / ARCHITECTES	DATE (mm/aa/aaaa)		
		09/02/2026		
CLIENT:	LES CONSTRUCTIONS CMI INC.			



SCAUX PROFESSIONNEL

PROJET
FONDATION VICTOR-CLOUTIER
NOTRE-DAME-DES-PINS, QC

TITRE
CROQUIS PRÉLIMINAIRE - ÉLEVATIONS

NUMÉRO CONTRAT	NUMÉRO DESSIN	DIVISION	REVISION
P2026-024	EsMx501		