


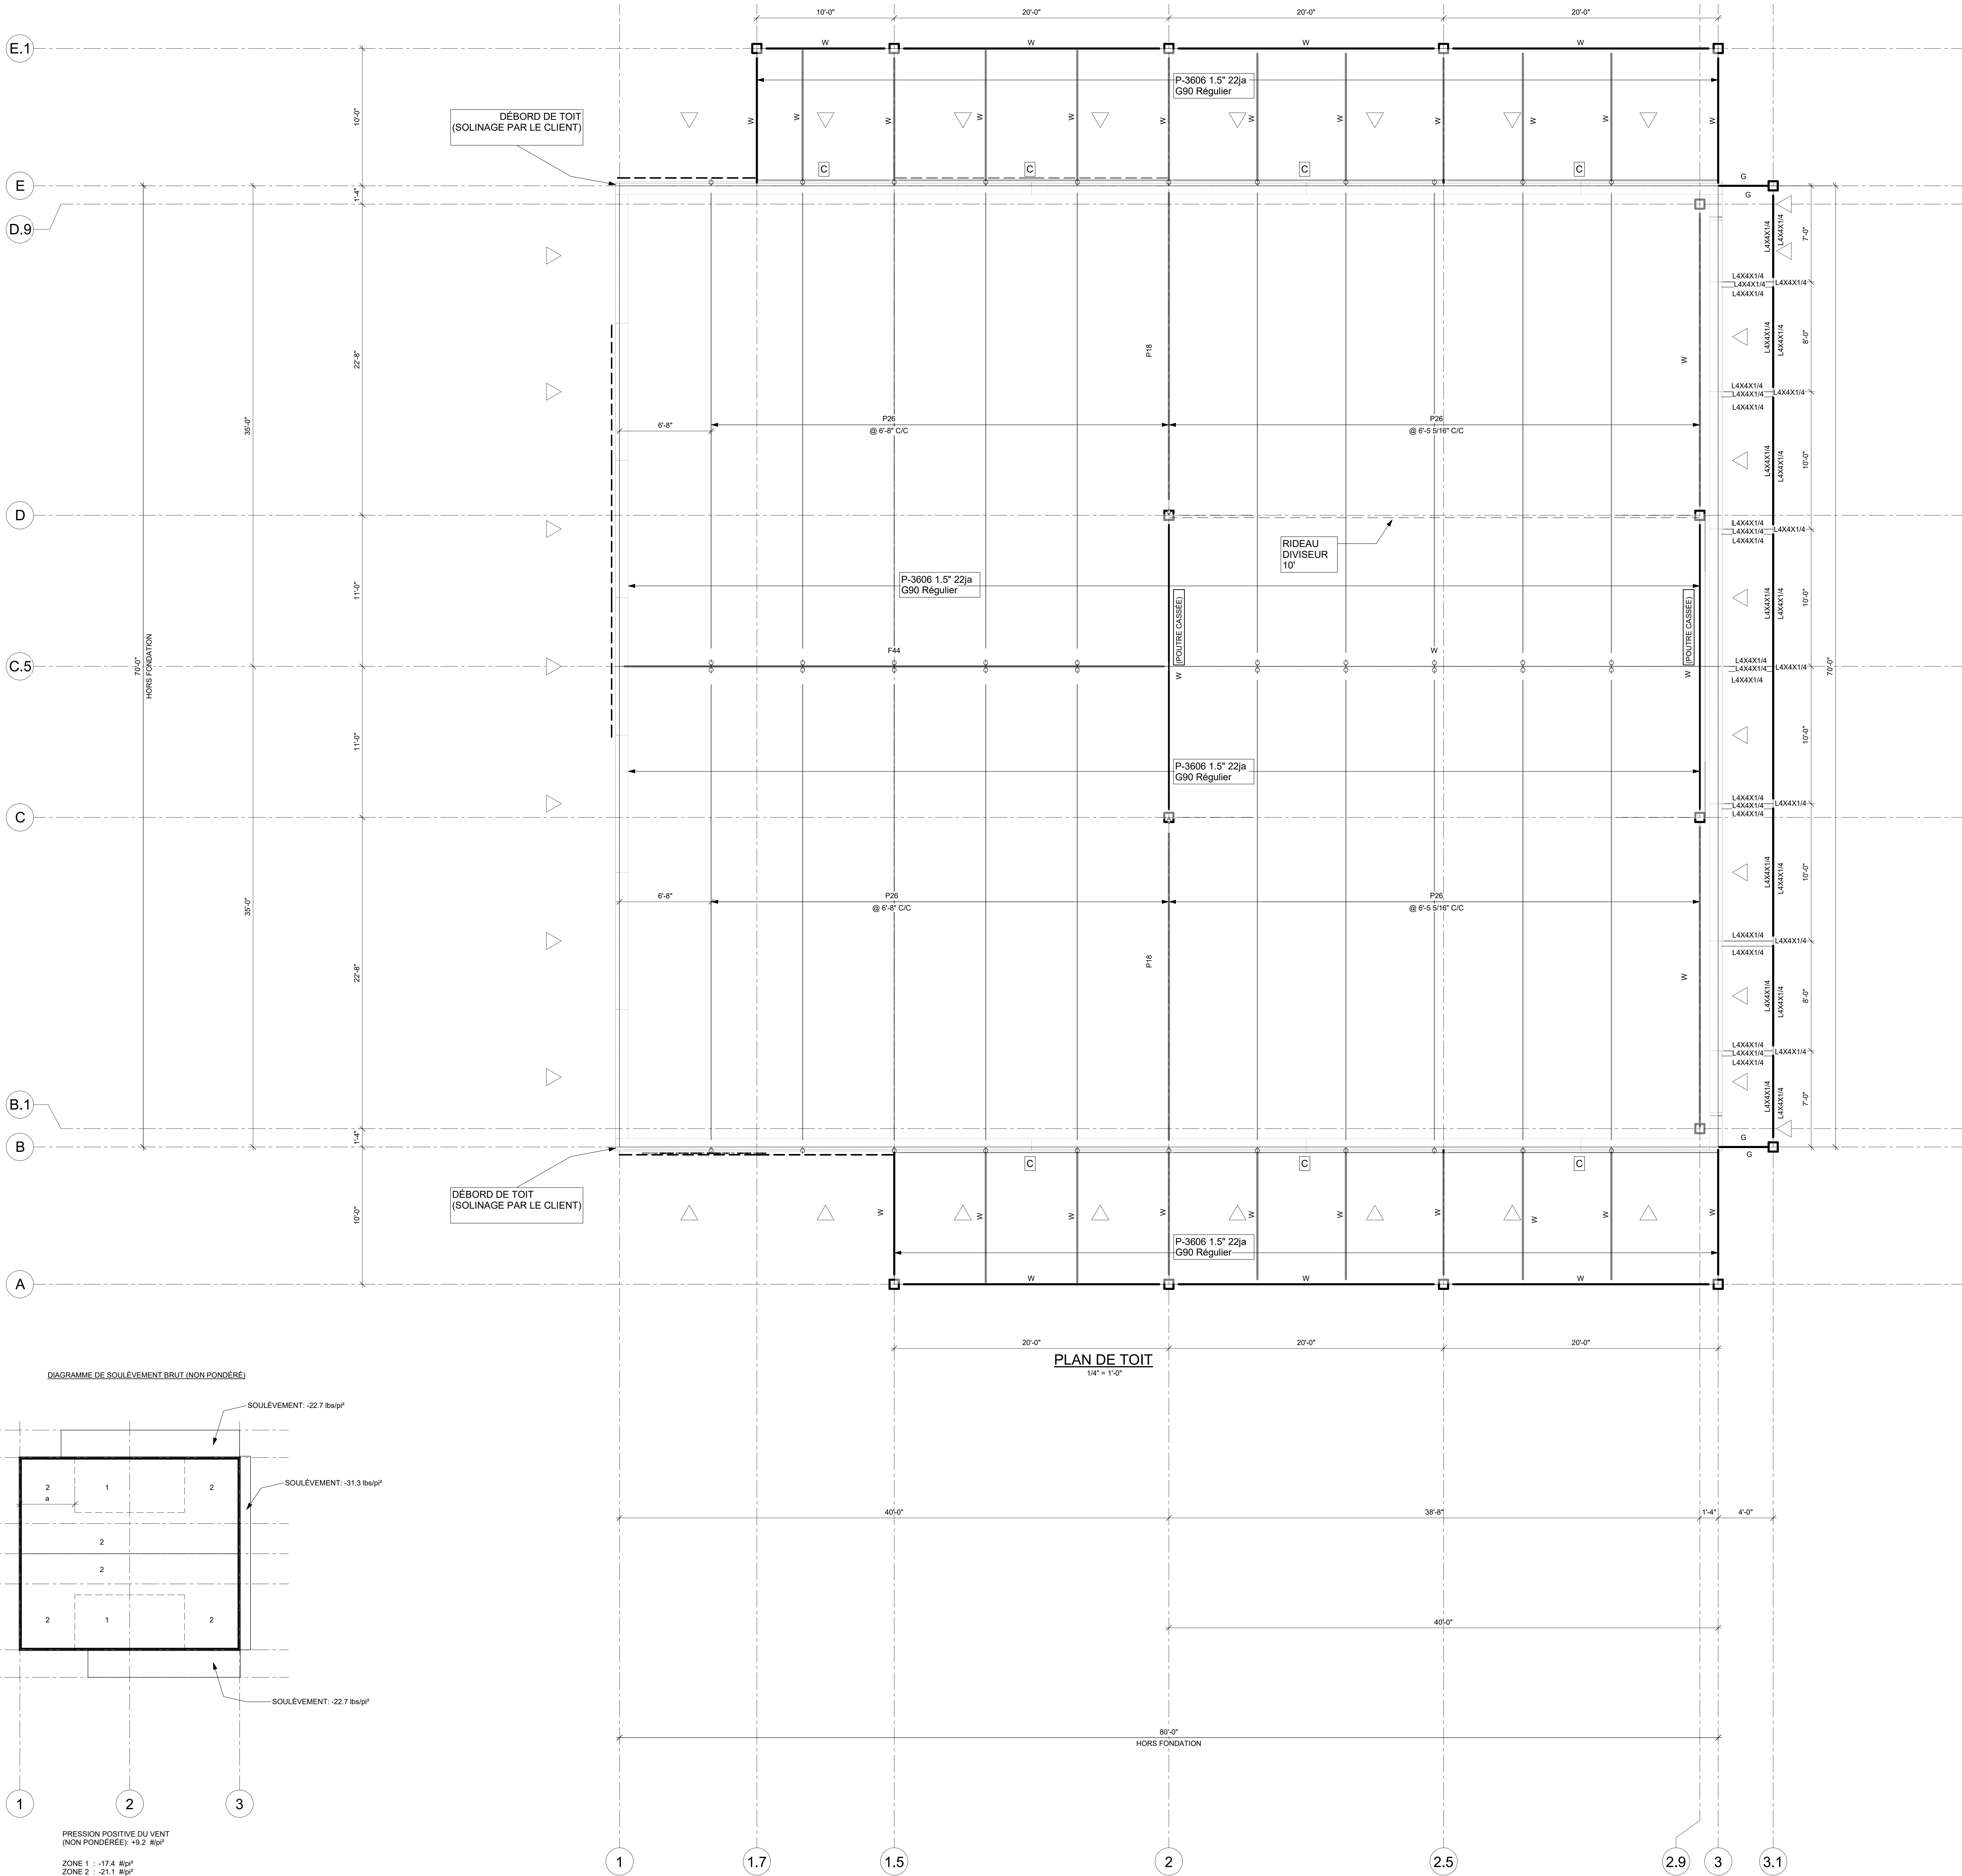


DIAGRAMME DE SOULÈVEMENT BRUT (NON PONDERÉ)

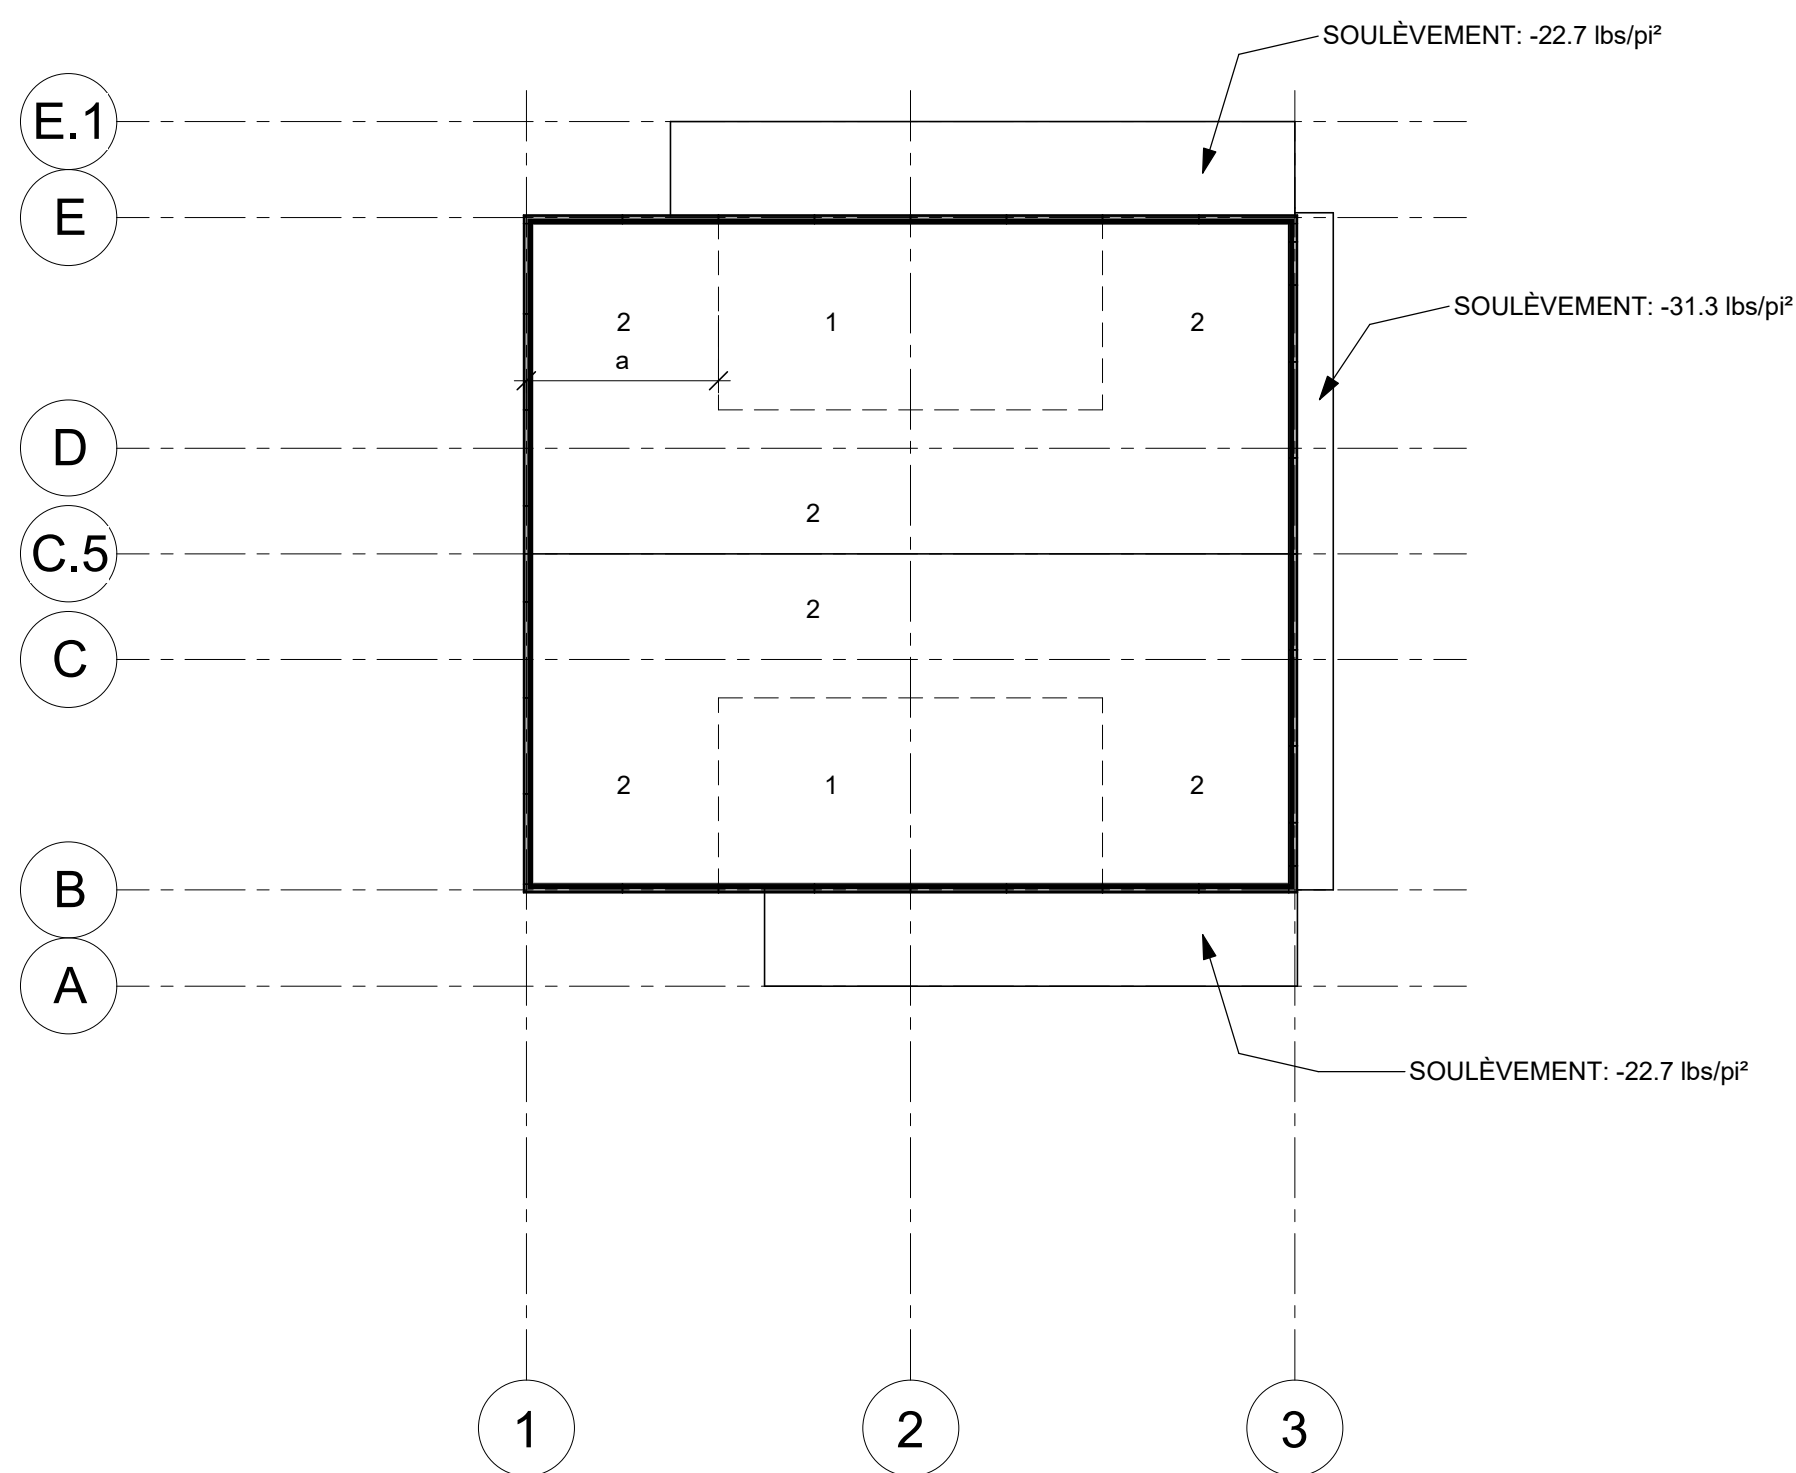

PRESSION POSITIVE DU VENT
(NON PONDERÉE): +9.2 #/ft²
ZONE 1 : -17.4 #/ft²
ZONE 2 : -21.1 #/ft²
a: 6'-0"